


NOTE :
1. DOOR HINGES : GEZE MAKE.
2. DOOR CLOSER : GEZE MAKE.
3. DOOR PANIC BAR : YELE MAKE.

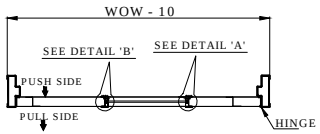

TOP VIEW

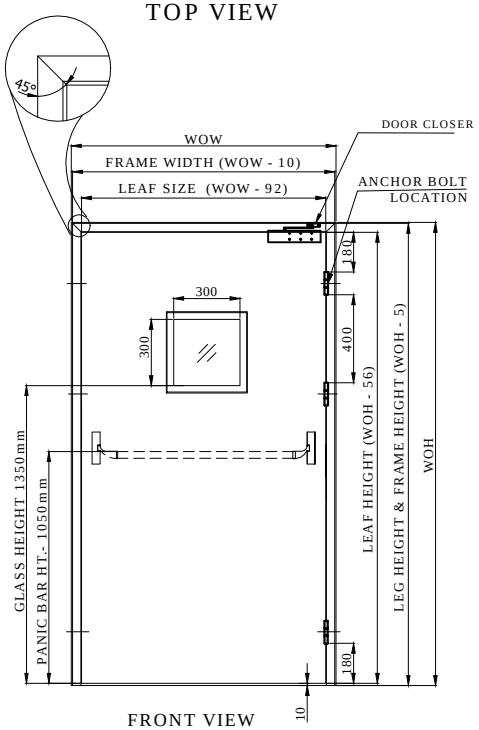


FRONT VIEW

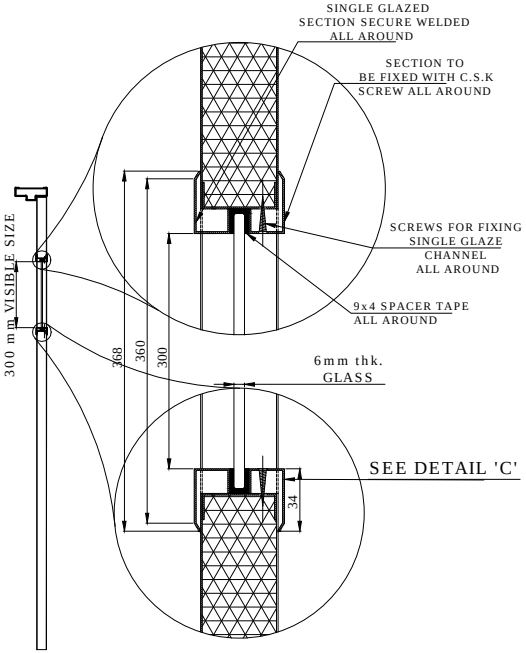


SIDE VIEW
SECTION A-A'

SINGLE GLAZE FIXING DETAIL

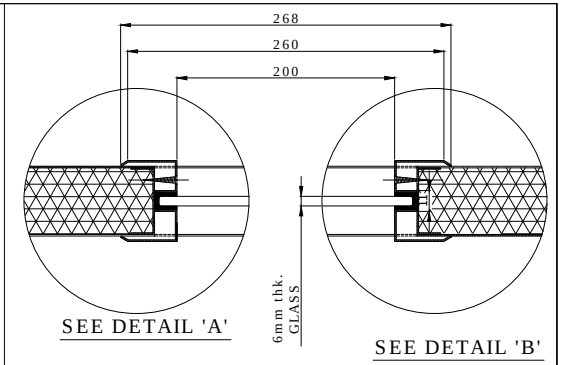



SEE DETAIL 'A'

SEE DETAIL 'B'

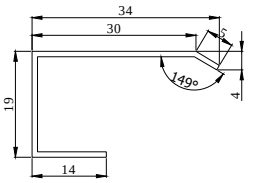


SEE DETAIL 'C'

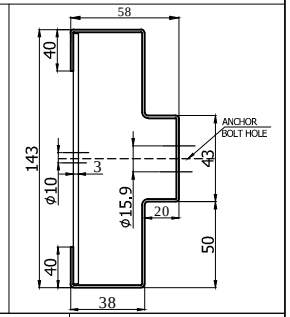

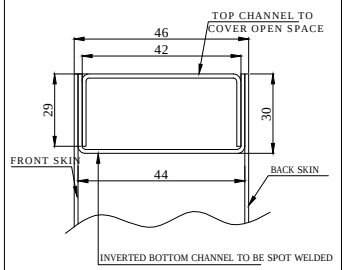

DOOR TOP SECTION DETAIL

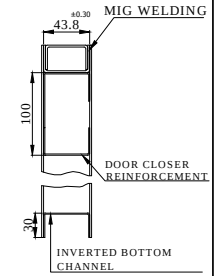

DOOR BOTTOM & TOP DETAIL

REV. NO	DATE	DRAWN	REMARK
R01	27.03.19	P.V.A	1.SPECIFICATION & QTY CHANGE.

SR. NO	WALL OPENING WIDTH	WALL OPENING HEIGHT	QTY	RAL	LOCATION	HARDWARE
05	1200	2100	01	9002	Block B - Metering Kiosk (GD6B)	Hinges , Door closer , Non-Fire rated Glass 300X300mm
04	1200	2100	01	9002	Block D - Metering Kiosk (GD6B)	Hinges , Door closer , Non-Fire rated Glass 300X300mm
03	1200	2100	01	9002	Block C - Metering Kiosk (GD6B)	Hinges , Door closer , Non-Fire rated Glass 300X300mm
02	1200	2100	01	9002	RMU 2 (GD6B)	Hinges , Door closer , Non-Fire rated Glass 300X300mm
01	1200	2100	01	3020	A-Block North Side Mezzanine Exit Door (GD2)	Hinges , Door closer , Single point panic bar with Glass vision panel

TOLERANCE - ±05mm

This drawing & design is the property of NIHVA TECHNOLOGIES. Not to be sold or copied to any other concern.

TITLE: SINGLE LEAF STEEL DOOR

	NAME	SIGN	DATE
DRAWN	P.V.A		21.03.2019
CHECK	V.M.T		21.03.2019
APPRD.			

NIHVA TECHNOLOGIES PVT. LTD.
NIHVA TECHNOLOGIES PVT. LTD. PUNE
Tel : 020 66304033
Email:- info@nihva.com
Website:- www.nihva.com

CLIENT - SYNERGY
PROJECT - EMBASSY
SITE LOCATION - CHAKAN, PUNE.
If any queries contact : design@nihva.com
DWG. NO. : NIHVA/18-19/0297/R01 | REV- R01
ALL DIMENSION ARE IN mm
SCALE: NTS | WT: | SHEET: 01 OF 01