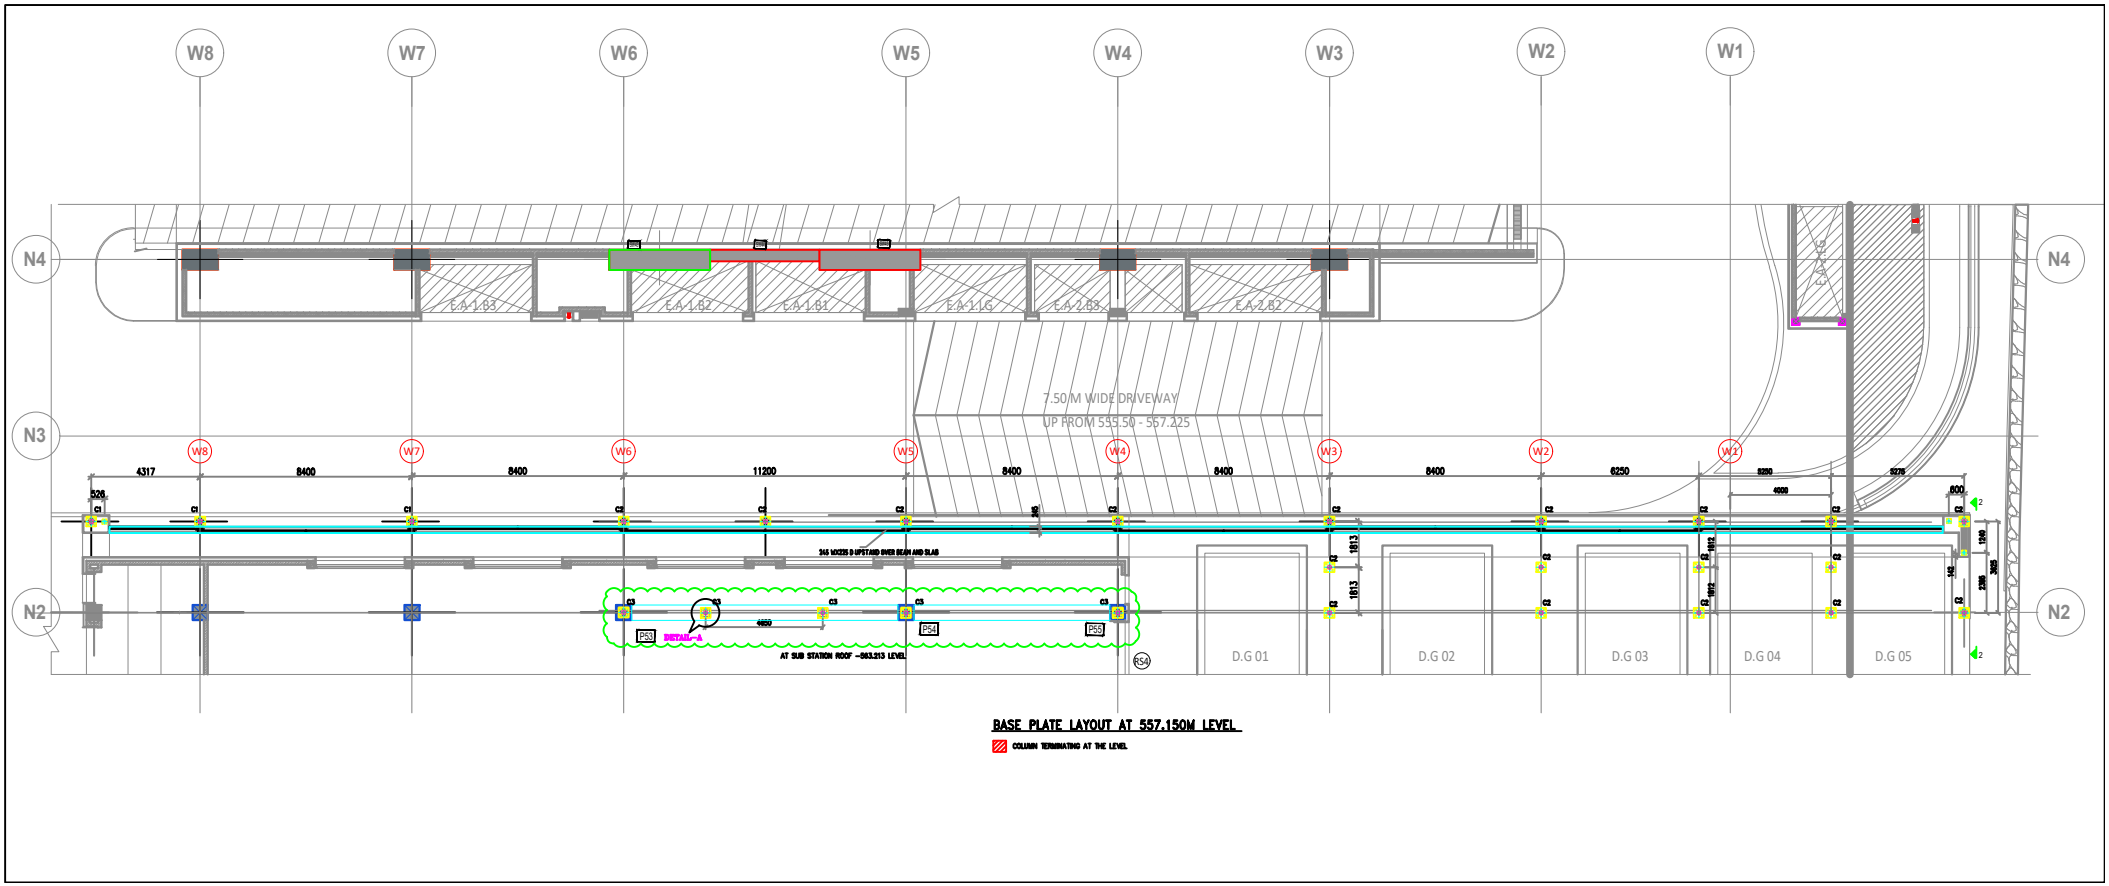


BASE PLATE LAYOUT AT 557.150M LEVEL

COLUMN TERMINATING AT THE LEVEL