

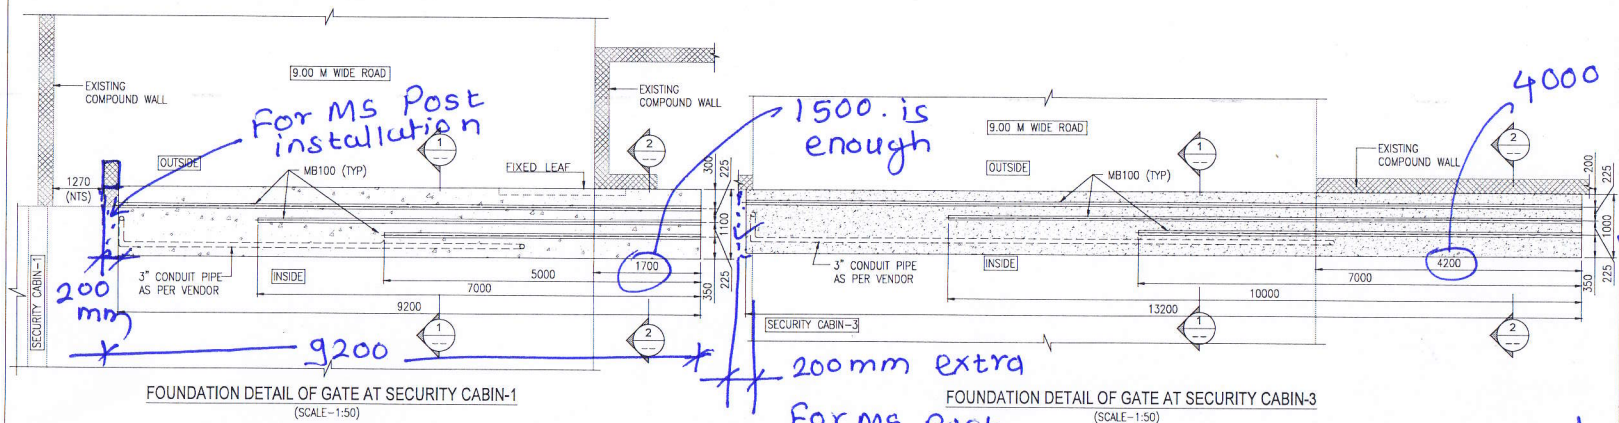


FOUNDATION DETAIL OF GATE AT SECURITY CABIN-1
(SCALE-1:50)


FOUNDATION DETAIL OF GATE AT SECURITY CABIN-3
(SCALE-1:50)

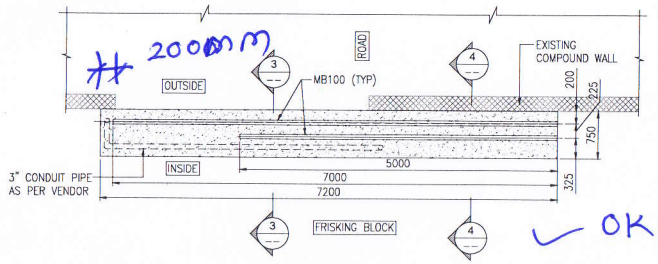


FOUNDATION DETAIL OF GATE AT OSD BLOCK & FRISKING BLOCK
(SCALE-1:50)

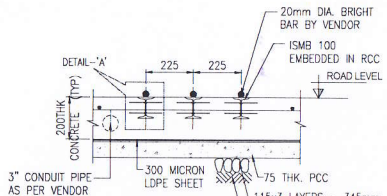


SECTION 1-1
(SCALE-1:15)

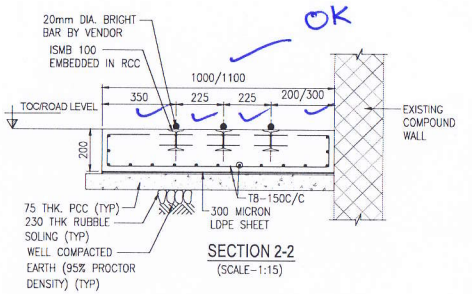


SECTION 2-2
(SCALE-1:15)

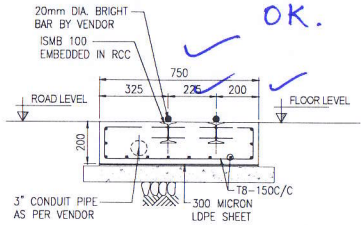


SECTION 3-3
(SCALE-1:15)

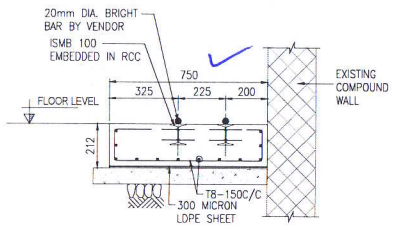

SECTION 4-4
(SCALE-1:15)

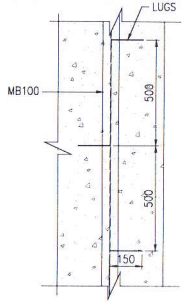

TYP. PLAN OF LUGS
(SCALE-1:15)

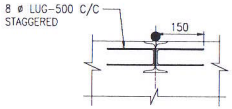

DETAIL-'A'
(SCALE-1:10)

Drawing is confirmed with comments. Please Proceed accordingly.

Omkar 31/1/2017

Omkar B. NIHVA

NOTES:-
ARCH. REFERENCE DRAWING NO:-NIHVA/17-18/0251
NIHVA/17-18/0252
NIHVA/17-18/0253

FOR CONSTRUCTION

ips INTERNATIONAL
Integrated Project Services
Engineering Design
Site Supervision
Consulting
www.ipsdb.com
C-1,C-Block, Community Centre, Naraina Vihar, New Delhi - 110 028
+91-11-25777806 phone
Kailash Vaibhav Industrial Complex Unit B-101 to 109, First Floor, Park Site Behind Godrej Residential Colony, Vikhroli (West), Mumbai - 400079
+91-22-67209717 phone


REVISION	DATE	DESCRIPTION	BY
00	25.11.2017	FOR CONSTRUCTION	NGS

DRAWING REFERENCE

SNO	DRAWING NAME	DWG NO.	REFERENCE
1	GENERAL NOTES, LEGENDS & DETAILS	IPS-14-1095-SD-1101	-
2	TYPICAL DETAILS OF RCC COLUMN & FOOTING	IPS-14-1095-SD-1102	-
3	TYPICAL DETAILS OF RCC BEAM & SLAB	IPS-14-1095-SD-1103	-

NOTES

1. ALL DIMENSIONS ARE IN MILLIMETERS AND LEVELS IN METERS UNO.
2. SOIL BEARING CAPACITY ASSUMED AS 400KN/m² AT DEPTH OF 1.7M. FROM NGL. AS PER SOIL REPORT ROCK STRATA IS AVAILABLE AT THIS DEPTH
3. GRADE OF REINFORCEMENT – Fe 500 (TOR STEEL)
4. GRADE OF CONCRETE SHALL BE M 25.
5. FOR BUILDING LOCATION REFER PLOT PLAN.
6. CLEAR COVER TO MAIN REINFORCEMENT SHALL BE AS FOLLOWS:
   i) FOOTING ----------75 mm
7. Ld = LAP LENGTH (DEVELOPMENT LENGTH SHALL BE 50 TIMES DIA OF BAR (U.N.O.)
8. FOR BUILDING CO-ORDINATES REFER ARCHITECTURE DRAWING.
9. ALL BLACK COTTON SOIL SHALL BE REMOVED FILLING SHALL BE DONE WITH GOOD QUALITY MURUM WITH PROCTOR DENSITY 95%

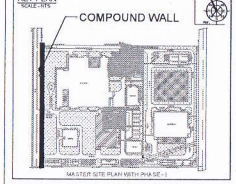KEY PLAN


CONFIDENTIAL
THE INFORMATION CONTAINED HEREIN MAY NOT BE USED OR REPRODUCED IN ANY MANNER WITHOUT WRITTEN PERMISSION OF INTEGRATED PROJECT SERVICES.

CLIENT
LUPIN LIMITED
MIHAN NAGPUR
Lupin Ltd.

DRAWING TITLE
LAYOUT & DETAILS OF SLIDING GATES FOR SECURITY CABIN-1,3 & FRISKING BLOCK

ENGINEER	ARCHITECT	DESIGNER
APP	SK	SSM
DRAWN BY	RE-REVIEWED BY	SCALE
NGS	RCC	1:50,1:15

IPS #	DRAWING NUMBER
14-1095	IPS-14-1095-SK-1598
XREF FILE(S)	
CAD FILE #	PAPER SIZE: A2
	REVISION: 00