
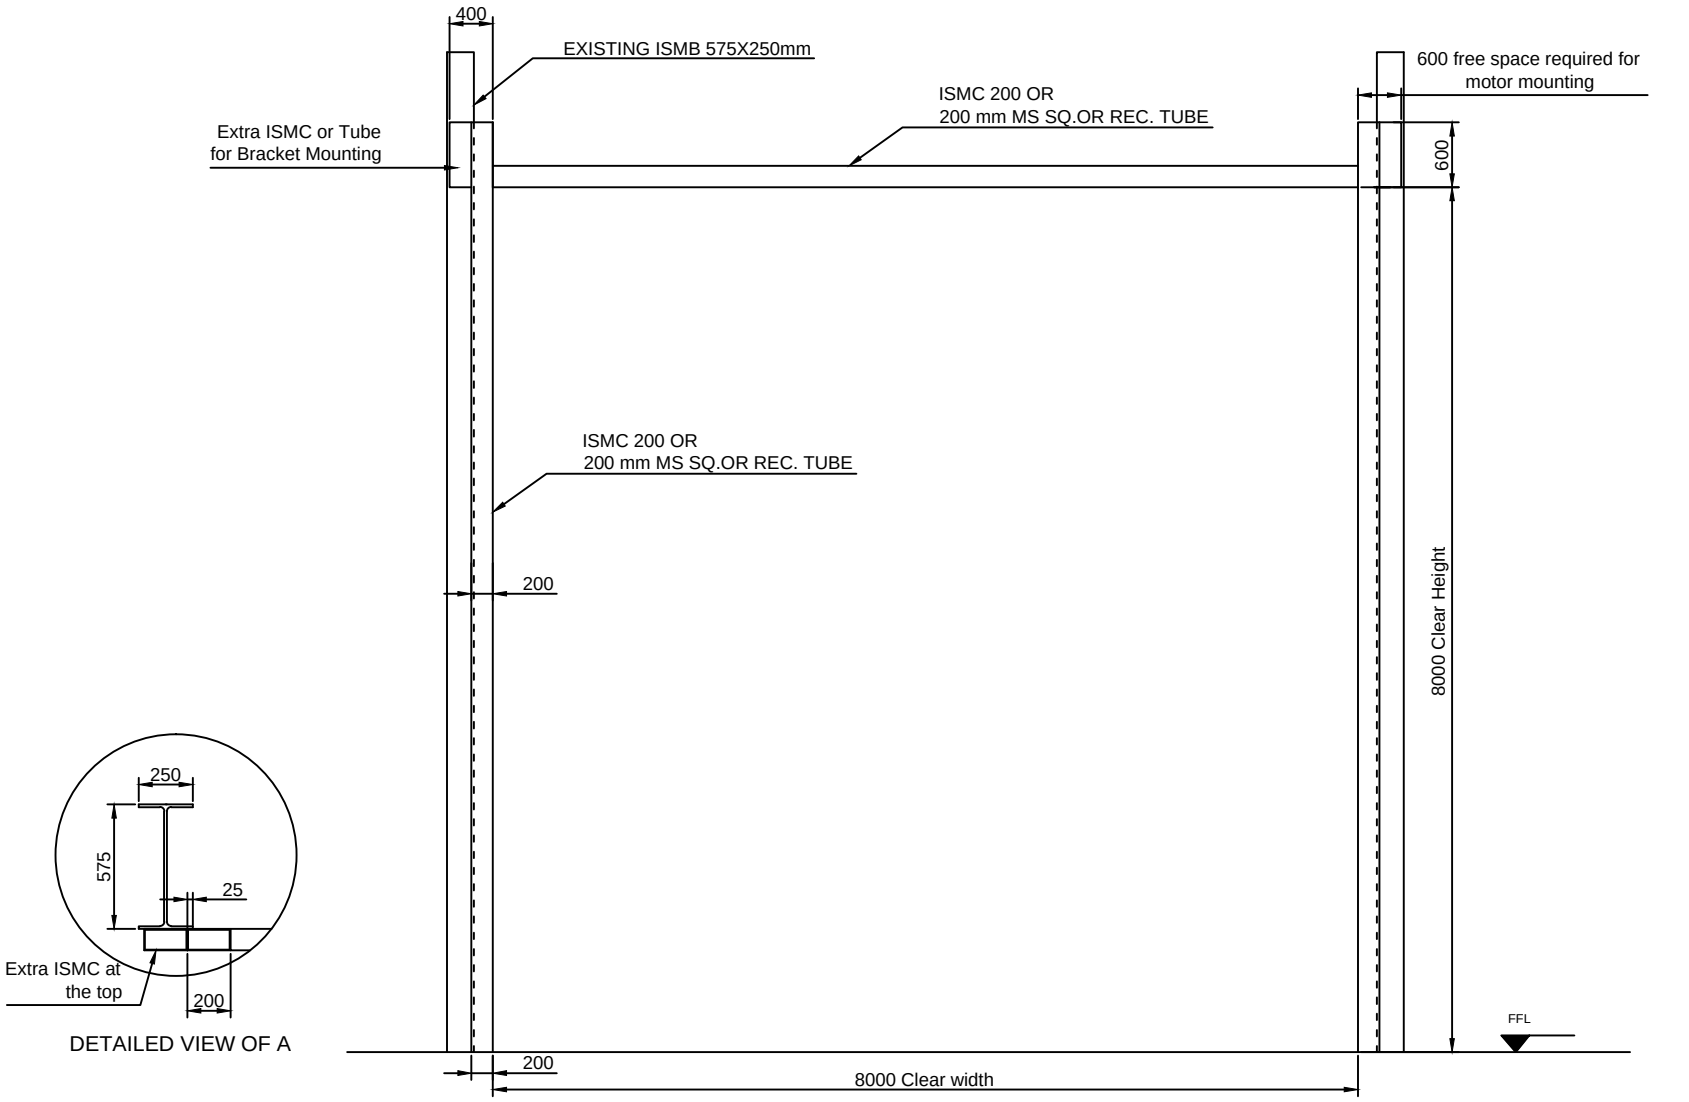


DETAILED VIEW OF A

INSIDE ELEVATION

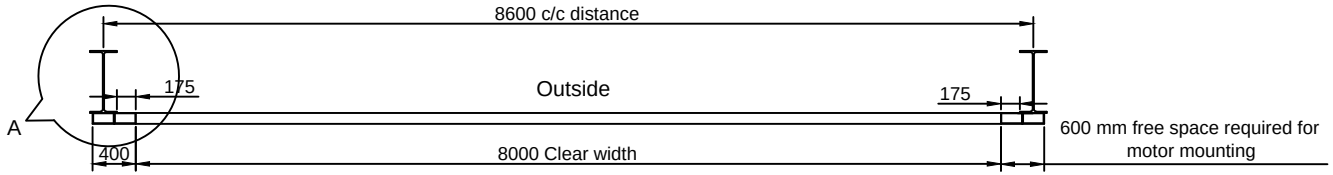

Inside

PLAN

DIMENSIONS:

SR NO	CLEAR WIDTH	CLEAR HEIGHT
1	8000mm	8000mm

NOTE: REQUIRED STRUCTURE FOR SHUTTER SHALL BE IN CLIENT SCOPE.

CLIENT: & BOYCE MFG. CO. LTD.
CONSULTANCY SERVICES FOR DETAILED ENGINEERING OF INDUSTRIAL EXPANSION PROJECT

PROJECT: GODREJ & BOYCE MFG. CO. LTD.
PROPOSED INDUSTRIAL EXPANSION AT VILLAGE VADVAL AND TAMBATI. TAL. KHALAPUR, DIST. RAIGAD.

ARCHITECT/CONSULTANT: TATA CONSULTING ENGINEERS LIMITED MUMBAI

PMC: CUSHMAN & WAKEFIELD
Cushman wakefield India Pvt. Ltd.
Onyx 11th Floor, North Main Road, Next to Westin Hotel, Koregaon Park, Pune 411001, India.

CONTRACTOR: RATILAL BHAGWANDAS CONSTRUCTION COMPANY PVT. LTD. PUNE.

NIHVA TECHNOLOGIES PVT. LTD. NIHVA TECHNOLOGY PVT. LTD. PUNE
Email:- info@nihva.com
Website:- www.nihva.com

DWG TITLE: STRUCTURE FOR ROLLING SHUTTER 8mx8m

DRN BY:	SCALE:	DWG NO:	REV NO:
OMKAR	NTS	NIHVA/16-17/0095/01	0
CHKD BY: SAGAR P.	DATE: 09-11-2016		

If any queries contact : projects@nihva.com

NOTE: ALL DIMENSION ARE IN mm

THIS DRAWING & DESIGNING IS THE PROPERTY OF NIHVA TECHNOLOGIES. NOT BE SOLD OR COPY TO ANY OTHER CONCERN.