

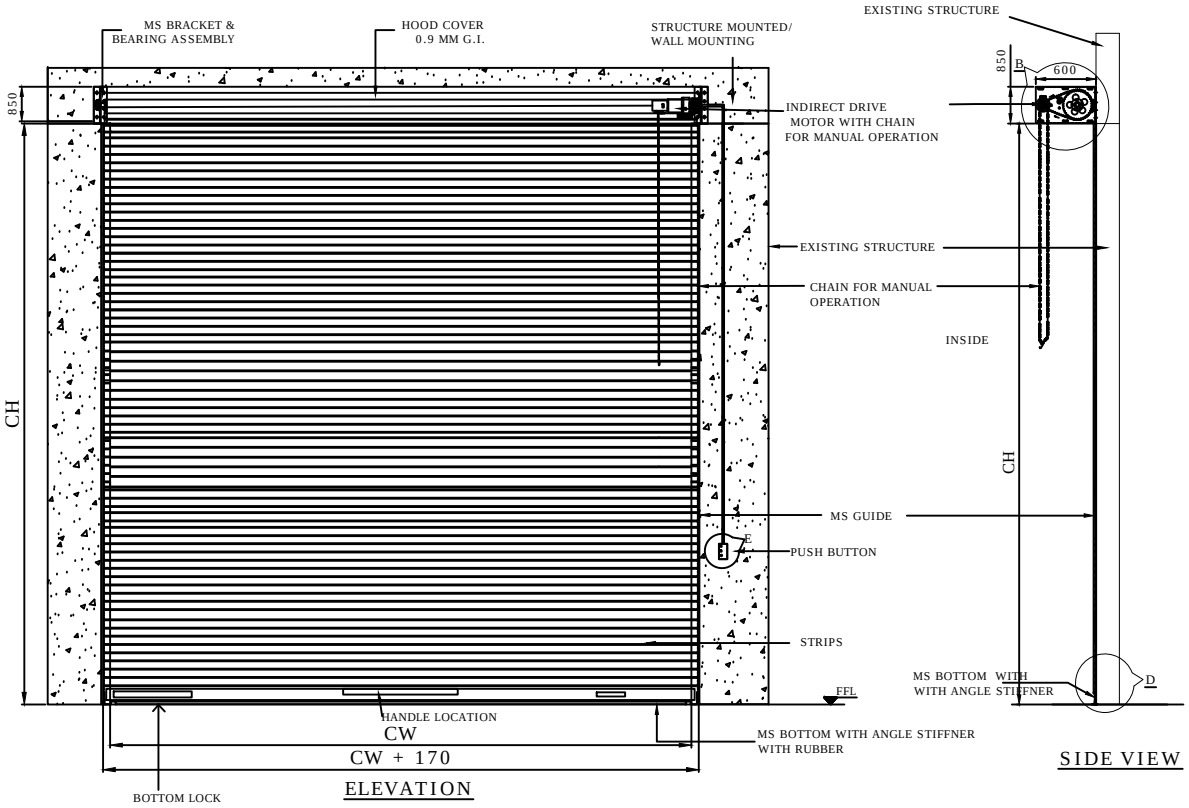


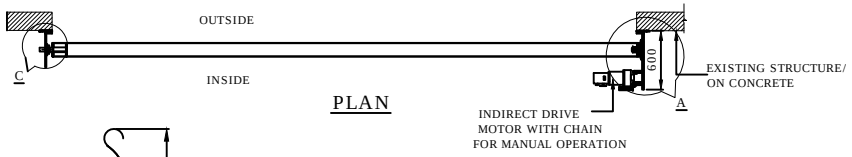


PLAN


NOTE:
(1) IF REQUIRED M.S.TECHNICAL STRUCTURE & FITTING IN CLIENT SCOPE.
(2) ALL CIVIL WORK IN CLIENT SCOPE.
(3) SHUTTER WILL BE ONLY INSTALLED AFTER STRUCTURE READY AS PER DRAWING PROVIDED IF REQUIRED .
(4) PLEASE REFER FOLLOWING TABLE & MENTION YOUR REQUIREMNT IN TABLE.

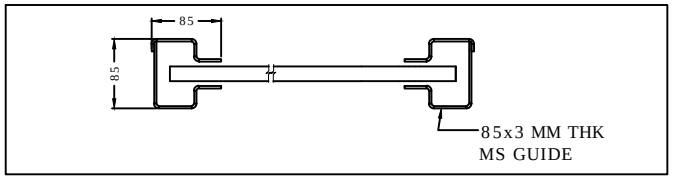


SR NO	PARAMETER	DESCRIPTION	CUSTOMER REMARK
1	SHUTTER MOUNTING	ON STRUCTURE / ON CONCRETE	
2	SURFACE FINISH	RAL CODE FOR POWDER COATING	

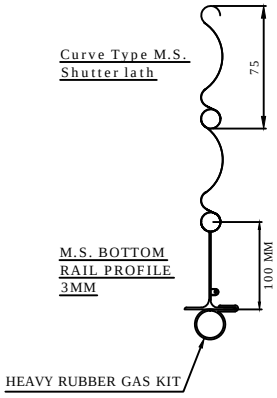

DETAILS : D

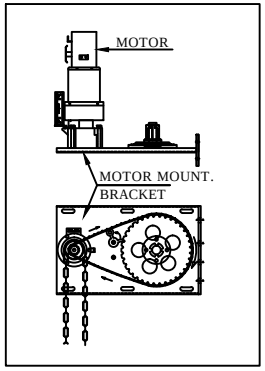

DETAILS : A & B

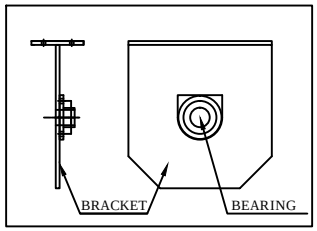

DETAILS : C

4500	4000	1	
CLEAR WIDTH (CW)	CLEAR HEIGHT (CH)	QUANTITY	RAL COLOR POWDER COATED

This drawing & design is the property of NIHVA TECHNOLOGIES. Not to be sold or copied to any other concern.

TITLE: MOTORIZED ROLLING SHUTTER

	NAME	SIGN	DATE
DRAWN	S.M.S.		26.10.2020
CHECK	K.P.		26.10.2020
APPRD.			

NIHVA TECHNOLOGIES PVT. LTD.
NIHVA TECHNOLOGIES PVT. LTD. PUNE
Tel : 020 66304033
Email:- info@nihva.com
Website:- www.nihva.com

CLIENT - QUALITY INFRASTRUCTURE
PROJECT - TENNECO AIR INDIA PVT LTD
SITE LOCATION - PUNE
If any queries contact : projectsupport@nihva.com
DWG. NO. : NIHVA/20-21/0089
REV- R00
ALL DIMENSION ARE IN mm
SCALE: NTS
WT:
SHEET: