




SIDE VIEW

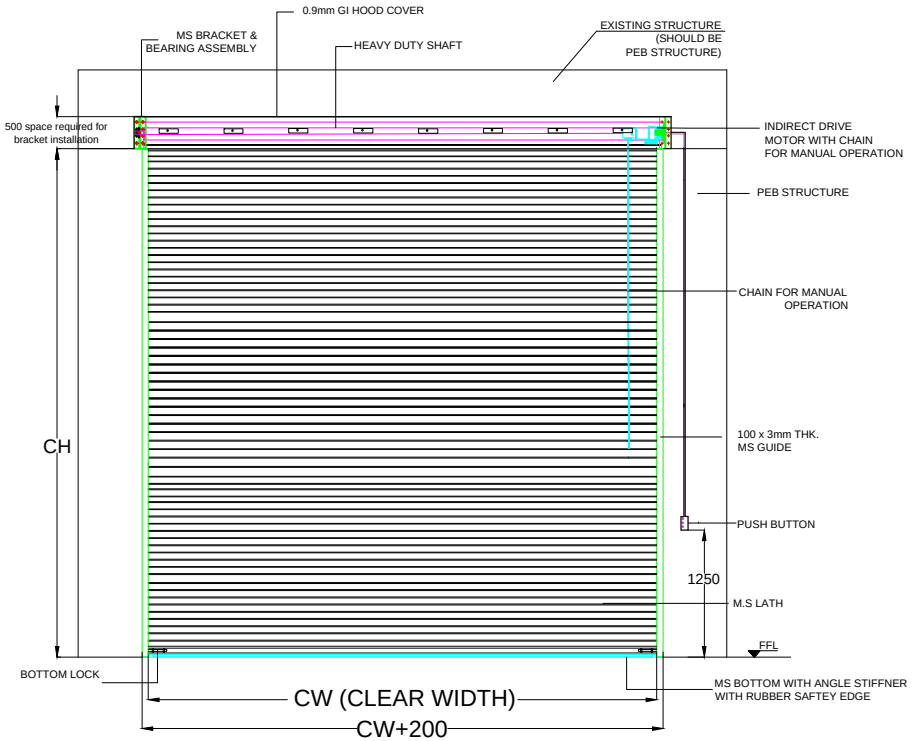


ELEVATION

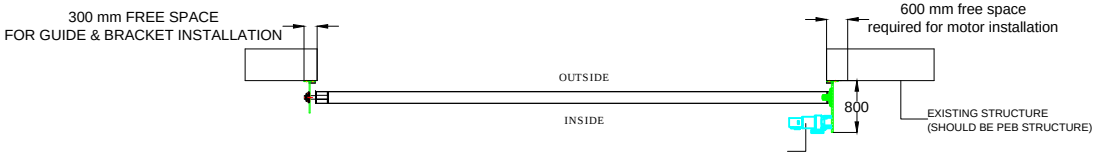

PLAN

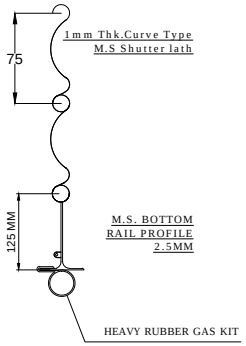

M.S. BOTTOM RAIL PROFILE 2.5MM

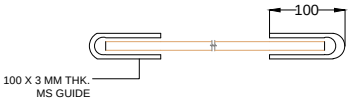

RAL COLOR & CODE

RAL 1003	
RAL 2004	
RAL 3000	
RAL 5002	
RAL 6005	
RAL 7035	
RAL 9005	
RAL 9010	

TOLERANCE - ±10mm

CLEAR WIDTH	CLEAR HEIGHT	QTY.
4000mm	5000mm	01 No.

NOTE-
1. ALL CIVIL WORK WILL BE CLIENT'S SCOPE.
2.STRUCTURE REQUIRED FOR SHUTTER IS IN CLIENT'S SCOPE.
3. RAL CODE - PLEASE TICK IN GIVEN BOX.

This drawing & design is the property of NIHVA TECHNOLOGIES. Not to be sold or copied to any other concern.

TITLE: MOTORISED ROLLING SHUTTER

	NAME	SIGN	DATE
DRAWN	P.V.A		16.08.2019
CHECK	V.M.T		16.08.2019
APPRD.			

NIHVA TECHNOLOGIES PVT. LTD.
Website:- www.nihva.com
NIHVA TECHNOLOGIES PVT. LTD. PUNE
Tel : 020 66304033
Email:- info@nihva.com

CLIENT - RELIABLE CONSTROTECH
PROJECT - TATA CUMMINS
SITE LOCATION - PHALTAN

If any queries contact : design@nihva.com
DWG. NO. : NIHVA/19-20/0079
REV- R00
ALL DIMENSION ARE IN mm
SCALE: NTS
WT:
SHEET: 01 OF 01