编号 No.	LC1521 1500X2100	名称 Name	平开双扇铝合金窗
		数量 Quantity	39

立面(洞口尺寸) Elevation(opening size)

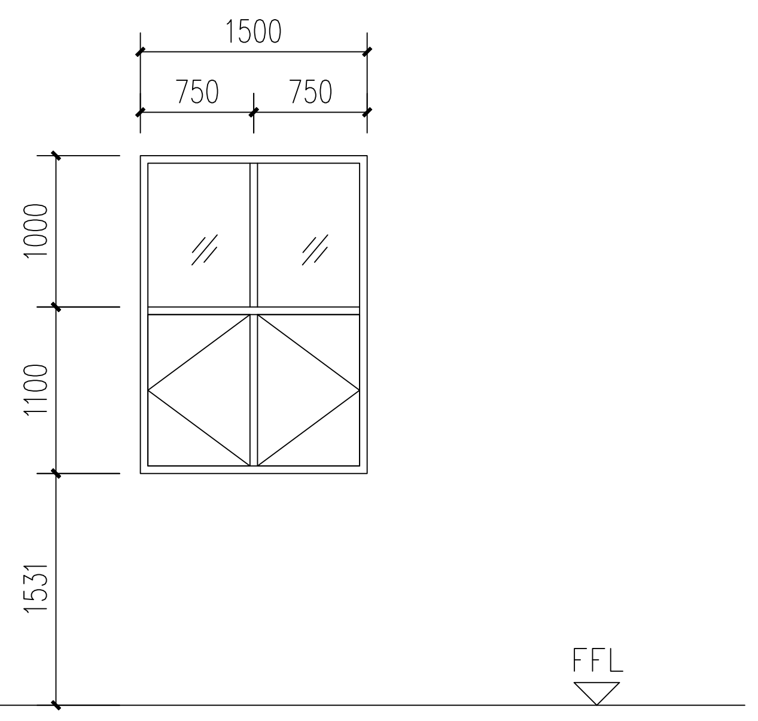

框 Frame	断热型铝合金，氟碳喷涂，隔热条高度26.0mm Heat-dissipating aluminum alloy, fluorocarbon spray, heat insulation strip height 26.0mm				
扇 Leaf	— -	铰链 Hinge	— -	纱窗 Screen	— —
玻璃 Glass	5Low-e+15A+5厚中空玻璃，中透光，离线单银 5Low-e+15A+5 thick insulating glass, medium light transmission, offline single silver	制动 Closure	手动 Manually	锁具 Lock	配套 Support
百叶 Louver	— —	门槛 Sill	— —	执手 Handle	— —
备注 Note	受力构件壁厚不小于1.6mm The wall thickness of the stressed member is not less than 1.6mm				

编号 No.	LC1560 1200X6000	名称 Name	上悬铝合金窗
		数量 Quantity	18

立面(洞口尺寸) Elevation(opening size)

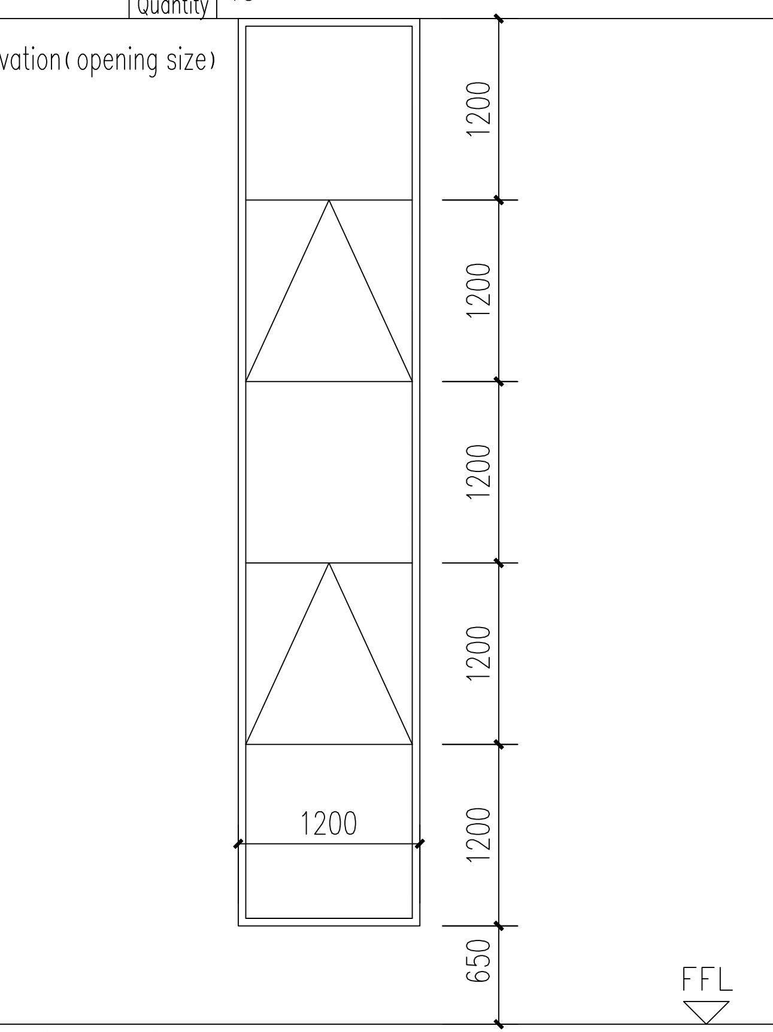

框 Frame	断热型铝合金，氟碳喷涂，隔热条高度26.0mm Heat-dissipating aluminum alloy, fluorocarbon spray, heat insulation strip height 26.0mm				
扇 Leaf	— -	铰链 Hinge	— -	纱窗 Screen	— —
玻璃 Glass	5Low-e+15A+5厚中空玻璃，中透光，离线单银 5Low-e+15A+5 thick insulating glass, medium light transmission, offline single silver	制动 Closure	手动 Manually	锁具 Lock	配套 Support
百叶 Louver	— —	门槛 Sill	— —	执手 Handle	— —
备注 Note	电动排烟窗，消防联动 Electric smoke exhaust window, fire linkage				

编号 No.	LC1506 1500X600	名称 Name	铝合金推拉窗
		数量 Quantity	33

立面(洞口尺寸) Elevation(opening size)

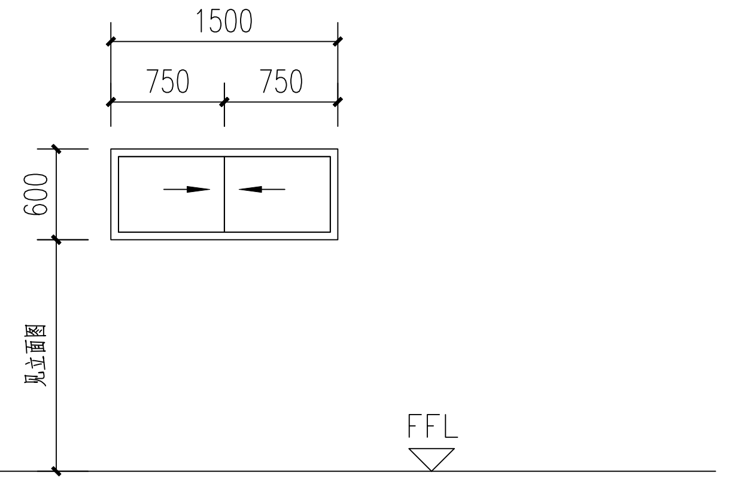

框 Frame	断热型铝合金，氟碳喷涂，隔热条高度26.0mm Heat-dissipating aluminum alloy, fluorocarbon spray, heat insulation strip height 26.0mm				
扇 Leaf	— -	铰链 Hinge	— -	纱窗 Screen	— —
玻璃 Glass	5Low-e+15A+5厚中空玻璃，中透光，离线单银 5Low-e+15A+5 thick insulating glass, medium light transmission, offline single silver	制动 Closure	手动 Manually	锁具 Lock	配套 Support
百叶 Louver	— —	门槛 Sill	— —	执手 Handle	— —
备注 Note	受力构件壁厚不小于1.6mm The wall thickness of the stressed member is not less than 1.6mm				

编号 No.	LC1531 1500X3100	名称 Name	铝合金推拉窗
		数量 Quantity	13

立面(洞口尺寸) Elevation(opening size)

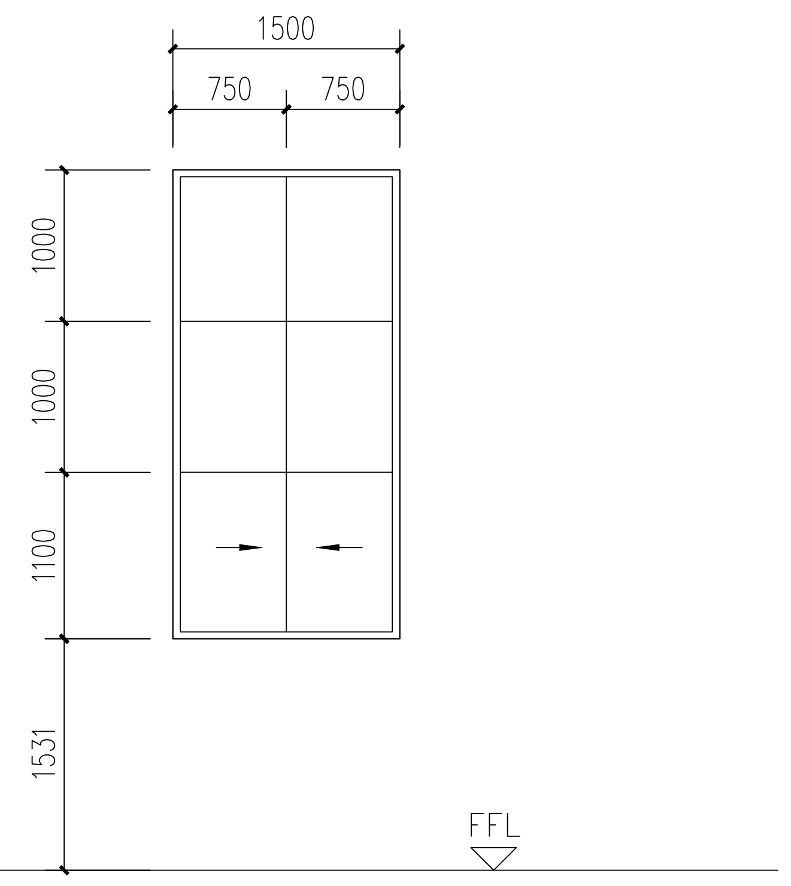

框 Frame	断热型铝合金，氟碳喷涂，隔热条高度26.0mm Heat-dissipating aluminum alloy, fluorocarbon spray, heat insulation strip height 26.0mm				
扇 Leaf	— -	铰链 Hinge	— -	纱窗 Screen	— —
玻璃 Glass	5Low-e+15A+5厚中空玻璃，中透光，离线单银 5Low-e+15A+5 thick insulating glass, medium light transmission, offline single silver	制动 Closure	手动 Manually	锁具 Lock	配套 Support
百叶 Louver	— —	门槛 Sill	— —	执手 Handle	— —
备注 Note	受力构件壁厚不小于1.6mm The wall thickness of the stressed member is not less than 1.6mm				

编号 No.	LC1836 1800X3600	名称 Name	铝合金推拉窗
		数量 Quantity	21

立面(洞口尺寸) Elevation(opening size)

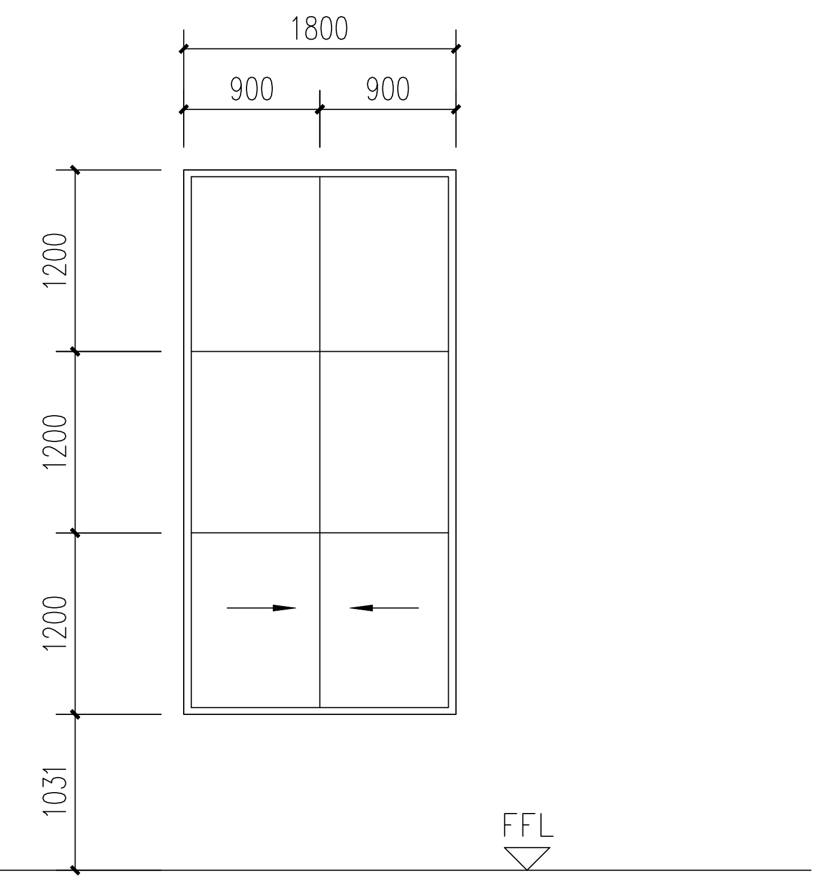

框 Frame	断热型铝合金，氟碳喷涂，隔热条高度26.0mm Heat-dissipating aluminum alloy, fluorocarbon spray, heat insulation strip height 26.0mm				
扇 Leaf	— -	铰链 Hinge	— -	纱窗 Screen	— —
玻璃 Glass	5Low-e+15A+5厚中空玻璃，中透光，离线单银 5Low-e+15A+5 thick insulating glass, medium light transmission, offline single silver	制动 Closure	手动 Manually	锁具 Lock	配套 Support
百叶 Louver	— —	门槛 Sill	— —	执手 Handle	— —
备注 Note	受力构件壁厚不小于1.6mm The wall thickness of the stressed member is not less than 1.6mm				

编号 No.	LC2421 2400X2100	名称 Name	平开双扇铝合金窗
		数量 Quantity	36

立面(洞口尺寸) Elevation(opening size)

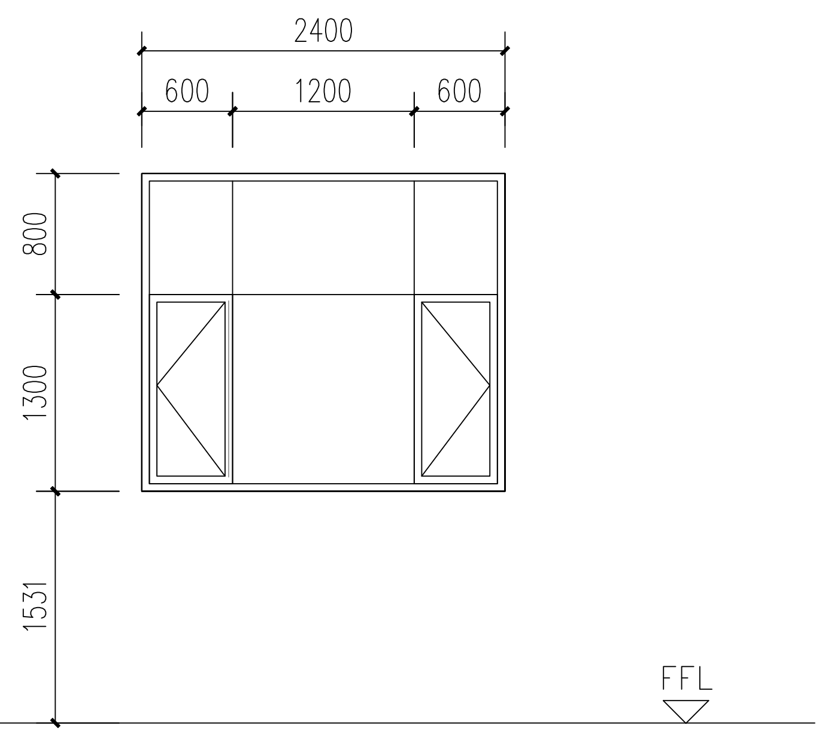

框 Frame	断热型铝合金，氟碳喷涂，隔热条高度26.0mm Heat-dissipating aluminum alloy, fluorocarbon spray, heat insulation strip height 26.0mm				
扇 Leaf	— -	铰链 Hinge	— -	纱窗 Screen	— —
玻璃 Glass	5Low-e+15A+5厚中空玻璃，中透光，离线单银 5Low-e+15A+5 thick insulating glass, medium light transmission, offline single silver	制动 Closure	手动 Manually	锁具 Lock	配套 Support
百叶 Louver	— —	门槛 Sill	— —	执手 Handle	— —
备注 Note	受力构件壁厚不小于1.6mm The wall thickness of the stressed member is not less than 1.6mm				

编号 No.	LC2431 2400X3100	名称 Name	平开双扇铝合金窗
		数量 Quantity	16

立面(洞口尺寸) Elevation(opening size)

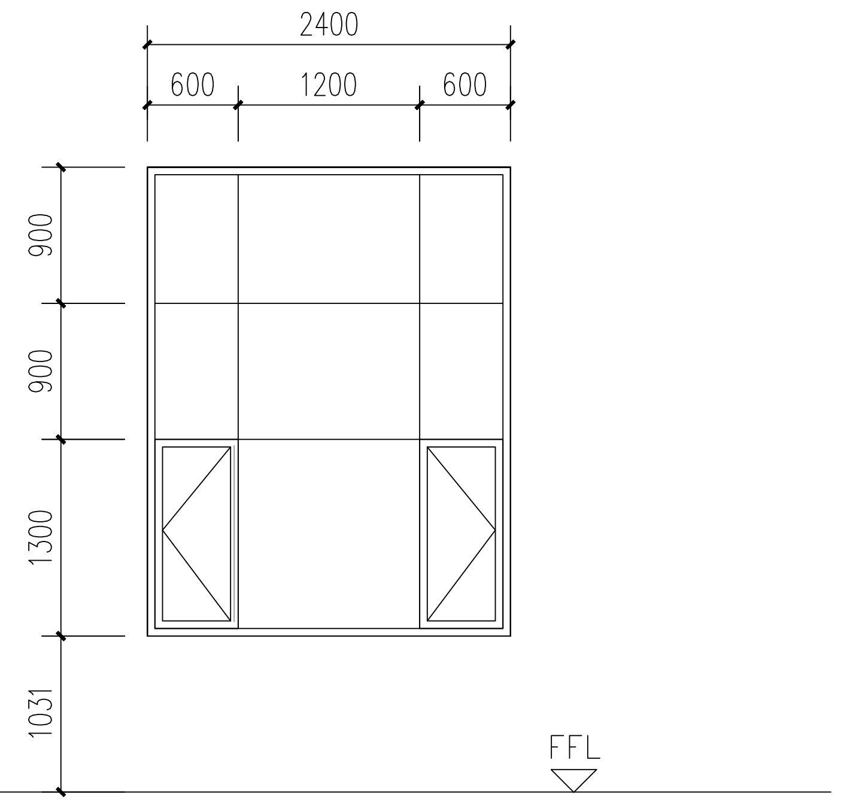

框 Frame	断热型铝合金，氟碳喷涂，隔热条高度26.0mm Heat-dissipating aluminum alloy, fluorocarbon spray, heat insulation strip height 26.0mm				
扇 Leaf	— -	铰链 Hinge	— -	纱窗 Screen	— —
玻璃 Glass	5Low-e+15A+5厚中空玻璃，中透光，离线单银 5Low-e+15A+5 thick insulating glass, medium light transmission, offline single silver	制动 Closure	手动 Manually	锁具 Lock	配套 Support
百叶 Louver	— —	门槛 Sill	— —	执手 Handle	— —
备注 Note	受力构件壁厚不小于1.6mm The wall thickness of the stressed member is not less than 1.6mm				

编号 No.	LC5006 5000X600	名称 Name	上悬铝合金窗
		数量 Quantity	12

立面(洞口尺寸) Elevation(opening size)

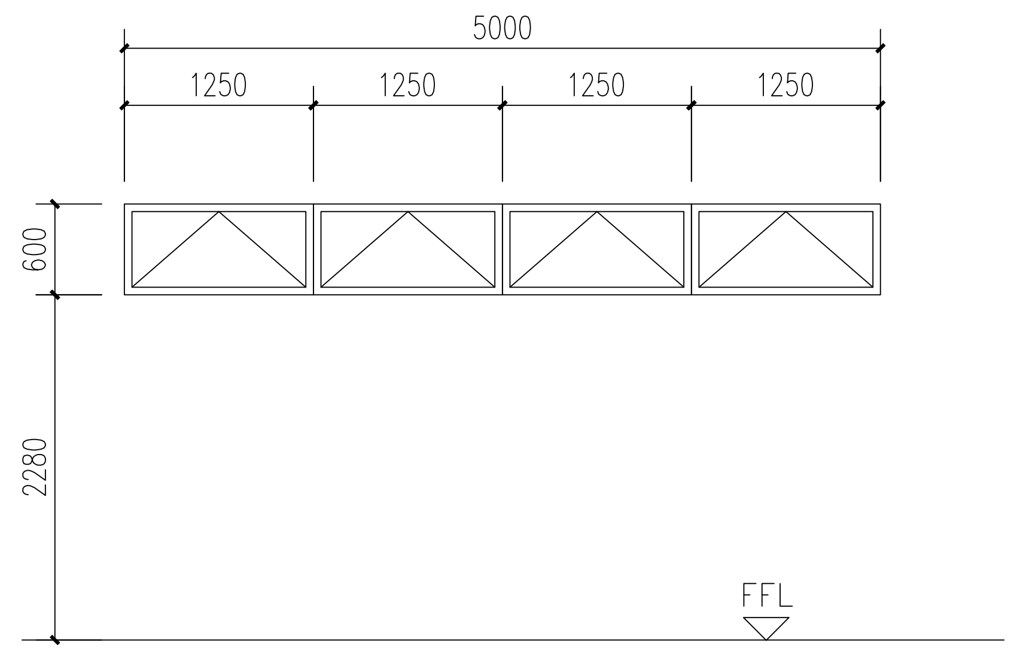

框 Frame	断热型铝合金，氟碳喷涂，隔热条高度26.0mm Heat-dissipating aluminum alloy, fluorocarbon spray, heat insulation strip height 26.0mm				
扇 Leaf	— -	铰链 Hinge	— -	纱窗 Screen	— —
玻璃 Glass	5Low-e+15A+5厚中空玻璃，中透光，离线单银 5Low-e+15A+5 thick insulating glass, medium light transmission, offline single silver	制动 Closure	手动 Manually	锁具 Lock	配套 Support
百叶 Louver	— —	门槛 Sill	— —	执手 Handle	— —
备注 Note	受力构件壁厚不小于1.6mm The wall thickness of the stressed member is not less than 1.6mm				

编号 No.	LC5006 5000X600	名称 Name	铝合金固定窗
		数量 Quantity	12

立面(洞口尺寸) Elevation(opening size)

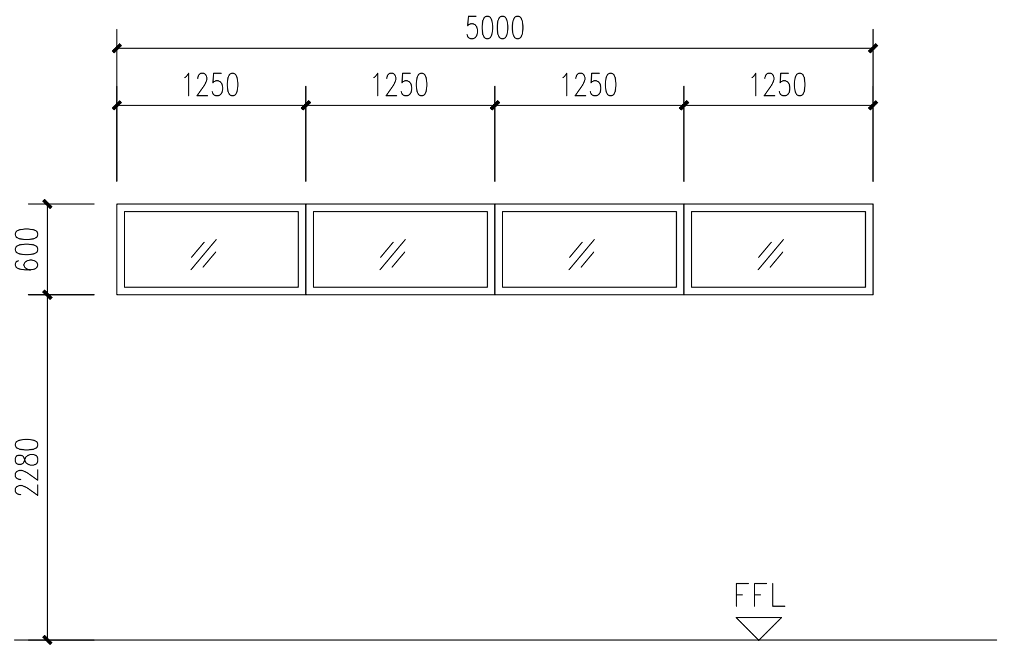

框 Frame	断热型铝合金，氟碳喷涂，隔热条高度26.0mm Heat-dissipating aluminum alloy, fluorocarbon spray, heat insulation strip height 26.0mm				
扇 Leaf	— -	铰链 Hinge	— -	纱窗 Screen	— —
玻璃 Glass	5Low-e+15A+5厚中空玻璃，中透光，离线单银 5Low-e+15A+5 thick insulating glass, medium light transmission, offline single silver	制动 Closure	手动 Manually	锁具 Lock	配套 Support
百叶 Louver	— —	门槛 Sill	— —	执手 Handle	— —
备注 Note	受力构件壁厚不小于1.6mm The wall thickness of the stressed member is not less than 1.6mm				

编号 No.	LC1215 1200X1500	名称 Name	铝合金固定窗
		数量 Quantity	1

立面(洞口尺寸) Elevation(opening size)

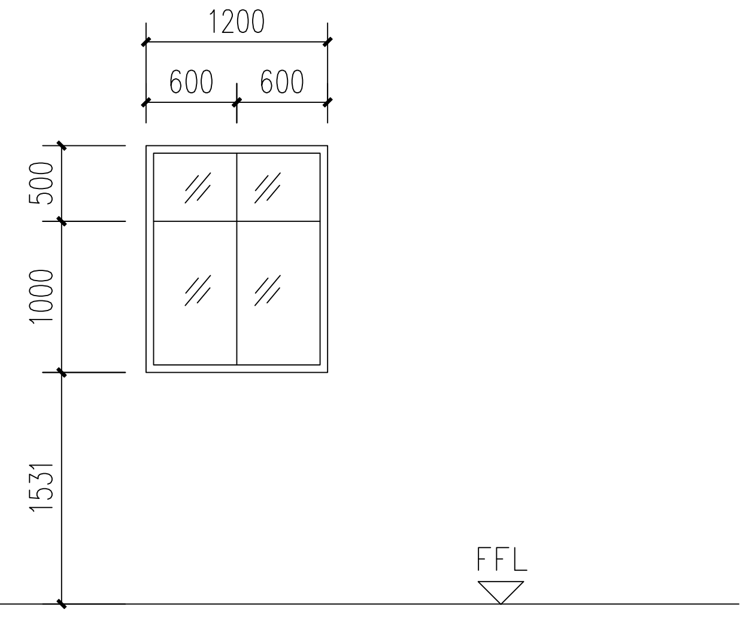

框 Frame	断热型铝合金，氟碳喷涂，隔热条高度26.0mm Heat-dissipating aluminum alloy, fluorocarbon spray, heat insulation strip height 26.0mm				
扇 Leaf	— -	铰链 Hinge	— -	纱窗 Screen	— —
玻璃 Glass	6厚白玻 6 thick white glass	制动 Closure	— -	锁具 Lock	配套 Support
百叶 Louver	— —	门槛 Sill	— —	执手 Handle	— —
备注 Note	受力构件壁厚不小于1.6mm The wall thickness of the stressed member is not less than 1.6mm				

Description:

1、The number of keys is confirmed by the owner and the supplier.
2、Doors and windows should be confirmed with the owner before ordering.
3、If the individual quantity in this door and window table does not match the actual dosage, the actual dosage shall prevail.
4、The division of the glass partition is only an indication, and the division is determined by the professional manufacturer according to the actual situation on the spot and the aesthetics.
5、All doors and windows are manufactured and installed by quality assurance manufacturers.
6、The high window on the wall (including the power window) is equipped with a manual hinge opening.
7、Aluminum alloy gold rainproof louvers are equipped with insect nets.
8、The sliding window sash should have means to prevent detachment from the outside, and when used for the external wall, a device for preventing the sash from falling out of the room should be provided.
9、A transparent glass door should be marked to prevent personal injury.
11、The height of the door opening should be calculated from the completion of the building. All doors and windows must be checked for actual hole size before machining.
12、Except as noted, see the "General Description of Building Construction Drawing Design".
13、< Indicates the opening direction of the door and window.
14、If there are no corresponding windows and doors in the doors and windows of the door and window table, it must be confirmed with the design before purchase, customization and construction.
15、The overall heat transfer coefficient of the external doors and windows with energy-saving requirements shall meet the requirements of the corresponding external doors and windows in the "Building Energy Efficiency Calculation Analysis Report". Exterior window structure: metal heat insulation profile (insulation strip height 26.0mm (5Low-e+15A+5 (medium light transmission, offline single silver), heat transfer coefficient 2.2W/m2.K, glass shading coefficient 0.65, window frame The coefficient is 0.75, the visible light transmittance is 0.60. The openable area of the outer window is not less than 30% of the window area. The outer door structure: 1.0mm steel plate + aluminum silicate fiber cotton (dry density 160Kg/m3) + 1.0mm steel plate), heat transfer coefficient The airtightness, watertightness and wind pressure rating of 2.2W/m2.K outer door and window shall comply with the relevant provisions of GB/T7106-2008, "Airtight, Watertight, Wind Pressure Performance Classification and Detection Methods for Building Exterior Doors and Windows", Airtight The property is not less than grade 6, that is, 1.5q1>1.0m3/m•h; the watertightness is not lower than grade 4, that is, 350Pa⩽ΔP⩽500Pa; the wind resistance is not lower than grade 5, that is, 3000Pa⩽P3⩽3500pa. The sound insulation performance classification is not lower than the level 4 of GB/T8485-2008 in the classification and detection method of air sound insulation performance of building doors and windows, that is, 40dB>R+C⩾35dB.
16、Except as noted, the wall thickness of ordinary steel door frame is not less than 1.5mm, and the wall thickness of steel door panel is not less than 0.8mm. The minimum wall thickness of the aluminum alloy door is 2.0mm, and the minimum wall thickness of the aluminum alloy window is 1.6mm.
17、Metal and heat insulation profiles for door and window glass (insulation strip height 26.0mm) (5Low-e+15A+5 (medium light transmission, offline single silver), heat transfer coefficient 2.2W/m2.K, glass shading coefficient 0.65, window The frame factor is 0.75, and the visible light transmittance is 0.60. Regardless of the size of the glass, it is necessary to use tempered glass for various ceilings, indoor partitions, inclined assembly windows, stairs, balconies, platforms, corridors, halls, and public panels. Building entrances, entrance halls and other parts that may injure people; fireproof glass with fire protection requirements shall comply with the "Technical Regulations for the Application of Building Glass" JGJ113-2015 7.2 and the "Building Safety Glass Management Regulations" Development and Reform Commission [2003] 2116 and local supervisors Relevant regulations of the department. All glass, single glass, 5mm thick glass on the door and window is greater than or equal to 0.5m2, and the glass with thickness of 6mm is greater than or equal to 0.9m2. Tempered glass should be used. The glass for blocking the vertical wall of the smoke is made of 12 thick laminated fireproof glass. There shall be no dust or water vapor in the hollow layer of the hollow glass. The coating layer of the single-coated glass and the frosted surface of the frosted glass shall face indoors; the single-coated glass of the insulating glass shall be the most The outer layer and the coating layer should face indoors. The size of the door and window glass should be matched with the frame slot, and the door and window glass should not directly contact the metal profile; the glass should be in close contact with the positioning block, the caulking strip and the sealing paste. It should be firm and sealed.
18、The smoke prevention performance of the fire shutter door should be less than 0.2m3/m2.min when the pressure difference is 20Pa. The fire endurance of the fire shutter should comply with the current national standard "Fireproofing Test Method for Fireproof Roller" GB7633 Judging conditions. Fire shutter doors should be equipped with fire detectors and alarm systems.
19、All swing doors have door closers and double fire doors with sequencers.

编号 No.	LC1509 1500X900	名称 Name	铝合金推拉窗
		数量 Quantity	5

立面(洞口尺寸) Elevation(opening size)

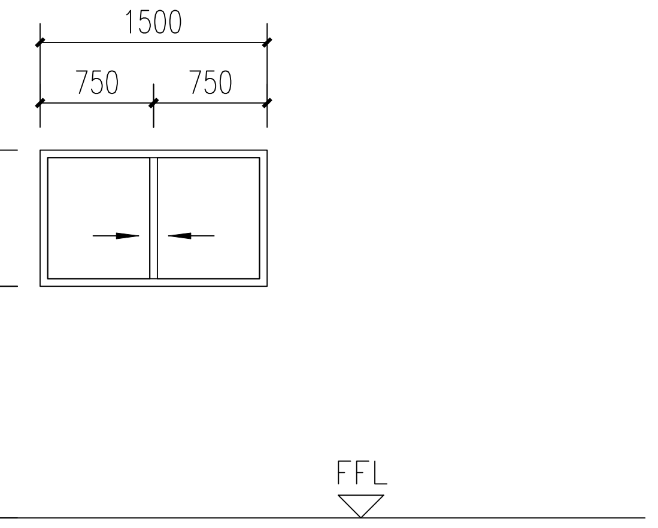

框 Frame	断热型铝合金，氟碳喷涂，隔热条高度26.0mm Heat-dissipating aluminum alloy, fluorocarbon spray, heat insulation strip height 26.0mm				
扇 Leaf	— -	铰链 Hinge	— -	纱窗 Screen	— —
玻璃 Glass	5Low-e+15A+5厚中空玻璃，中透光，离线单银 5Low-e+15A+5 thick insulating glass, medium light transmission, offline single silver	制动 Closure	手动 Manually	锁具 Lock	配套 Support
百叶 Louver	— —	门槛 Sill	— —	执手 Handle	— —
备注 Note	受力构件壁厚不小于1.6mm The wall thickness of the stressed member is not less than 1.6mm				

专业 Discipline	签署 Signature
电照 LI	
工艺 PR	
供电 EL	
自控 IC	
通信 CO	
给水排水 PL	
空调通风 HV	
工业管道 PP	
总图 MP	
建筑 AR	
结构 ST	

缩引图 Keyplan

版本 REV.	版本说明 Description	日期 Date
1	IFC	20190329

注册执业印章 Registered Stamp

注册执业师 Professional Engineer

出图印章 Print Stamp

咨询公司 Consultant

JLL®

设计单位 Designer

信息产业电子第十一设计研究院科技工程股份有限公司
The IT Electronics Eleventh Design & Research Institute
Scientific and Technological Engineering Corporation Ltd.
中国 成都 新华大道双林路251号
NO. 251 Shuanglin Rd. Xinhua Avenue. Chengdu, China
邮编：610021 P.C.:610021
十一科技
设计证号: A151000523

建设单位 Owner

Hengtong Optic-Electric
India Private Ltd

项目名称 Project Name

Indian Optical Fiber
and Cable Project

图纸名称 Drawing Title

建筑—Architecture
光纤光缆厂房—Optical Fiber Plant
门窗大样图四
DOOR AND WINDOW PICTURE 4

设计 Designed By	梁智浩		项目号 Project No.	2017-08设-043
制图 Drawn By	梁智浩		设计阶段 Des. Stage	施工图
校对 Checked By	张凤磊		专业 Discipline	建筑
审核 Reviewed By	赵军		比例 Scale	1:100
审定 Approved			版本 Version	1
专业负责人 Discipline Leader	赵军		日期 Date	20190329
项目负责人 Design Manager	汤敏		页数 Sheet No.	
图号 Drawing No.	HTIN-AR-01-DWS-00-004			