

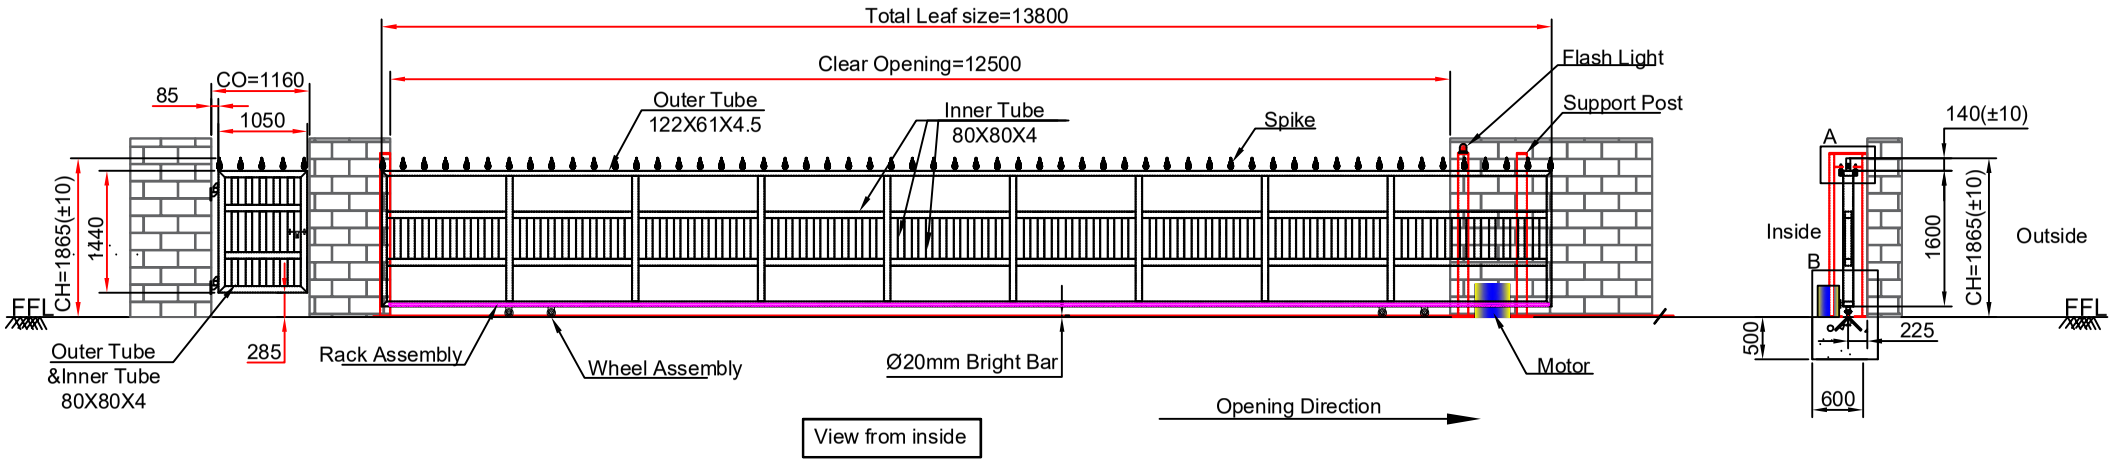


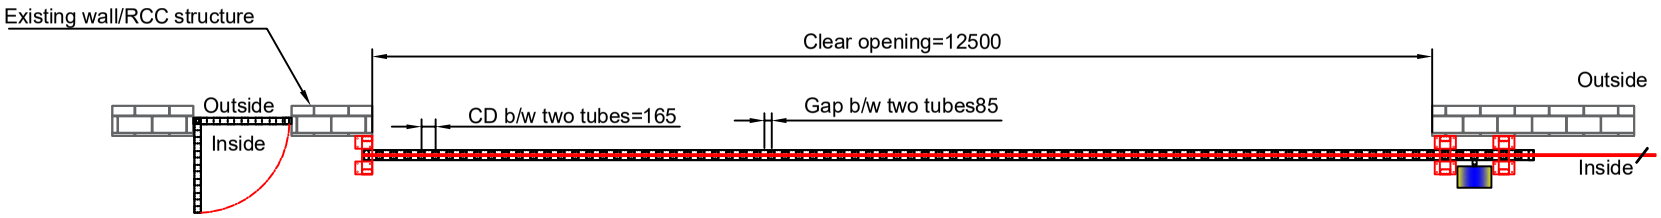


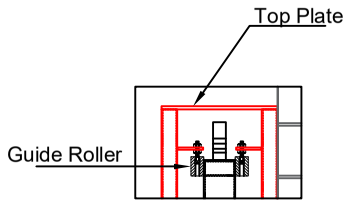

DEATILS : A

**CO=CLEAR OPENING
**CH=CLEAR HEIGHT

DEATILS : B

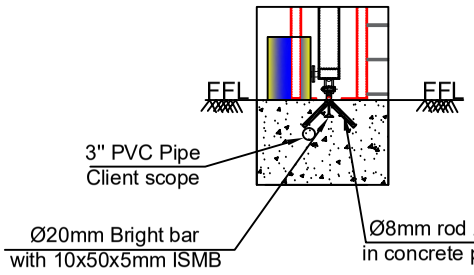

Note:-

1.All Dimension are in MM.
2.All Civil work and if required motor foundation or ms bracket will be in Client scope
3.Civil,Installation and Fabrication Tolerance will be ±20mm
4.Reuired Parking will be 13900mm
5.Surface Finish(painting): Approved RAL 9011(Graphite Black)
6.Nihva will provide 2core wire, 4core wire and flexible conduit pipe 19ID upto 7mtr remaining required wire and pipe will be in client scope.

Rev No.	Revision	Date	Revised By
3.	Wicket gate leaf size has been changed from 1600mm to 1440mm	19/12/2022	Sujata
2.	Gap between two tube gas been changed as per client	07/12/2022	Sujata
1.	Electrical wire details has been added.	15/10/2022	Sujata

This drawing & design is the property of NIHVA TECHNOLOGIES. Not to be sold or copied to any other concern.

TITLE:-
Automatic Sliding with Wicket Gate

	NAME	DATE	SIGN
DRAWN	SUJATA	13/10/2022	
CHECK	A.K	13/10/2022	
APPRD.	V.T	13/10/2022	

If any queries contact : design@nihva.com

ALL DIMENSION ARE IN mm

NIHVA
NIHVA TECHNOLOGIES PVT. LTD.

NIHVA TECHNOLOGIES PVT. LTD. PUNE
Tel : 020 66304033
Email:- info@nihva.com
Website:- www.nihva.com

CLIENT - Suraj Buildcon Pvt Ltd
LOCATION - Pune
PRODUCT - A.Sliding and Wicket Gate | QTY-00
DWG NO:- NIHVA/22-23/CLT/0141 | REV-03
SCALE: NTS | SCALE:-- 1:1 | SHEET: 01 OF 01