

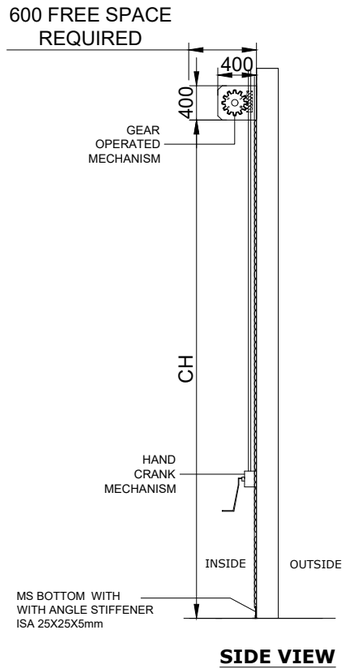



SIDE VIEW

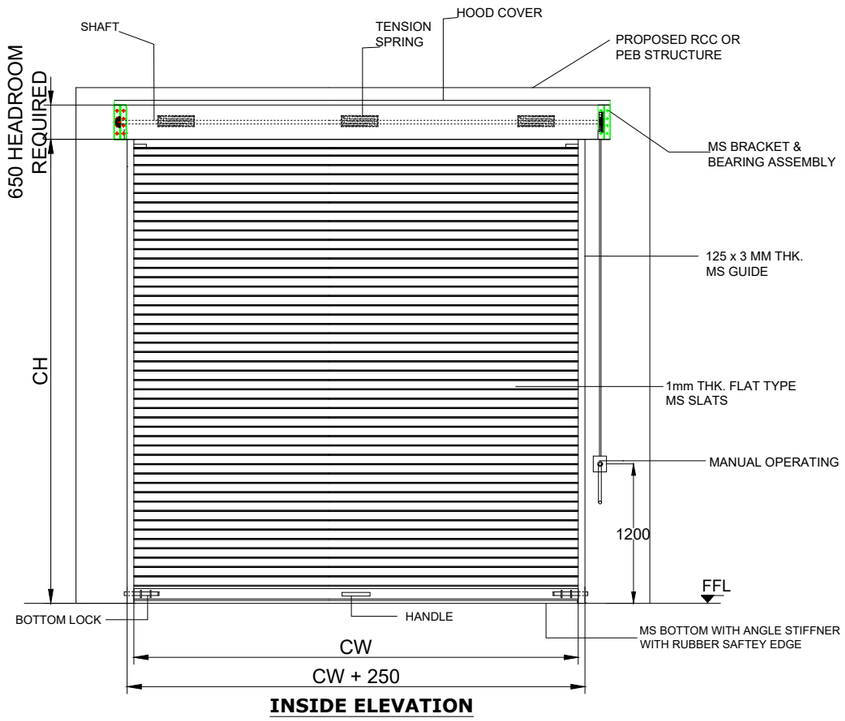

INSIDE ELEVATION

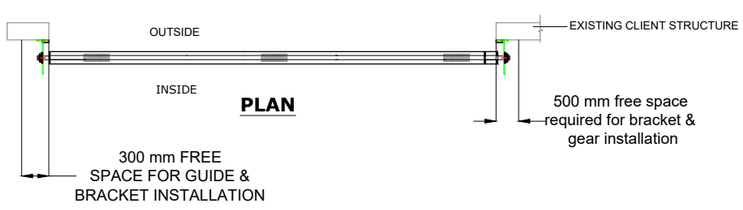


PLAN

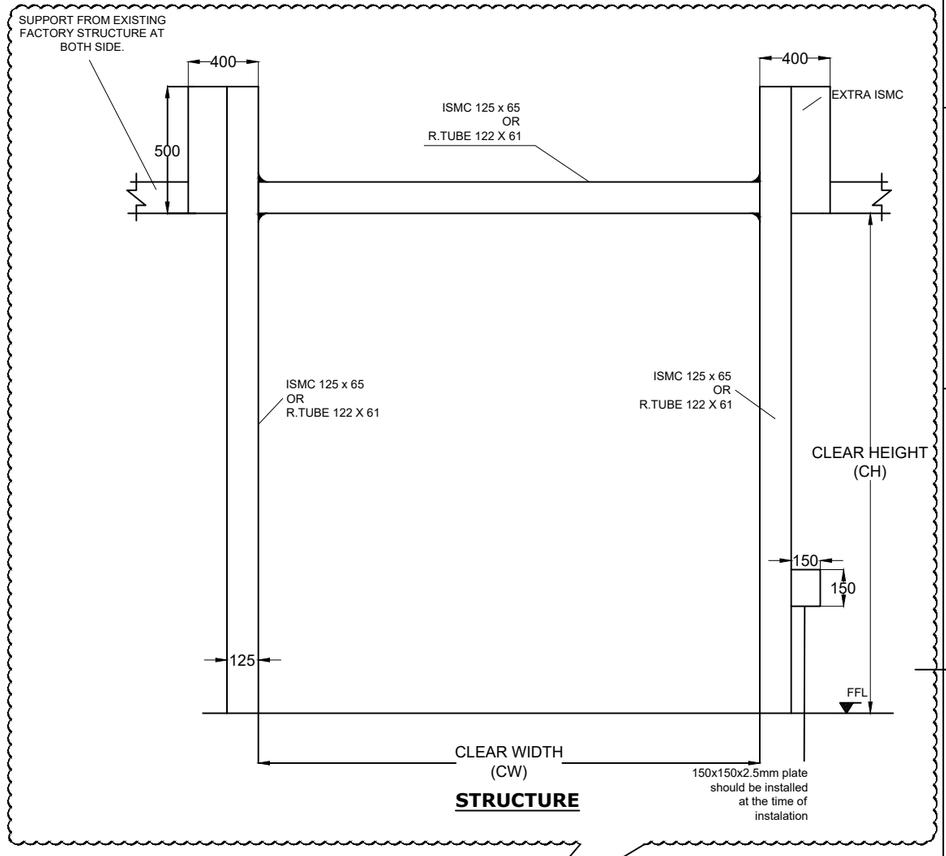

STRUCTURE


IF STRUCTURE REQUIRED FOR SHUTTER IS IN CLIENT'S SCOPE

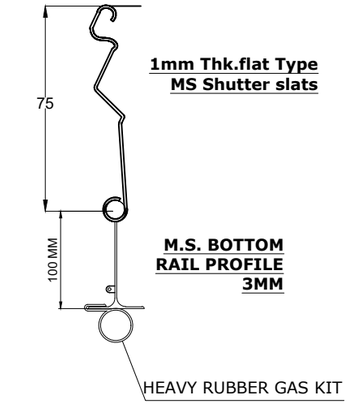

1mm Thk.flat Type MS Shutter slats

M.S. BOTTOM RAIL PROFILE 3MM

M.S. BOTTOM RAIL PROFILE 2.5MM

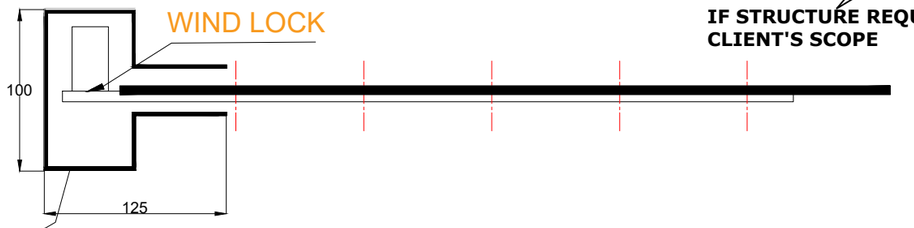

125 X 3 MM THK. MS GUIDE

" T " TYPE GUIDE

SR NO	(CW) CLEAR WIDTH	(CH) CLEAR HEIGHT	QUANTITY
1	4000	4500	07 NOS

NOTE-
1. ALL CIVIL WORK WILL BE CLIENT'S SCOPE.
2.IF STRUCTURE REQUIRED FOR SHUTTER IS IN CLIENT'S SCOPE.

This drawing & design is the property of NIHVA TECHNOLOGIES. Not to be sold or copied to any other concern.

	NAME	SIGN	DATE
DRAWN	B.S.		04.10.2025
CHECK	V.T.		04.10.2025
APPRD.	V.T.		04.10.2025

TITLE: GEAR OPERATED ROLLING SHUTTER

NIHVA TECHNOLOGIES PVT. LTD.
NIHVA TECHNOLOGIES PVT. PUNE
Tel : 020 66304033
Email:- info@nihva.com
Website:- www.nihva.com

CLIENT - VTP
PROJECT -
SITE LOCATION -
If any queries contact : design@nihva.com
DWG. NO. : NIHVA/21-22/VDR/020
REV- R00
ALL DIMENSION ARE IN mm
SCALE: NTS
WT:
SHEET: 01 OF 01