
CLIENT													
WEIGHT ESTIMATION SHEET													
CLIENT			ECR BUILDTECH PRV LTD								DATE	16-01-2025	
PROJECT			Motorised Telescope Sliding Gate (One side opening)								LOCATION	RAJSTHAN	
FINISH SIZE			14 m x 1.8m								PREPARED BY	BHARATI	
SR	**DESC**	**DETAILS**	**MATERIAL GRADE**	**SP.GRAVITY**	**DIA**	**WIDTH**	**HEIGHT**	**THICKNESS**	**LENGTH**	**UOM**	**QUANTITY**	**WEIGHT**	**REMARK**
1	SINGLE LEAF (4670MM X 1800 MM)	Tube - Outer Frame	MS	7.85		100	50	3	38820	mm	1	263	954
		Vertical Inner Support - Tube	MS	7.85		40	40	2.5	234600	mm	1	691	
2		Post	MS	7.85		72	72	3	18400	No's	1	18	
3	Bottom Track	En 8 Bright Hardchrome Bar	En8	7.85	25				45	M	1	176	
		If ISMC C channel 100 x 50 x 5 in our scope	MS	7.85					45	M	1	477	
		Wire Rope			8				31020	M	1		
		Rack & pinion							12	M	1		
4	Accessories	Bottom Side wheel Assembly (4 inch)	MS	7.85						No's	6		
		Nylon Roller with bearing								No's	8		
										Weight For Required Qty	1	1625	
										Weight Including Safety Factor	1.5	2438	
Mode Of Operation = Motorised													
Motor Selection = According		1430.8	kg										
Tow Tube CD = 100 mm													

REFERENCE IMAGE

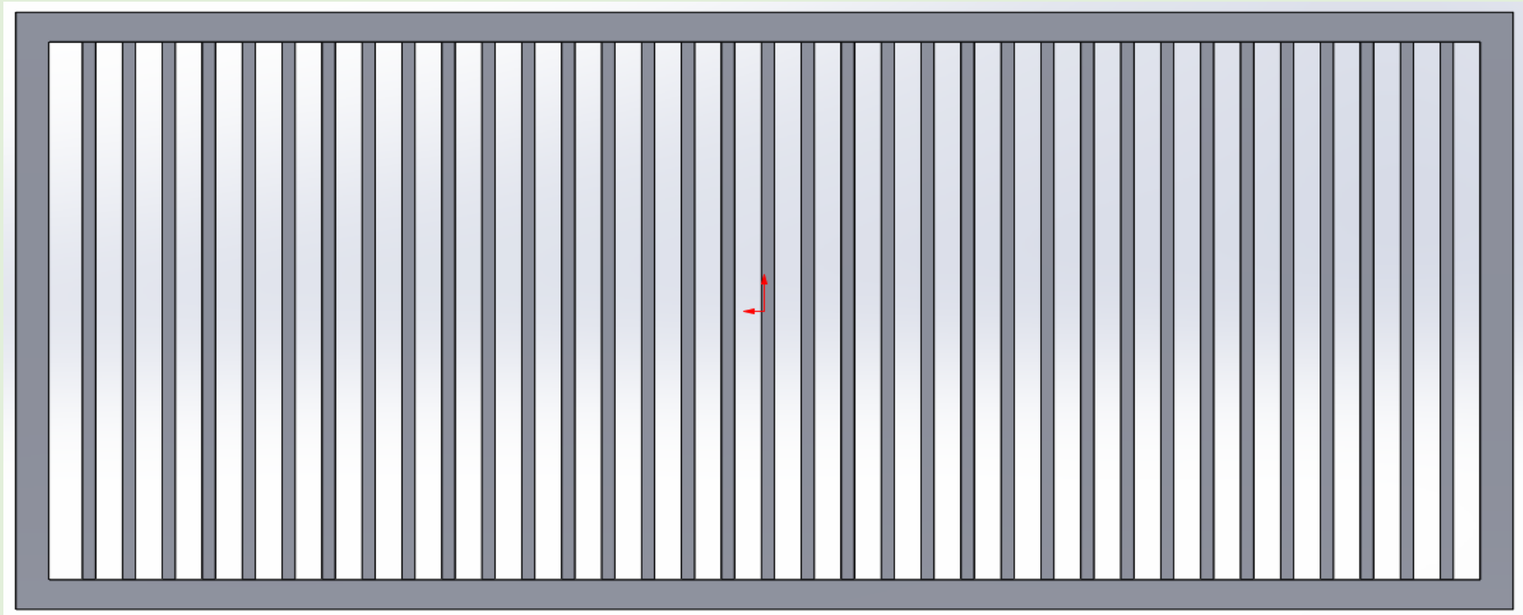

3 Leaf -4670 x 1800MM

Gate Qty - 01

CLIENT

WEIGHT ESTIMATION SHEET

CLIENT	ECR BUILDTECH PRV LTD	DATE	16-01-2025
PROJECT	Motorised Telescope Sliding Gate (One side opening)	LOCATION	RAJSTHAN
FINISH SIZE	8.1 m x 1.8m	PREPARED BY	BHARATI


SR	DESC	DETAILS	MATERIAL GRADE	SP.GRAVITY	DIA	WIDTH	HEIGHT	THICKNESS	LENGTH	UOM	QUANTITY	WEIGHT	REMARK
1	SINGLE LEAF (3000MM X 1800 MM)	Tube - Outer Frame	MS	7.85		100	50	3	28800	mm	1	195	646
		Vertical Inner Support - Tube	MS	7.85		40	40	2.5	153000	mm	1	450	
2		Post	MS	7.85		72	72	3	18400	No's	1	18	
3	Bottom Track	En 8 Bright Hardchrome Bar	En8	7.85	25				25	M	1	99	
		If ISMC C channel 100 x 50 x 5 in our scope	MS	7.85					25	M	1	265	
		Wire Rope			8				21000	M	1		
		Rack & pinion							12	M	1		
4	Accessories	Bottom Side wheel Assembly (4 inch)	MS	7.85						No's	6		
		Nylon Roller with bearing								No's	8		
										Weight For Required Qty	1	1028	
										Weight Including Safety Factor	1.5	1542	

Mode Of Operation = Motorised

Motor Selection = According | 968.6 | kg

Tow Tube CD = 100 mm

REFERENCE IMAGE

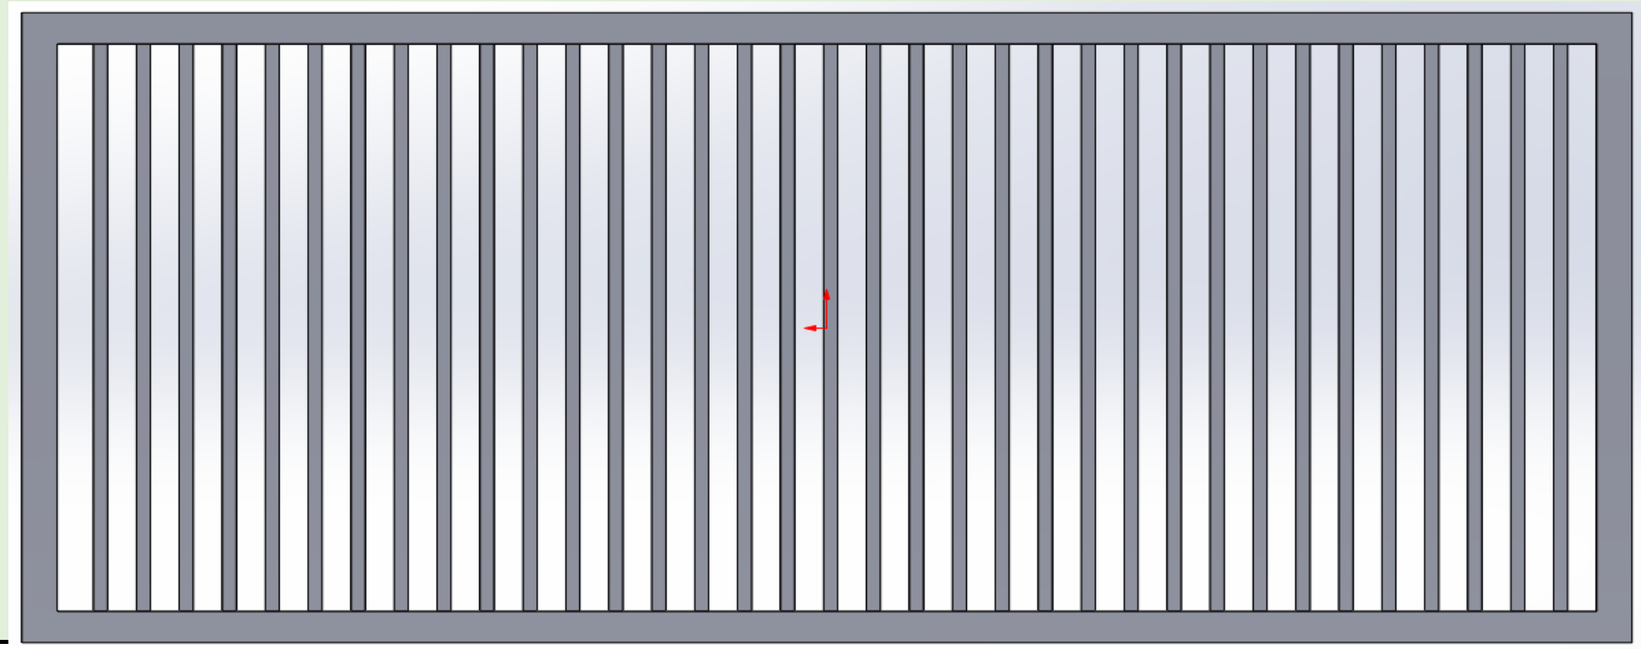

af -4670 x 1800MM

Gate Qty - 01

CLIENT

WEIGHT ESTIMATION SHEET

CLIENT			Gyandhara								DATE	16-01-2025	
PROJECT			Wicket Gate								LOCATION	RAJSTHAN	
FINISH SIZE			990 MM x 1.8 m								PREPARED BY	Bharati	
SR	**DESC**	**DETAILS**	**MATERIAL GRADE**	**SP.GRAVITY**	**DIA**	**WIDTH**	**HEIGHT**	**THICKNESS**	**LENGTH**	**UOM**	**QUANTITY**	**WEIGHT**	**REMARK**
1	SINGLE LEAF (990 MM X 1.8 M)	Tube - Outer Frame	MS	7.85		100	50	3	5580	mm	1	38	89
		Vertical Inner Support - Tube	MS	7.85		50	50	2	17000	mm	1	51	Weight OF leaf
3	Accessories	Hinges	MS	7.85						No's	3	0	
		Manual Lock	MS	7.85						No's	1		
		Tower Bolt	MS	7.85						No's	1		
										Weight For Required Qty	1	89	
										Weight Including Safety Factor	1.5	134	

Mode Of Operation = Manual

REFERENCE IMAGE

