
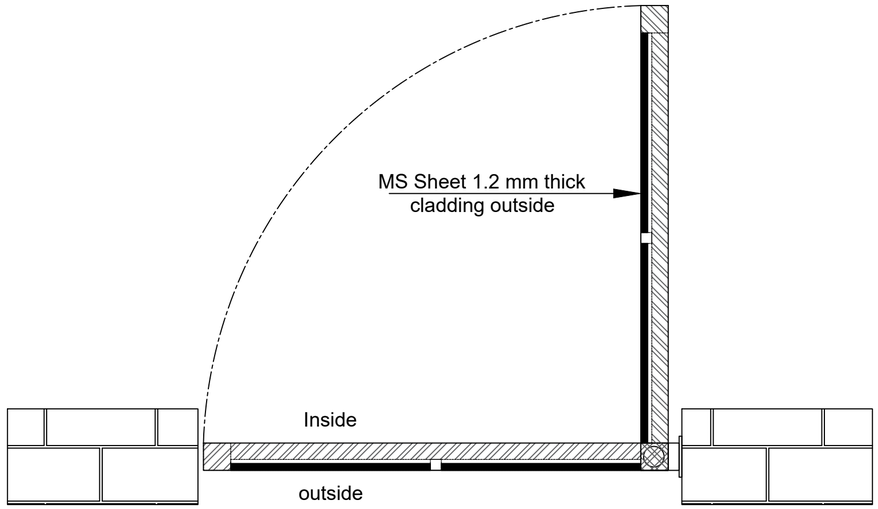


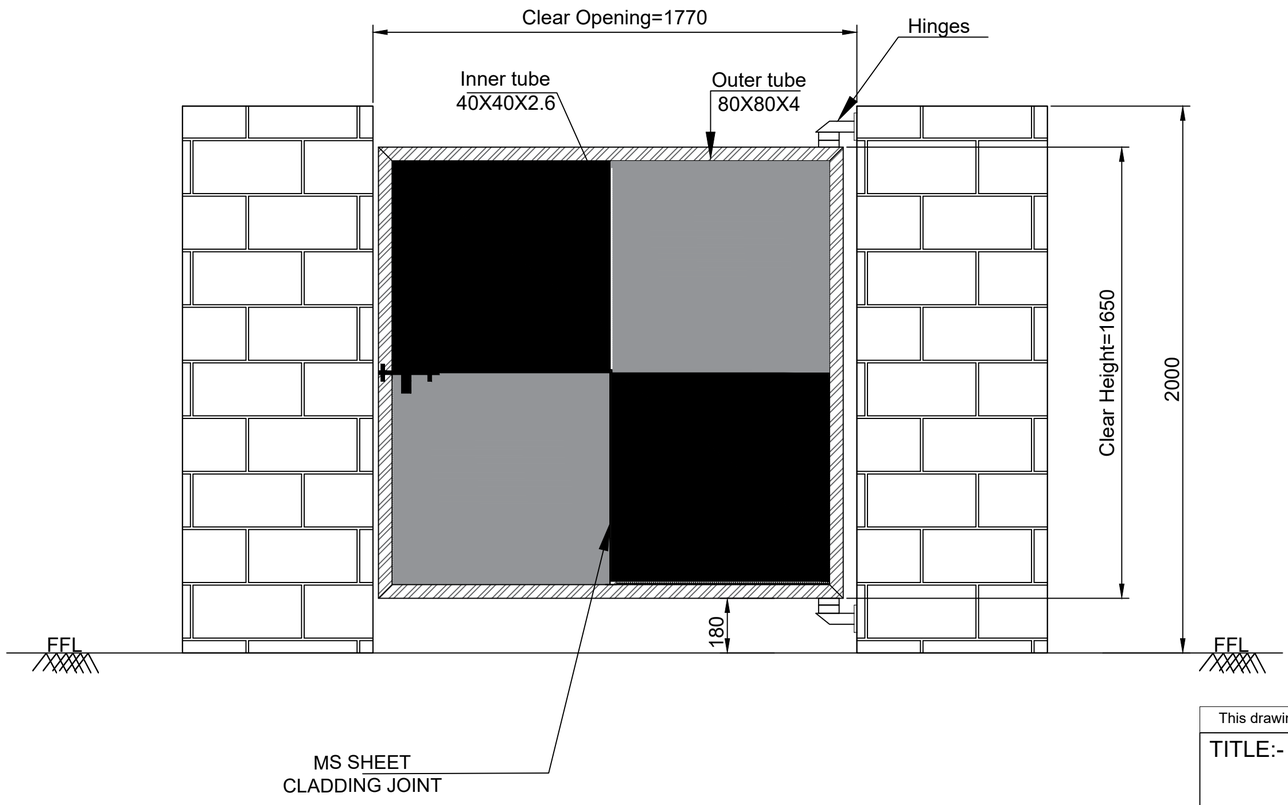

Note:-


1.All Dimension are in MM.

2.Required all civil work is in Client Scope.

3.Installation and Fabrication tolerance will be ±20mm

4. Coating : Approved RAL 9002

Rev No.	Revision	Date	Revised By
1	Revision Done As Per Client Requirements	23/07/2022	Sujata

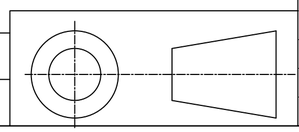

This drawing & design is the property of NIHVA TECHNOLOGIES. Not to be sold or copied to any other concern.

TITLE:- WICKET GATE

NIHVA TECHNOLOGIES PVT. LTD.

NIHVA TECHNOLOGIES PVT. LTD. PUNE
Tel : 020 66304033
Email:- info@nihva.com
Website:- www.nihva.com

	NAME	DATE	SIGN
DRAWN	M.SUTAR	19-07-2022	
CHECK	M.SUTAR	19-07-2022	
APPRD.	A.KURHADE	19-07-2022	

If any queries contact : design@nihva.com

ALL DIMENSION ARE IN mm

CLIENT - S.S.GHORPADE CONSTRUCTIONS PVT. LTD.

LOCATION -

PRODUCT - WICKET GATE

DWG NO:- NIHVA/22-23/CLT/0082 REV- 0

SCALE: NTS SCALE:-- 1:1 SHEET: 01 OF 01