

1

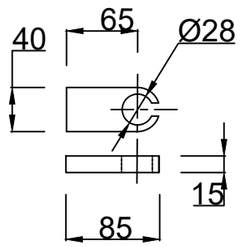


MNTG. BRACKET
40 X 85 X 15 MM THK
MTRL - M.S.
QTY= 40 NOS.

2

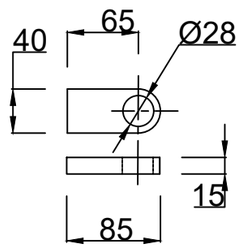


MNTG. BRACKET
40 X 85 X 15 MM THK
MTRL - M.S.
QTY= 20 NOS.

3

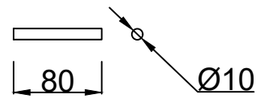

ROUND BAR
- DIA 16 X 80 MM
MTRL - M.S.
QTY= 20 NOS.

4

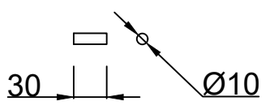


ROUND BAR
- DIA 16 X 30 MM
MTRL - M.S.
QTY= 20 NOS.


5

ROD 25 X 900 L
MTRL - M.S.

QTY= 20 NOS.

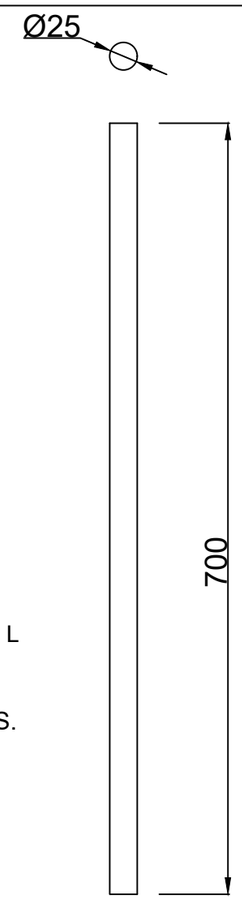

6

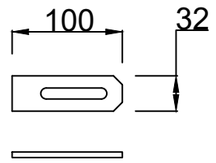


HANDLE PLATE
32 X 100 X 5 MM THK
MTRL - M.S.
QTY= 20 NOS.

A


SUBASSEMBLY AT SHOP
PER HEIGHT MNTG PLATE

QTY=65
NOS

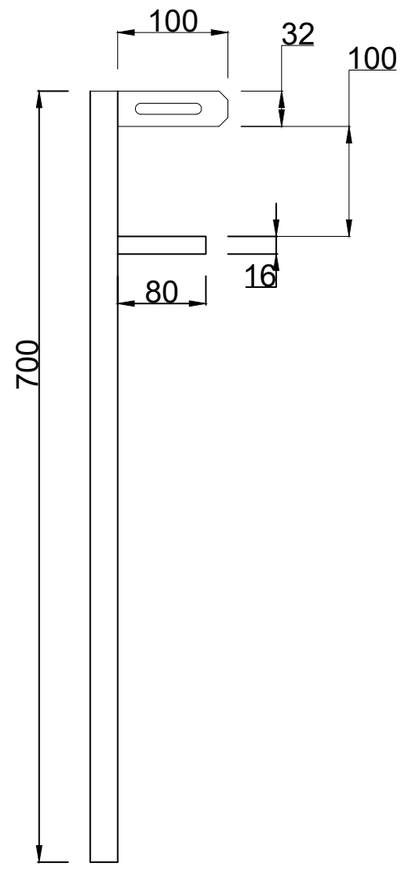

B

FINAL FITTING AT SITE
PER HEIGHT MNTG PLATE

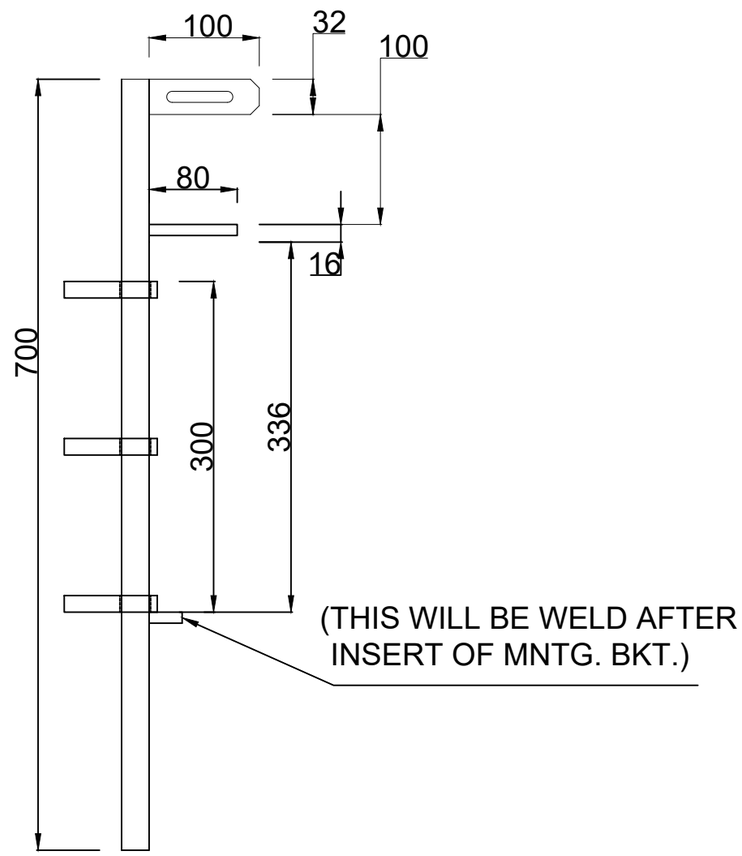

This drawing & design is the property of NIHVA TECHNOLOGIES. Not to be sold or copied to any other concern.

TITLE:- CRM DOORS TOWER BOLT ASM				NIHVA TECHNOLOGIES PVT. LTD. PUNE Tel : 020 66304033 Email:- info@nihva.com Website:- www.nihva.com
	NAME	DATE	SIGN	
DRAWN	M.SUTAR	15/06/2022		CLIENT - NIHVA TECHNOLOGIES PVT.LTD
CHECK	M.SUTAR	15/06/2022		LOCATION -
APPRD.				PRODUCT - SLIDING DOOR
If any queries contact : design@nihva.com				DWG NO:-NIHVA/22-23/MNFG/0036 / REV- 0
ALL DIMENSION ARE IN mm				SCALE: NTS / SCALE:-- 1:1 / SHEET: 01 OF 01

	Date	Revised By