
MAINTENANCE STOPPER

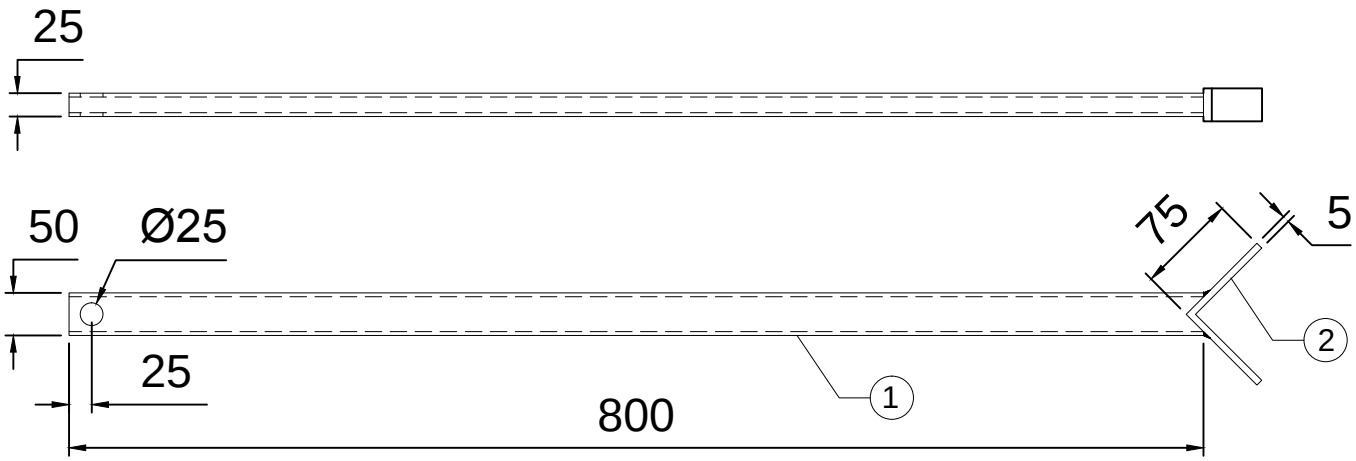

1. SQ .TUBE 50 X 25 X 3 THK X 800L = 2 NOS
2. ISA 75 X 75 X 5 X 35L = 2 NOS

TOLERANCE - ±5mm

This drawing & design is the property of NIHVA TECHNOLOGIES. Not to be sold or copied to any other concern.

TITLE				
MAINTENANCE STOPPER DRG				NIHVA TECHNOLOGIES PVT. LTD.
	NAME	SIGN	DATE	
DRAWN	PRADEEP		05.09.2018	CLIENT -
CHECK	PRADEEP		05.09.2018	PROJECT - DLSD1009
APPRD.	PRADEEP		05.09.2018	SITE LOCATION -
If any queries contact : design@nihva.com				DWG. NO. : NIHVA/18-19/MFG/DLSD1009/009
ALL DIMENSION ARE IN mm				SCALE: NTS / WT: / REV- 0

NIHVA TECHNOLOGIES PVT. LTD. PUNE
Tel : 020 66304033
Email:- info@nihva.com
Website:- www.nihva.com