
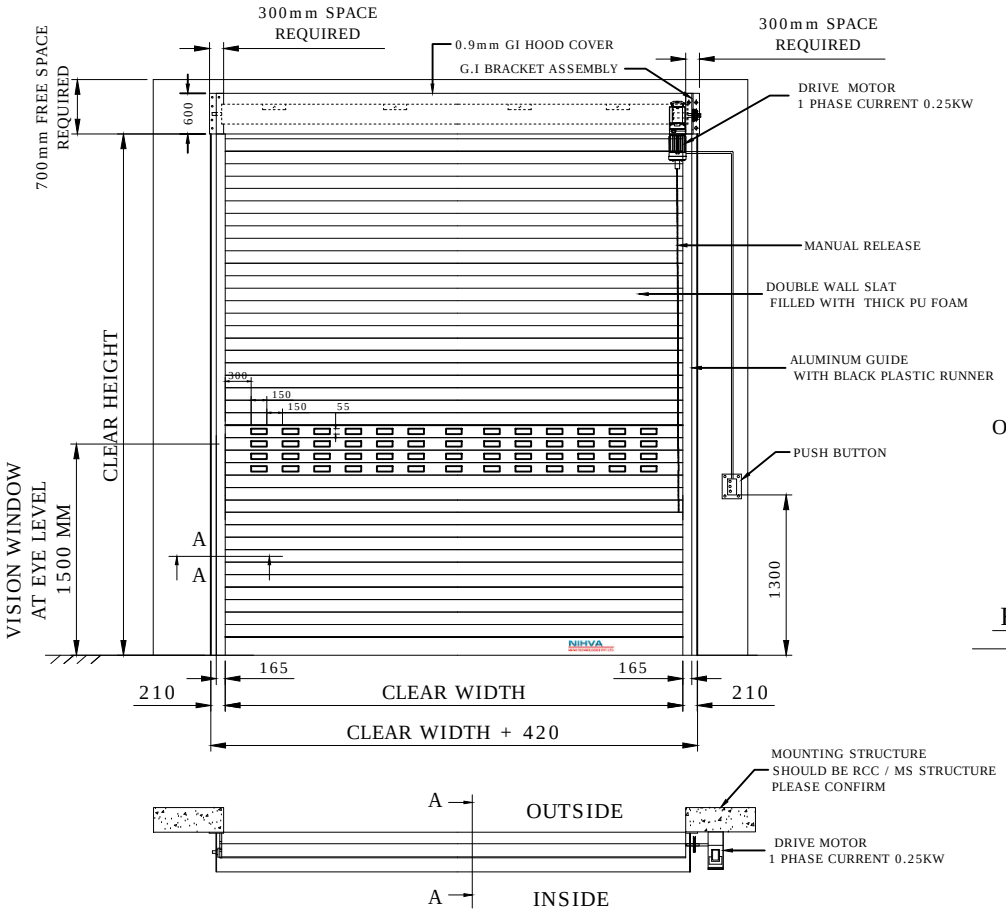


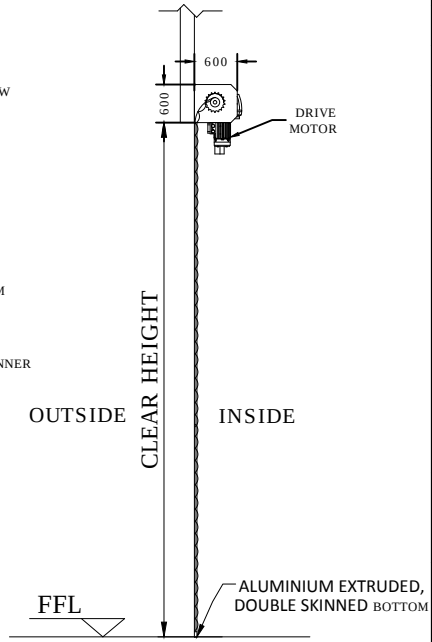


Section A-A

NOTE : DOOR TO BE FIXED FROM INSIDE ONLY

STANDARD COLOR OF SLATS & SHUTTER -RAL9002 (GRAY WHITE)

Main Slats
Double Wall Rolling Shutter



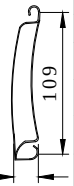

DIMENSION :

CLEAR WIDTH	CLEAR HEIGHT	QUANTITY
5000 mm	4500 mm	1 NO

MATERIAL :

THICKNESS :

CLIENT SCOPE :-

1. STEEL STRUCTURE PROCUREMENT, FIXING & STRENGTH IS CLIENT RESPONSIBILITY.
2. 1 PHASE SUPPLY SHOULD BE PROVIDED.
3. SOLID STATE INLINE (UPS/STABILIER) 2KVA CAPACITY REQUIRED.

NOTES :-
1. OPERATOR IS ALWAYS ON RIGHT SIDE.
2. CONTROLLER IS ALWAYS ON OPERATOR SIDE.

NIHVA TECHNOLOGIES PVT. LTD.
NIHVA TECHNOLOGIES PVT. LTD. PUNE
Email:- info@nihva.com
Website:- www.nihva.com

TITLE:
DOUBLE WALL ROLLING SHUTTER

CLIENT'S APPROVAL :

CLIENT - M A ENGINEERING
PROJECT - JOHN DEERE INDIA PVT LTD
SITE LOCATION - PUNE
DWG. NO. : NIHVA/20-21/0058 | REV- 00
SCALE: NTS | WT: | SHEET:1 OF 1
DRAWN BY: S.M.S. | DATE: 3.10.2020
CHECKED BY: P.V.A. | DATE: 3.10.2020
APPROVED BY : | DATE:
If any queries contact: projectsupport@nihva.com
NOTE: ALL DIMENSIONS ARE IN mm

THIS DRAWING & DESIGN IS THE PROPERTY OF NIHVA TECHNOLOGIES. NOT TO BE SOLD OR COPIED TO ANY OTHER CONCERN.