

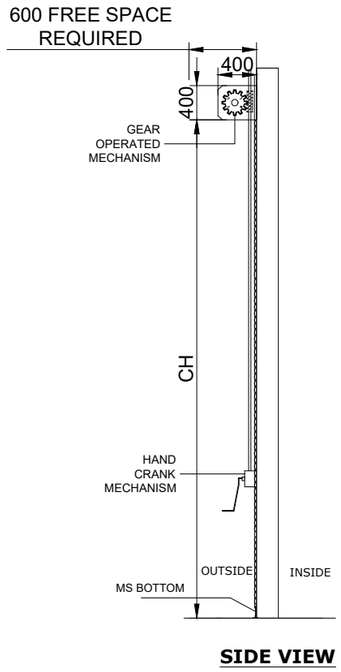


SIDE VIEW

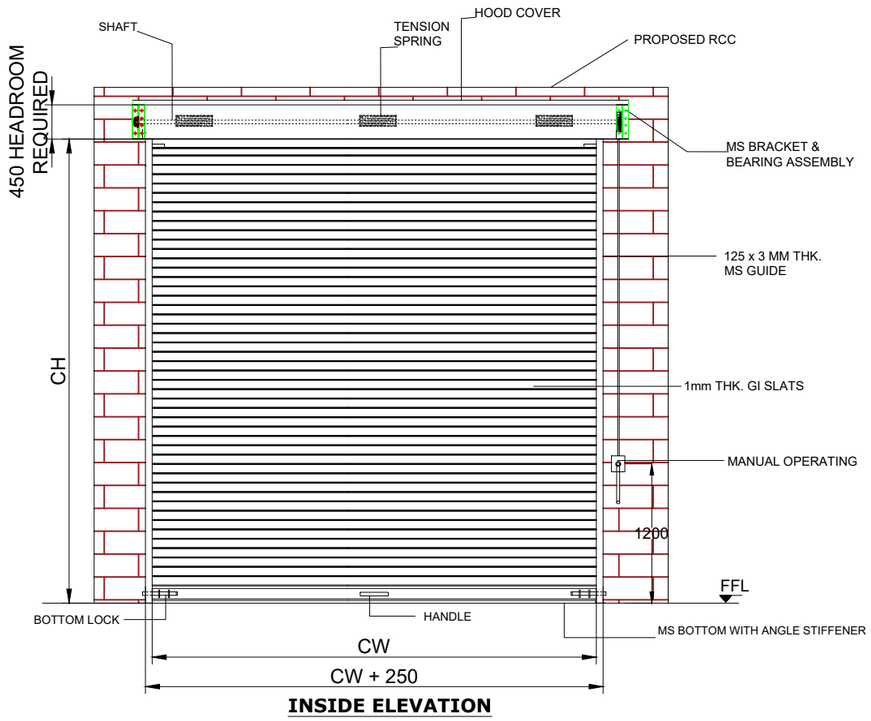


INSIDE ELEVATION

PLAN

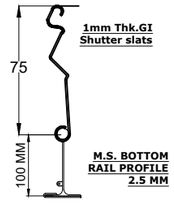

M.S. BOTTOM RAIL PROFILE 2.5MM

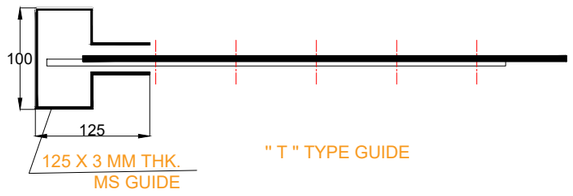

" T " TYPE GUIDE

NOTE-
1. ALL CIVIL WORK WILL BE CLIENT'S SCOPE.
2.IF STRUCTURE REQUIRED FOR SHUTTER IS IN CLIENT'S SCOPE.

TECHNICAL SPECIFICATION:-

SR.	SPECIFICATION	DETAILS
1.	DESCRIPTION & DRIVE	GEAR OPERATED SHUTTER
2.	LOCATION AREA	OUTSIDE AREA
3.	MOUNTING SURFACE	SIDE BRACKETS: ON CONCRETE
4.	SLAT	75 MM WIDE - 1 MM THICK GI
5.	BOTTOM PROFILE	M.S. PLATE 100X2.5 MM THICK WITH ANGLE STIFFNER
6.	GUIDE PROFILE	M.S."T" SHAPE -100X125X3 MM THK .
7.	HOOD COVER & MOTOR COVER	MADE OF GI SHEET THICKNESS 0.9 MM.
8.	MATERIAL FINISH	SYNTHETIC ENAMEL PAINT

SR NO	(CW) CLEAR WIDTH	(CH) CLEAR HEIGHT	QUANTITY
1	3000	4000	03 NOS

This drawing & design is the property of NIHVA TECHNOLOGIES. Not to be sold or copied to any other concern.

TITLE
GEAR OPERATED ROLLING SHUTTER

	NAME	SIGN	DATE
DRAWN	B.S.		06.10.2025
CHECK	V.T.		06.10.2025
APPRD.	V.T.		06.10.2025

NIHVA TECHNOLOGIES PVT. LTD.
NIHVA TECHNOLOGIES PVT. LTD. PUNE
Tel : 020 66304033
Website:- www.nihva.com
Email:- info@nihva.com

CLIENT - VTP
PROJECT -
SITE LOCATION -
If any queries contact : design@nihva.com
DWG. NO. : NIHVA/21-22/VDR/020
REV- R00
ALL DIMENSION ARE IN mm
SCALE: NTS
WT:
SHEET: 01 OF 01