


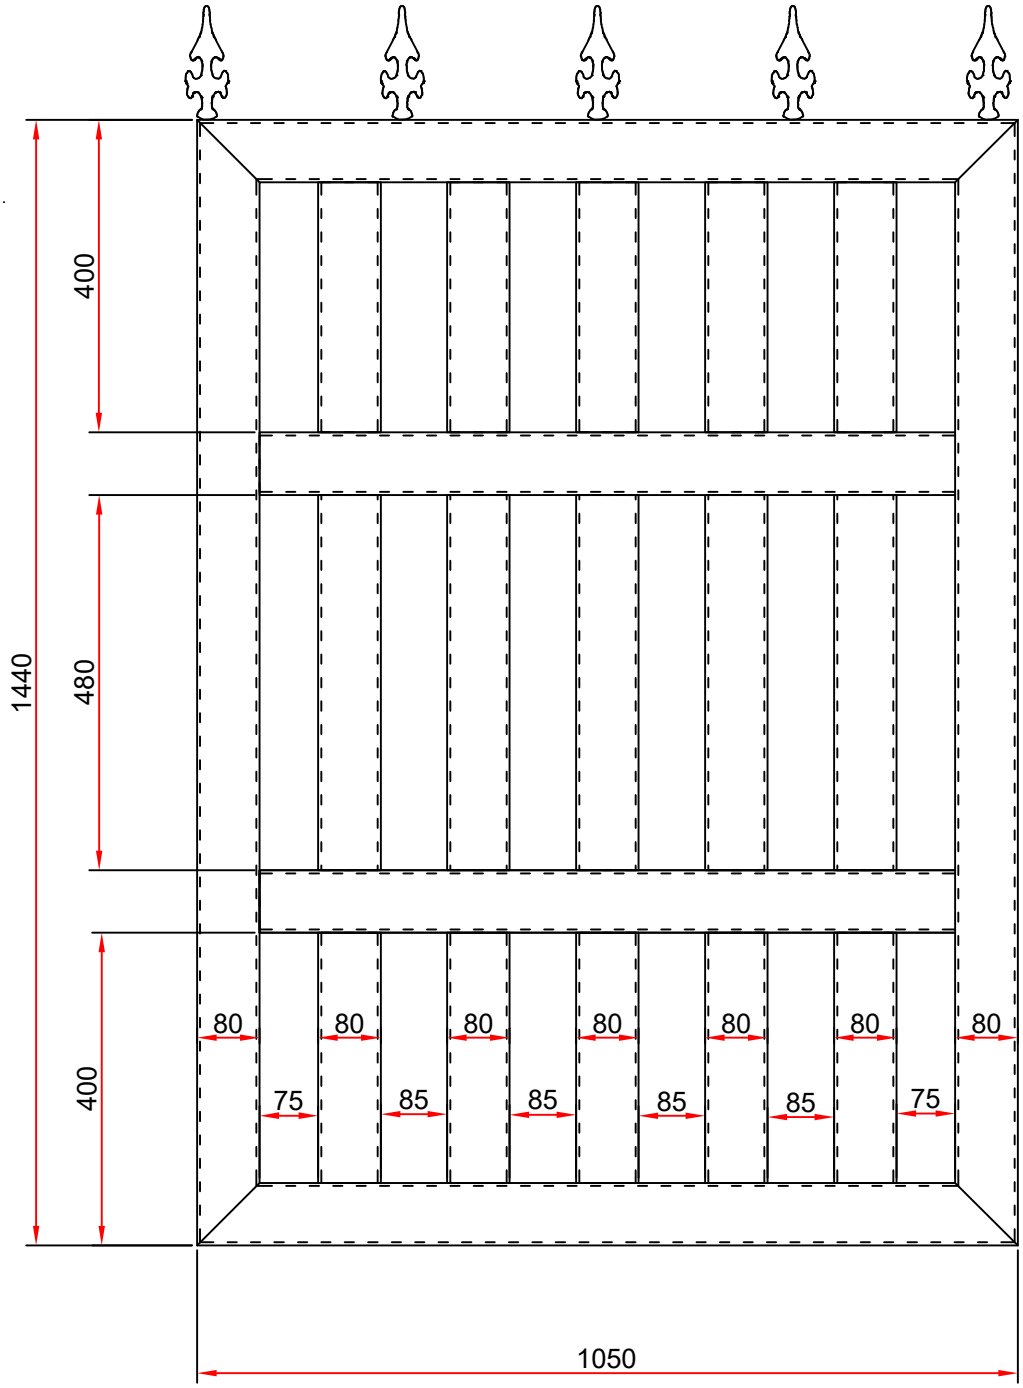

QTY:-03NOs

This drawing & design is the property of NIHVA TECHNOLOGIES. Not to be sold or copied to any other concern.

TITLE:- WICKET GATE				NIHVA TECHNOLOGIES PVT. LTD. PUNE Tel : 020 66304033 Email:- info@nihva.com Website:- www.nihva.com
	NAME	DATE	SIGN	
DRAWN	SUJATA	19/12/2022		CLIENT -Suraj Buildcon Pvt Ltd
CHECK	A.K	19/12/2022		LOCATION - Pune
APPRD.	V.T	19/12/2022		PRODUCT - Wicket Gate — QTY:-03NOs
If any queries contact : design@nihva.com				DWG NO:-NIHVA/22-23/CLT/0143_2 — REV- 00
ALL DIMENSION ARE IN mm				SCALE: NTS — SCALE:-- 1:1 — SHEET: 01 OF 01

Rev No.	Revision	Date	Revised By