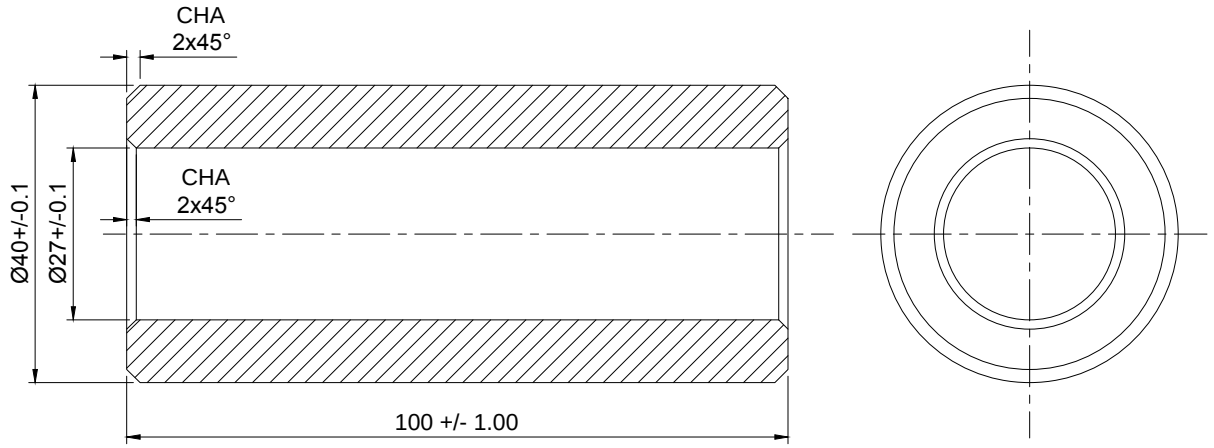


NOTE:~ MTL : MS

BUSH Ø40 X 103L = 19 NOS

NOTE : ~ PLEASE MAINTAIN 8 MM GAP BETWEEN TWO LIP BUSHES.

This drawing & design is the property of NIHVA TECHNOLOGIES. Not to be sold or copied to any other concern.

TITLE

LIP MOUNTING BUSH

NIHVA TECHNOLOGIES PVT. LTD.
NIHVA TECHNOLOGIES PVT. LTD. PUNE
Tel : 020 66304033
Email:- info@nihva.com
Website:- www.nihva.com

	NAME	SIGN	DATE
DRAWN	PRADEEP		14.04.2018
CHECK	PRADEEP		14.04.2018
APPRD.	PRADEEP		14.04.2018

If any queries contact : design@nihva.com	DWG. NO. :NIHVA/18-19/VDR/353		
ALL DIMENSION ARE IN mm	SCALE: NTS	WT:	REV- 0

CLIENT -

PROJECT - NSDL2025

SITE LOCATION -