CAPACITY	20 TON
BAILING CHAMBER	1000L X 500W X 1000H
BAIL SIZE	1000L X 500W X 300H

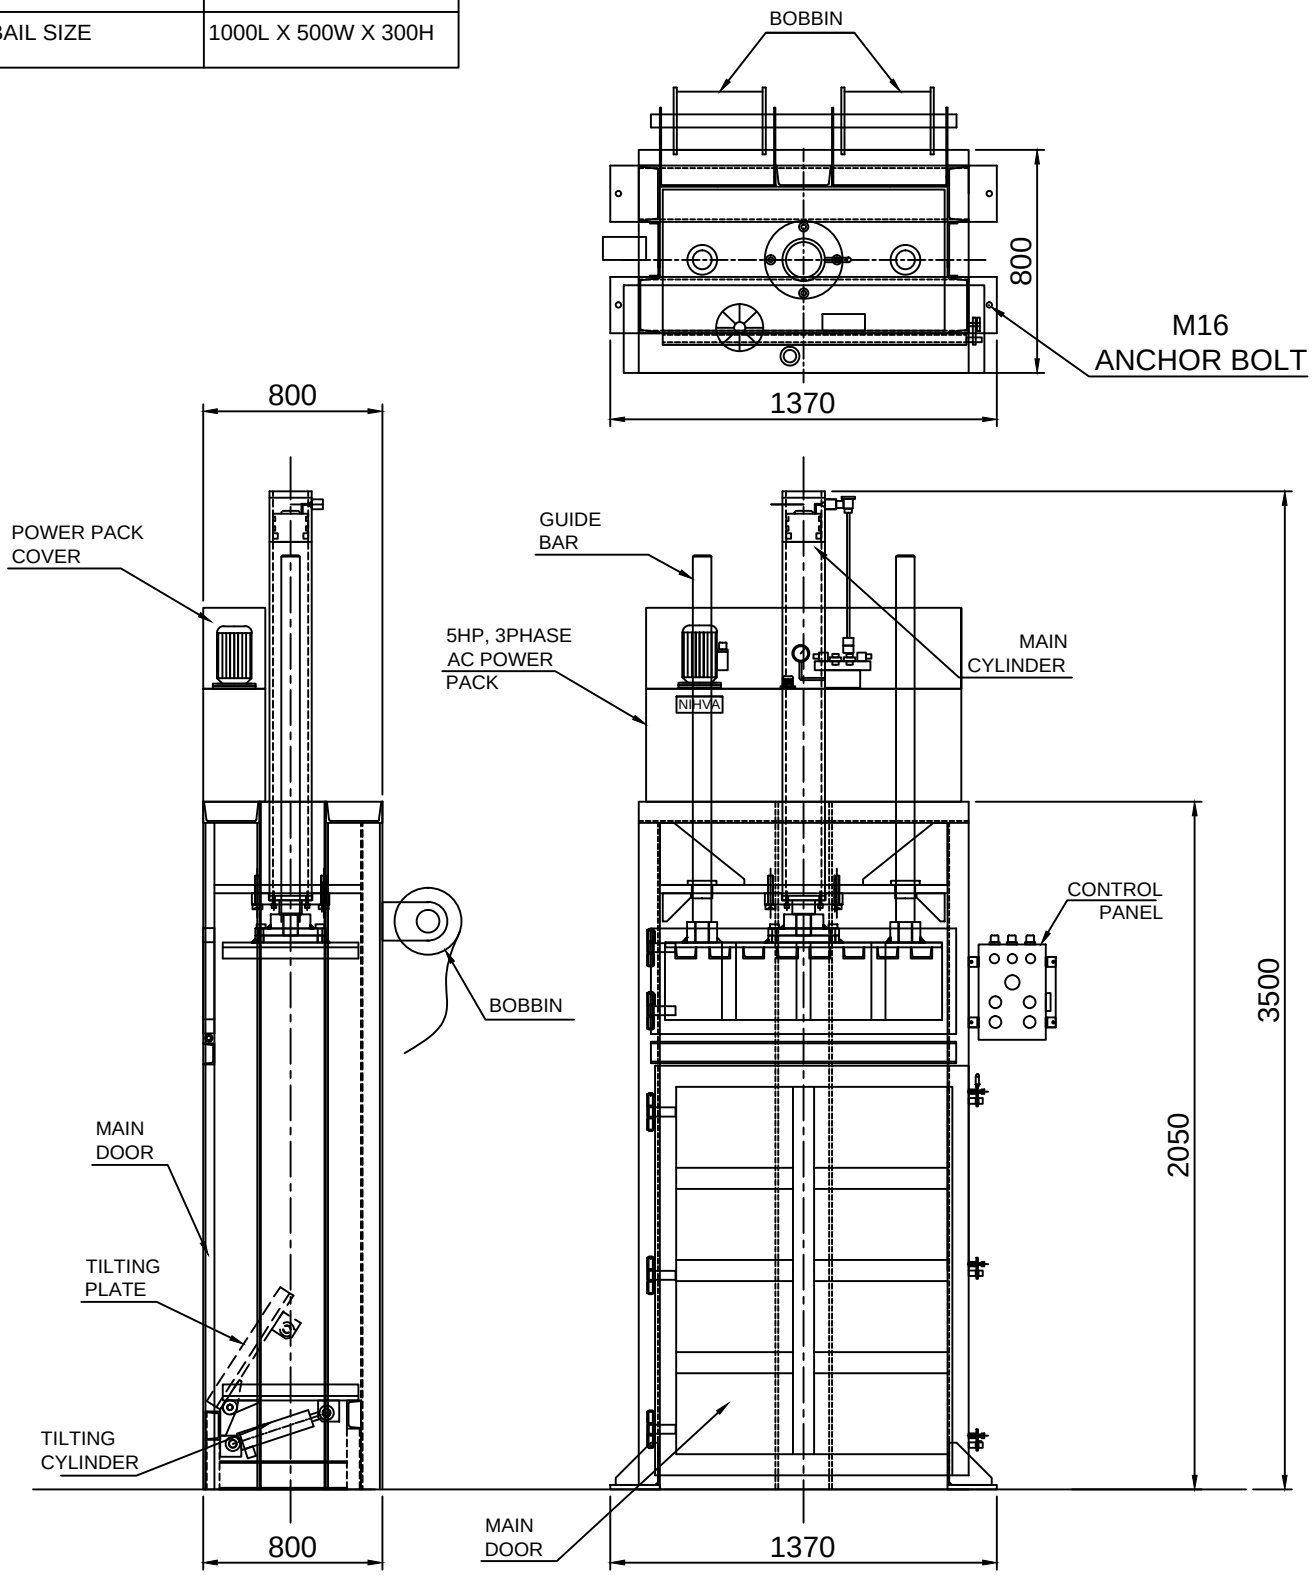

REV NO	REV DATE	DRAWN	REMARK
R03	19.10.2019	P.V.A	1. POWER PACK COVER ADDED. 2. OVER ALL WIDTH INCREASE.
R02	05.10.2019	P.V.A	1. POWER PACK LOCATION CHANGE
R01	01.10.2019	P.V.A	1. POWER PACK LOCATION CHANGE 2. CHAMBER SIZE CHANGE

This drawing & design is the property of NIHVA TECHNOLOGIES. Not to be sold or copied to any other concern.

TITLE

BAILING PRESS

	NAME	SIGN	DATE
DRAWN	P.A		18.09.2019
CHECK	G.J		18.09.2019
APPRD.			

If any queries contact : design@nihva.com

ALL DIMENSION ARE IN mm

NIHVA TECHNOLOGIES PVT. LTD.
NIHVA TECHNOLOGIES PVT. LTD. PUNE
Tel : 020 66304033
Email:- info@nihva.com
Website:- www.nihva.com

CLIENT - IKEA

PROJECT -

SITE LOCATION -

DWG. NO. :NIHVA/1 9-20/0096/R03 | REV- R03

SCALE: NTS | WT: | SHEET: 01 OF 01