

Revision		Date	By
A	Corrected mullion hoist positions, floor pits altered	2022-09-02	EB
B	New measurements, doors redrawn	2022-10-11	EB

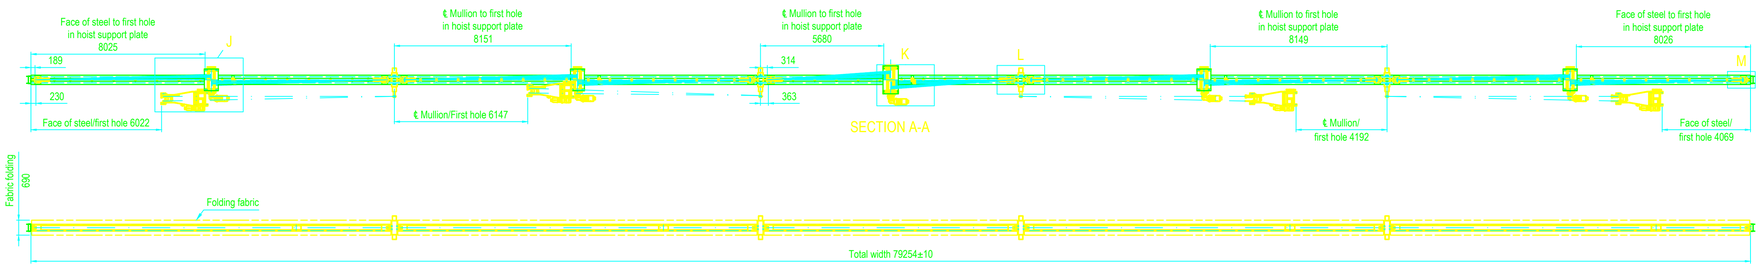


SECTION A-A


SECTION B-B

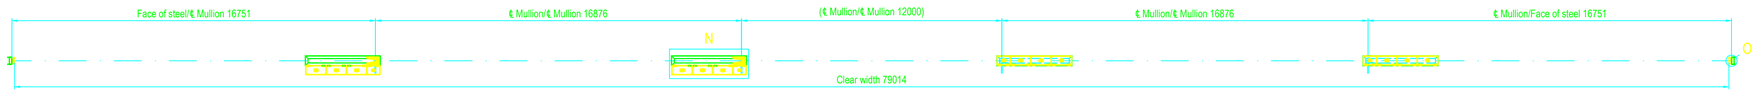


SECTION C-C

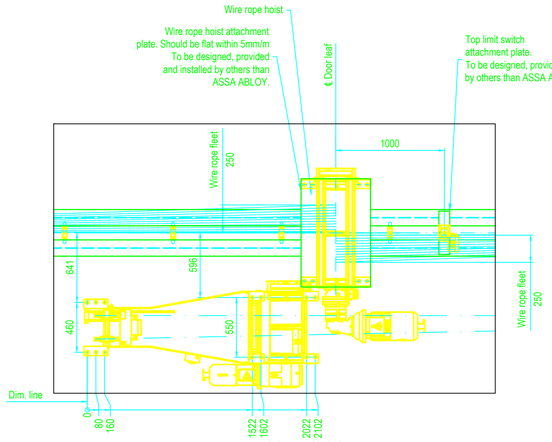


DETAIL J, SCALE (1:20)

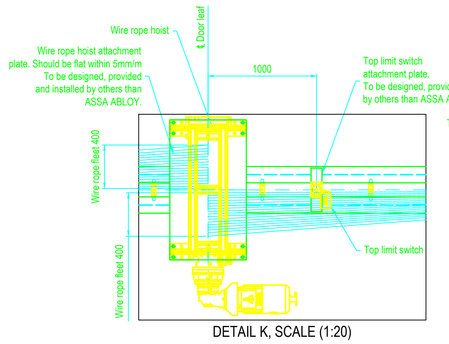


DETAIL K, SCALE (1:20)

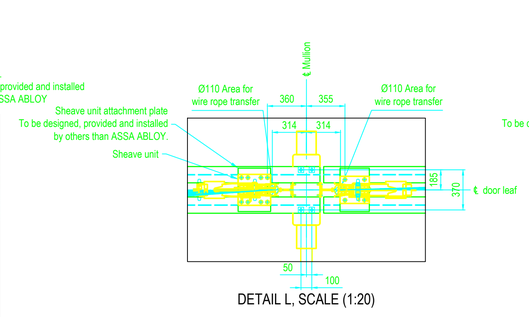


DETAIL L, SCALE (1:20)

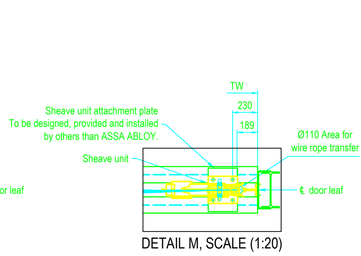

DETAIL M, SCALE (1:20)

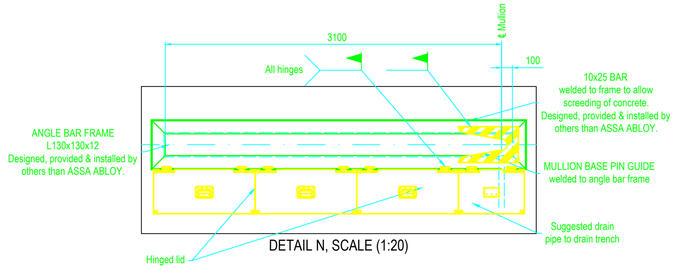

DETAIL N, SCALE (1:20)

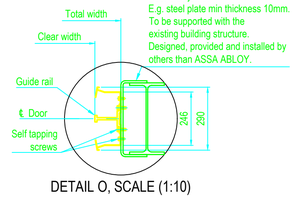

DETAIL O, SCALE (1:10)

DOOR IDENTITY NUMBER: 84800001

LOAD DIAGRAM & NOTES, ref. to drwng. no. 77446

INTERFACE, SECTIONS ref. to drwng. no. 77445

INTERFACE, ELEVATION ref. to drwng. no. 77443

DESIGNED: EB	SIZE: A1P	SCALE: 1:100	
CODE: 84800	If not otherwise stated: Tolerances ISO 2768-mK EN ISO 13920-B		
ITEM NO	Cutting class ISO 9013:442		
DATE: 2022-08-23	Weld class ISO 5817:C		
ASSA ABLOY	Surface finish Smooth raw surface	DRAWING NO: 77444	REVISION: B

GMR Aero Technic Hangar1
India
Megadoor 79014x23000/14000
Interface, Plan views

PLOT DATE