


PIT DRAWING FOR DOCK LEVELER - 2000(W) X 3000(L)X480(H)

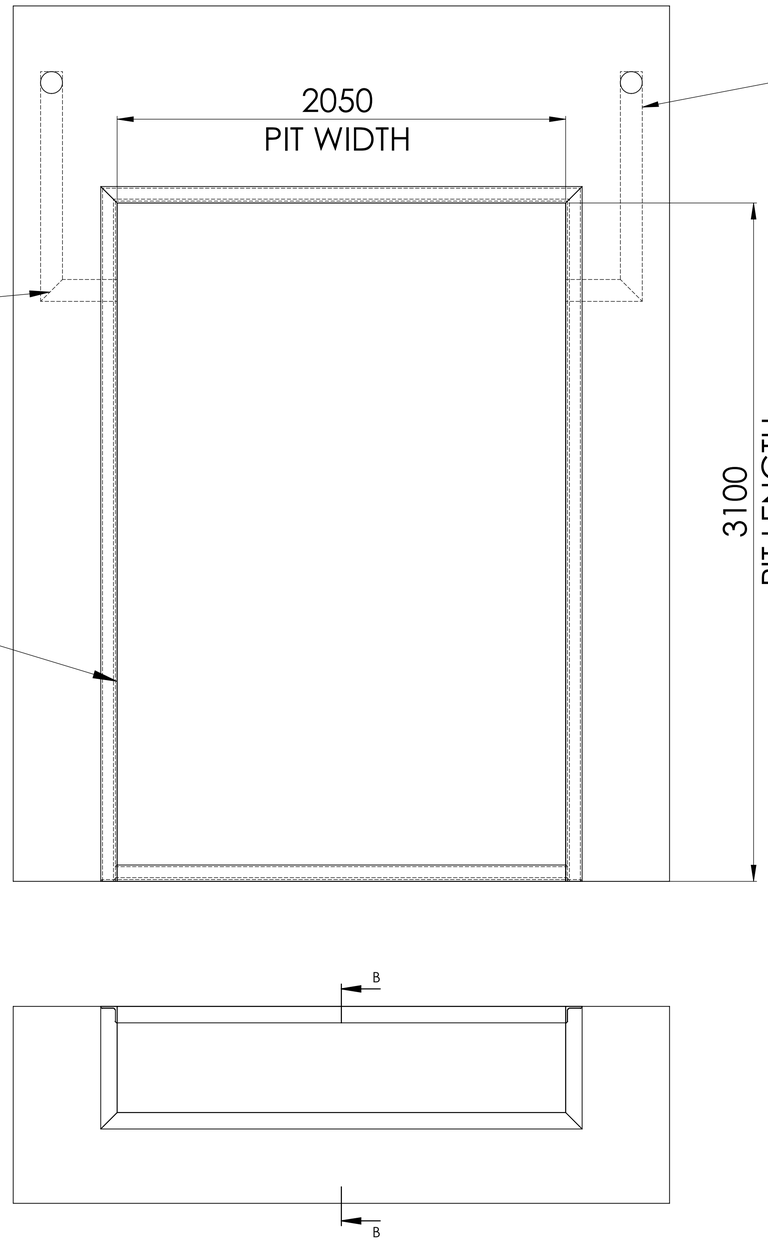

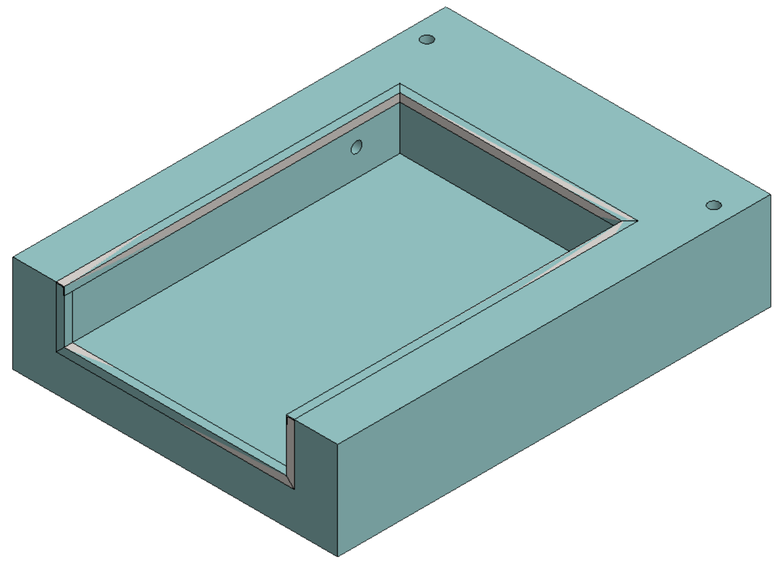

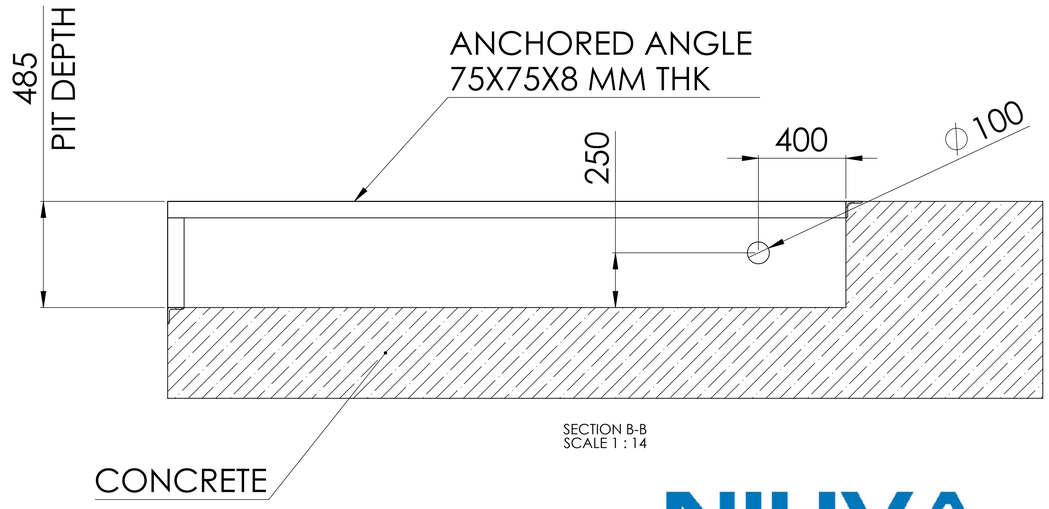

SECTION B-B
SCALE 1 : 14

NOTES-

1. REQUIRED ANGLE , DUCT , PIT & ALL CIVIL WORK IS IN CLIENT SCOPE .
2. PIT SURFCACE SHOULD BE PARALLEL .
3. ARRANGEMENT FOR PROPER DRAINAGE SHOULD BE DONE .
4. PIT SHOULD BE CAPABLE TO TAKE LOAD OF 18000KG .

NIHVA
We Make Possible

UNLESS OTHERWISE SPECIFIED: DIMENSIONS ARE IN MILLIMETERS SURFACE FINISH: TOLERANCES: LINEAR: ANGULAR:	FINISH:		DEBURR AND BREAK SHARP EDGES	DO NOT SCALE DRAWING	REVISION
	NAME	SIGNATURE	DATE	TITLE: NIHVA/20-21/0161	
DRAWN	SIDDHESHWAR		15.2.2021		
CHK'D					
APP'V'D					
MFG					
Q.A					
MATERIAL:				DWG NO. PIT FOR DL	A1
WEIGHT:				SCALE:1:20	SHEET 1 OF 1