


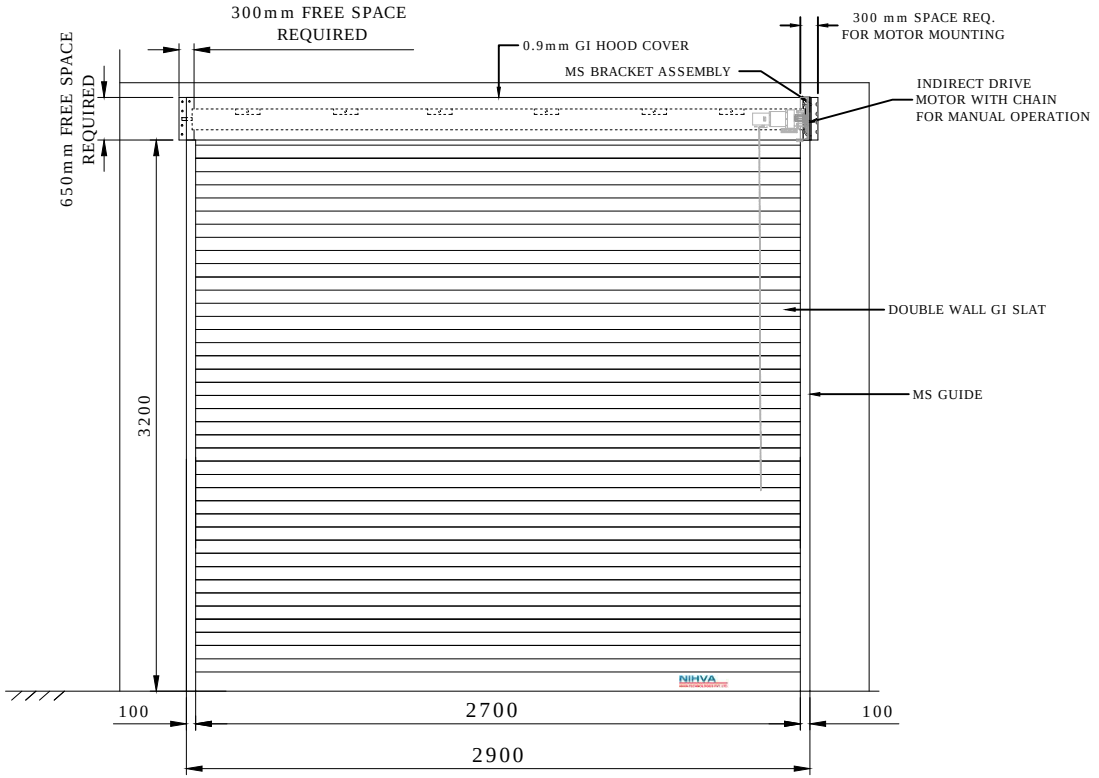


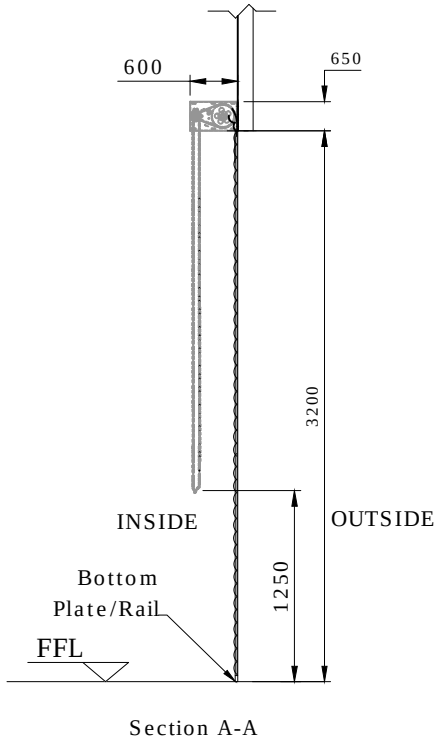


Section A-A

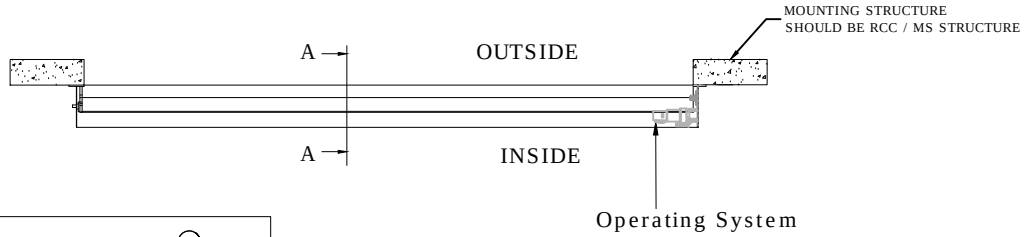

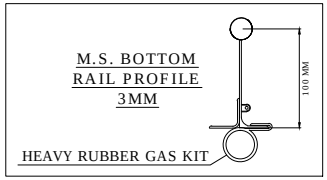

Main Slats
Double Wall Rolling Shutter

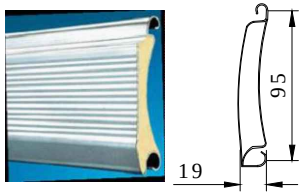

COLOR:-
1.TRAFFIC WHITE:-RAL9016
2.GREY:-RAL 7035
3.Gentian Blue:-RAL5010
4.Signal Red:-RAL3001

COLOR - PU PAINT AS PER APPROVED RAL SHADE.

CLEAR WIDTH (CW)	CLEAR HEIGHT (CH)	QUANTITY
2700 mm	3200 mm	2 NOS

DIMENSION :

CLEAR WIDTH	CLEAR HEIGHT	QUANTITY
2700 mm	3200 mm	2 NOS

MATERIAL :

THICKNESS :

NOTE:-
1. STRUCTURE FOR SHUTTER FOR SHUTTER WILL BE IN CLIENT'S SCOPE.
2. 3 PHASE SUPPLY SHOULD BE PROVIDED.

NIHVA TECHNOLOGIES PVT. LTD.
NIHVA TECHNOLOGIES PVT. LTD. PUNE
Email:- info@nihva.com
Website:- www.nihva.com

TITLE:

DOUBLE WALL ROLLING SHUTTER

CLIENT'S APPROVAL :

CLIENT - FERRERO INDIA PVT. LTD.

PROJECT -

SITE LOCATION - BARAMATI.

DWG. NO. : NIHVA/17-18/0243

SCALE: NTS	WT:	SHEET:1 OF 1

DRAWN BY: SURAJ	DATE: 15-10-2017
CHECKED BY: SHEKHAR	DATE: 15-10-2017
APPROVED BY : SHEKHAR	DATE: 15-10-2017

If any queries contact : projects@nihva.com

NOTE: ALL DIMENSIONS ARE IN mm

THIS DRAWING & DESIGN IS THE PROPERTY OF NIHVA TECHNOLOGIES. NOT TO BE SOLD OR COPIED TO ANY OTHER CONCERN.