Weitergabe sowie Vervielfältigung dieses Dokuments, Verwertung und Mitteilung seines Inhalts sind nur nach vorheriger ausdrücklicher schriftlicher Zustimmung von SMS Meer GmbH gestattet. Das Dokument ist vor unberechtigtem Zugriff Dritter zu schützen. Zuwiderhandlungen verpflichten zu Schadensersatz. Alle Rechte aus Patent-/Gebrauchsmuster-/Markenschutz vorbehalten.

The reproduction, distribution and utilization of this document as well as the disclosure of its content to others without prior explicit written consent of SMS Meer GmbH is prohibited. Holder has to protect this document against unauthorized withdrawal of third parties. Offenders will be held liable for the payment of damages. All rights reserved in case of patent/utility model/trademark protection.

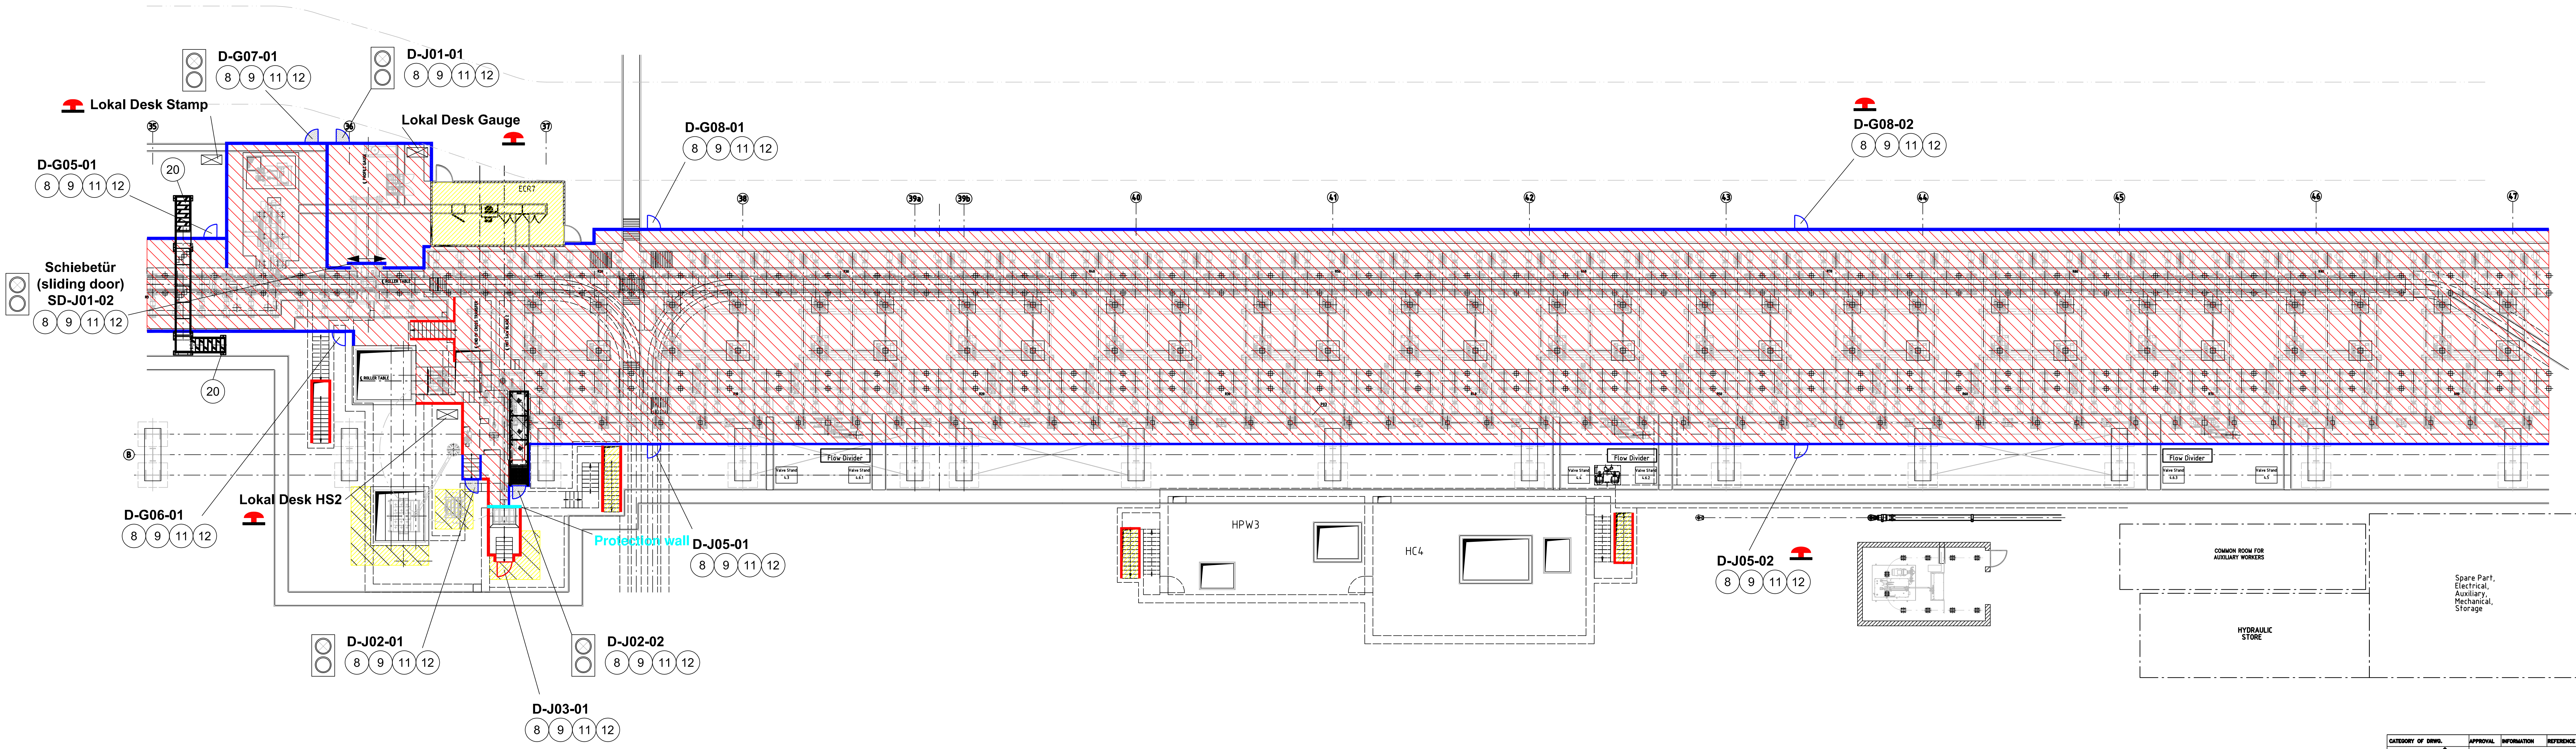
D-G07-01
8 9 11 12
D-J01-01
8 9 11 12
Lokal Desk Stamp
Lokal Desk Gauge
D-G05-01
8 9 11 12
20
Schiebetür
(sliding door)
SD-J01-02
8 9 11 12
ECR7
D-G08-01
8 9 11 12
D-G08-02
8 9 11 12
35
36
37
38
39a
39b
40
41
42
43
44
45
46
47
20
Flow Divider
Flow Divider
Flow Divider
D-G06-01
8 9 11 12
Lokal Desk HS2
Protection wall
D-J05-01
8 9 11 12
HPW3
HC4
D-J05-02
8 9 11 12
COMMON ROOM FOR AUXILIARY WORKERS
HYDRAULIC STORE
Spare Part,
Electrical,
Auxiliary,
Mechanical,
Storage
D-J02-01
8 9 11 12
D-J02-02
8 9 11 12
D-J03-01
8 9 11 12

GATE	DANGER ZONE 1 No access while unit is in operation.
GATE WITH MECH. LOCKING DEVICE	DANGER ZONE 2 Access only to qualified and authorized persons possible in defined operating states. High Residual Risks Note safety instructions in operating and maintenance manual.
GATE WITH ELECT. LOCKING DEVICE	DANGER ZONE 3 Access only to qualified and authorized persons possible in defined operating states. Low Residual Risks Note safety instructions in operating and maintenance manual.
DOOR WITH MECH. LOCKING DEVICE	DANGER ZONE 4 Permanente working place: Unrestricted access possible while unit is in operation. Note general safety instructions.
DOOR WITH ELECT. LOCKING DEVICE	WORKING PLACE Part of no access zone, that can be entered by trained operators under particular conditions only Note safety instructions in operating and maintenance manual.
DOOR	REQUEST-/ ACKNOWLEDGEMENT BUTTON
DOOR WITH MECH. LOCKING DEVICE	EMERGENCY STOP
DOOR WITH ELECT. LOCKING DEVICE	ACKNOWLEDGEMENT BUTTON

ESCAPE ROUTES
RAILING
REMOVABLE RAILING
FENCE
REMOVABLE FENCE
REMOVABLE CHAIN
LIGHT CURTAIN

9463 0000 / RAILBHIL

CATEGORY OF DRWG.	APPROVAL	INFORMATION	REFERENCE	RECORD	CONSTRUCTION

SAIL

BHILAI STEEL PLANT, BHILAI, CHATTISGARH
7,0 MTPA EXPANSION

मेकॉन लिमिटेड
MECON LIMITED

VENSDOR'S NAME: SMS Meer/SMS Meer India/ABB
PACKAGE DESCRIPTION: UNIVERSAL RAIL MILL (Pkg No-047)
TITLE OF DRAWING. PARTITION 6, SAFETY LAYOUT
SCALE-
VENDOR'S DRG NO.-
PROJECT DRG. NO. BSP-SMS Meer-08-047-21-130-35-BE-06654 REV. -

Fertigungsvorschriften
Manufacturing Instructions
SN 200

Ursprung / Origin
Fertiggewicht
Finished weight
kg
Modell-Nr.
Pattern-No.
Werkstoff / Material
Projektionsmethode 1
First angle projection method
ISO 128

	Datum Date	Name
Bearb. Drawn	27.09.11	Fryen
Geprüft Checked	27.09.11	Prätzel
Norm Stand		

Typ
Type Safety Layout
Benennung
Teilbereich, 6
Title
PARTITION 6
Maßstab
Scale
1:100

Sach-Nr. Drawing-No.
0100133-00.654
Blatt
Sheet 1
6 Blätter
Sheets

Aus-gabe Issue	Änderung Revision	Datum Date	Name

SMS MEER
SMS group

Ersatz für:/Supersedes:
Ersetzt durch:/Superseded by:

Diese Zeichnung und alle darauf enthaltenen Informationen sind vertraulich. This drawing and all information on it is confidential.
A0