




6

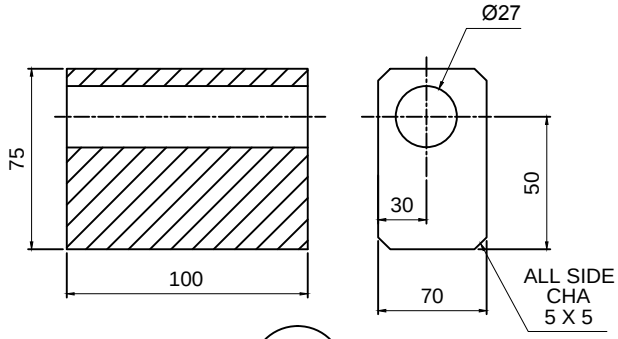

14

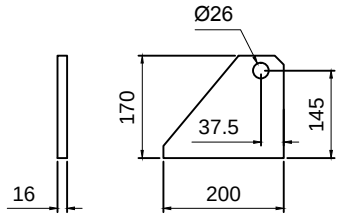

8

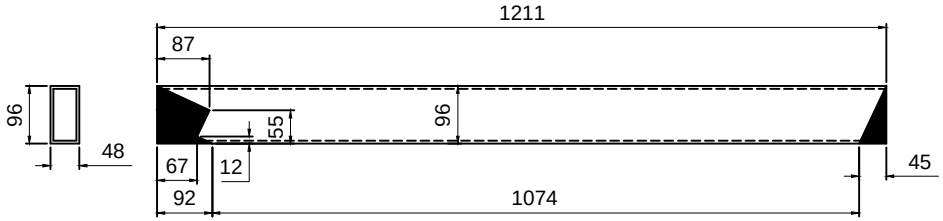

11

This drawing & design is the property of NIHVA TECHNOLOGIES. Not to be sold or copied to any other concern.

TITLE			
BASE FRAME DETILS			
	NAME	SIGN	DATE
DRAWN	P.A		08.08.2020
CHECK	G.J		08.08.2020
APPRD.			
If any queries contact : design@nihva.com			
ALL DIMENSION ARE IN mm			

NIHVA
NIHVA TECHNOLOGIES PVT. LTD.
Website:- www.nihva.com
NIHVA TECHNOLOGIES PVT. LTD. PUNE
Tel : 020 66304033
Email:- info@nihva.com

CLIENT -			
PROJECT -			
SITE LOCATION -			
DWG. NO. : NIHVA/20-21/VDR/0030			REV- R00
SCALE: NTS	WT:		SHEET: 01 OF 01