
ITEM NO.	PART NUMBER	DESCRIPTION	QTY.
1	GUIDE RAILS-T75-1B	STD (10060 mm)	6
2	panel 1		1
3	2D DRAWING BUSBAR FLASHER	STD (LOOSE PART)	5
4	2D DRAWING Anchor Bolt M10x75	STD	70
5	moter with stand		1
6	2D DRAWING RACK	STD (M4 RACK, 30x8x1000 mm, ZINC COATED WITH SPACERS AND SCREWS.)	10
7	C - CHANEL	70X30X575	22
8	panel 2		1
9	panel 3		1

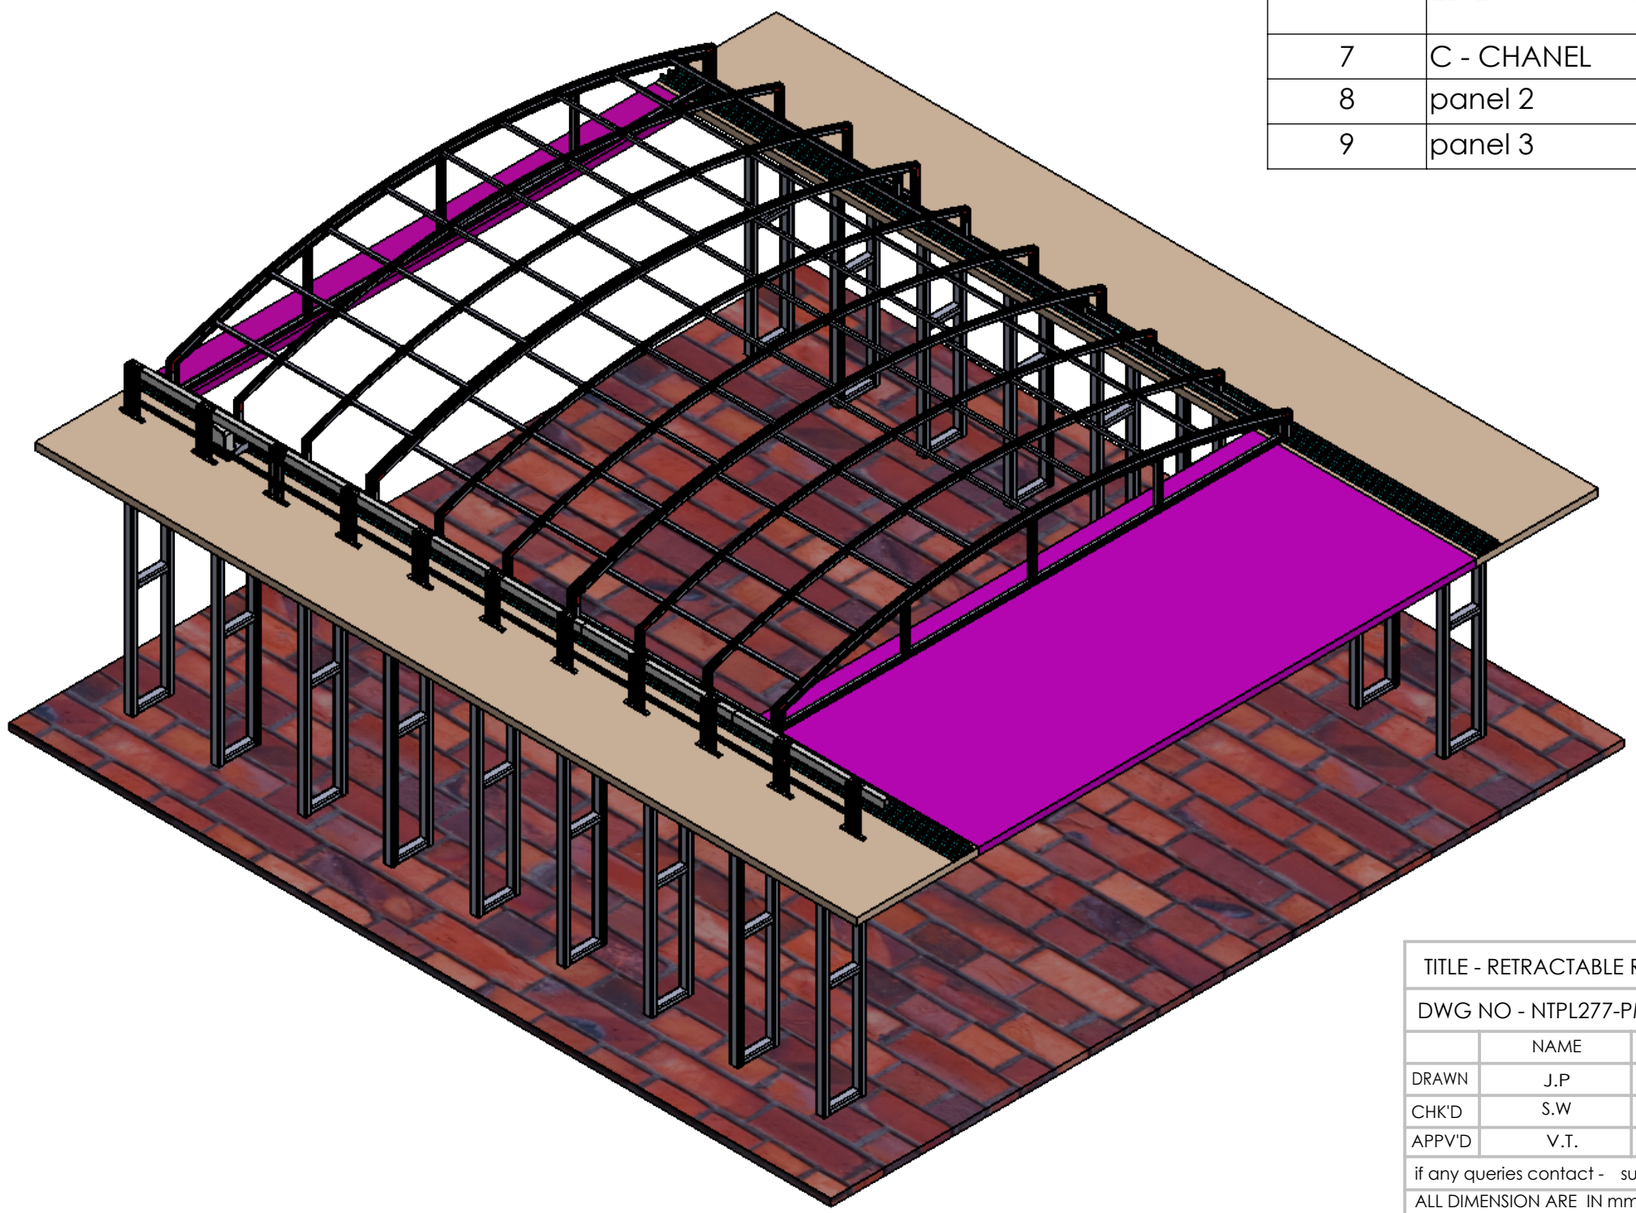

TITLE - RETRACTABLE ROOF

DWG NO - NTPL277-PM-001-00-000-00

NIHVA Technologies Pvt. Ltd.

NIHVA TECHNOLOGIES PVT.LTD.PUNE

Website - www.nihva.com

	NAME	SIGNATURE	DATE
DRAWN	J.P		10-04-2025
CHK'D	S.W		10-04-2025
APPV'D	V.T.		10-04-2025

PROJECT NO - NTPL277-PM

PRODUCT - RETRACTABLE ROOF

SITE LOCATION - AYODHYA

if any queries contact - supportautomation@nihva.com

REVISION -


QTY - 1

ALL DIMENSION ARE IN mm


A3


SCALE -

SHEET 1 OF 24

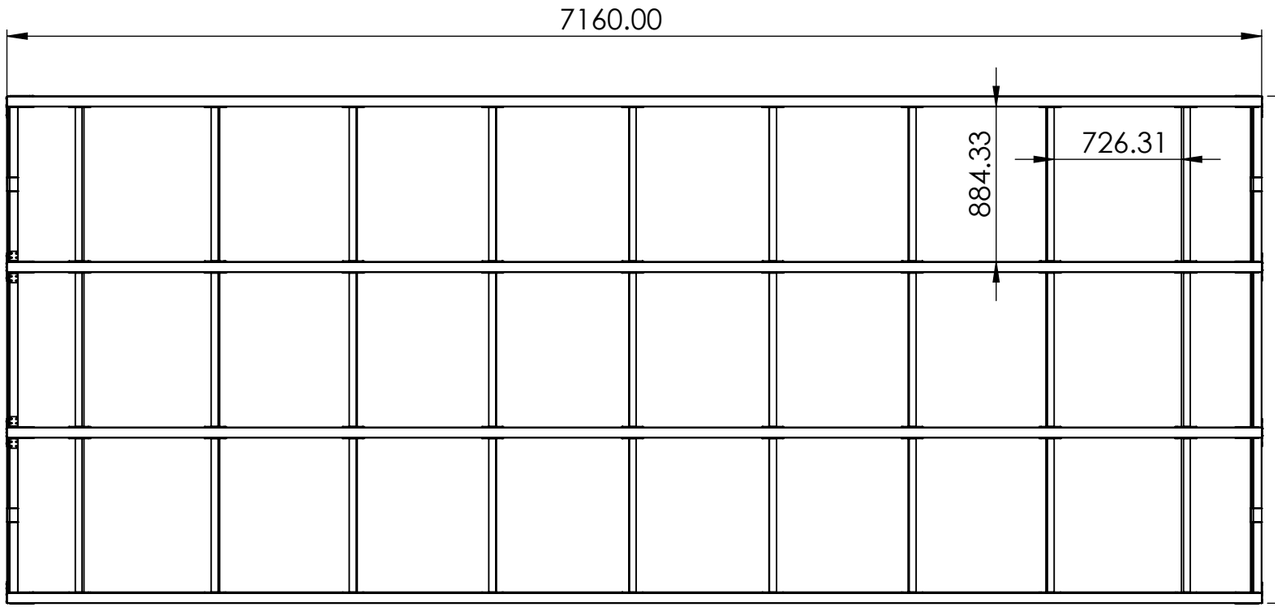


ITEM NO.	PART NUMBER	DESCRIPTION	QTY.
1	panel 1 ass.		1
2	panel 1 closer		1
3	L PALTE	JOINING PLATE	12
4	2D DRAWING PROFILE L ANGLE WELDING PLATE	JOINING PLATE Al metal	8
5	T PLATE	JOINING PLATE	8
6	L ANGLE PLATE	JOINING PLATE	4

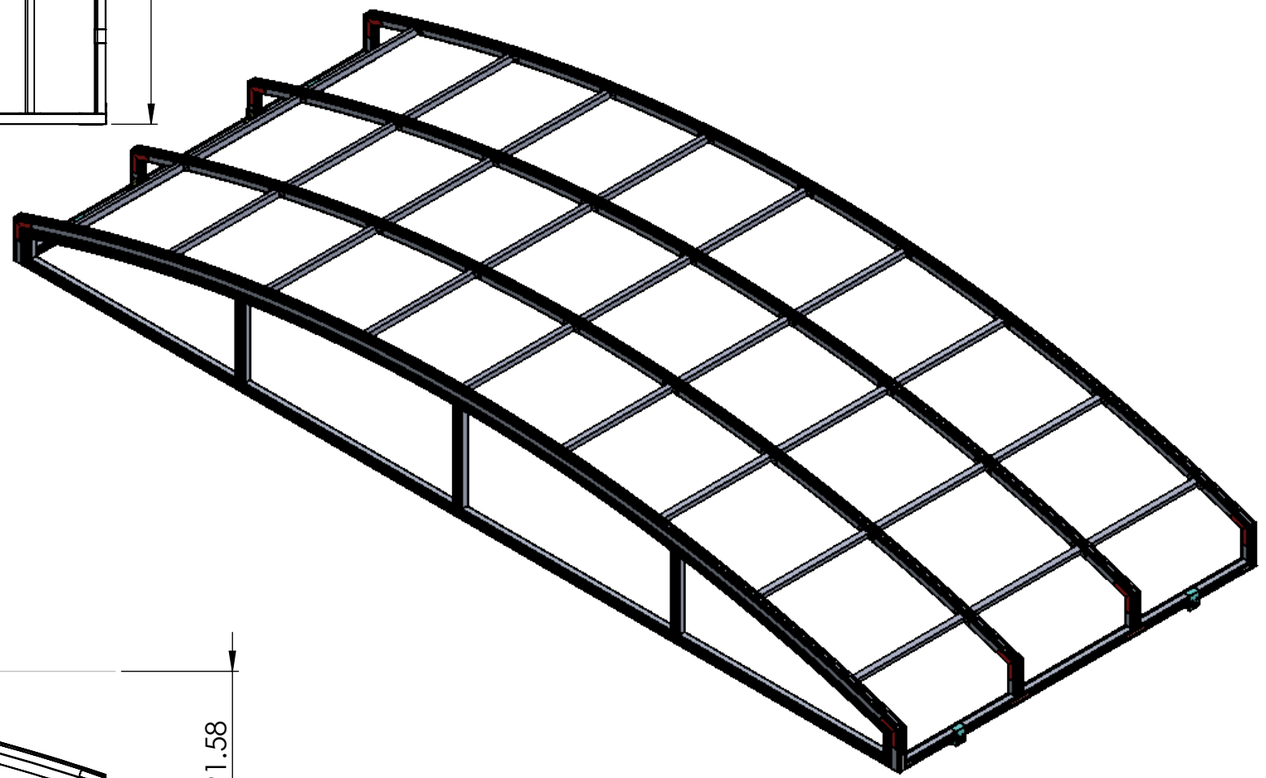


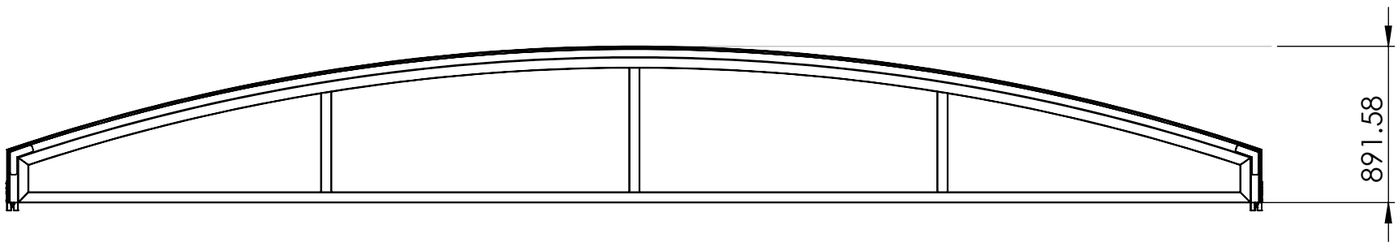


TITLE - RETRACTABLE ROOF				NIHVA TECHNOLOGIES PVT.LTD.PUNE
DWG NO - NTPL277-PM-001-01-000-00				Website - www.nihva.com
	NAME	SIGNATURE	DATE	PROJECT NO - NTPL277-PM
DRAWN	J.P		10-04-2025	PRODUCT - RETRACTABLE ROOF
CHK'D	S.W		10-04-2025	SITE LOCATION - AYODHYA
APPV'D	V.T.		10-04-2025	
if any queries contact - supportautomation@nihva.com				REVISION - QTY - 1
ALL DIMENSION ARE IN mm			A3	SCALE - SHEET 2 OF 24

ITEM NO.	PART NUMBER	DESCRIPTION	QTY.
1	panel 1		1

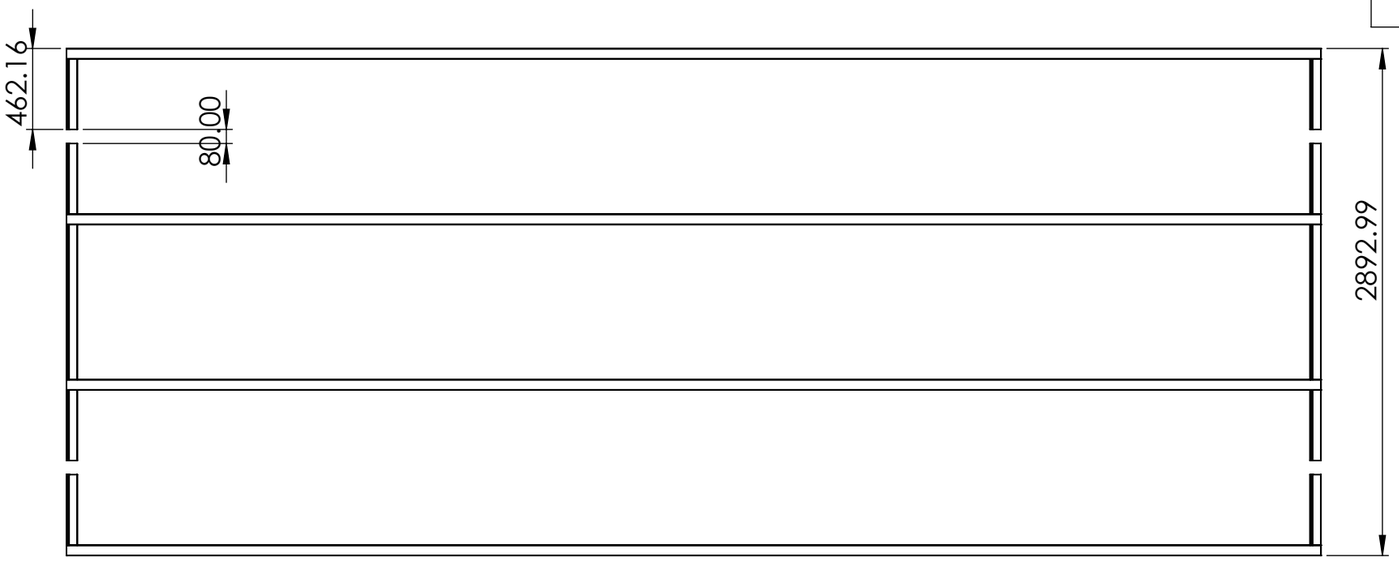


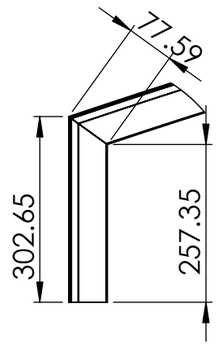

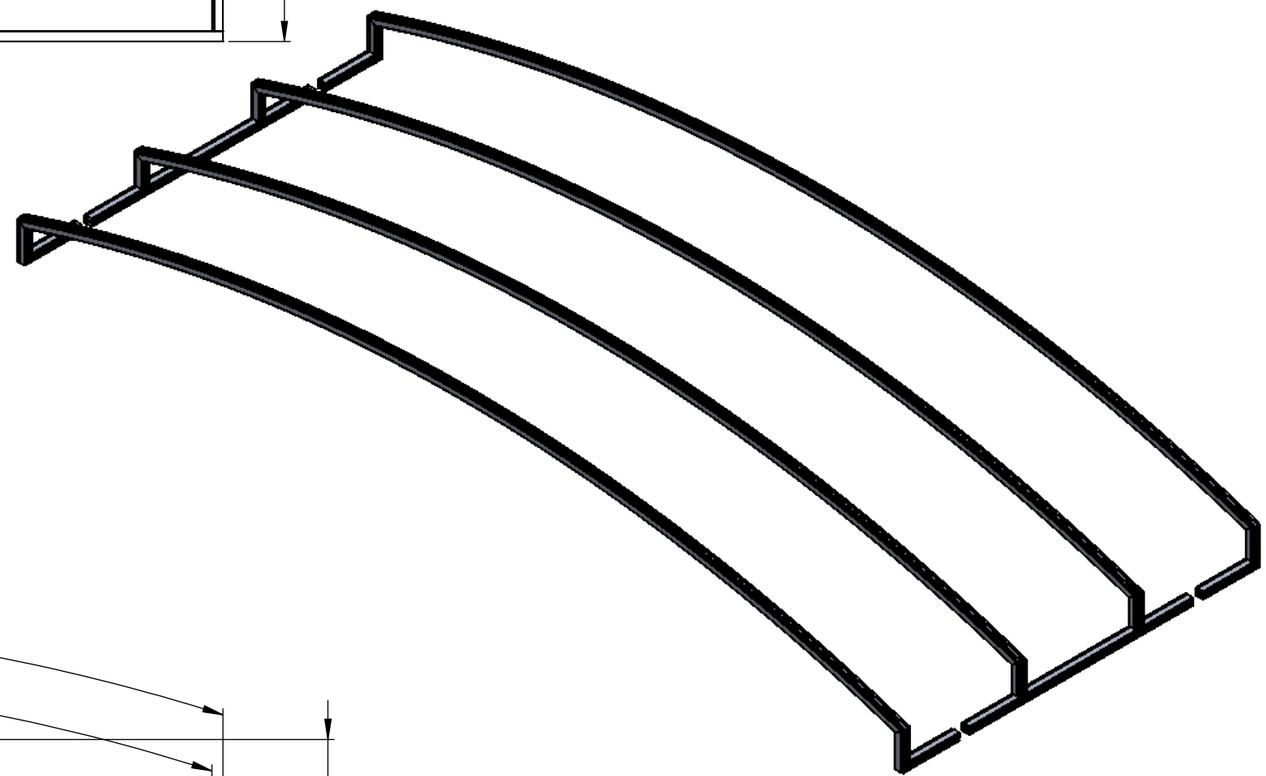


DETAIL A

SCALE 1 : 10

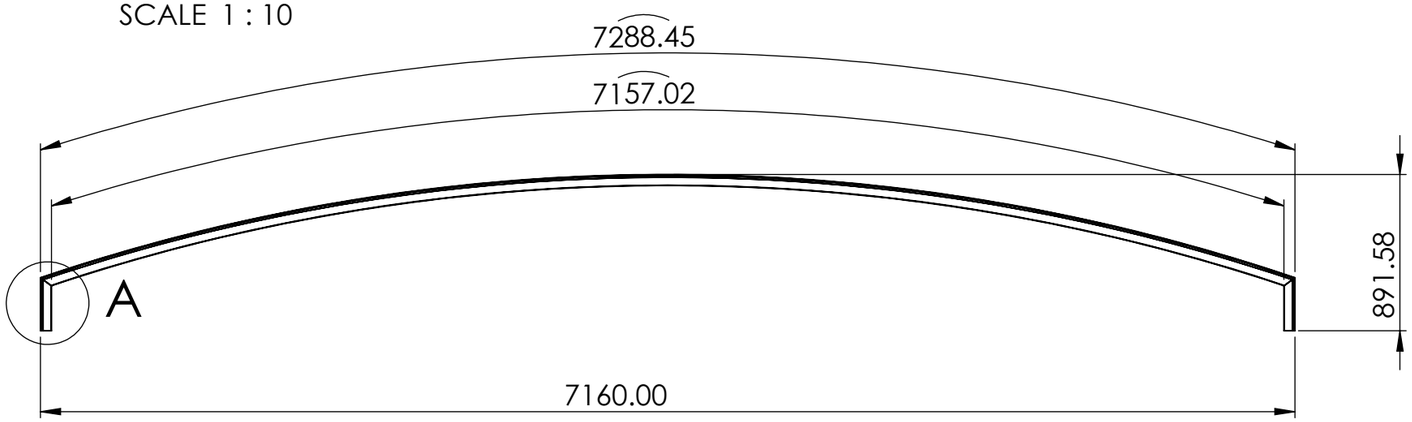


TITLE - RETRACTABLE ROOF				NIHVA TECHNOLOGIES PVT.LTD.PUNE
DWG NO - NTPL277-PM-001-01-000-01				Website - www.nihva.com
	NAME	SIGNATURE	DATE	PROJECT NO - NTPL277-PM
DRAWN	J.P		10-04-2025	PRODUCT - RETRACTABLE ROOF
CHK'D	S.W		10-04-2025	SITE LOCATION - AYODHYA
APPV'D	V.T.		10-04-2025	
if any queries contact - supportautomation@nihva.com				REVISION - QTY - 1
ALL DIMENSION ARE IN mm			A3	SCALE - SHEET 3 OF 24


ITEM NO.	PART NUMBER	DESCRIPTION	QTY.
1	panel 1 closer		1

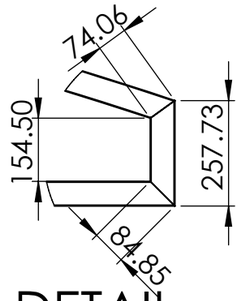


DETAIL B

SCALE 1 : 15

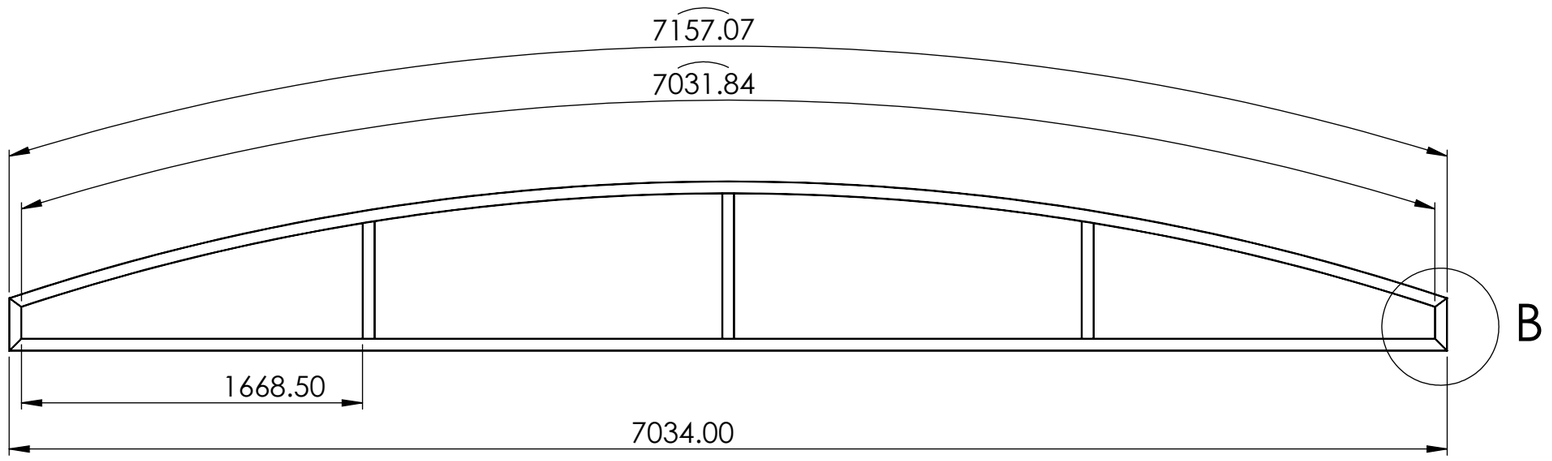


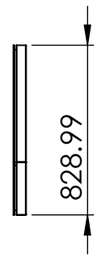


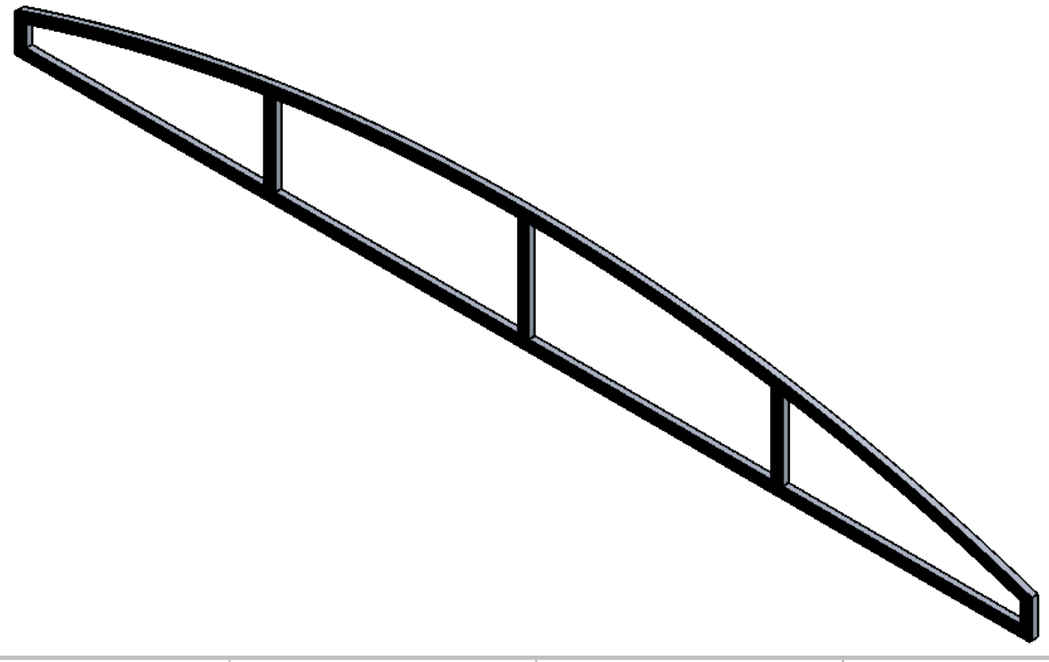


TITLE - RETRACTABLE ROOF				NIHVA TECHNOLOGIES PVT.LTD.PUNE Website - www.nihva.com
DWG NO - NTPL277-001-01-000-02				
	NAME	SIGNATURE	DATE	PROJECT NO - NTPL277-PM
DRAWN	J.P		10-04-2025	PRODUCT - RETRACTABLE ROOF
CHK'D	S.W		10-04-2025	SITE LOCATION - AYODHYA
APPV'D	V.T.		10-04-2025	
if any queries contact - supportautomation@nihva.com				REVISION - QTY - 1
ALL DIMENSION ARE IN mm			A3	SCALE - SHEET 4 OF 24

ITEM NO.	PART NUMBER	DESCRIPTION	QTY.
1	roof support	40x40x2 square tube	72

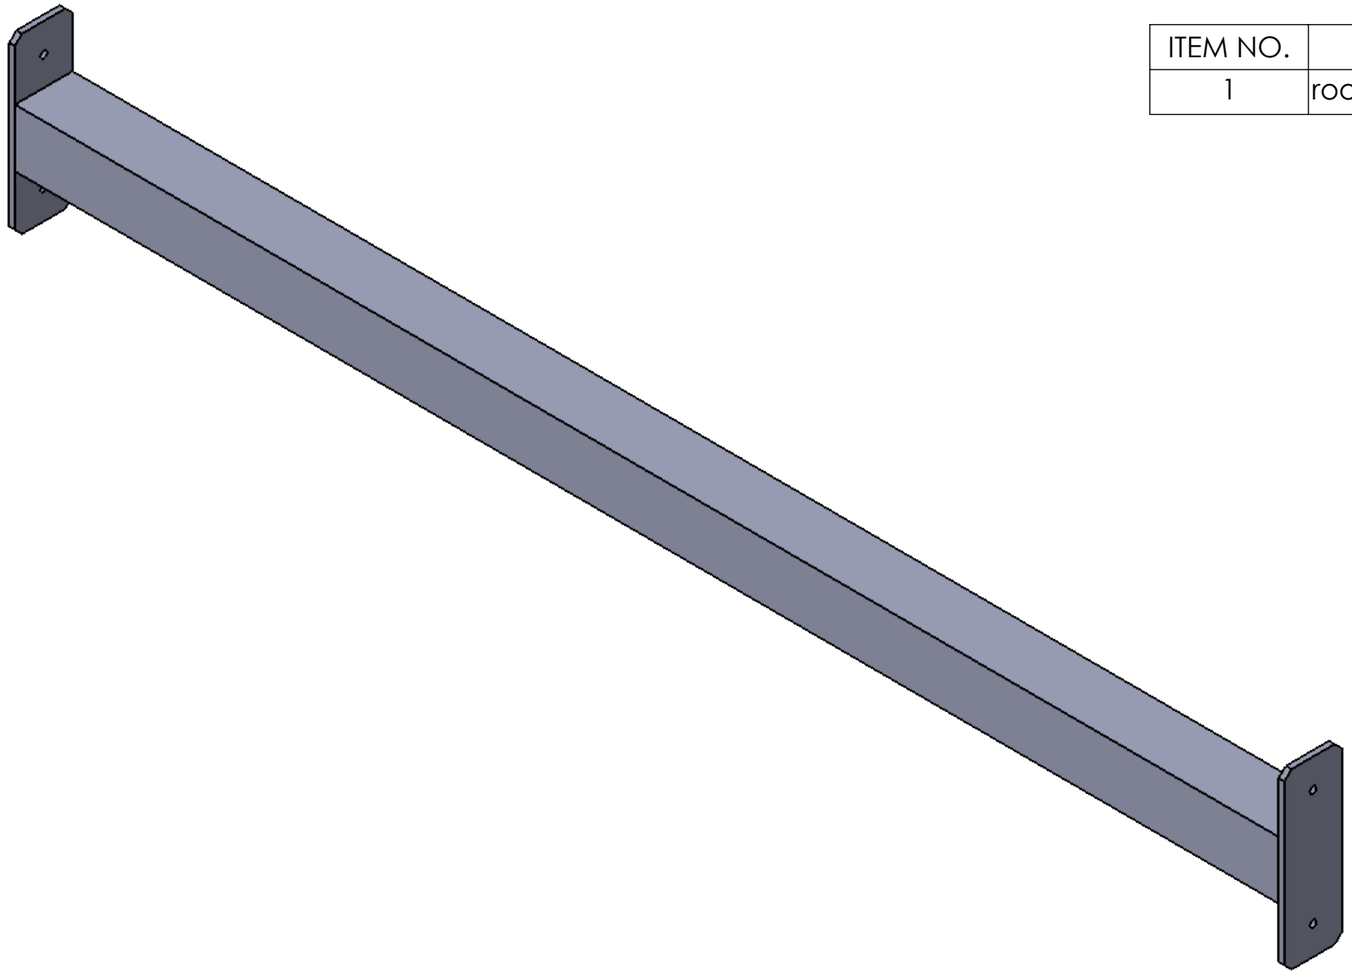


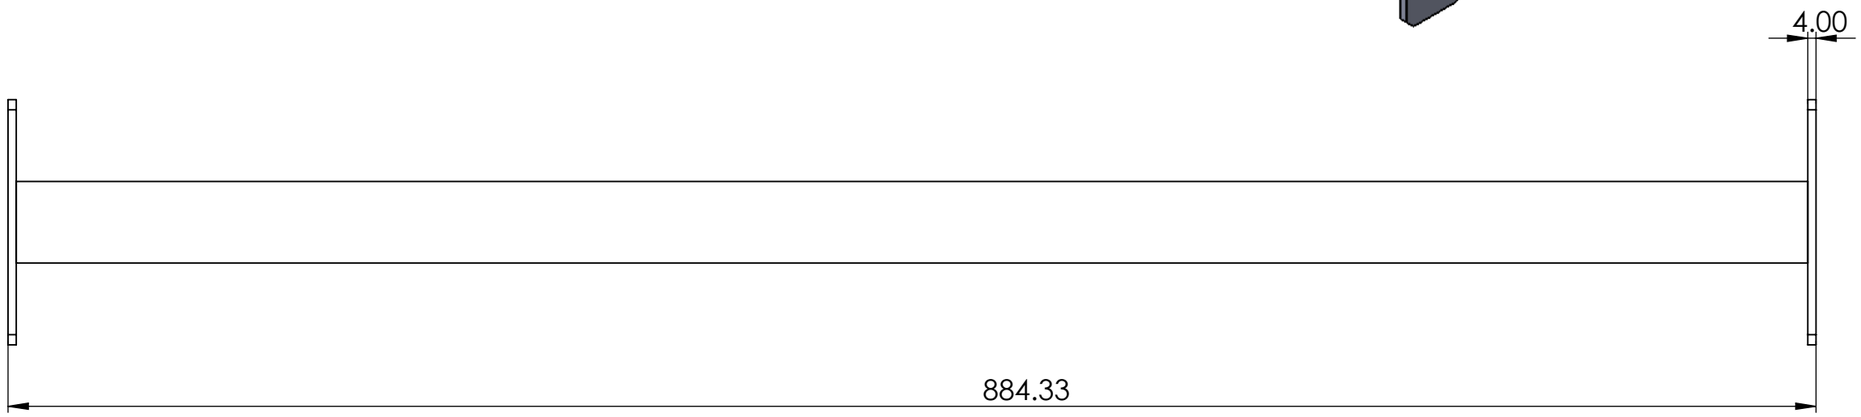


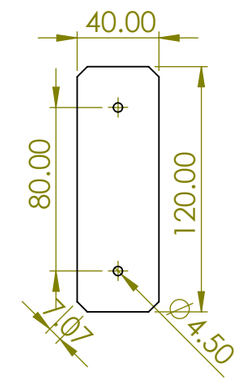

TITLE - RETRACTABLE ROOF				NIHVA TECHNOLOGIES PVT.LTD.PUNE
DWG NO - NTPL277-PM-001-01-000-03				Website - www.nihva.com
	NAME	SIGNATURE	DATE	PROJECT NO - NTPL277-PM
DRAWN	J.P		10-04-2025	PRODUCT - RETRACTABLE ROOF
CHK'D	S.W		10-04-2025	SITE LOCATION - AYODHYA
APPV'D	V.T.		10-04-2025	
if any queries contact - supportautomation@nihva.com				REVISION - QTY - 1
ALL DIMENSION ARE IN mm		A3		SCALE - SHEET 5 OF 24


ITEM NO.	PART NUMBER	DESCRIPTION	QTY.
1	L PLATE	SS304- 91X106X3 MM THK	24

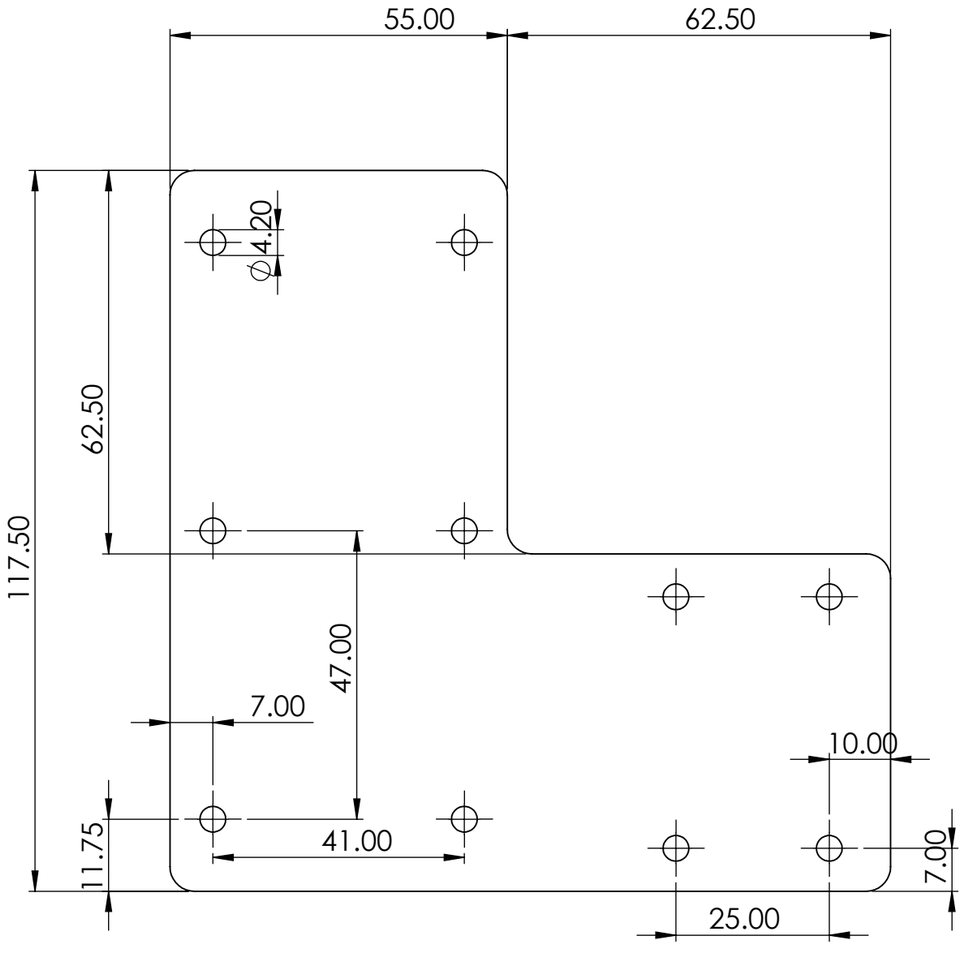


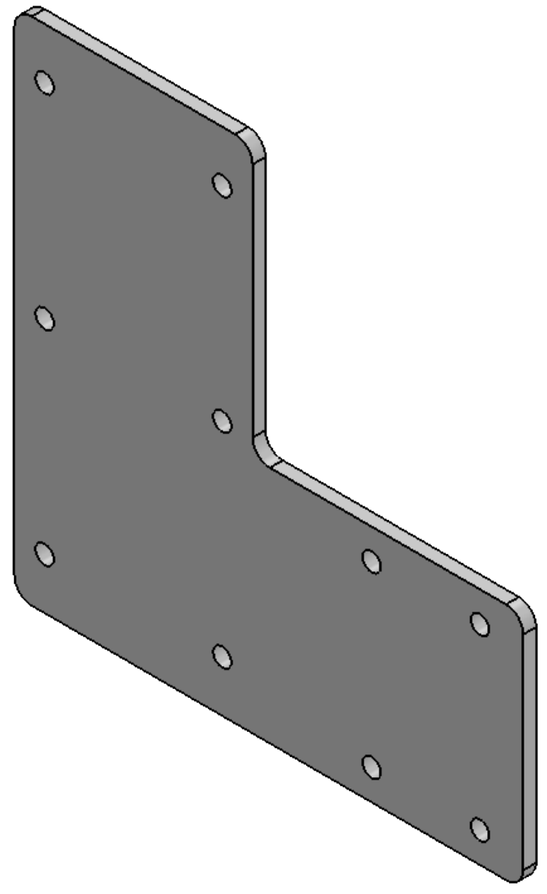


TITLE - RETRACTABLE ROOF				NIHVA TECHNOLOGIES PVT.LTD.PUNE
DWG NO - NTPL277-PM-001-01-000-04				Website - www.nihva.com
	NAME	SIGNATURE	DATE	PROJECT NO - NTPL277-PM
DRAWN	J.P		10-04-2025	PRODUCT - RETRACTABLE ROOF
CHK'D	S.W		10-04-2025	SITE LOCATION - AYODHYA
APPV'D	V.T.		10-04-2025	
if any queries contact - supportautomation@nihva.com				REVISION - QTY - 1
ALL DIMENSION ARE IN mm			A3	SCALE - SHEET 6 OF 24

ITEM NO.	PART NUMBER	DESCRIPTION	QTY.
1	L ANGLE PLATE	SS304 - 60X60X3 MM	36

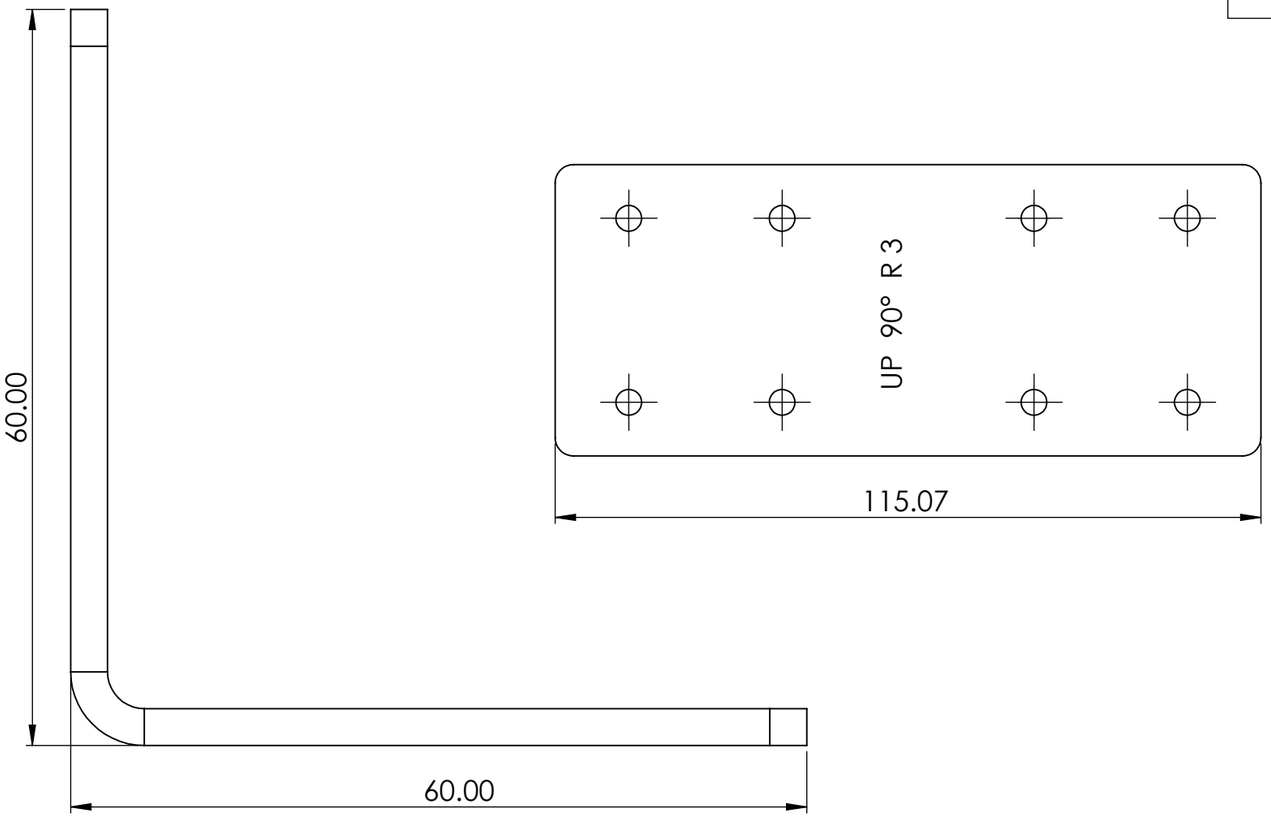


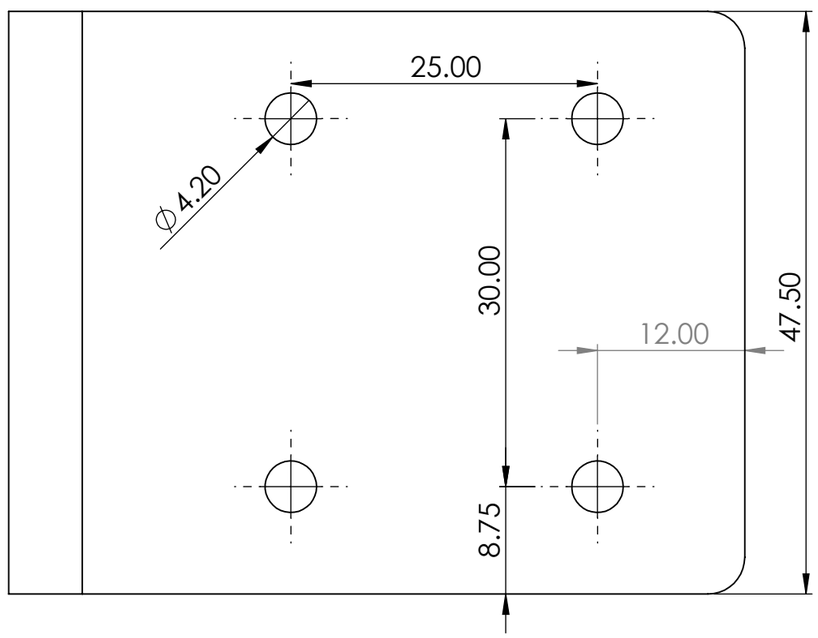


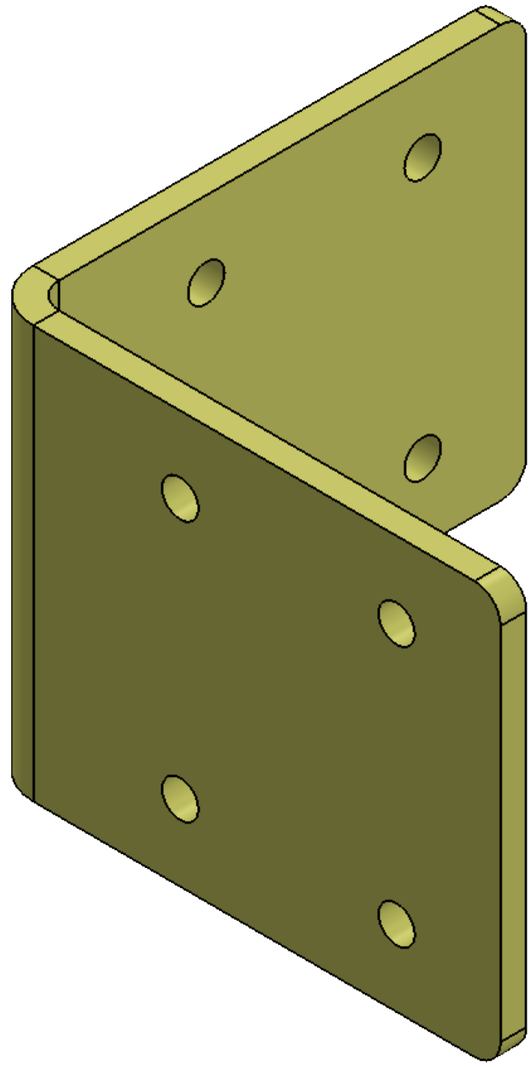

TITLE - RETRACTABLE ROOF				NIHVA TECHNOLOGIES PVT.LTD.PUNE
DWG NO - NTPL277=PM-001-01-000-05				Website - www.nihva.com
	NAME	SIGNATURE	DATE	PROJECT NO - NTPL277-PM
DRAWN	J.P		10-04-2025	PRODUCT - RETRACTABLE ROOF
CHK'D	S.W		10-04-2025	SITE LOCATION - AYODHYA
APPV'D	V.T.		10-04-2025	
if any queries contact - supportautomation@nihva.com				REVISION - QTY - 1
ALL DIMENSION ARE IN mm		A3		SCALE - SHEET 7 OF 24


ITEM NO.	PART NUMBER	DESCRIPTION	QTY.
1	T PLATE	SS304 -117.5X156X3 MM THK	24

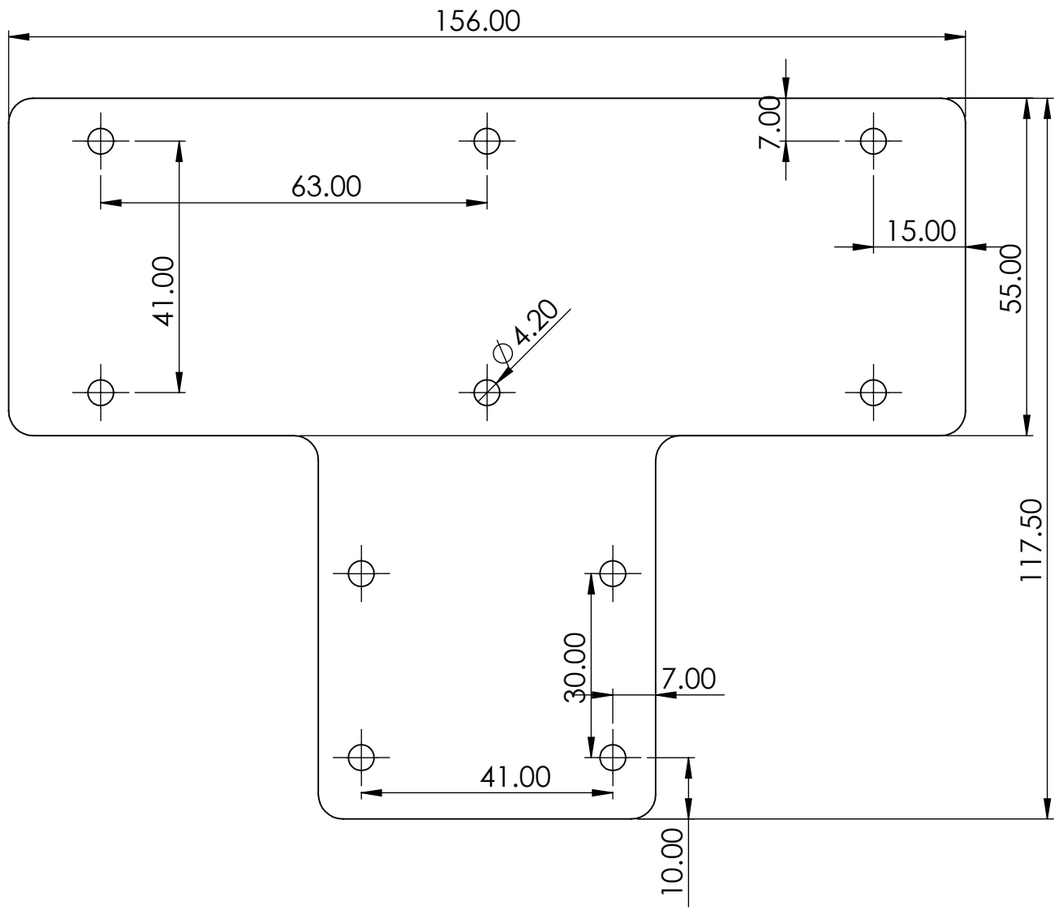


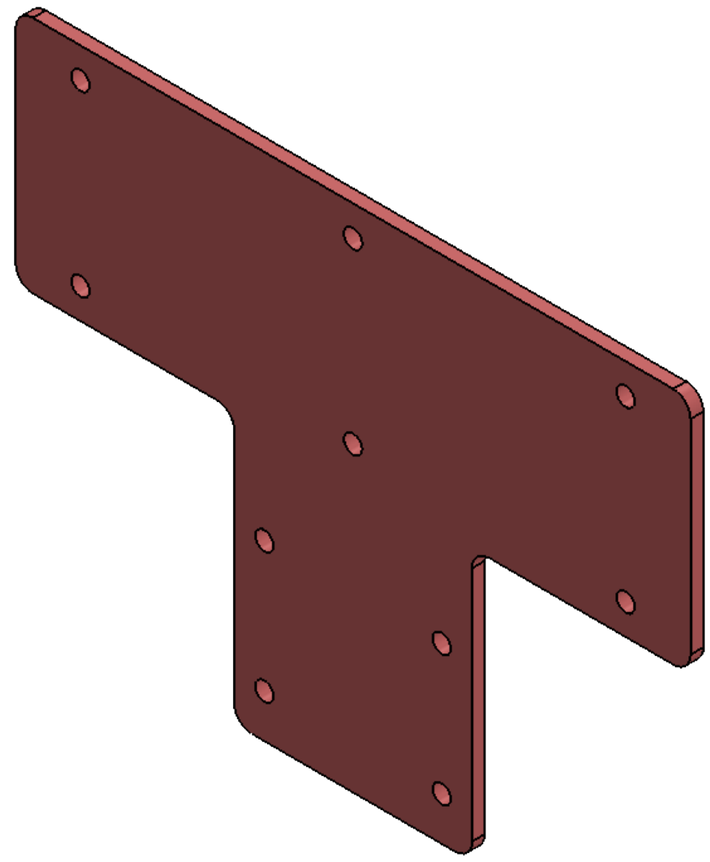


TITLE - RETRACTABLE ROOF				NIHVA TECHNOLOGIES PVT.LTD.PUNE
DWG NO - NTPL277-PM-001-01-000-06				Website - www.nihva.com
	NAME	SIGNATURE	DATE	PROJECT NO - NTPL277-PM
DRAWN	J.P		10-04-2025	PRODUCT - RETRACTABLE ROOF
CHK'D	S.W		10-04-2025	SITE LOCATION - AYODHYA
APPV'D	V.T.		10-04-2025	
if any queries contact - supportautomation@nihva.com				REVISION - QTY - 1
ALL DIMENSION ARE IN mm		A3		SCALE - SHEET 8 OF 24


ITEM NO.	PART NUMBER	DESCRIPTION	QTY.
1	2D DRAWING PROFILE L ANGLE WELDING PLATE	JOINING PLATE Al metal	24

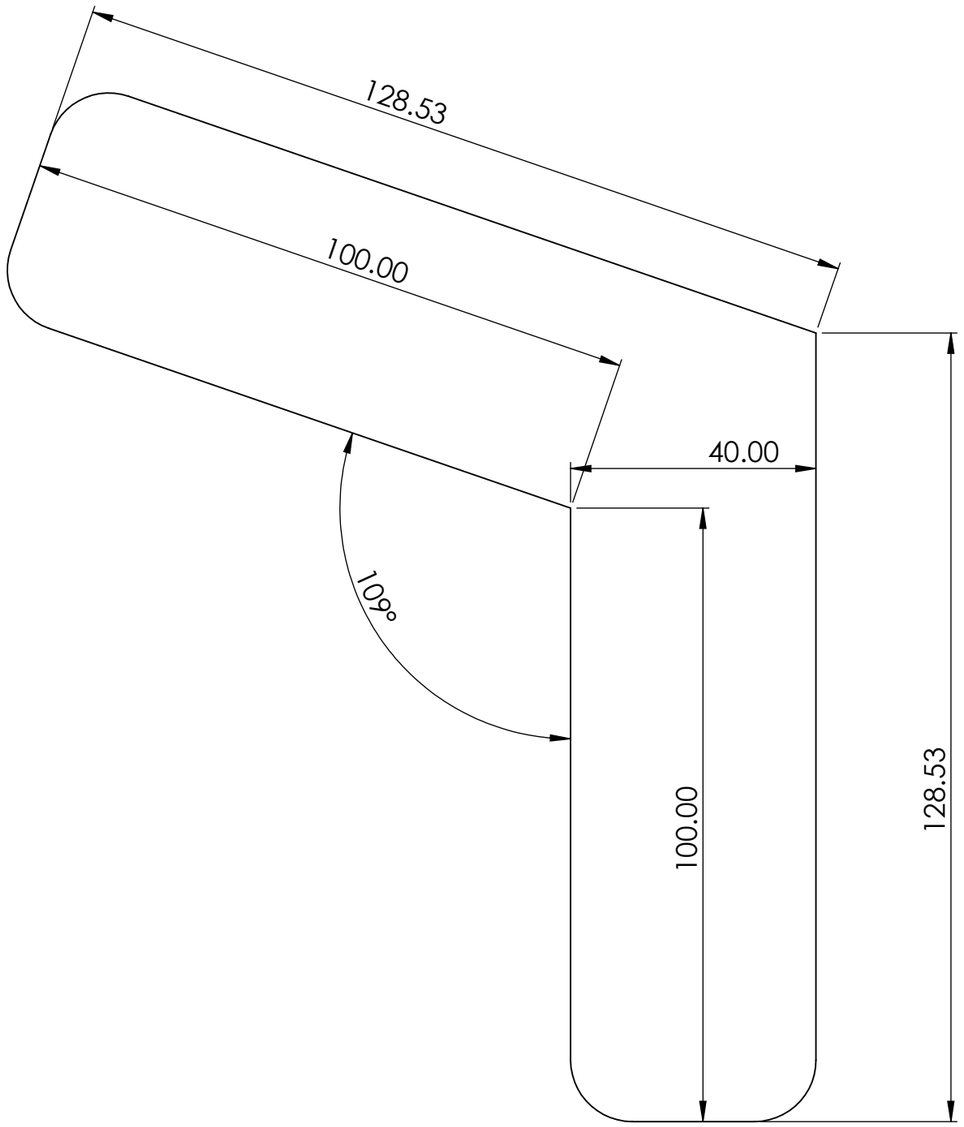


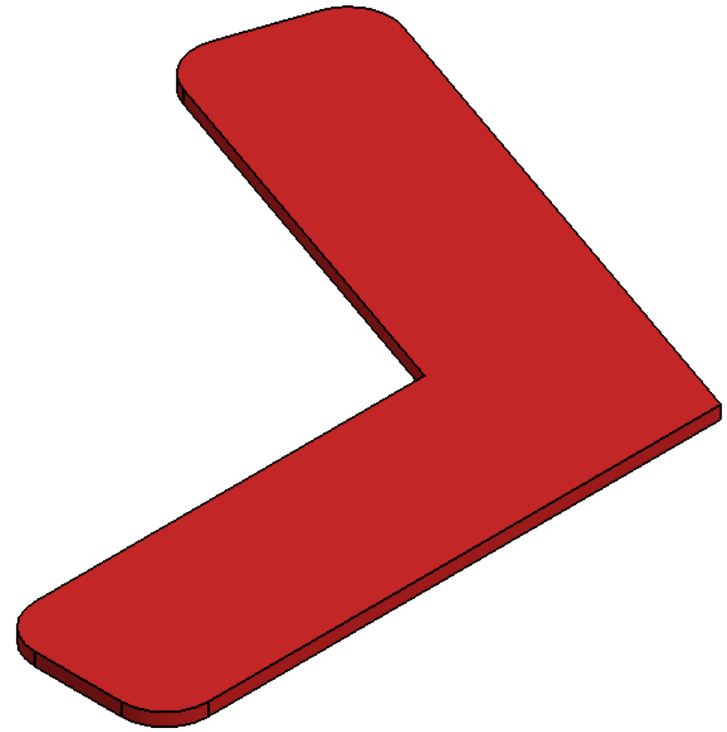

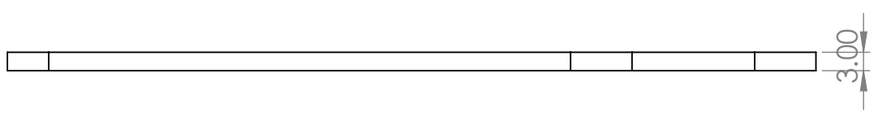


TITLE - RETRACTABLE ROOF				NIHVA TECHNOLOGIES PVT.LTD.PUNE Website - www.nihva.com
DWG NO - NTPL277-PM-001-01-000-07				
	NAME	SIGNATURE	DATE	PROJECT NO - NTPL277-PM
DRAWN	J.P		10-04-2025	PRODUCT - RETRACTABLE ROOF
CHK'D	S.W		10-04-2025	SITE LOCATION - AYODHYA
APPV'D	V.T.		10-04-2025	
if any queries contact - supportautomation@nihva.com				REVISION - QTY - 1
ALL DIMENSION ARE IN mm		A3		SCALE - SHEET 9 OF 24

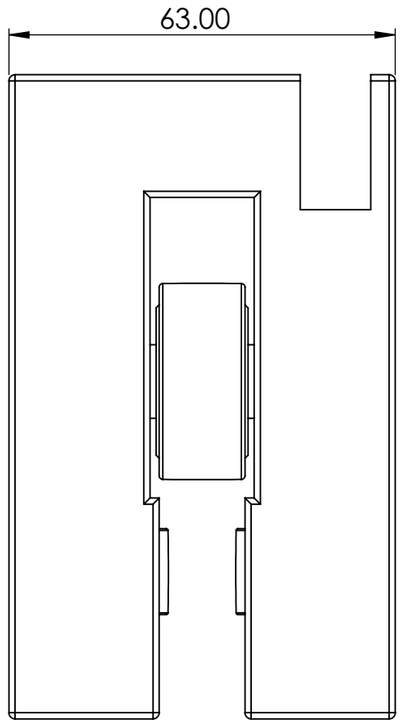

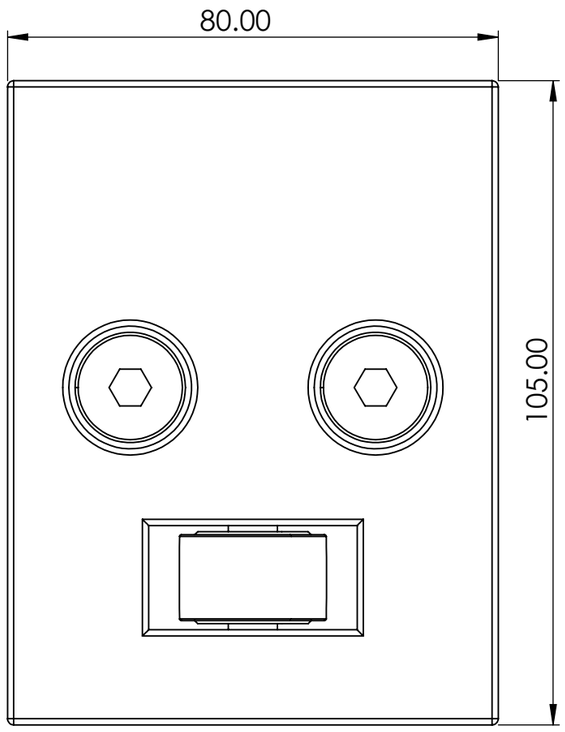



ITEM NO.	PART NUMBER	DESCRIPTION	QTY.
1	BEARING BLOCK (T75-1B)	80X105X63 MM (VMC PART)	1
2	SKF_NATR 12	BRG(STD)	2
3	SKF_NATR 8	BRG(STD)	2
4	2D DRAWING SHOULDER BOLT NATR 12 12x36 M10		2
5	ISO 7379 - 8 x 30 --- N M8		2

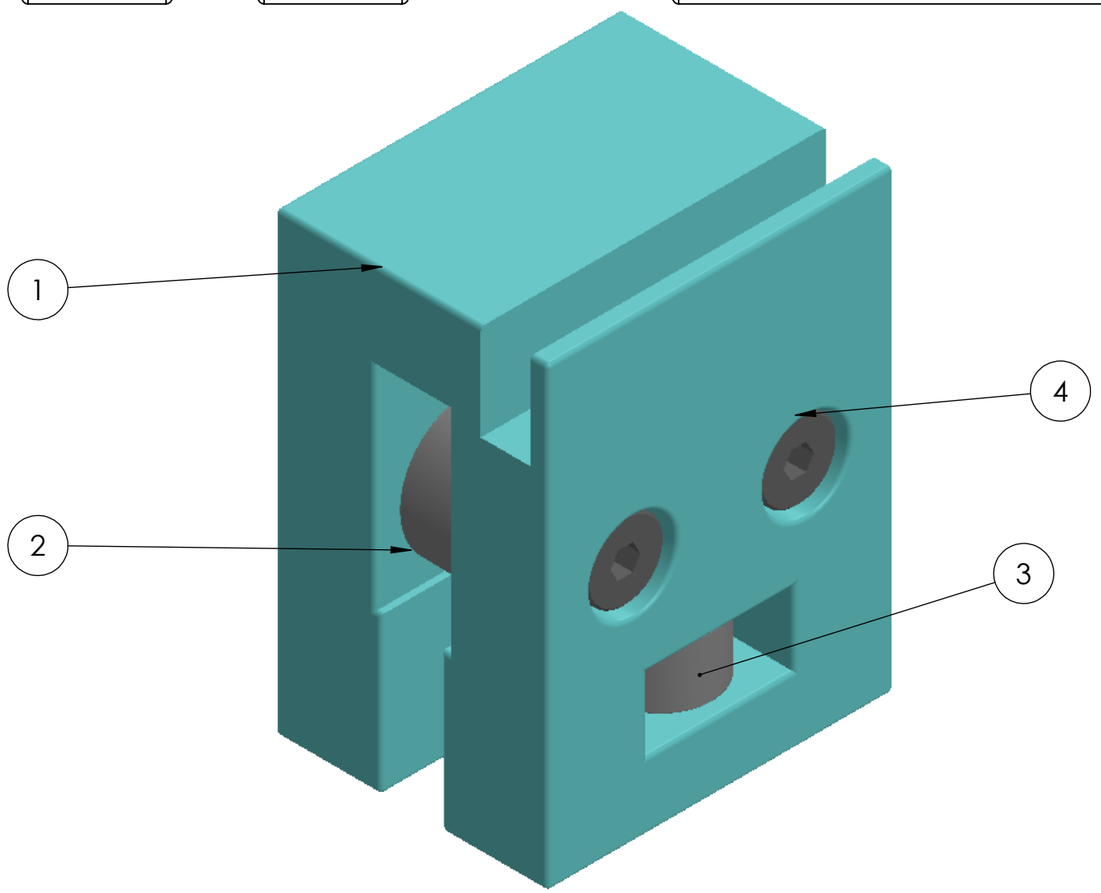



TITLE - RETRACTABLE ROOF				NIHVA TECHNOLOGIES PVT.LTD.PUNE Website - www.nihva.com
DWG NO - NTPL277-PM-001-01-001-00				
	NAME	SIGNATURE	DATE	PROJECT NO - NTPL277-PM
DRAWN	J.P		10-04-2025	PRODUCT - RETRACTABLE ROOF
CHK'D	S.W		10-04-2025	SITE LOCATION - AYODHYA
APPV'D	V.T.		10-04-2025	
if any queries contact - supportautomation@nihva.com				REVISION - QTY - 1
ALL DIMENSION ARE IN mm		A3		SCALE - SHEET 10 OF 24

ITEM NO.	PART NUMBER	DESCRIPTION	QTY.
1	BEARING BLOCK (T75-1B)	80X105X63 MM (VMC PART)	12

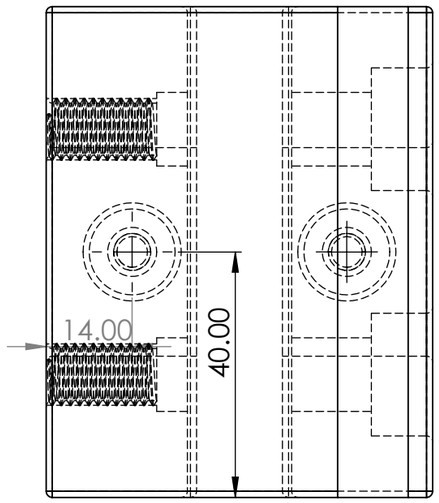

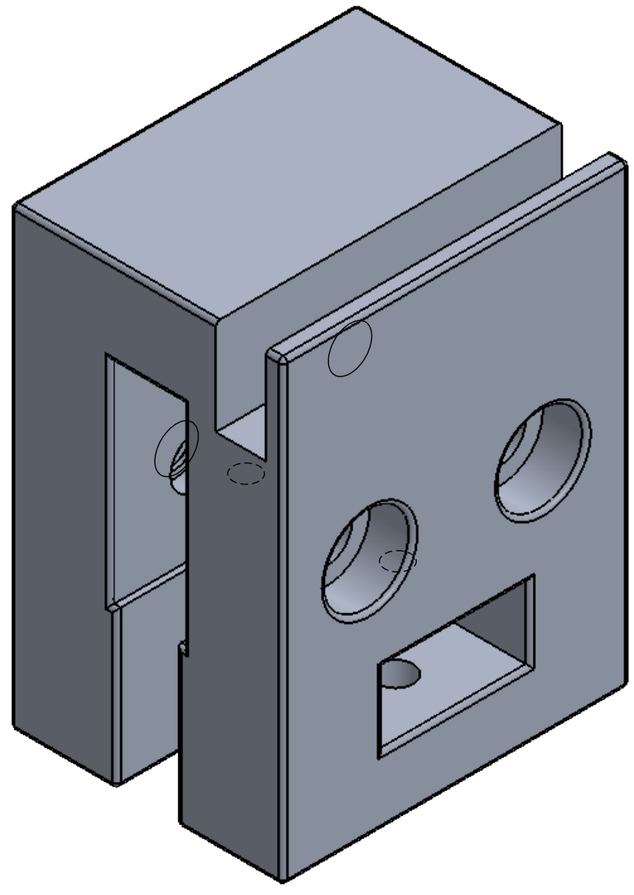

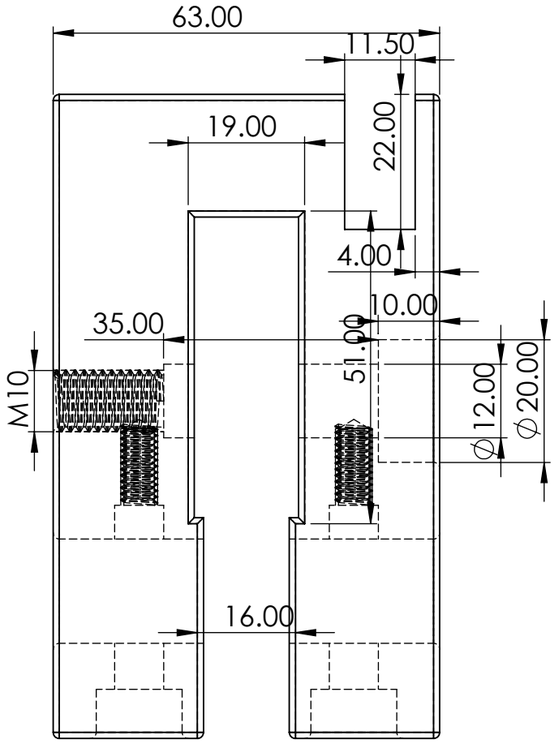

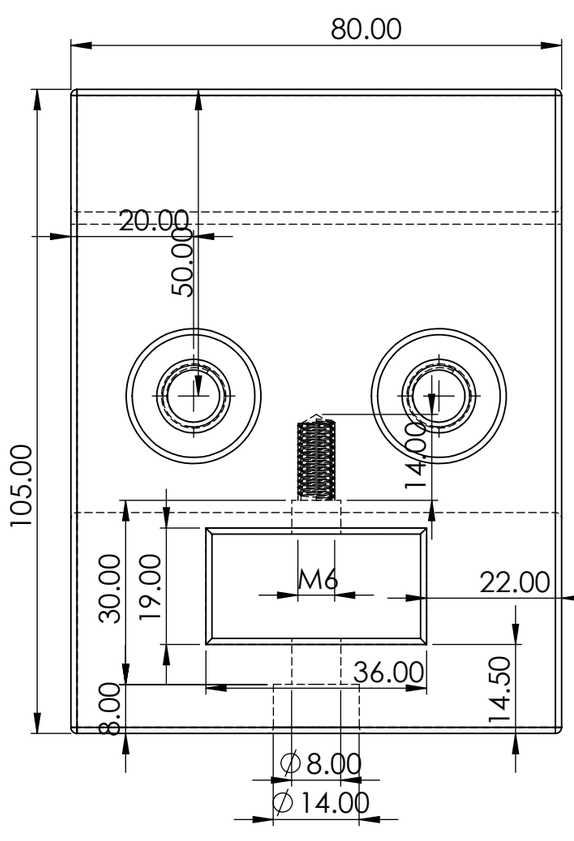

TITLE - RETRACTABLE ROOF

DWG NO - NTPL277-PM-001-01-001-01


NIHVA TECHNOLOGIES PVT.LTD.PUNE

Website - www.nihva.com


	NAME	SIGNATURE	DATE	PROJECT NO - NTPL277-PM
DRAWN	J.P		10-04-2025	PRODUCT - RETRACTABLE ROOF
CHK'D	S.W		10-04-2025	SITE LOCATION - AYODHYA
APPV'D	V.T.		10-04-2025	


if any queries contact - supportautomation@nihva.com | REVISION - | QTY - 1

ALL DIMENSION ARE IN mm | A3 | SCALE - | SHEET 11 OF 24

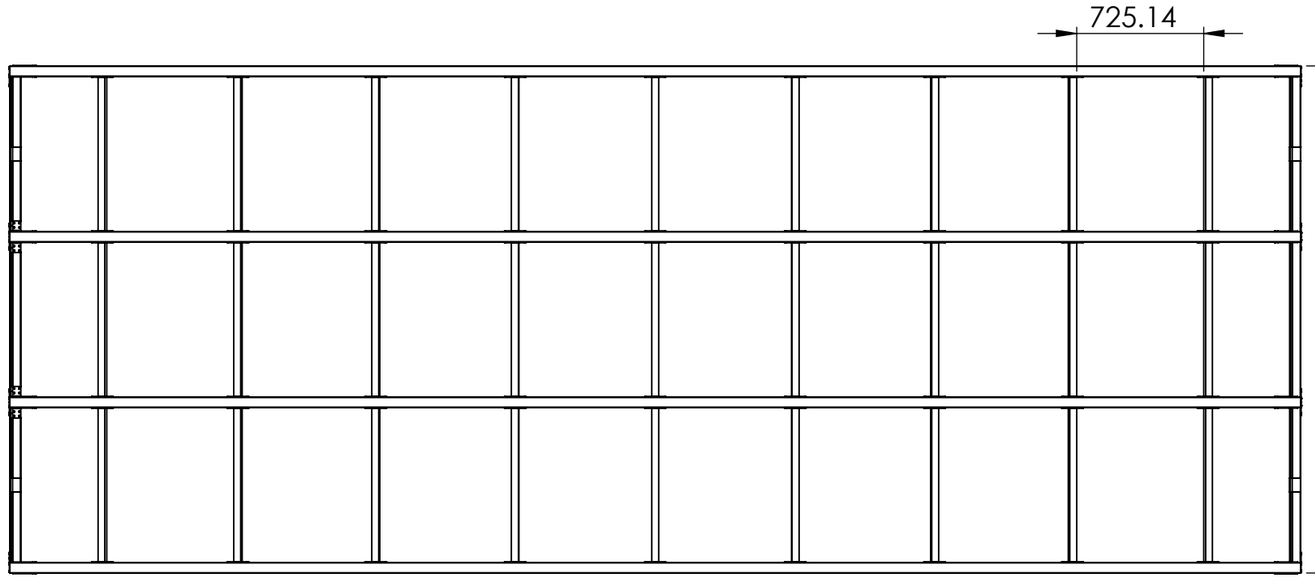

ITEM NO.	PART NUMBER	DESCRIPTION	QTY.
1	2panel 1 ass.		1
2	L PALTE	JOINING PLATE	4
3	2D DRAWING PROFILE L ANGLE WELDING PLATE	JOINING PLATE Al metal	8
4	T PLATE	JOINING PLATE	5
5	L ANGLE PLATE	JOINING PLATE	4

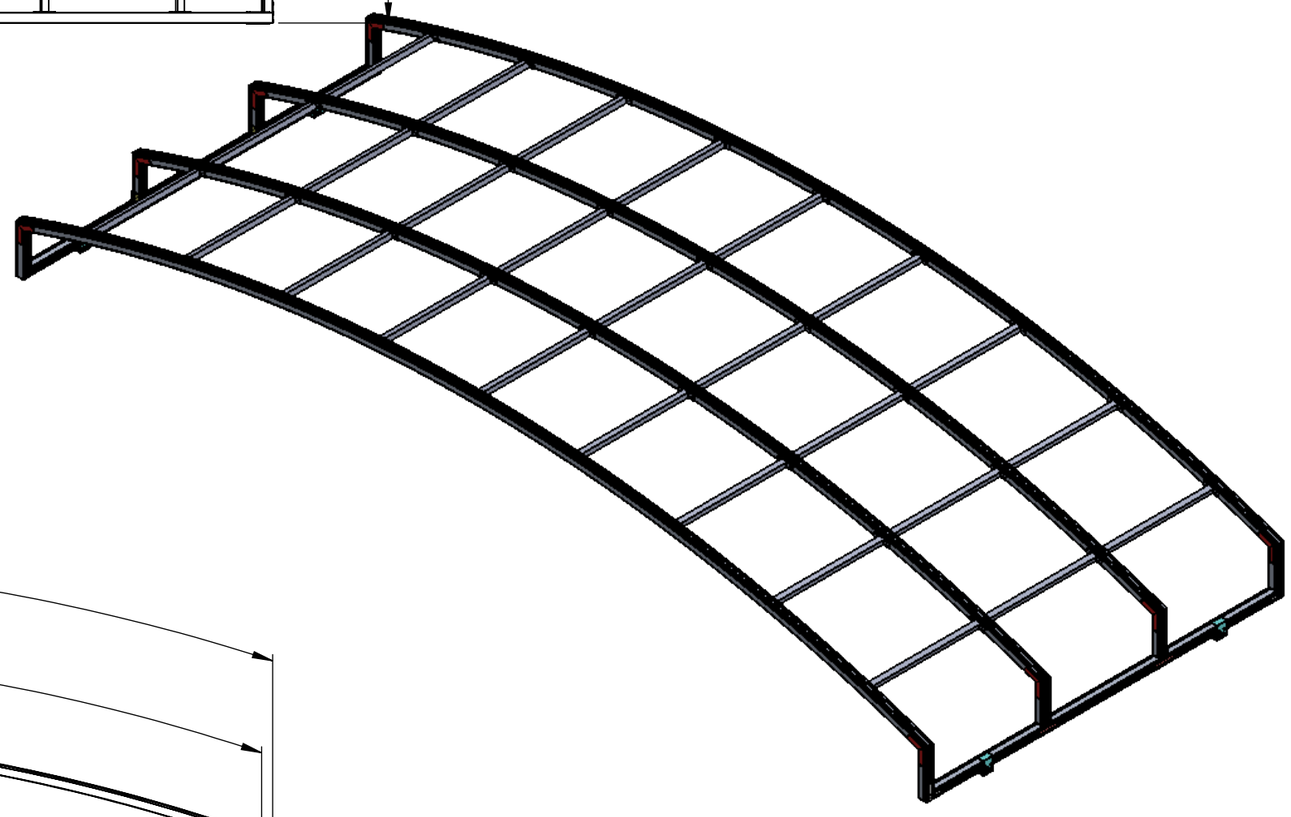


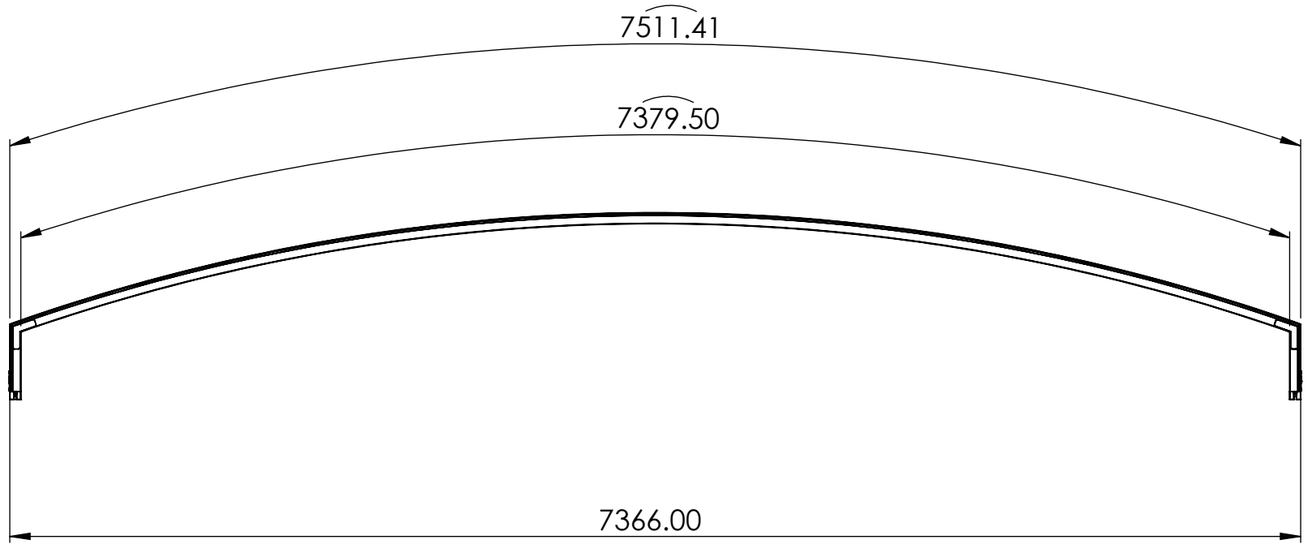

TITLE - RETRACTABLE ROOF				NIHVA TECHNOLOGIES PVT.LTD.PUNE
DWG NO - NTPL277-PM-001-02-000-00				Website - www.nihva.com
	NAME	SIGNATURE	DATE	PROJECT NO - NTPL277-PM
DRAWN	J.P		10-04-2025	PRODUCT - RETRACTABLE ROOF
CHK'D	S.W		10-04-2025	SITE LOCATION - AYODHYA
APPV'D	V.T.		10-04-2025	
if any queries contact - supportautomation@nihva.com				REVISION - QTY - 1
ALL DIMENSION ARE IN mm			A3	SCALE - SHEET 12 OF 24


ITEM NO.	PART NUMBER	DESCRIPTION	QTY.
1	panel 2		1




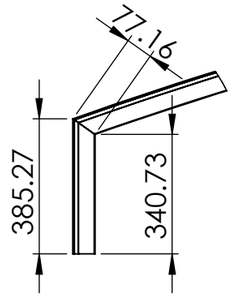

DETAIL C


SCALE 2 : 35

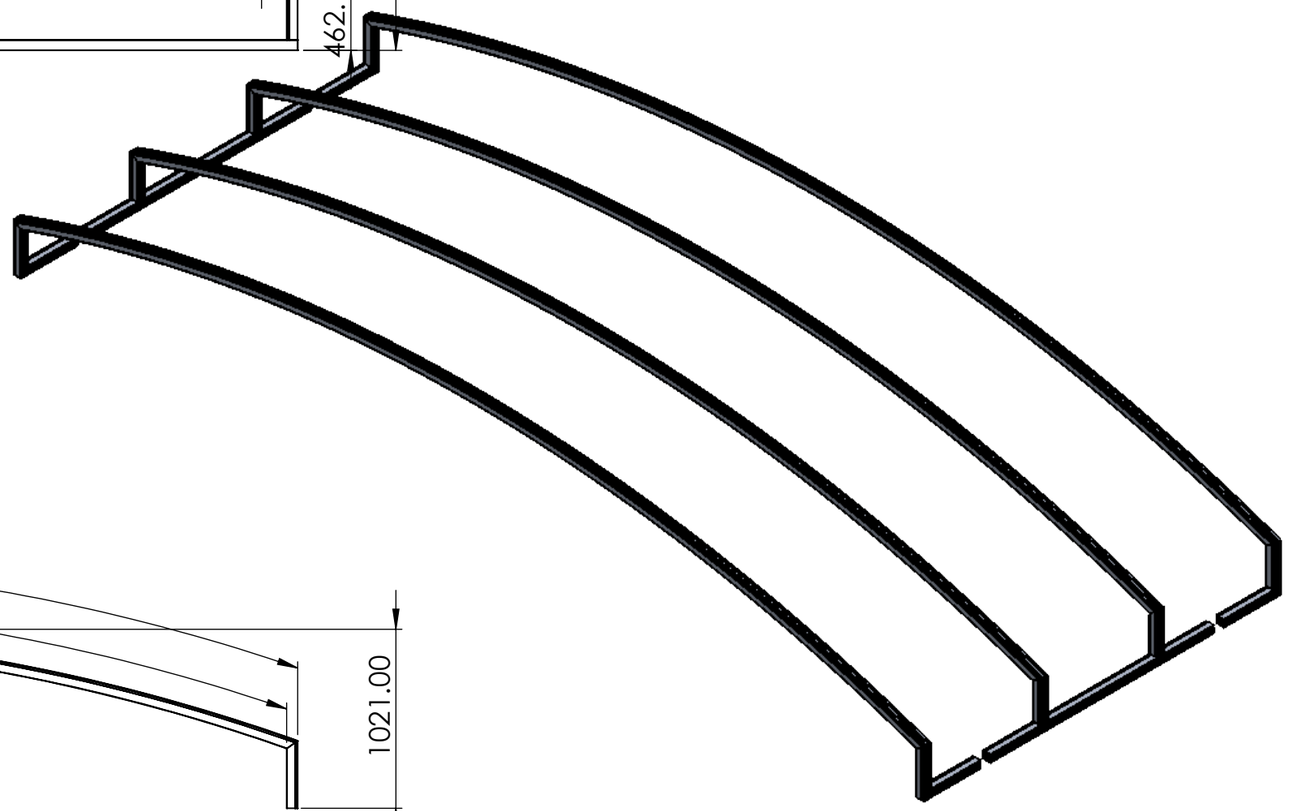


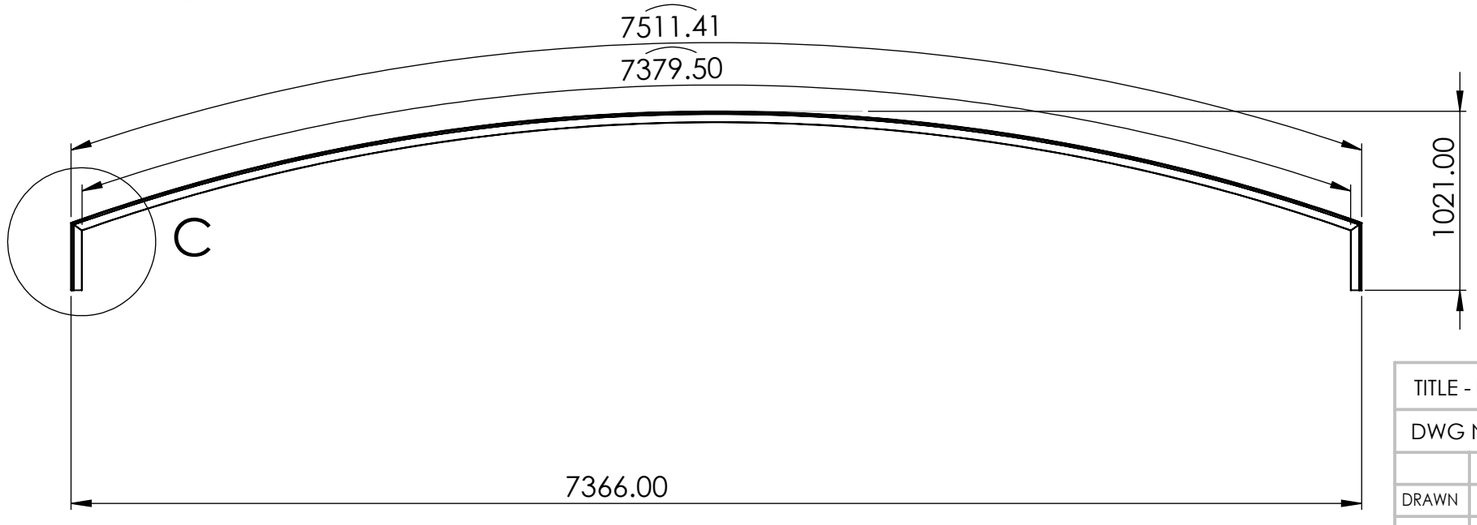


TITLE - RETRACTABLE ROOF				NIHVA TECHNOLOGIES PVT.LTD.PUNE Website - www.nihva.com
DWG NO - NTPL277-PM-001-02-000-01				
	NAME	SIGNATURE	DATE	PROJECT NO - NTPL277-PM
DRAWN	J.P		10-04-2025	PRODUCT - RETRACTABLE ROOF
CHK'D	S.W		10-04-2025	SITE LOCATION - AYODHYA
APPV'D	V.T.		10-04-2025	
if any queries contact - supportautomation@nihva.com				REVISION - QTY - 1
ALL DIMENSION ARE IN mm			A3	SCALE - SHEET 13 OF 24


ITEM NO.	PART NUMBER	DESCRIPTION	QTY.
1	panel 3 ass.		1
2	panel 3 closer		1
3	L PALTE	JOINING PLATE	4
4	2D DRAWING PROFILE L ANGLE WELDING PLATE	JOINING PLATE Al metal	16
5	T PLATE	JOINING PLATE	4
6	L ANGLE PLATE	JOINING PLATE	4

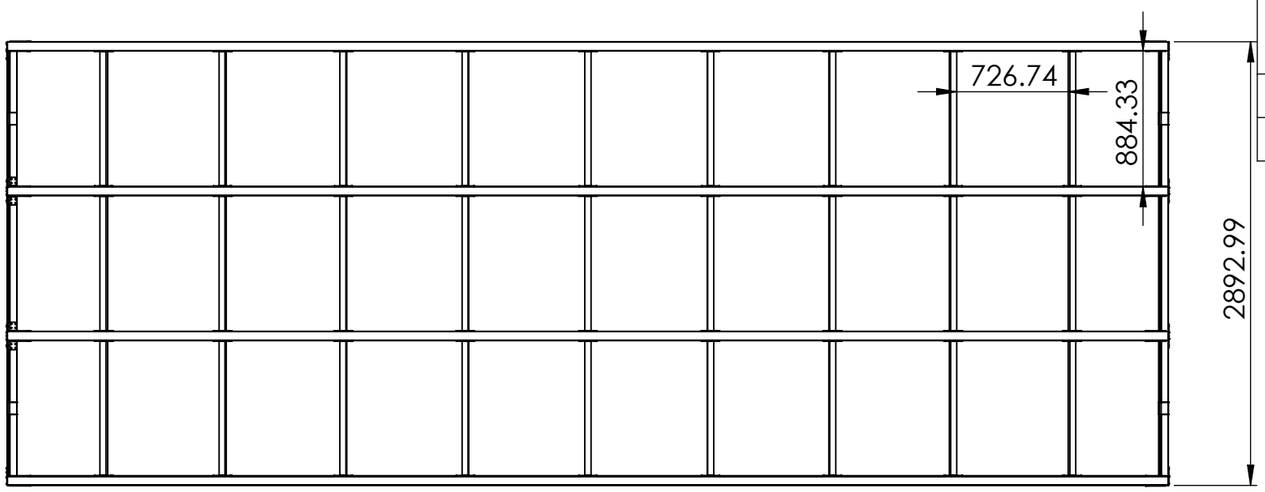

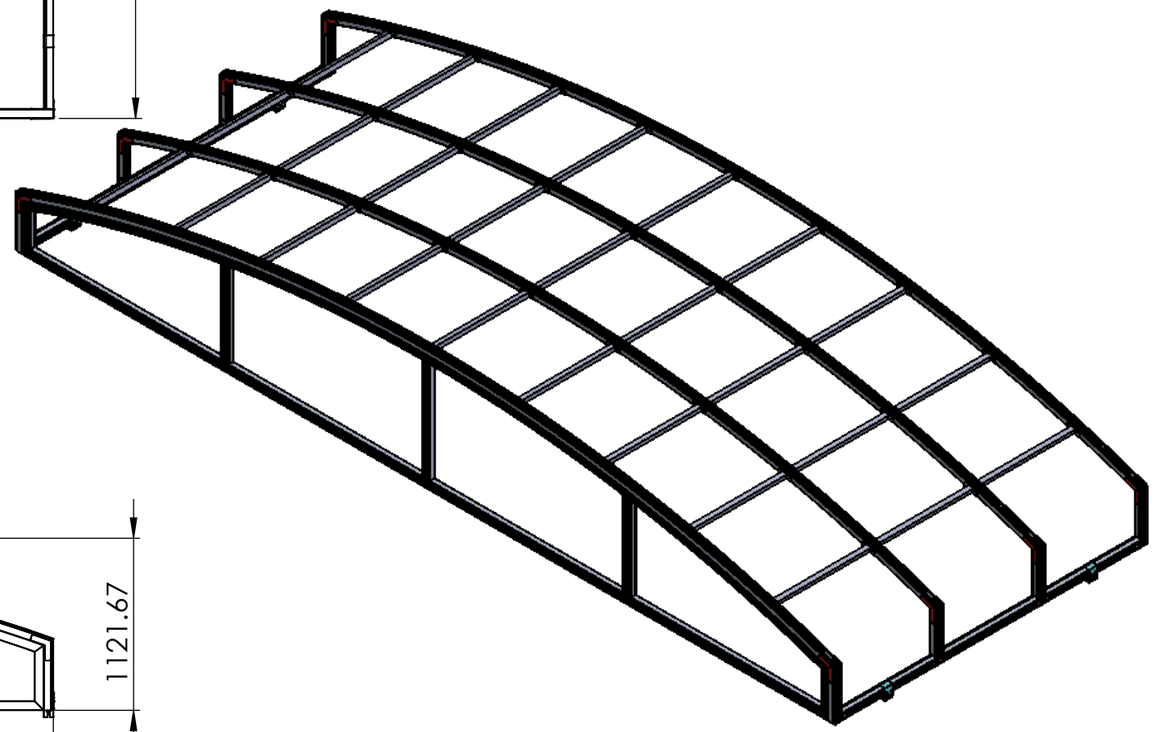


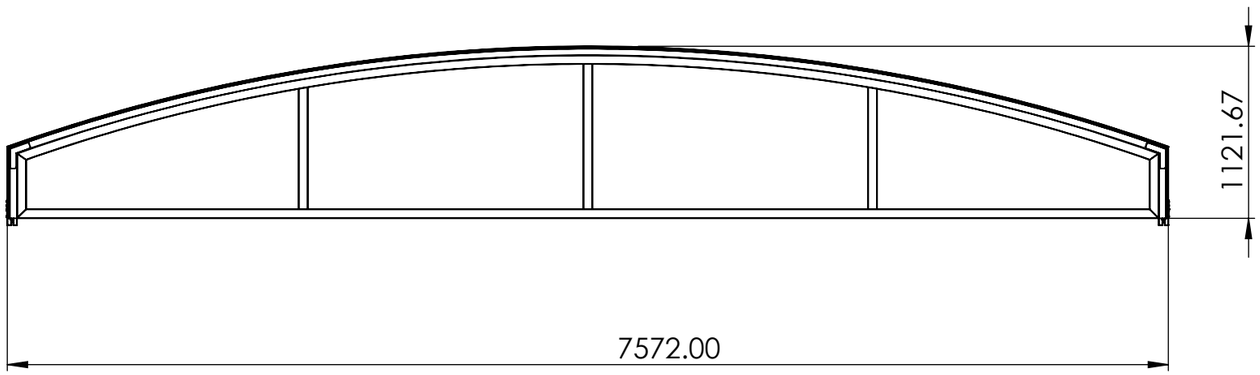

TITLE - RETRACTABLE ROOF				NIHVA TECHNOLOGIES PVT.LTD.PUNE
DWG NO - NTPL277-PM-001-03-000-00				Website - www.nihva.com
	NAME	SIGNATURE	DATE	PROJECT NO - NTPL277-PM
DRAWN	J.P		10-04-2025	PRODUCT - RETRACTABLE ROOF
CHK'D	S.W		10-04-2025	SITE LOCATION - AYODHYA
APPV'D	V.T.		10-04-2025	
if any queries contact - supportautomation@nihva.com				REVISION - QTY - 1
ALL DIMENSION ARE IN mm		A3		SCALE - SHEET 14 OF 24

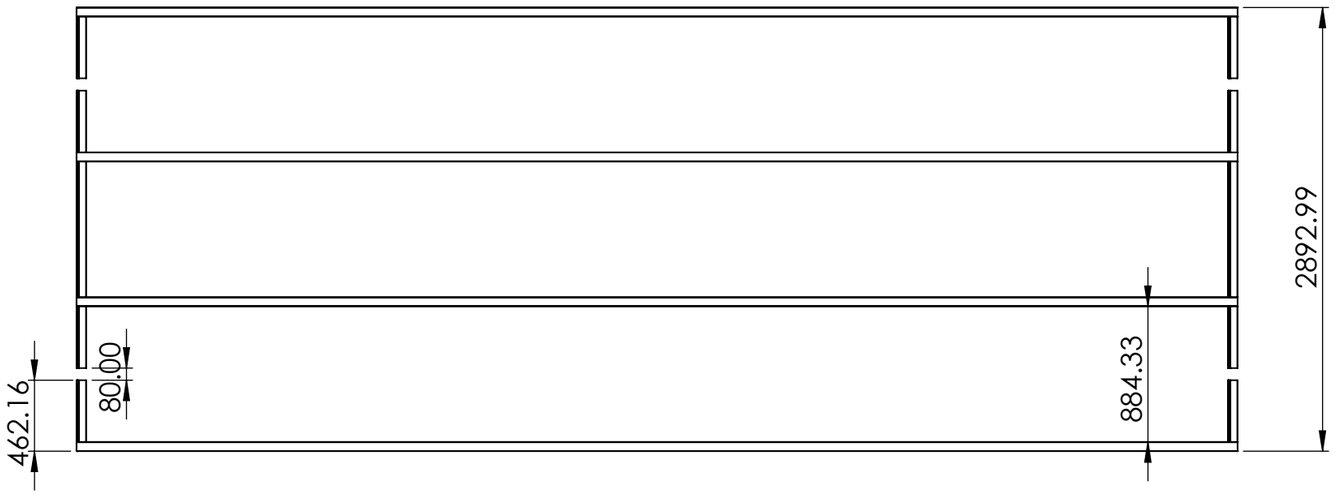



ITEM NO.	PART NUMBER	DESCRIPTION	QTY.
1	panel 3		1

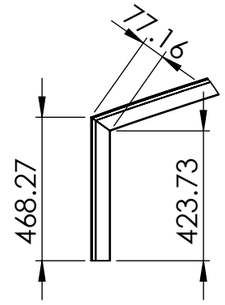

DETAIL D


SCALE 1 : 20

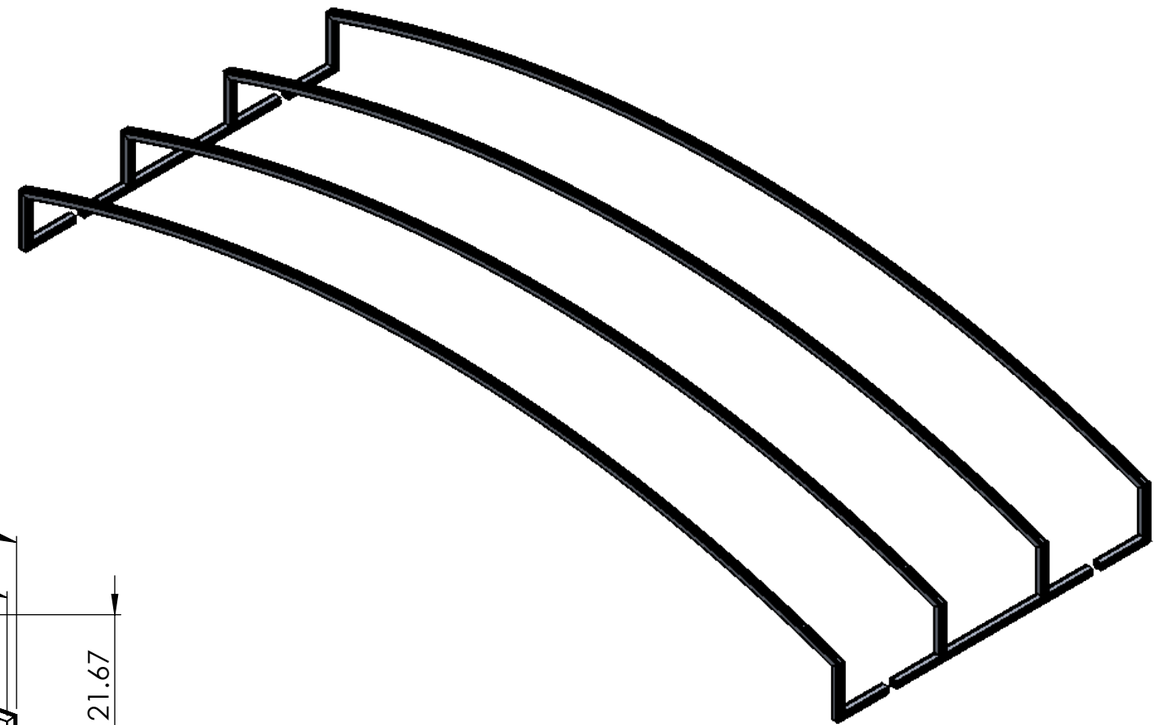


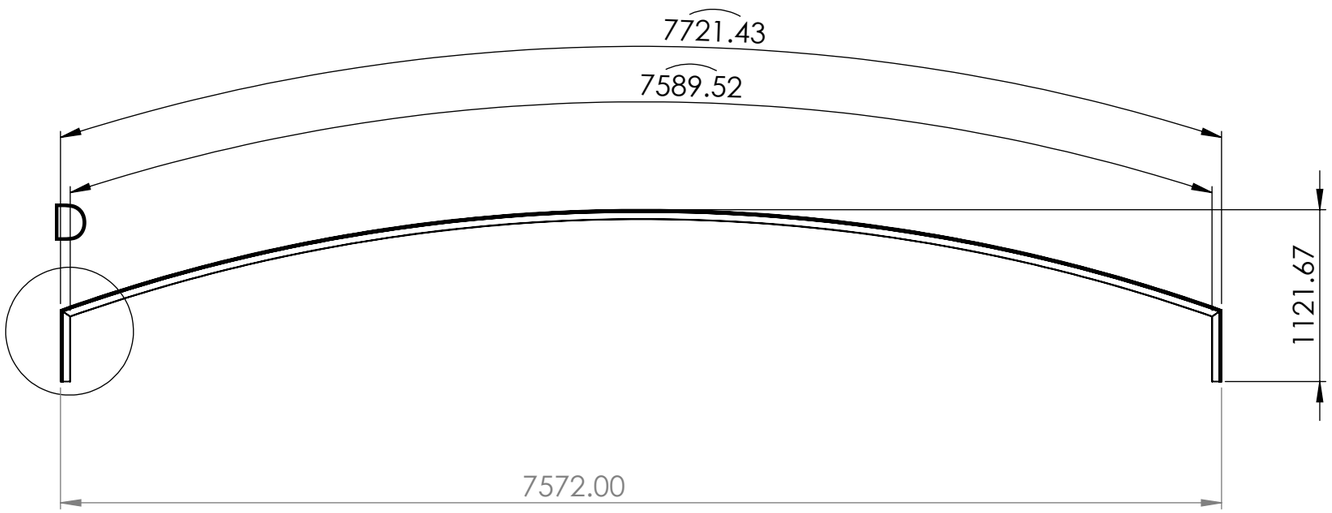

TITLE - RETRACTABLE ROOF				NIHVA TECHNOLOGIES PVT.LTD.PUNE
DWG NO - NTPL277-PM-001-03-000-01				Website - www.nihva.com
	NAME	SIGNATURE	DATE	PROJECT NO - NTPL277-PM
DRAWN	J.P		10-04-2025	PRODUCT - RETRACTABLE ROOF
CHK'D	S.W		10-04-2025	SITE LOCATION - AYODHYA
APPV'D	V.T.		10-04-2025	
if any queries contact - supportautomation@nihva.com				REVISION - QTY - 1
ALL DIMENSION ARE IN mm		A3		SCALE - SHEET 15 OF 24


ITEM NO.	PART NUMBER	DESCRIPTION	QTY.
1	panel 3 closer		1

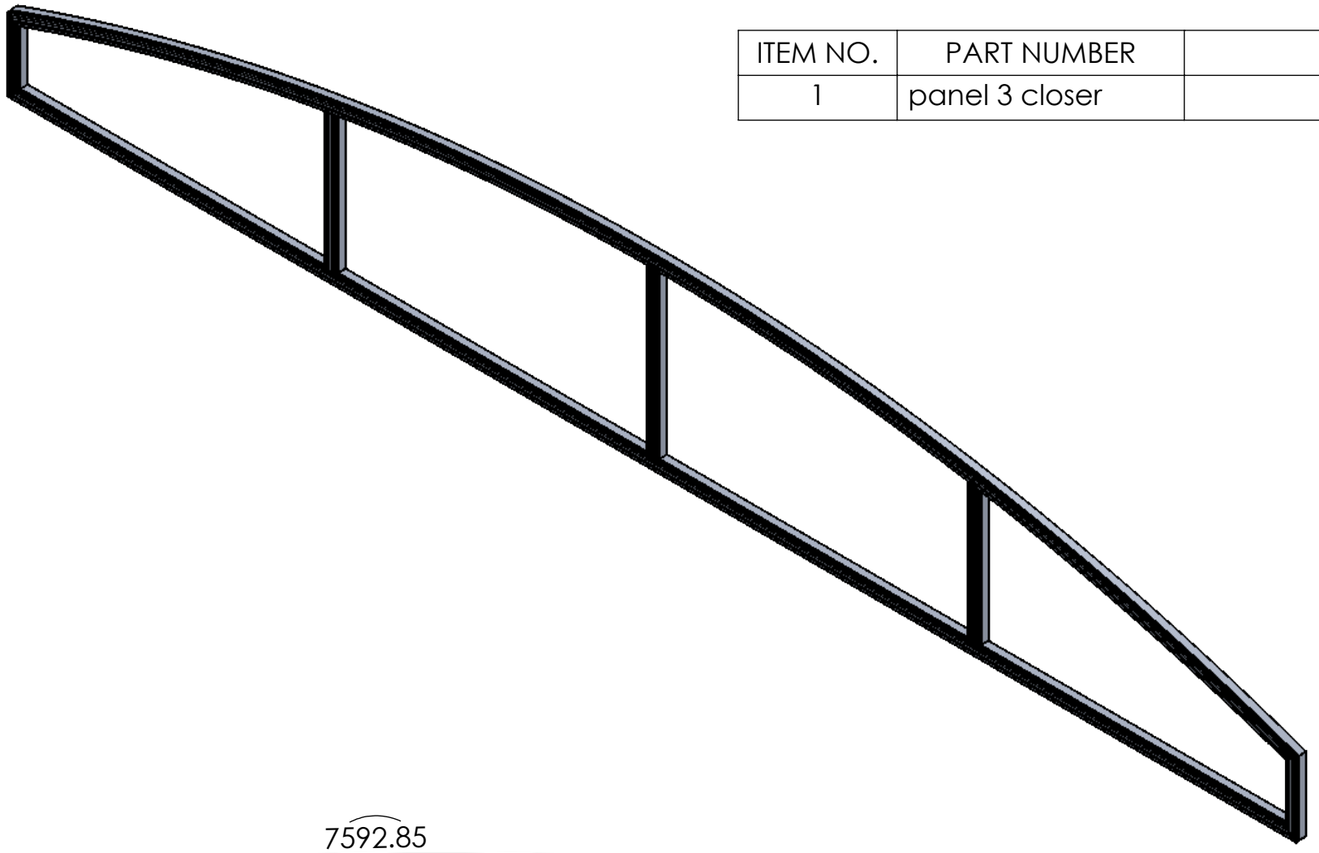

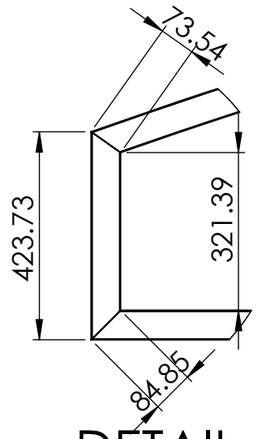

DETAIL E


SCALE 2 : 25

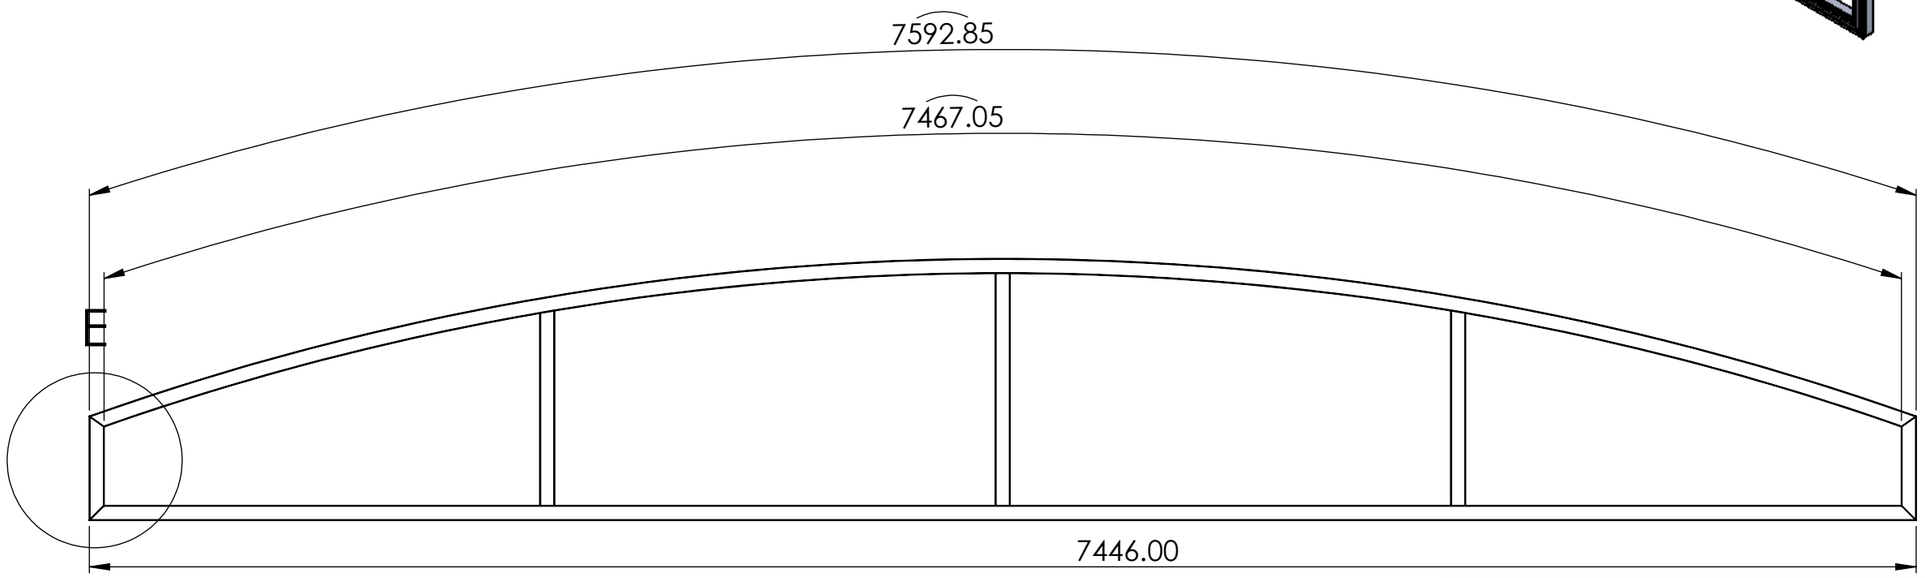




TITLE - RETRACTABLE ROOF				NIHVA TECHNOLOGIES PVT.LTD.PUNE
DWG NO - NTPL277-PM-001-00-000-00				Website - www.nihva.com
	NAME	SIGNATURE	DATE	PROJECT NO - NTPL277-PM
DRAWN	J.P		10-04-2025	PRODUCT - RETRACTABLE ROOF
CHK'D	S.W		10-04-2025	SITE LOCATION - AYODHYA
APPV'D	V.T.		10-04-2025	
if any queries contact - supportautomation@nihva.com				REVISION - QTY - 1
ALL DIMENSION ARE IN mm			A3	SCALE - SHEET 16 OF 24


ITEM NO.	PART NUMBER	DESCRIPTION	QTY.
1	MOTOR MTG BRACKET NICE 1T	MS	1

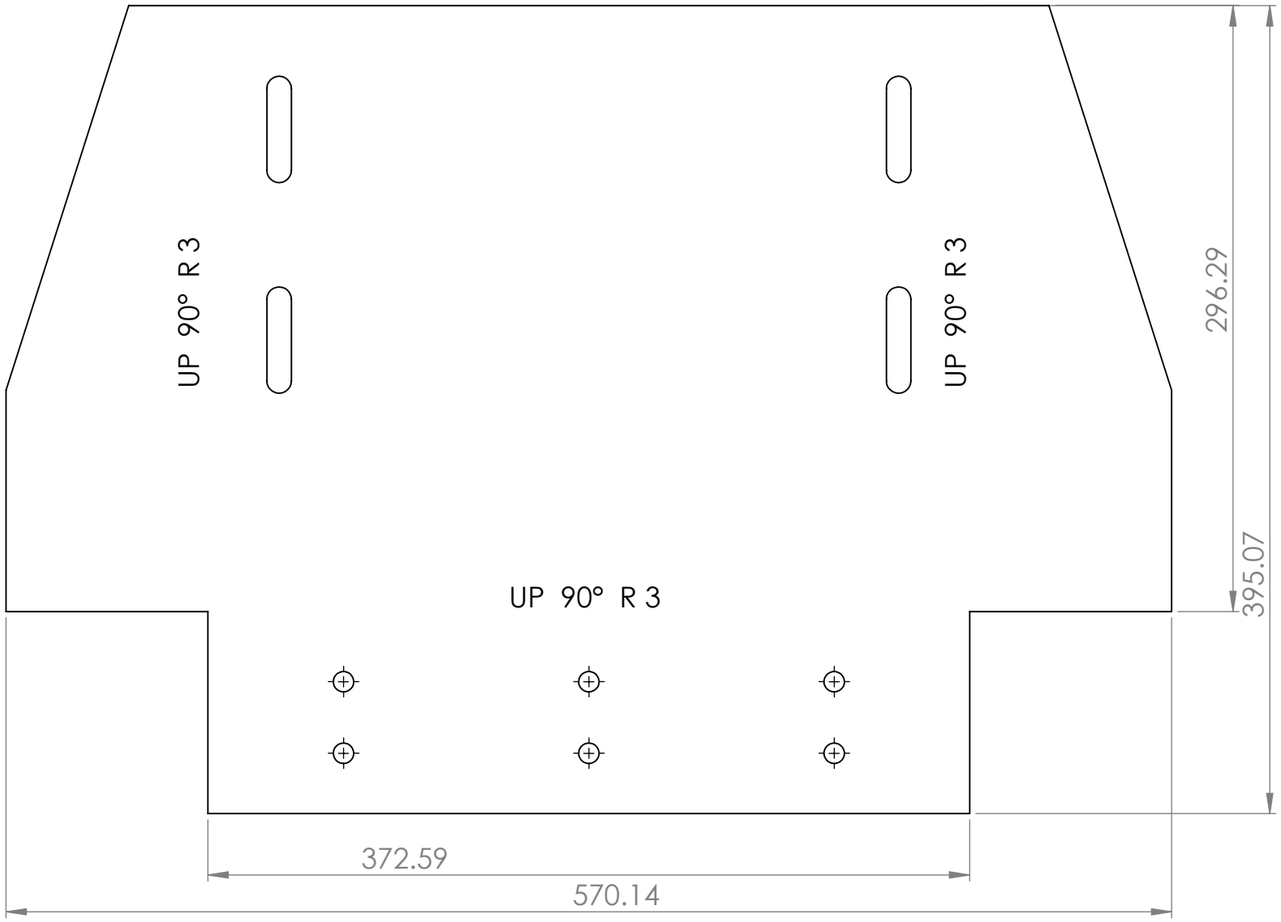


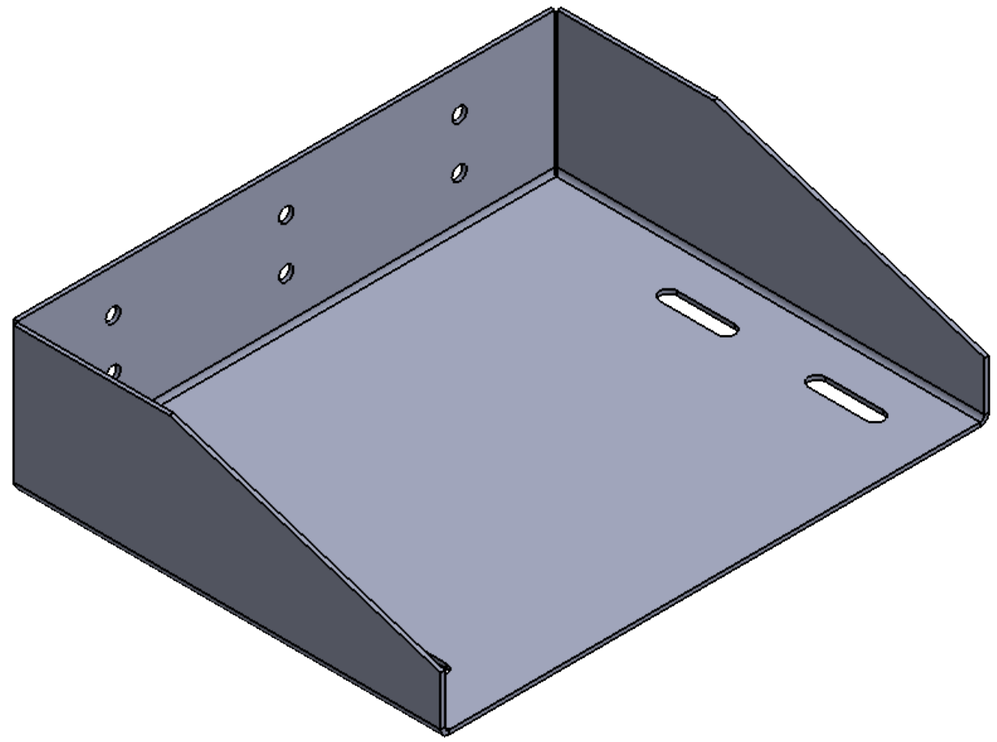


TITLE - RETRACTABLE ROOF				NIHVA TECHNOLOGIES PVT.LTD.PUNE
DWG NO - NTPL277-PM-001-00-000-01				Website - www.nihva.com
	NAME	SIGNATURE	DATE	PROJECT NO - NTPL277-PM
DRAWN	J.P		10-04-2025	PRODUCT - RETRACTABLE ROOF
CHK'D	S.W		10-04-2025	SITE LOCATION - AYODHYA
APPV'D	V.T.		10-04-2025	
if any queries contact - supportautomation@nihva.com				REVISION - QTY - 1
ALL DIMENSION ARE IN mm			A3	SCALE - SHEET 17 OF 24


ITEM NO.	PART NUMBER	DESCRIPTION	QTY.
1	C - CHANEL	70X30X575	22

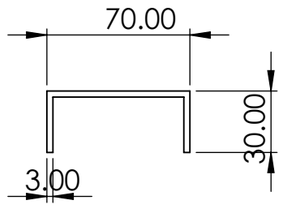

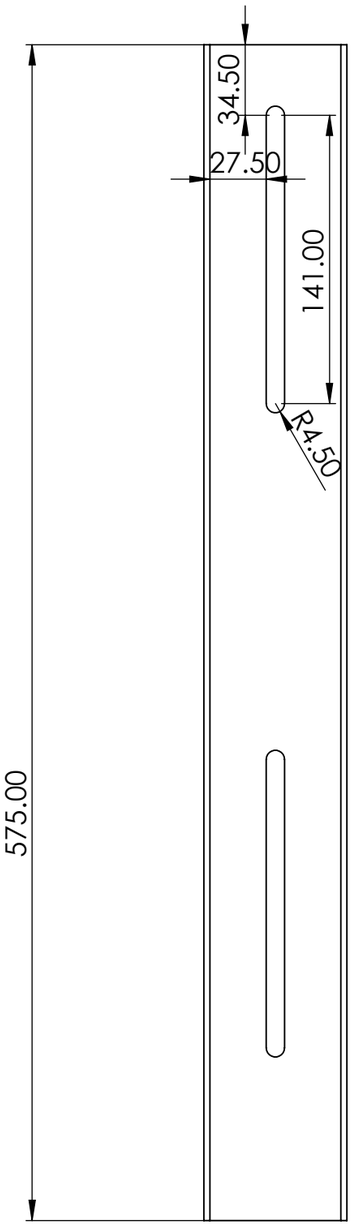

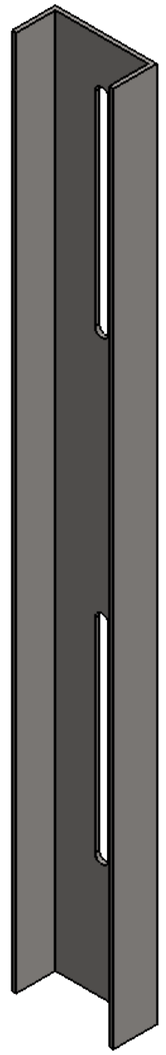


TITLE - RETRACTABLE ROOF				NIHVA TECHNOLOGIES PVT.LTD.PUNE
DWG NO - NTPL277-PM-001-00-000-02				Website - www.nihva.com
	NAME	SIGNATURE	DATE	PROJECT NO - NTPL277-PM
DRAWN	J.P		10-04-2025	PRODUCT - RETRACTABLE ROOF
CHK'D	S.W		10-04-2025	SITE LOCATION - AYODHYA
APPV'D	V.T.		10-04-2025	
if any queries contact - supportautomation@nihva.com				REVISION - QTY - 1
ALL DIMENSION ARE IN mm			A3	SCALE - SHEET 18 OF 24

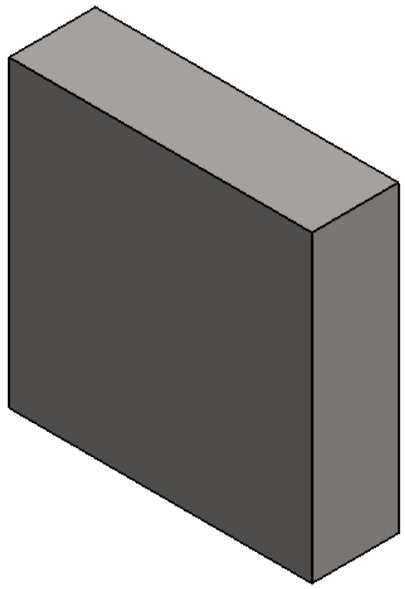


ITEM NO.	PART NUMBER	DESCRIPTION	QTY.
1	C- CHANEL JOINING PLATE	35X40X10MM THK	11




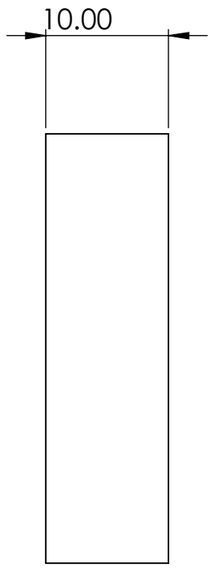


TITLE - RETRACTABLE ROOF				NIHVA TECHNOLOGIES PVT.LTD.PUNE
DWG NO - NTPL277-001-00-000-03				Website - www.nihva.com
	NAME	SIGNATURE	DATE	PROJECT NO - NTPL277-PM
DRAWN	J.P		10-04-2025	PRODUCT - RETRACTABLE ROOF
CHK'D	S.W		10-04-2025	SITE LOCATION - AYODHYA
APPV'D	V.T.		10-04-2025	
if any queries contact - supportautomation@nihva.com				REVISION - QTY - 1
ALL DIMENSION ARE IN mm		A3		SCALE - SHEET 19 OF 24

ITEM NO.	PART NUMBER	DESCRIPTION	QTY.
1	C- CHANEL MTG BASE PLATE	320X50X10MM THK	11

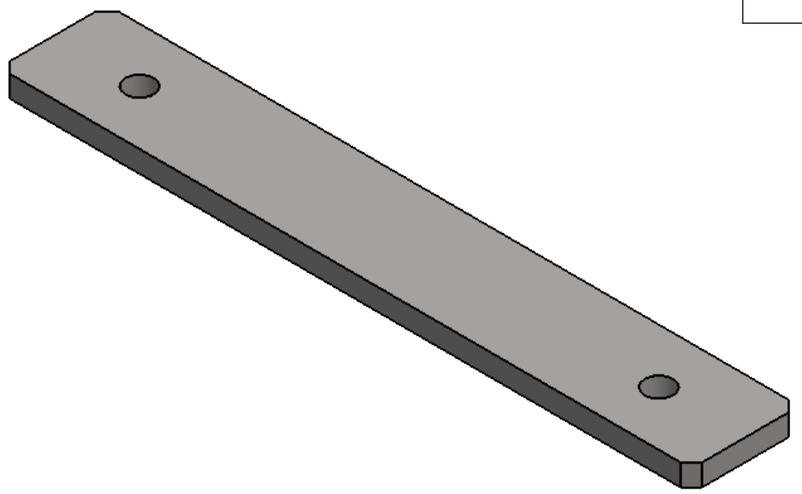


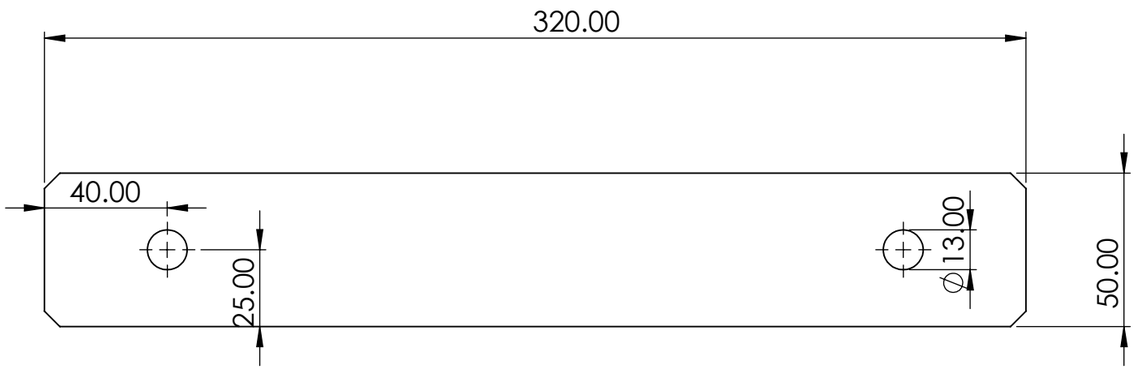


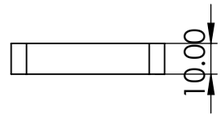


TITLE - RETRACTABLE ROOF				NIHVA TECHNOLOGIES PVT.LTD.PUNE
DWG NO - NTPL277-PM-001-00-000-04				Website - www.nihva.com
	NAME	SIGNATURE	DATE	PROJECT NO - NTPL277-PM
DRAWN	J.P		10-04-2025	PRODUCT - RETRACTABLE ROOF
CHK'D	S.W		10-04-2025	SITE LOCATION - AYODHYA
APPV'D	V.T.		10-04-2025	
if any queries contact - supportautomation@nihva.com				REVISION - QTY - 1
ALL DIMENSION ARE IN mm			A3	SCALE - SHEET 20 OF 24

ITEM NO.	PART NUMBER	DESCRIPTION	QTY.
1	BUSBAR FLASHER MTG L PLATE	70X142X2 MM THK	11

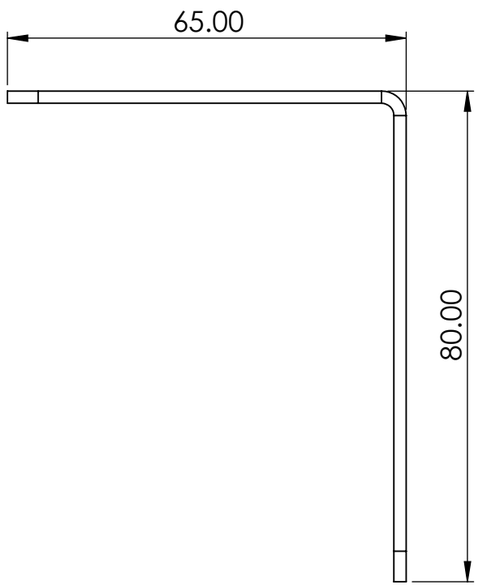

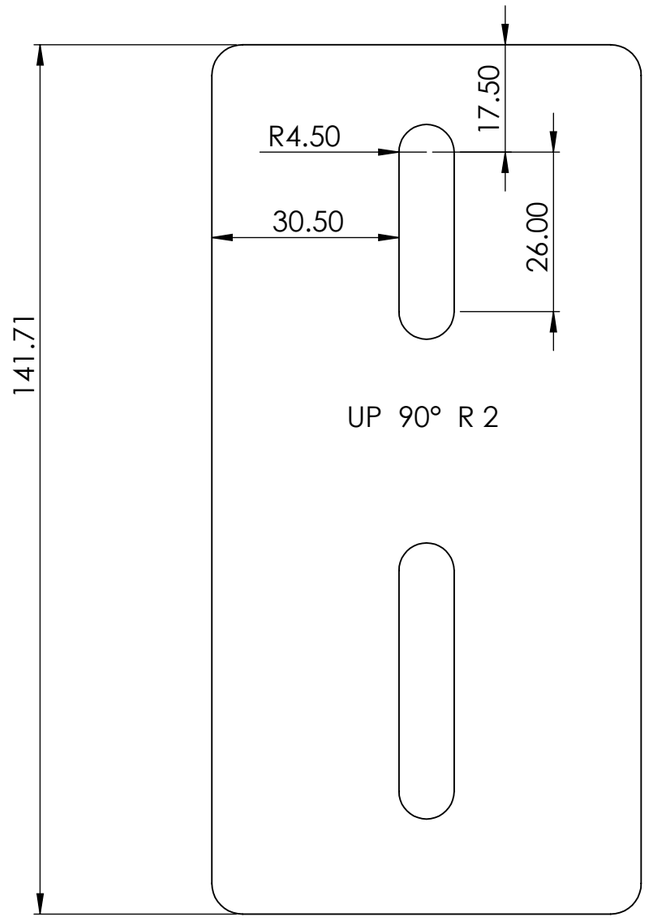


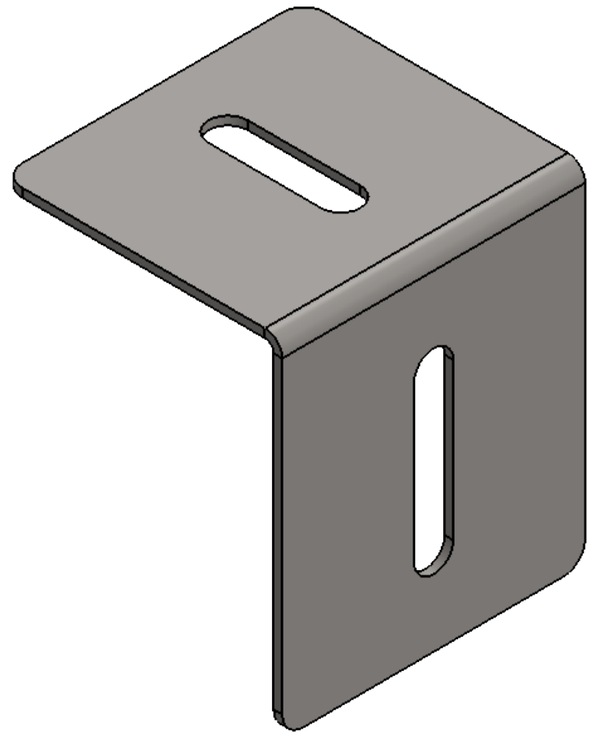

TITLE - RETRACTABLE ROOF				NIHVA TECHNOLOGIES PVT.LTD.PUNE
DWG NO - NTPL277-PM-001-00-000-05				Website - www.nihva.com
	NAME	SIGNATURE	DATE	PROJECT NO - NTPL277-PM
DRAWN	J.P		10-04-2025	PRODUCT - RETRACTABLE ROOF
CHK'D	S.W		10-04-2025	SITE LOCATION - AYODHYA
APPV'D	V.T.		10-04-2025	
if any queries contact - supportautomation@nihva.com				REVISION - QTY - 1
ALL DIMENSION ARE IN mm			A3	SCALE - SHEET 21 OF 24


ITEM NO.	PART NUMBER	DESCRIPTION	QTY.
1	2D DRAWING SALAVI MAM BUSBAR FLASHER	STD (LOOSE PART)	5


Thickness - 1 mm

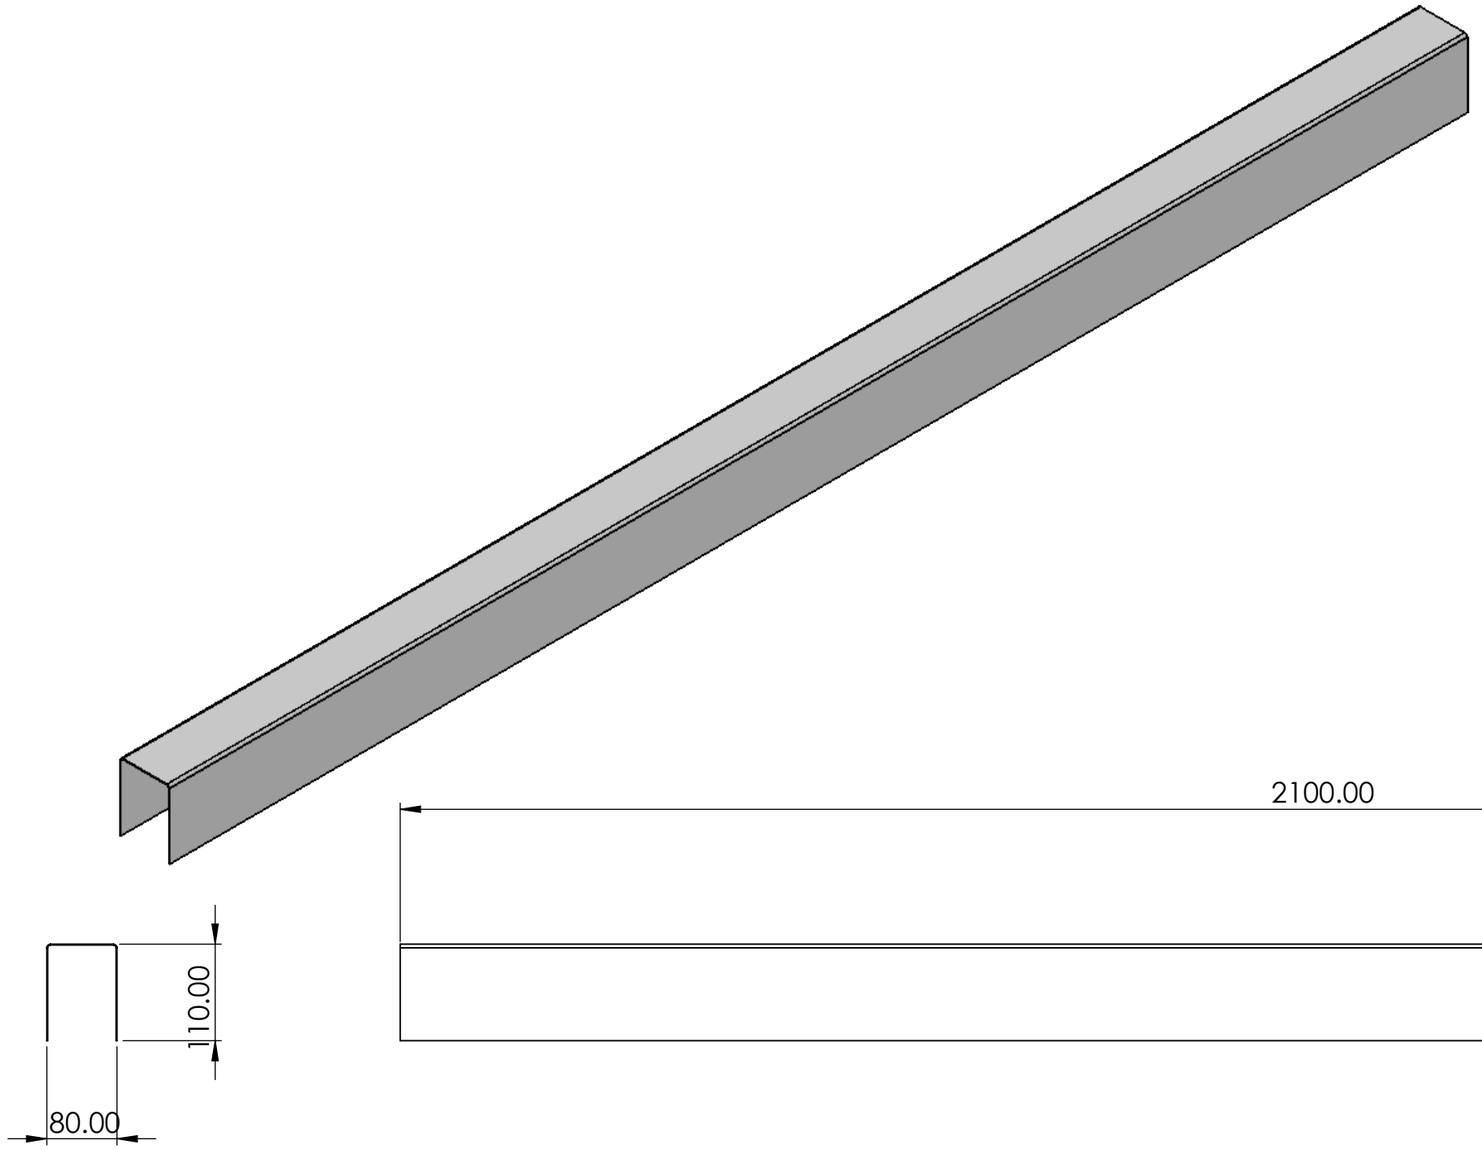

TITLE - RETRACTABLE ROOF				NIHVA TECHNOLOGIES PVT.LTD.PUNE Website - www.nihva.com
DWG NO - NTPL277-PM-001-00-000-06				
	NAME	SIGNATURE	DATE	PROJECT NO - NTPL277-PM
DRAWN	J.P		10-04-2025	PRODUCT - RETRACTABLE ROOF
CHK'D	S.W		10-04-2025	SITE LOCATION - AYODHYA
APPV'D	V.T.		10-04-2025	
if any queries contact - supportautomation@nihva.com				REVISION - QTY - 1
ALL DIMENSION ARE IN mm		A3		SCALE - SHEET 22 OF 24


ITEM NO.	PART NUMBER	DESCRIPTION	QTY.
1	2D DRAWING RACK	STD (M4 RACK, 30x8x1000 mm, ZINC COATED WITH SPACERS AND SCREWS.)	11

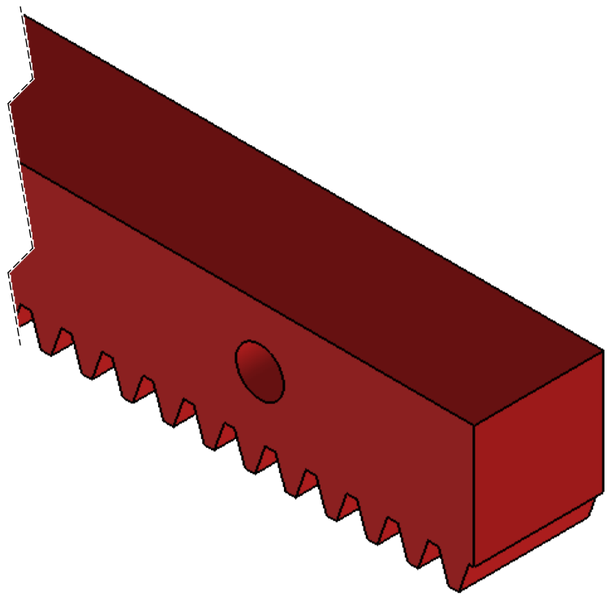


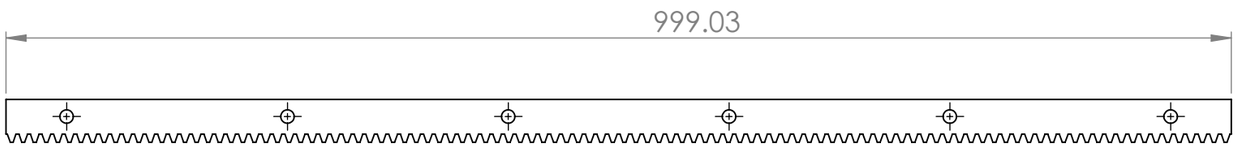


TITLE - RETRACTABLE ROOF				NIHVA TECHNOLOGIES PVT.LTD.PUNE
DWG NO - NTPL277-PM-001-00-000-06				Website - www.nihva.com
	NAME	SIGNATURE	DATE	PROJECT NO - NTPL277-PM
DRAWN	J.P		10-04-2025	PRODUCT - RETRACTABLE ROOF
CHK'D	S.W		10-04-2025	SITE LOCATION - AYODHYA
APPV'D	V.T.		10-04-2025	
if any queries contact - supportautomation@nihva.com				REVISION - QTY - 1
ALL DIMENSION ARE IN mm		A3		SCALE - SHEET 23 OF 24

ITEM NO.	PART NUMBER	DESCRIPTION	QTY.
1	GUIDE RAILS-T75-1B	STD (10060 mm)	6

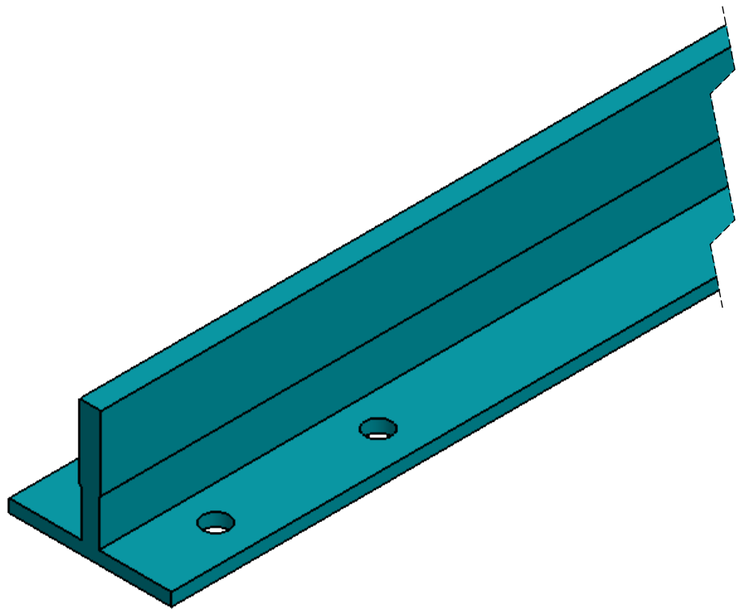

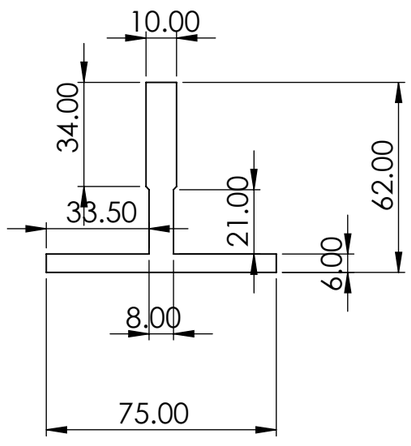

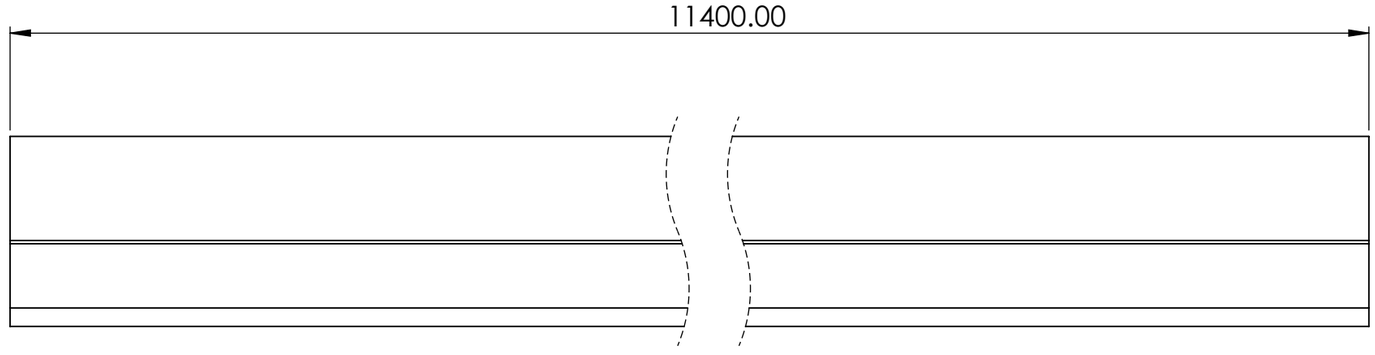

TITLE - RETRACTABLE ROOF				NIHVA TECHNOLOGIES PVT.LTD.PUNE Website - www.nihva.com
DWG NO - NTPL277-PM-001-00-000-07				
	NAME	SIGNATURE	DATE	PROJECT NO - NTPL277-PM
DRAWN	J.P		10-04-2025	PRODUCT - RETRACTABLE ROOF
CHK'D	S.W		10-04-2025	SITE LOCATION - AYODHYA
APPV'D	V.T.		10-04-2025	
if any queries contact - supportautomation@nihva.com				REVISION - QTY - 1
ALL DIMENSION ARE IN mm			A3	SCALE - SHEET 24 OF 24