
ASSA ABLOY

General Drawing RR3000 ISO

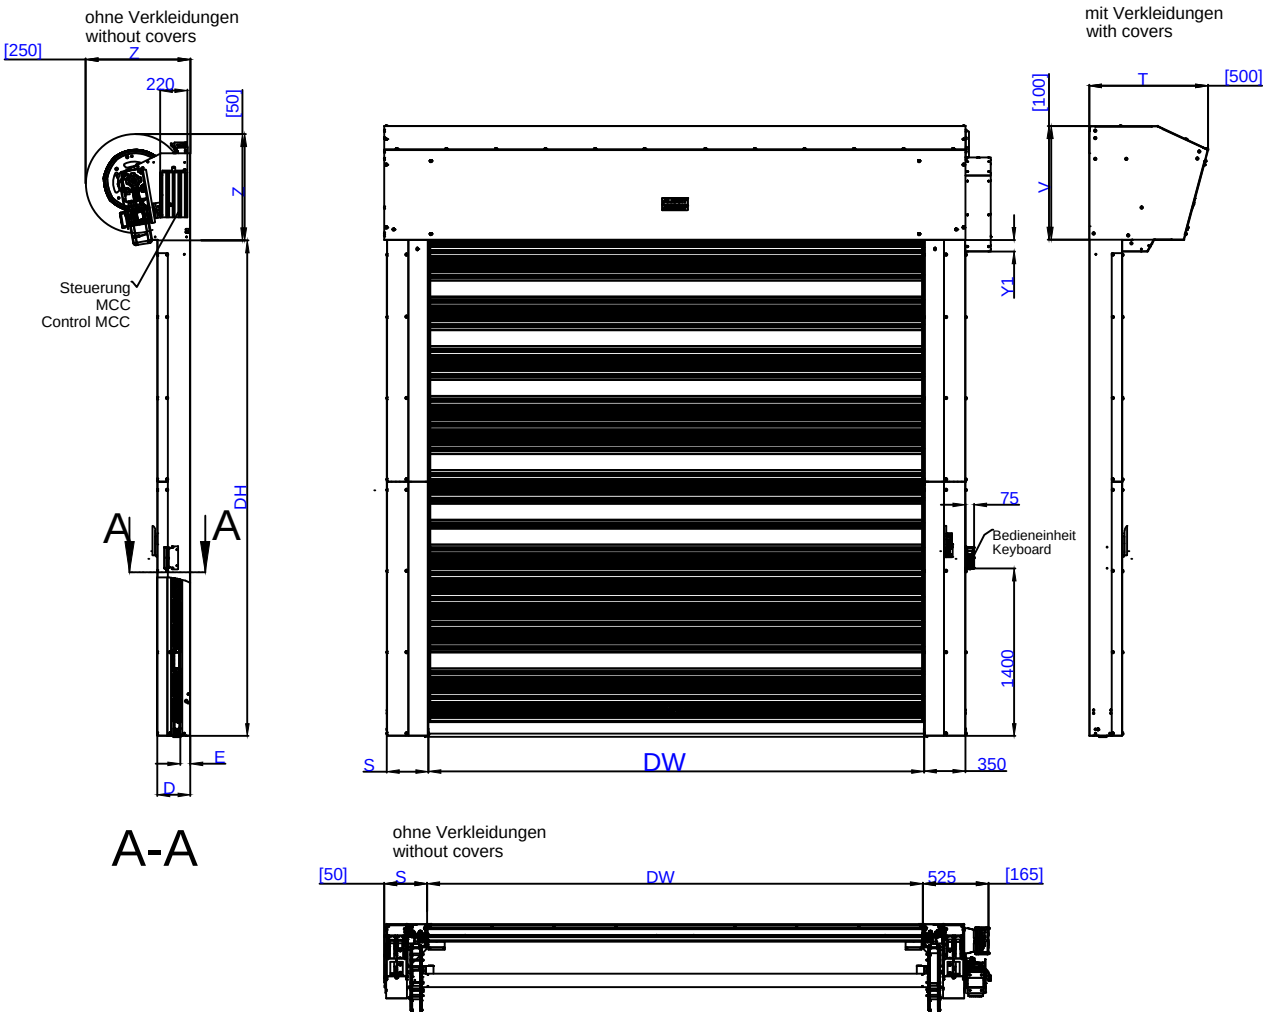

DW	DH	QUANTITY
2000	2500	1

Torausführung Door type	E	D	Z	S	V	T	Y1	Y2
A	84	267	880	350	920	960	105	330

This drawing & design is the property of NIHVA TECHNOLOGIES. Not to be sold or copied to any other concern.

TITLE

RR 3000 ISO
HSD

CLIENT APPROVAL

ALL DIMENSION ARE IN mm

NIHVA
NIHVA TECHNOLOGIES PVT. LTD.

NIHVA TECHNOLOGIES
PVT. LTD. PUNE
Tel : 020 66304033
Email:- info@nihva.com
Website:- www.nihva.com

	SIGN	DATE
DRAWN	OMKAR	14/08/17
CHECK	SHEKHAR	14/08/17
REV.		
APPRD.	SHEKHAR	14/08/17
MFG		
Ref. No.		

CLIENT - MASQATI DAIRY

PROJECT -

SITE - HYDERABAD

DWG. NO. - NIHVA/17-18/0154

SCALE: NTS | WT: | SHEET: 01 OF 01

If any queries contact : projects@nihva.com