
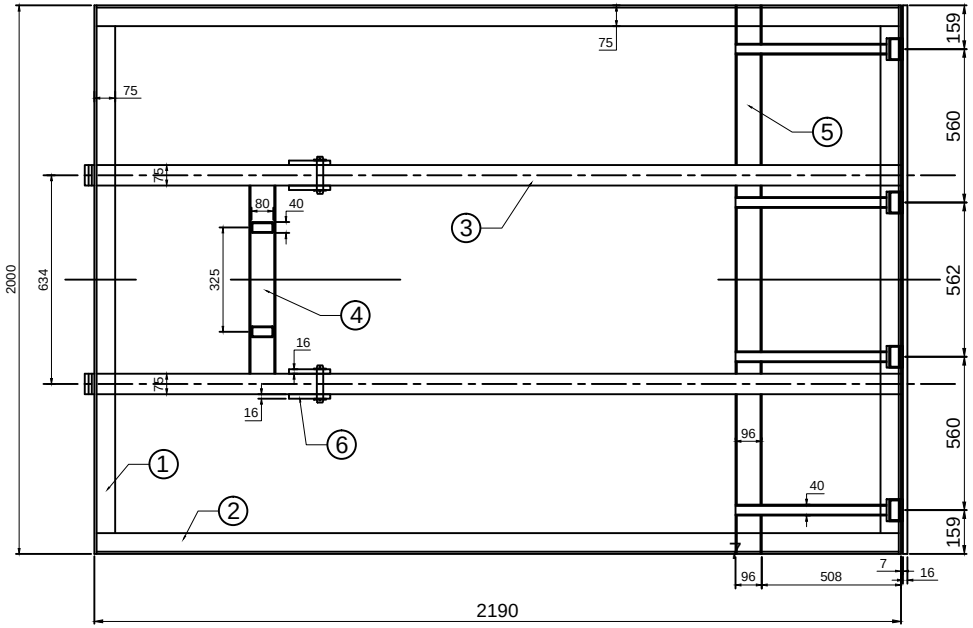


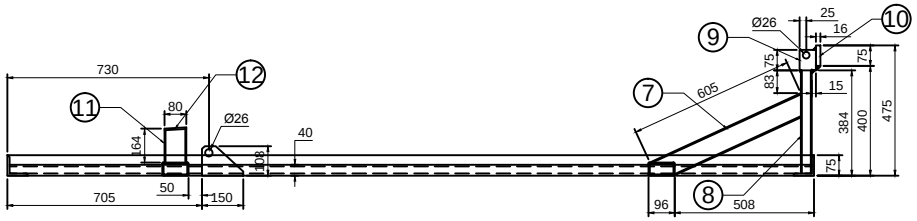

NOTE:~ MTL : MS

PART NO.	PART NAME	DESCRIPTION	QTY
1.	ISA	75 X 75 X 8 X 2000L	2 NOS
2.	ISA	75 X 75 X 8 X 2174L (NOTCH)	2 NOS
3.	ISMC	75 X 70 X 2174L (NOTCH)	2 NOS
4.	R.TUBE	96 X 48 X 4.8 THK X 558L	2 NOS
5.	R.TUBE	96 X 48 X 4.8 THK X 637L	2 NOS
6.	PROFILE	108 X 16 X 150L	4 NOS
7.	FLAT	80 X 40 X 4 THK X 605L (NOTCH)	4 NOS
8.	R.TUBE	80 X 40 X 4 THK X 375L (NOTCH)	4 NOS
9.	SOLID	75 X 60 X 80L	4 NOS
10.	FLAT	75 X 16 X 2025L	1 NO
11.	R.TUBE	80 X 40 X 4 THK X 165L	2 NOS
12.	FLAT	40 X 5 X 80L	2 NOS
13.			
14.			
15.			
16.			

REV NO	DATE	DRAWN	DESCRIPTION
01	21.09.2018	P.A	POINT 02,03 &10 LENGTH CHANGED.

TITLE

BASE FRAME ASSLY

	NAME	SIGN	DATE
DRAWN	PRADEEP		05.09.2018
CHECK	PRADEEP		05.09.2018
APPRD.	PRADEEP		05.09.2018

If any queries contact : design@nihva.com

ALL DIMENSION ARE IN mm

NIHVA TECHNOLOGIES PVT. LTD.

NIHVA TECHNOLOGIES PVT. LTD. PUNE
Tel : 020 66304033
Email:- info@nihva.com
Website:- www.nihva.com

CLIENT -

PROJECT - DLSD1010

SITE LOCATION -

DWG. NO. : NIHVA/18-19/MFG/DLSD1010/004/R01

SCALE: NTS | WT: | REV- 01