




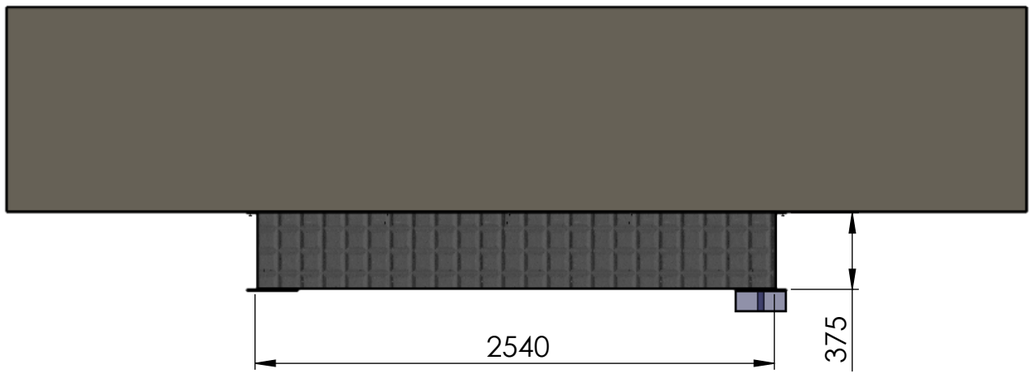


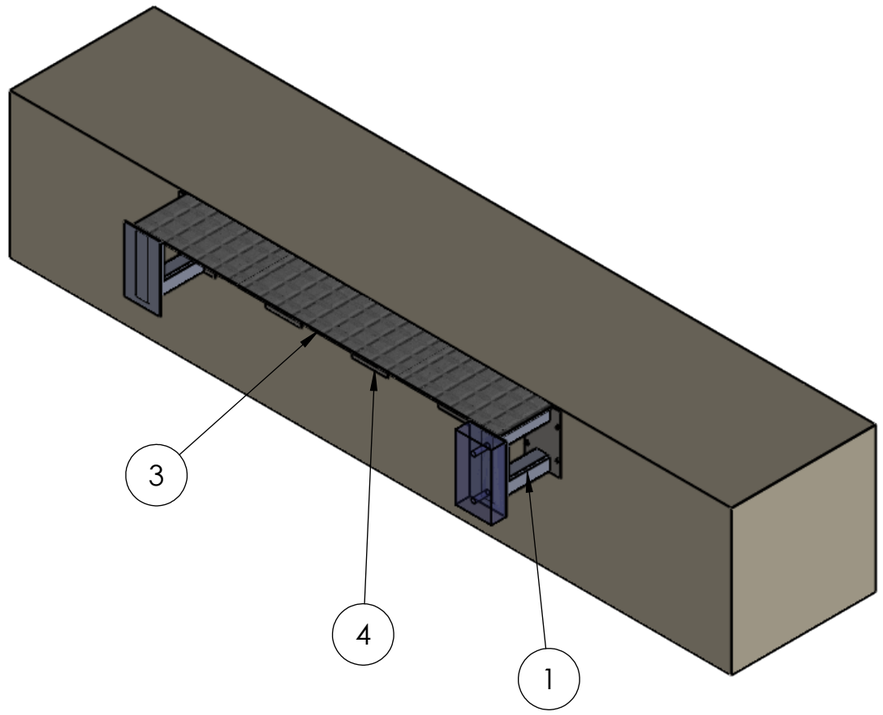



ITEM NO.	PART NUMBER	QTY.
1	DOCK BUMPER(450X250X100) MM	2
2	SHS 100X100X2	2
3	CHEQUERED PLATE (2540X375X8 MM)	1
4	CHEQUERED PLATE SUPPORT	3

TITLE - PROLOGIS				NIHVA TECHNOLOGIES PVT.LTD.PUNE Website - www.nihva.com
DWG NO - NTPL-324-01			QTY - 1	
	NAME	SIGNATURE	DATE	PROJECT NO - NTPL-324
DRAWN	B.S.		10.03.2026	PRODUCT - LOADING UNLOADING FIX PLATFORM
CHK'D	V.T.		10.03.2026	SITE LOCATION - KARAPANAHALLI , KARNATAKA
APPV'D	V.T.		10..03.2026	
if any queries contact - Design2@nihva.com				REVISION -
ALL DIMENSION ARE IN mm			A3	SCALE - SHEET 1 OF 5

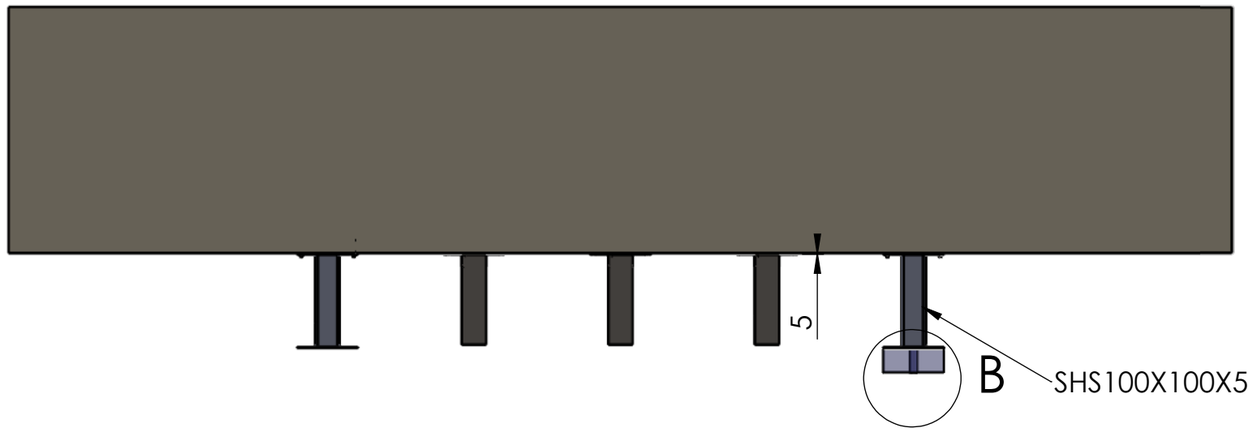

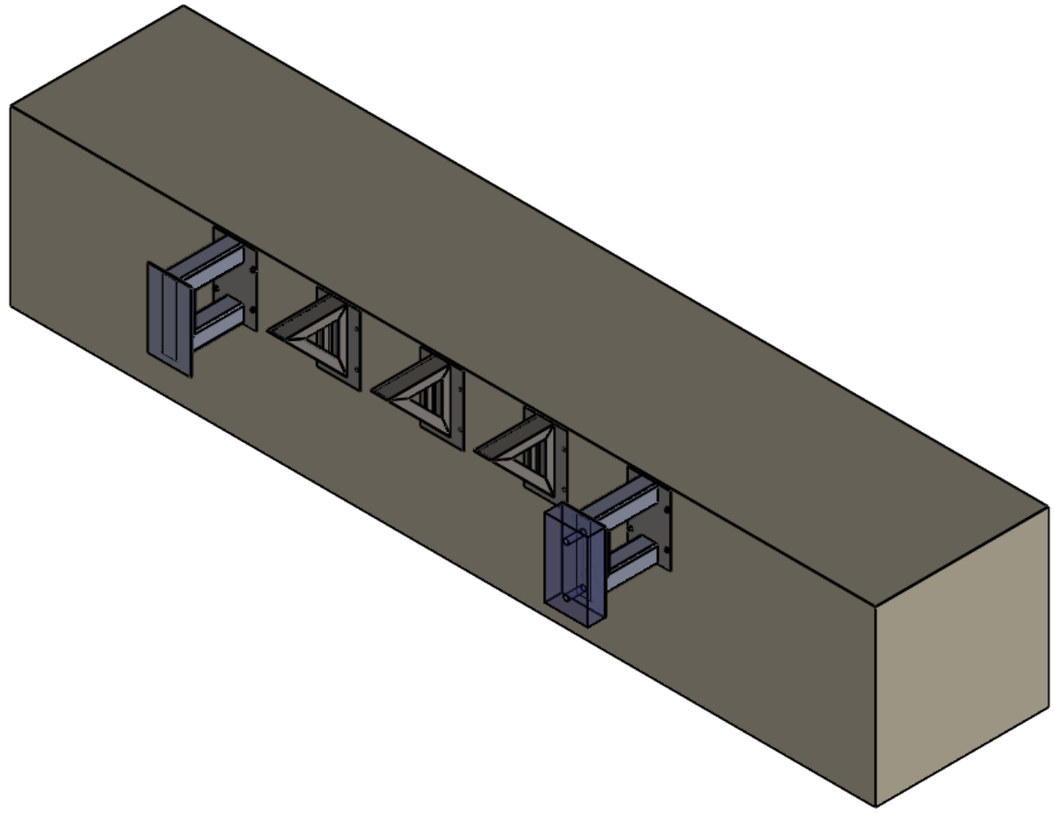

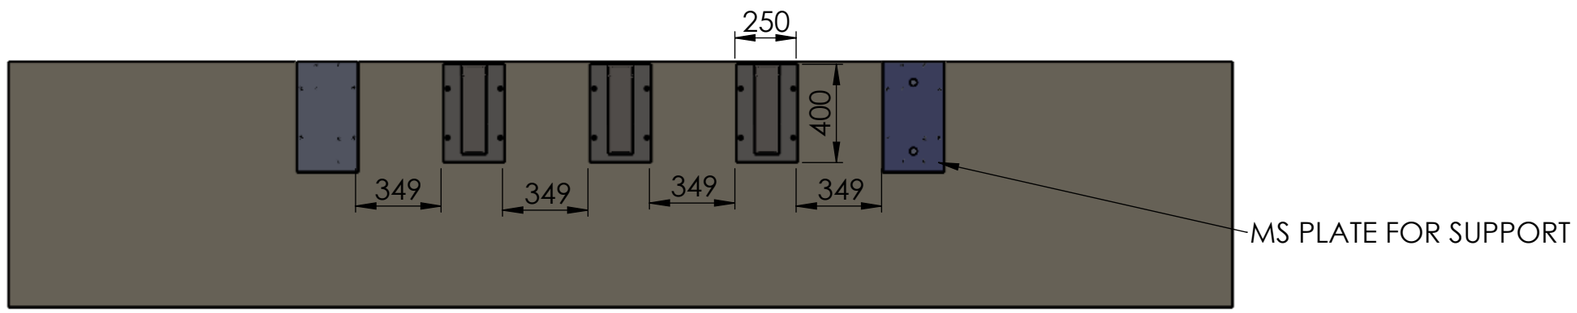


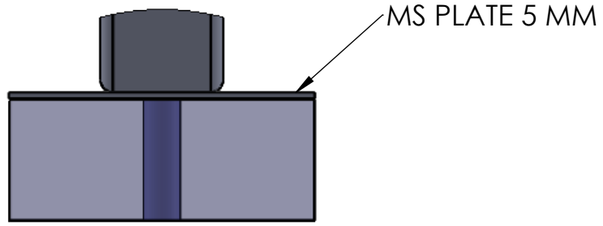

DETAIL B


SCALE 1 : 5


TITLE - PROLOGIS				NIHVA TECHNOLOGIES PVT.LTD.PUNE Website - www.nihva.com
DWG NO - NTPL-321-01			QTY - 1	
	NAME	SIGNATURE	DATE	PROJECT NO - NTPL-324
DRAWN	B.S.		10.03.2026	PRODUCT - LOADING UNLOADING FIX PLATFORM
CHK'D	V.T.		10.03.2026	SITE LOCATION - KARAPANAHALLI , KARNATAKA
APPV'D	V.T.		10.03.2026	
if any queries contact - Design2@nihva.com				REVISION -
ALL DIMENSION ARE IN mm			A3	SCALE - SHEET 2 OF 5

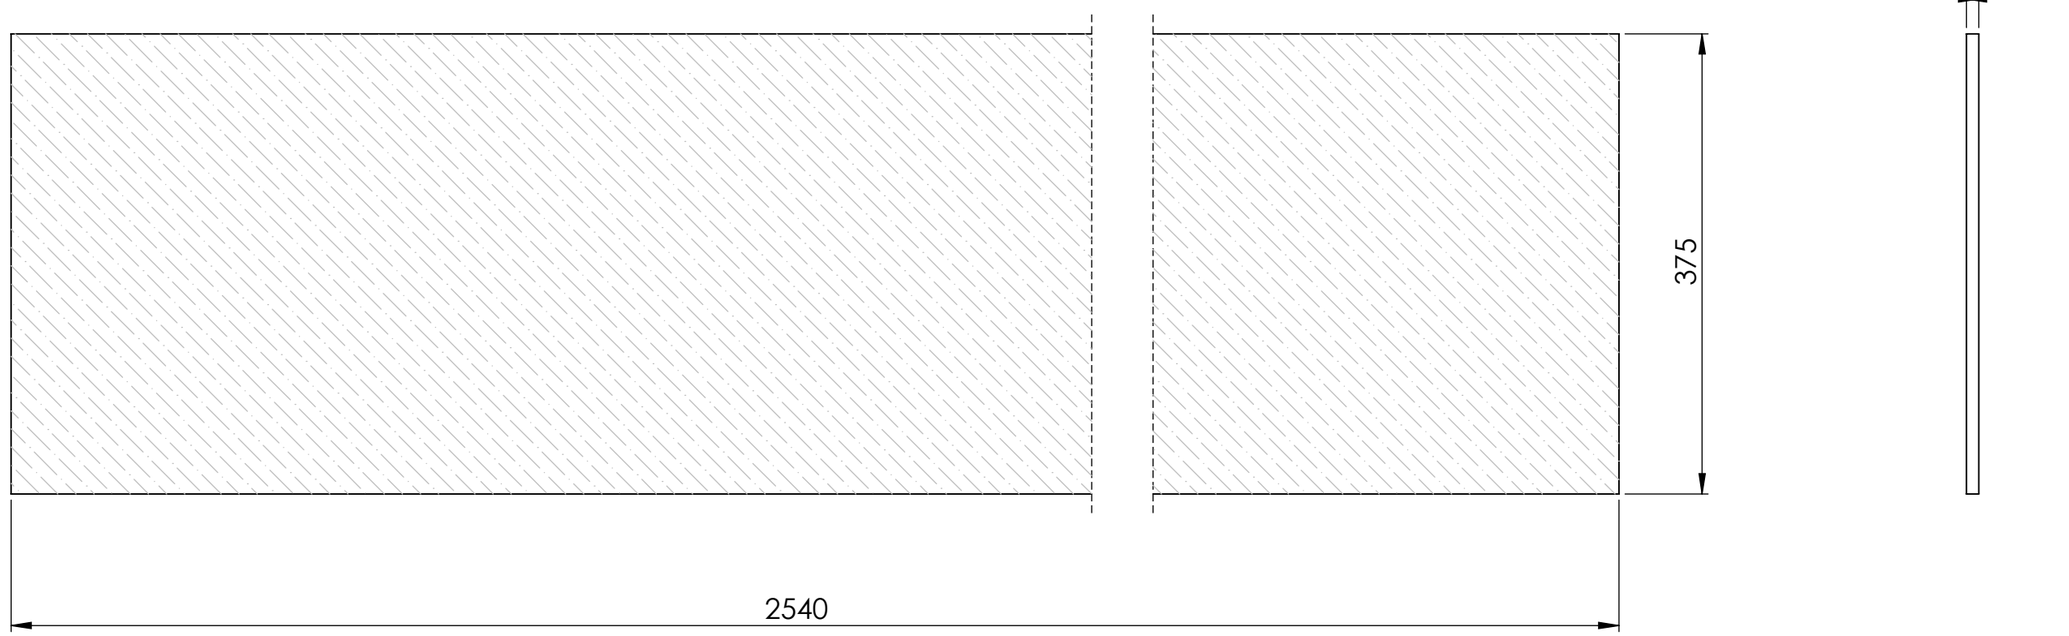



CHEQUERED PLATE QTY - 1 NOS

TITLE - PROLOGIS				NIHVA TECHNOLOGIES PVT.LTD.PUNE Website - www.nihva.com
DWG NO - NTPL-324-01-001			QTY - 1	
	NAME	SIGNATURE	DATE	PROJECT NO - NTPL-324
DRAWN	B.S.		10.03.2026	PRODUCT - LOADING UNLOADING FIX PLATFORM
CHK'D	V.T.		10.03.2026	SITE LOCATION - KARAPANAHALLI, KARNATAKA
APPV'D	V.T.		10.03.2026	
if any queries contact - supportautomation@nihva.com				REVISION -
ALL DIMENSION ARE IN mm			A3	SCALE - SHEET 3 OF 5

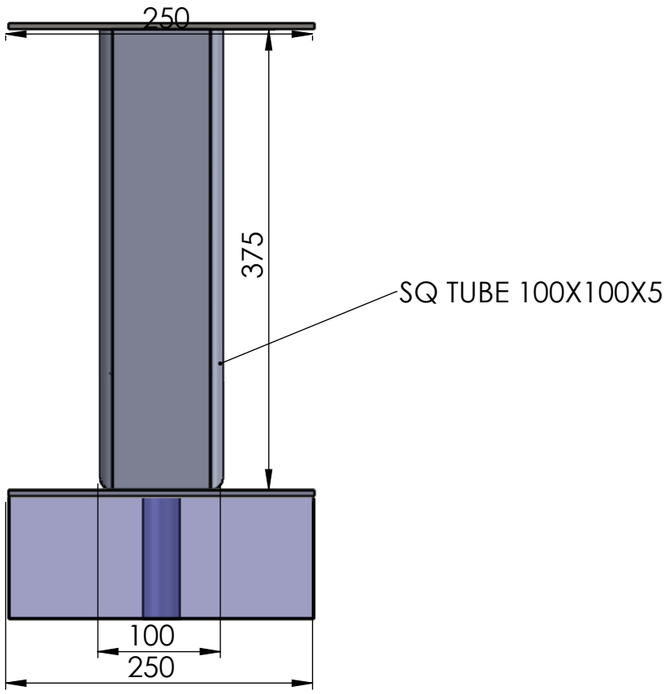

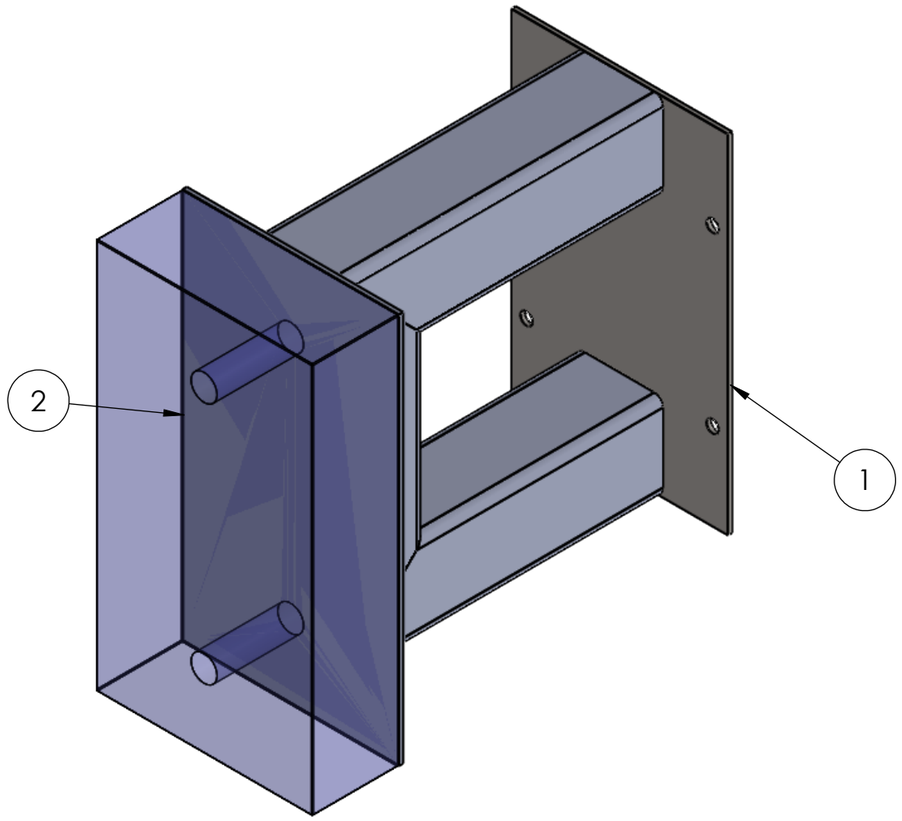

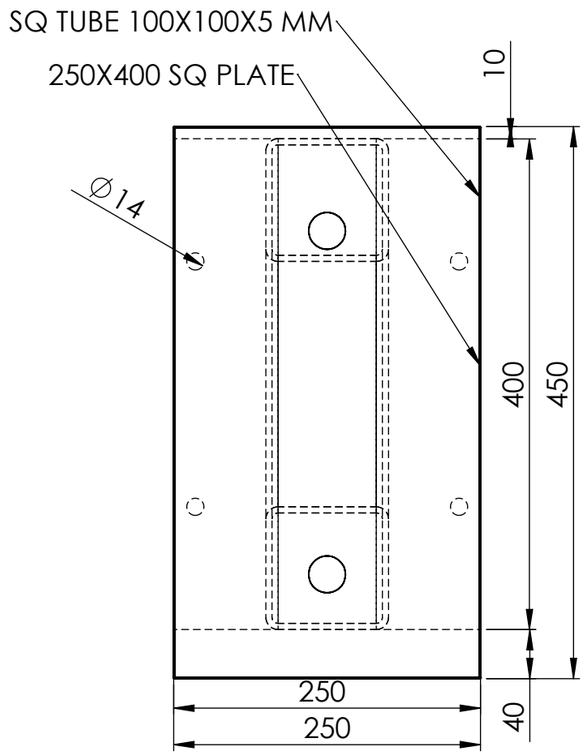


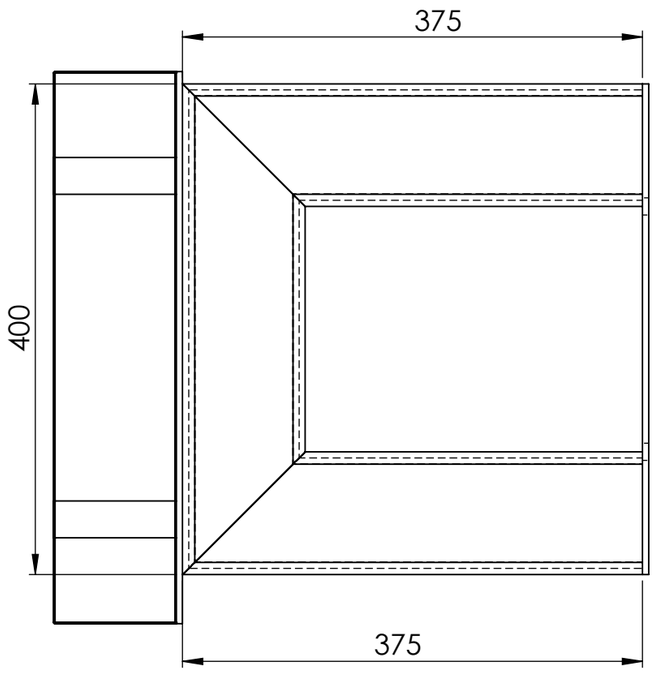



ITEM NO.	PART NUMBER	DESCRIPTION	QTY.
1	SHS 100X100X2	5MM(T)	1
2	MS PLATE	5 MM(T)	1
3	SHS 100	SQ TUBE 100X100X5MM	1
4	DOCK BUMPER	450X250X100	1


QTY - 2 NOS

TITLE - PROLOGIS				NIHVA TECHNOLOGIES PVT.LTD.PUNE
DWG NO - NTPL-324-01-002			QTY - 2	Website - www.nihva.com
	NAME	SIGNATURE	DATE	PROJECT NO - NTPL-324
DRAWN	B.S.		10.03.2026	PRODUCT - LOADING UNLOADING FIX PLATFORM
CHK'D	V.T.		10.03.2026	SITE LOCATION - KARAPANAHALLI , KARNATAKA.
APPV'D	V.T.		10.03.2026	
if any queries contact - Design2@nihva.com				REVISION -
ALL DIMENSION ARE IN mm		A3		SCALE - SHEET 4 OF 5

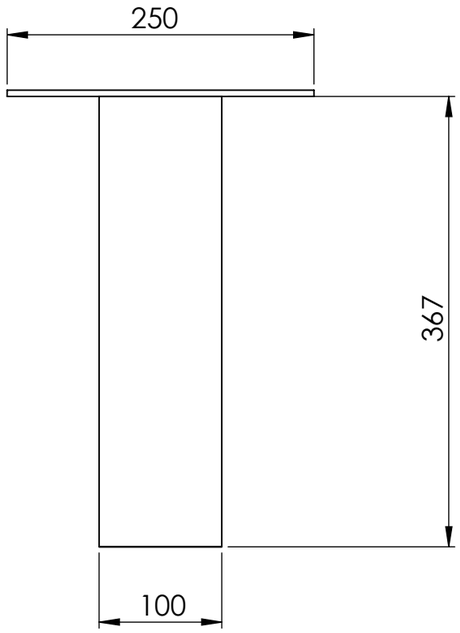

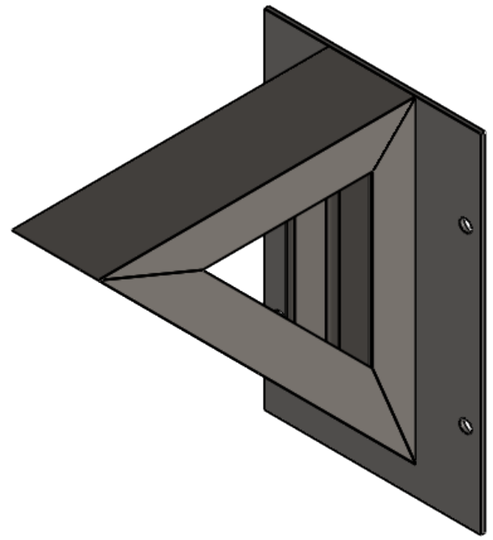

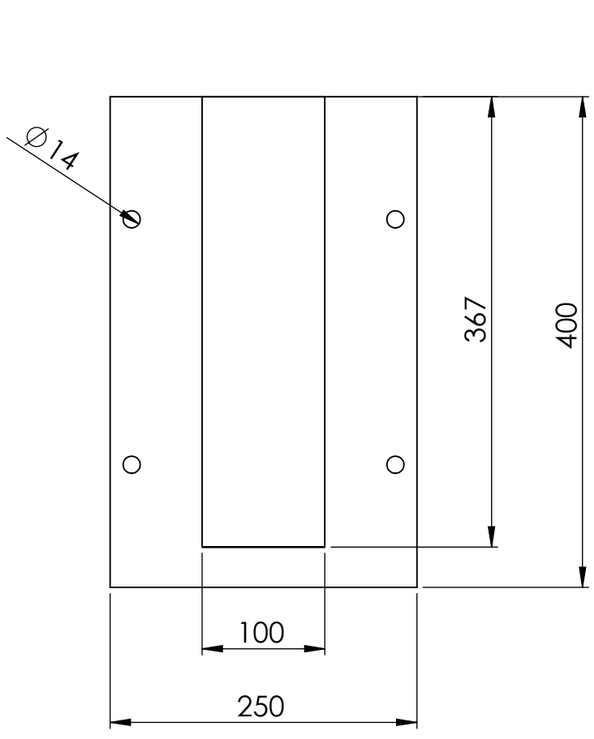

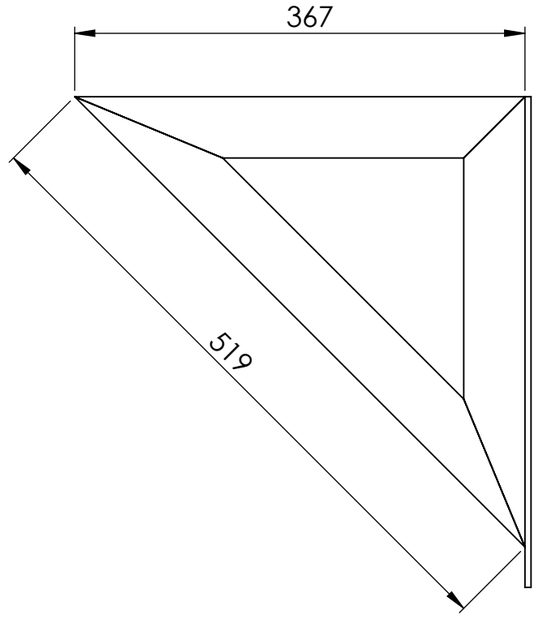

QTY -3 NOS FOR ONE SET

TITLE -PROLOGIS				NIHVA TECHNOLOGIES PVT.LTD.PUNE Website - www.nihva.com
DWG NO - NTPL-324-01-003			QTY - 3	
	NAME	SIGNATURE	DATE	PROJECT NO - NTPL-324
DRAWN	B.S.		10.03.2026	PRODUCT - LOADING UNLOADING FIX PLATFORM
CHK'D	V.T.		10.03.2026	SITE LOCATION -KARAPANAHALLI,KARNATAKA.
APPV'D	V.T.		10.03.2026	
if any queries contact - Design2@nihva.com				REVISION -
ALL DIMENSION ARE IN mm			A3	SCALE - SHEET 5 OF 5