


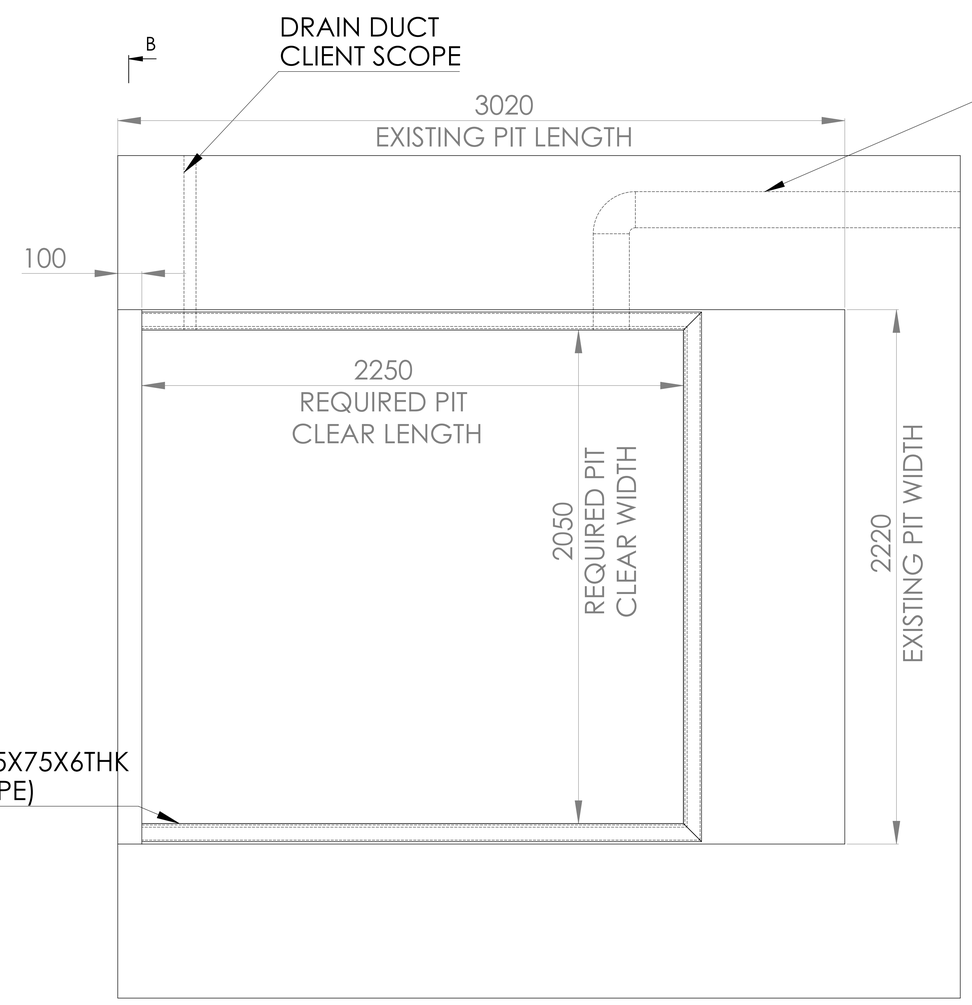


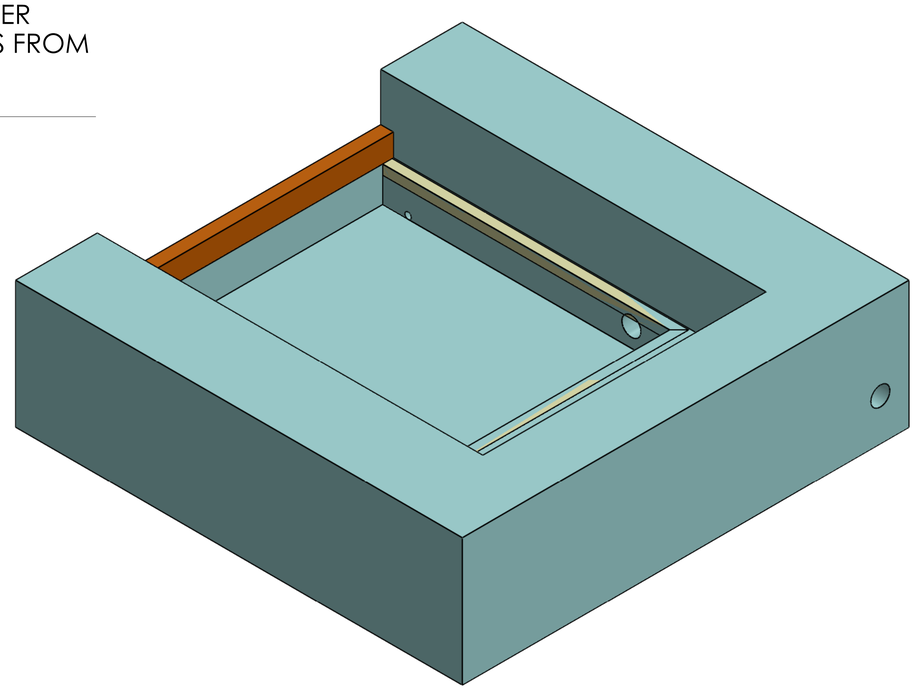

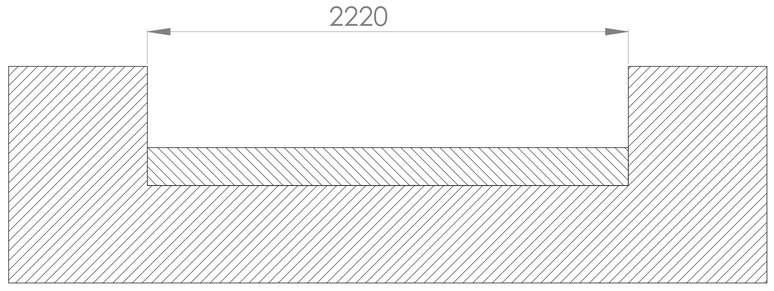

SECTION B-B
SCALE 1 : 10

PIT DRAWING
(CLIENT SCOPE)

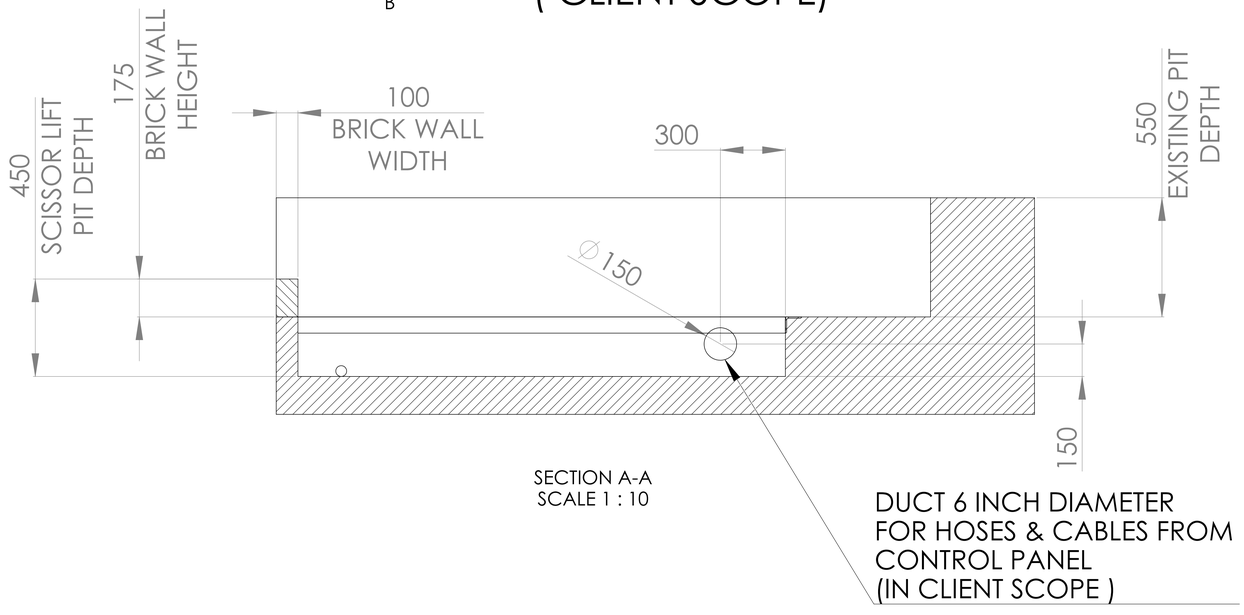

SECTION A-A
SCALE 1 : 10

NOTES-
1. PIT FOR SCISSOR LIFT HAS TO BE DIAGONALLY WITHIN 3-5MM.
2. BASE OF PIT HAS TO BE IN WATER LEVEL & RIGHT ANGLE TO THE VERTICAL SIDE WALLS .
3. PROPER ARRANGEMENT FOR ROUTING HOSES & CABLES HAVE TO BE MADE DEPENDING ON SITE CONDITIONS & POSITION OF POWER PACK .(IN CLIENT SCOPE).
4. COVERING REQUIRED FOR HOSES , PANEL , CABLES & ALL RELATED CIVIL WORK IS IN CLIENT SCOPE .
5. PIT , DUCT & ALL CIVIL WORK IS IN CLIENT SCOPE .
6. PIT SHOULD BE CAPABLE TO TAKE ATLEAST 6000KG OF LOAD.

NIHVA
We Make Possible

UNLESS OTHERWISE SPECIFIED: DIMENSIONS ARE IN MILLIMETERS
SURFACE FINISH:
TOLERANCES:
LINEAR:
ANGULAR:

FINISH:

DEBURR AND BREAK SHARP EDGES

DO NOT SCALE DRAWING | REVISION

DWG NO - NIHVA/20-21/0095/R02

	NAME	SIGNATURE	DATE
DRAWN	SIDDHESHWAR		1.1.2021
CHK'D			
APPV'D			
MFG			
Q.A			

MATERIAL:

WEIGHT:

TITLE: ADVIK HI-TECH SCISSOR LIFT

DWG NO: PIT DRAWING

A0

SCALE:1:20

SHEET 2 OF 2