

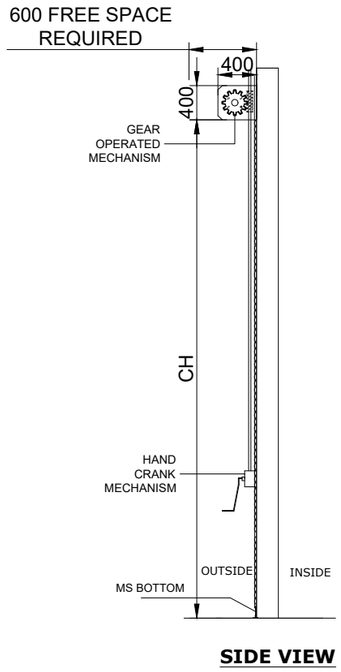



SIDE VIEW

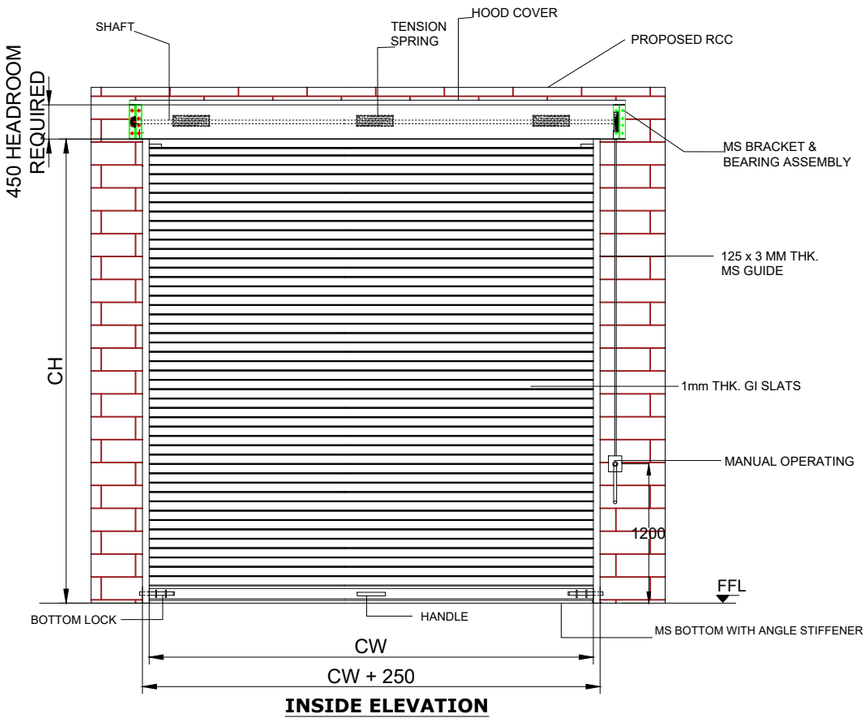


INSIDE ELEVATION

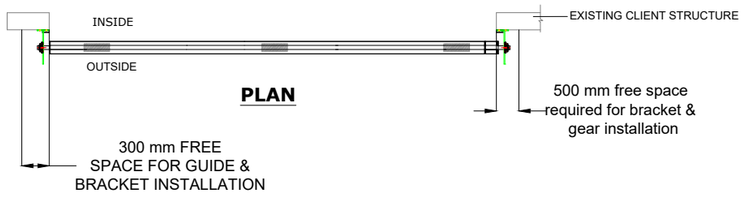

PLAN

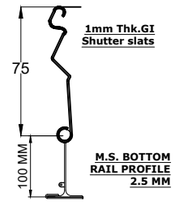

M.S. BOTTOM RAIL PROFILE 2.5MM

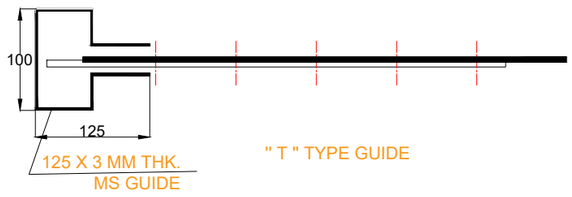

" T " TYPE GUIDE

NOTE-
1. ALL CIVIL WORK WILL BE CLIENT'S SCOPE.
2.IF STRUCTURE REQUIRED FOR SHUTTER IS IN CLIENT'S SCOPE.

TECHNICAL SPECIFICATION:-

SR.	SPECIFICATION	DETAILS
1.	DESCRIPTION & DRIVE	GEAR OPERATED SHUTTER
2.	LOCATION AREA	OUTSIDE AREA
3.	MOUNTING SURFACE	SIDE BRACKETS: ON CONCRETE
4.	SLAT	75 MM WIDE - 1 MM THICK GI
5.	BOTTOM PROFILE	M.S. PLATE 100X2.5 MM THICK WITH ANGLE STIFFNER
6.	GUIDE PROFILE	M.S."T" SHAPE -100X125X3 MM THK .
7.	HOOD COVER & MOTOR COVER	MADE OF GI SHEET THICKNESS 0.9 MM.
8.	MATERIAL FINISH	SYNTHETIC ENAMEL PAINT

SR NO	(CW) CLEAR WIDTH	(CH) CLEAR HEIGHT	QUANTITY
1	3962	4113	01 NOS
2	3922	4140	01 NOS
3	3995	4088	01 NOS
4	4020	4102	01 NOS
5	4000	4120	01 NOS
6	3964	4059	01 NOS
7	3990	4110	01 NOS

This drawing & design is the property of NIHVA TECHNOLOGIES. Not to be sold or copied to any other concern.

TITLE
GEAR OPERATED ROLLING SHUTTER

	NAME	SIGN	DATE
DRAWN	B.S.		06.10.2025
CHECK	V.T.		06.10.2025
APPRD.	V.T.		06.10.2025

If any queries contact : design@nihva.com

ALL DIMENSION ARE IN mm

NIHVA
NIHVA TECHNOLOGIES PVT. LTD.
Website:- www.nihva.com
NIHVA TECHNOLOGIES PVT. LTD. PUNE
Tel : 020 66304033
Email:- info@nihva.com

CLIENT - VTP
PROJECT -
SITE LOCATION -
DWG. NO. : NIHVA/21-22/VDR/020 | REV- R00
SCALE: NTS | WT: | SHEET: 01 OF 01