

DRAWING




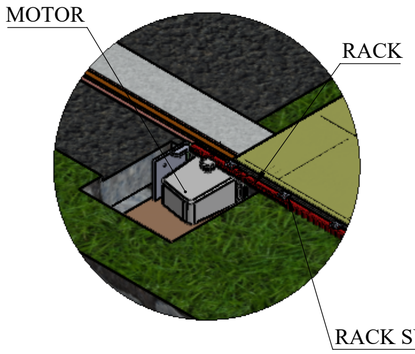


DETAIL A
SCALE 1 : 20

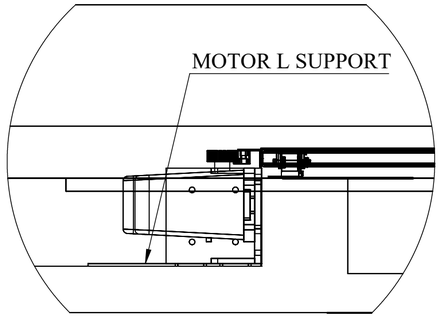

DETAIL B
SCALE 1 : 10

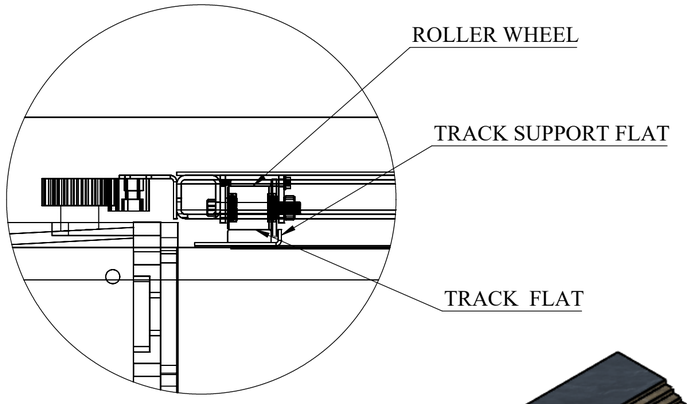

DETAIL C
SCALE 1 : 4

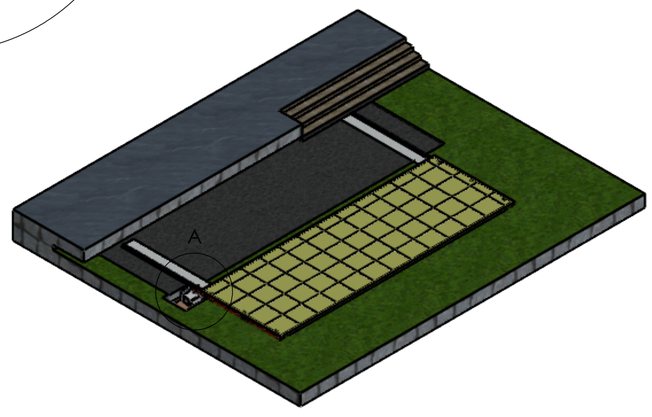





REV DESCRIPTION	DATE	REV NO
	29-07-2025	REV 00
1.		

NOTE :

Keep track clean before the panel movement.

SPECIAL INSTRUCTION'S :

TITLE - SWIMMING POOL ENCLOSER			NIHVA TECHNOLOGIES PVT.LTD.PUNE Website - www.nihva.com
DWG NO - NTPL-000-PM-001-00-00-00			
	NAME	SIGNATURE	DATE
DRAWN	V.W.		29-07-2025
CHK'D	P.M.		30-07-2025
APPV'D	V.T.		30-07-2025
If any queries contact - design.nihva@gmail.com			
ALL DIMENSION ARE IN mm			A2

PRODUCT - SWIMMING POOL DECK	
PROJECT NO - NTPL-000-PM	REVISION - 00
SITE LOCATION -	WEIGHT -
MATRIAL -	QTY - 1
PROJECTION METHOD:	SCALE :
	SHEET 1 OF 2