
LOCATION - MEDICAL AREA 02(MAIN HOSPITAL)

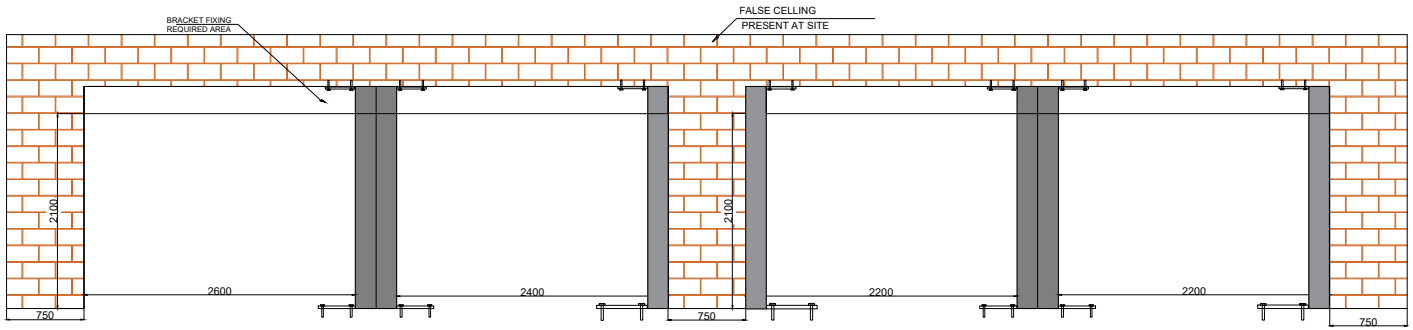

SHUTTER SIZES :-

SR.	CLEAR WIDTH	CLEAR HEIGHT	QTY.
01	2200 mm	2100 mm	02
02	2600 mm	2100 mm	01
03	2400 mm	2100 mm	01

NOTE :-

1. All DIMENSIONS ARE IN MM.
2. REQUIRED STEEL STRUCTURE IN CLIENT SCOPE.
3. HIGH LEX BOARD / INTERIOR SHEET/ PUFF PANEL REMOVER OR CUTTING IN CLIENT SCOPE

This drawing & designing is the property of NIHVA TECHNOLOGIES. Not to be sold or copied to any other concern.

TITLE :- MOTORISED ROLLING SHUTTER			NIHVA TECHNOLOGIES PVT. LTD. PUNE Tel : 020 66304033 Email:- info@nihva.com Website :- www.Nihva.com
	NAME	DATE	CLIENT - KLE Hospital
DRAWN	B.S.	04/02/2026	PROJECT - MOTORISED ROLLING SHUTTER
CHECK & APPROVAL	V.T.	04/02/2026	FORMAT NO - NIHVA-DD-F-03
			DWG. NO. : NIHVA/24-25/MP/1308001 REV-00
			SCALE: NTS WT: SHEET: 01 OF 01
ALL DIMENSION ARE IN mm			If any queries contact : design@nihva.com