

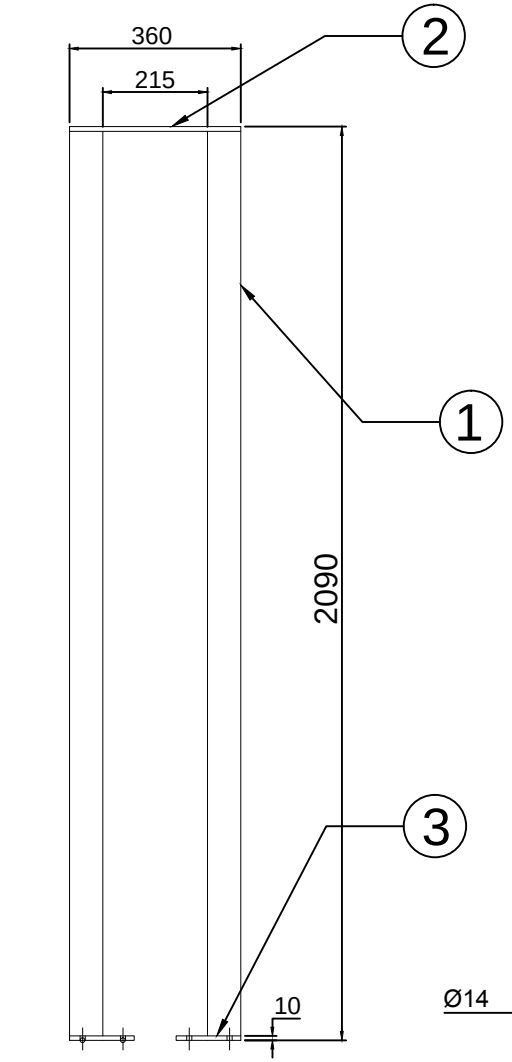


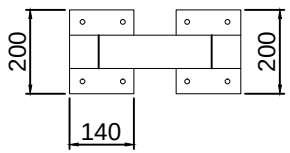


POST

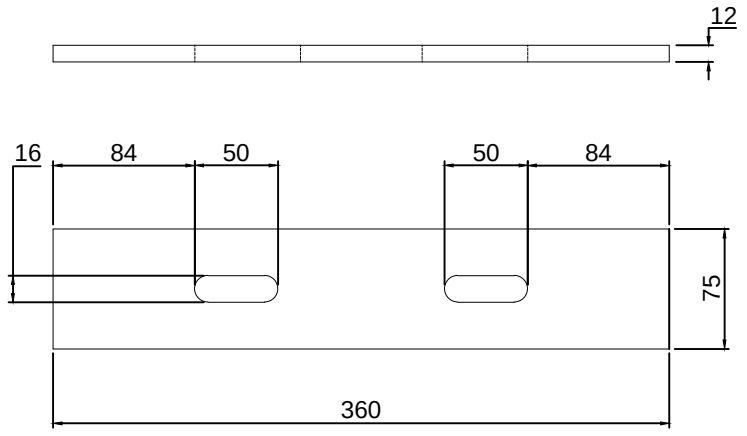

2 TOP PLATE

SR.NO	DESCRIPTION	SPECIFICATION	QTY	WEIGHT
5	NYLON WHEEL	Ø50 X 75L WITH M14 STUD	8 NOS	
4	ANCHOR BOLT	M12 X 150L	32 NOS	
3	PROFILE	140 X 12 X 200L	8 NOS	
2	PROFILE	75 X 12 X 360L	4 NOS	
1	SQ. TUBE	72 X 72 X 3.2 THK X 2065L	8 NOS	

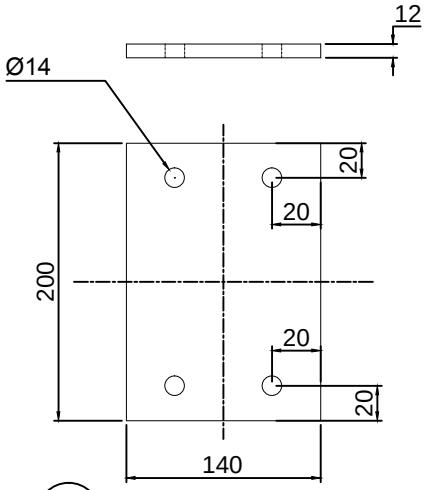

3 BASE PLATE

This drawing & designing is the property of NIHVA TECHNOLOGIES. Not to be sold or copied to any other concern.

TITLE: SLIDING GATE POST DRAWING

	NAME	SIGN	DATE
DRAWN	P.V.A		26.07.19
CHECK	V.M.T		26.07.19
APPROVAL			

If any queries contact : design@nihva.com

ALL DIMENSION ARE IN mm

NIHVA TECHNOLOGIES PVT. LTD.
NIHVA TECHNOLOGIES PVT. LTD. PUNE
Tel : 020 66304033
Website:- www.nihva.com
Email:- info@nihva.com

CLIENT -

PROJECT -

SITE LOCATION -

DWG. NO. : NIHVA/19-20/VDR/158 REV.:- 0

SCALE: NTS WT: SHEET: 01 OF 01