

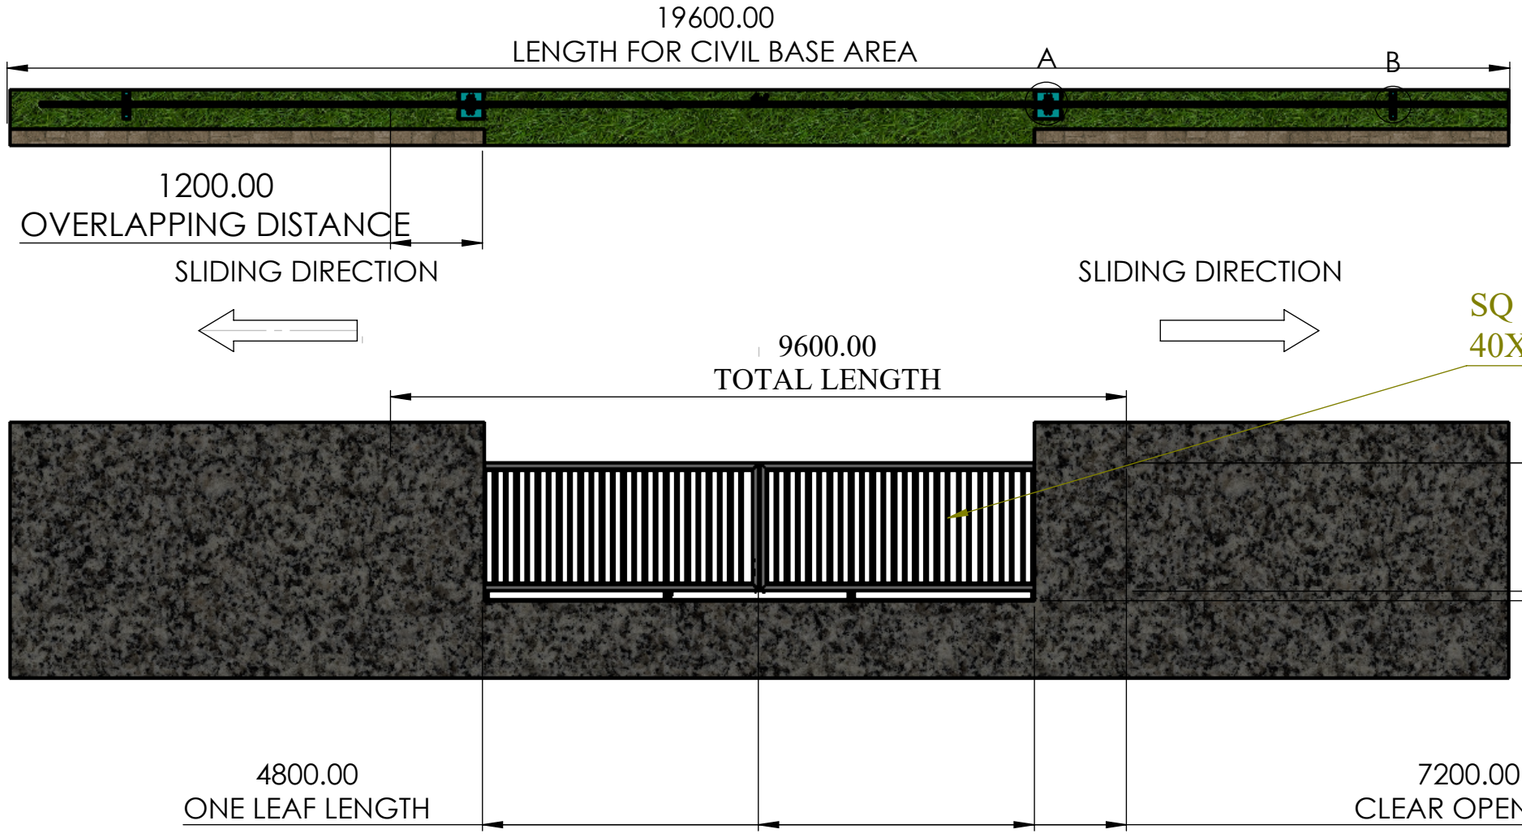


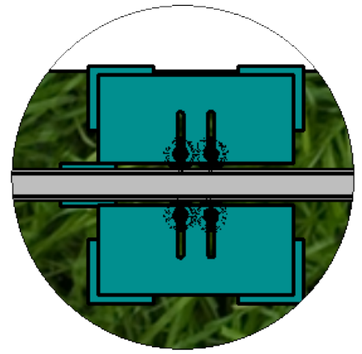

DETAIL A
SCALE 1 : 10

POST 1AND NYLON BEARING ASM

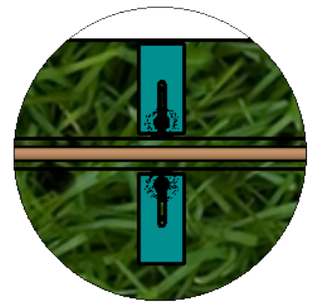

DETAIL B
SCALE 1 : 10

POST 2 AND NYLON BEARING ASM

TITLE - GATE				NIHVA TECHNOLOGIES PVT.LTD.PUNE Website - www.nihva.com
DWG NO - NTPL268-PM			QTY - 1	
	NAME	SIGNATURE	DATE	PROJECT NO - NTPL268-PM- AD
DRAWN	V.B.		02-05-2025	PRODUCT -SLIDING GATE
CHK'D	S.W.		02-05-2025	SITE LOCATION -
APPV'D	V.T.		02-05-2025	
if any queries contact - supportautomation@nihva.com				REVISION -00
ALL DIMENSION ARE IN mm			A3	SCALE - SHEET 1 OF 1