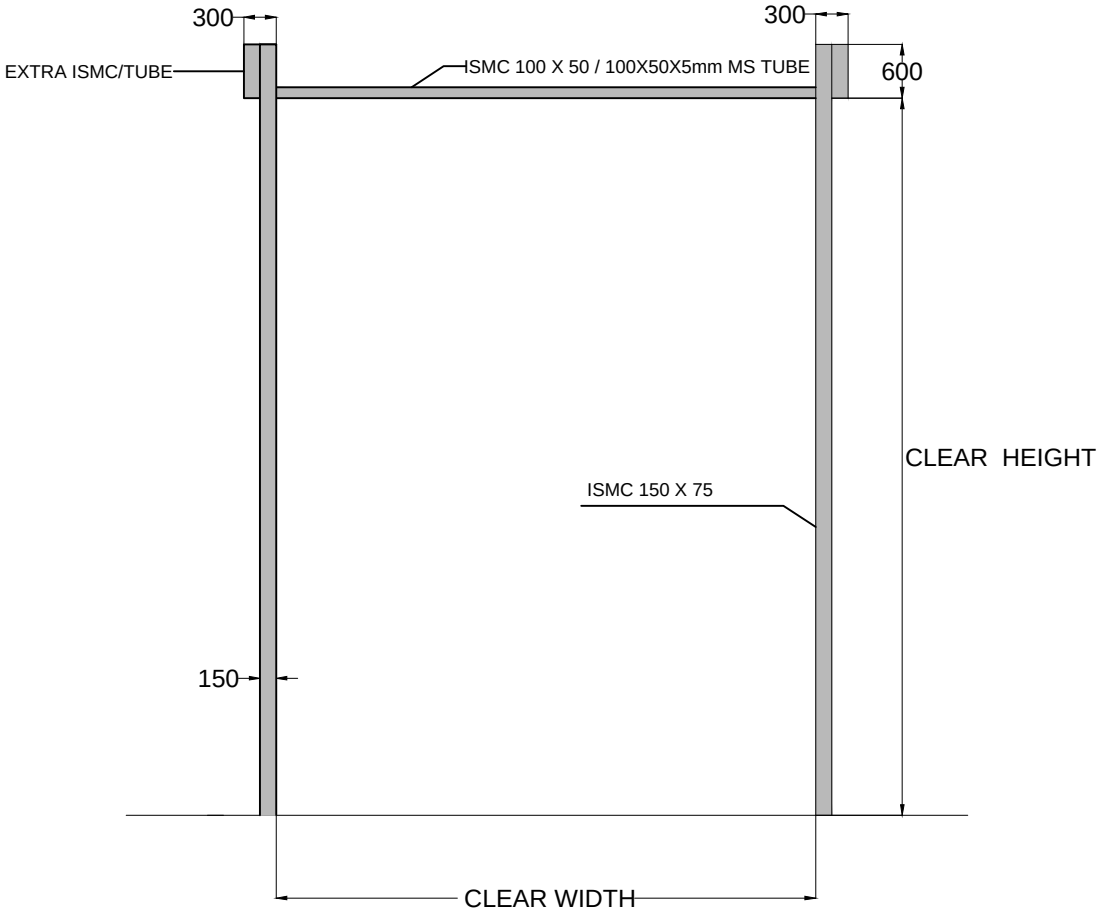


STRUCTURE FOR MOTORIZED ROLLING SHUTTER.

NOTE :

1. MATERIAL FOR ALL STRUCTURE = M.S
2. ALL CIVIL WORK WILL BE IN CLIENT SCOPE.
3. REQUIRED STEEL STRUCTURE IN CLIENT SCOPE.

CLEAR WIDTH	CLEAR HEIGHT	QTY.
4500	5000	01 NO
3500	4000	09 NOS
3000	3000	15 NOS

TOLERANCE - ±10mm

This drawing & design is the property of NIHVA TECHNOLOGIES. Not to be sold or copied to any other concern.

TITLE
STRUCTURE FOR GEAR OPERATED ROLLING SHUTTER

NIHVA TECHNOLOGIES PVT. LTD.
NIHVA TECHNOLOGIES PVT. LTD. PUNE
Tel : 020 66304033
Email:- info@nihva.com
Website:- www.nihva.com

	NAME	SIGN	DATE
DRAWN	P.V.A		25.03.2019
CHECK	V.M.T		25.03.2019
APPRD.			

CLIENT - GROUP SURYA

PROJECT -

SITE LOCATION - PUNE

If any queries contact : design@nihva.com

DWG. NO. : NIHVA/18-19/0319 REV- 00

ALL DIMENSION ARE IN mm

SCALE: NTS WT: SHEET: 01 OF 01