




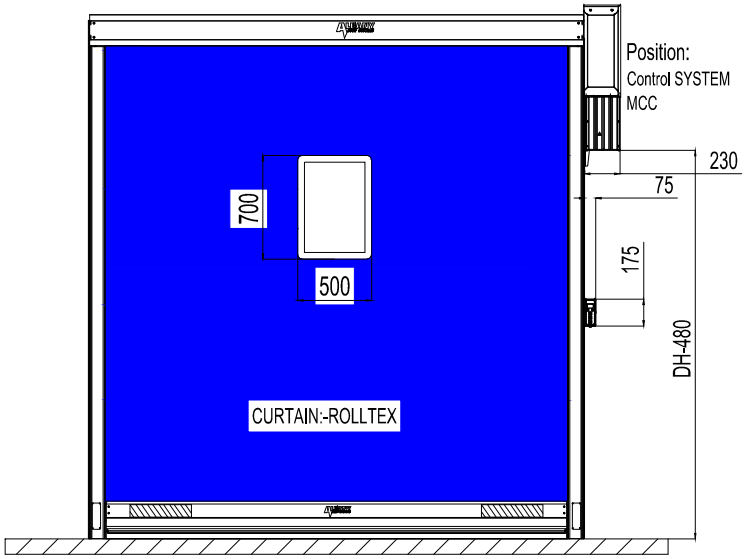


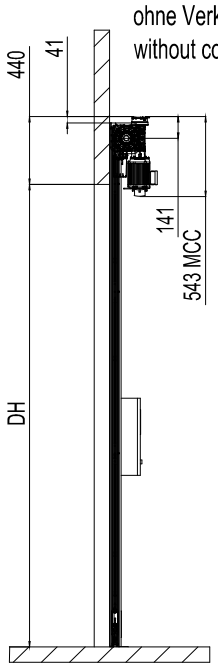

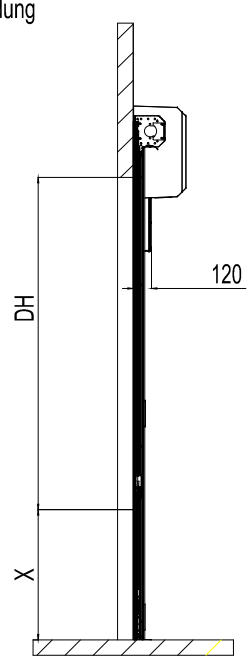

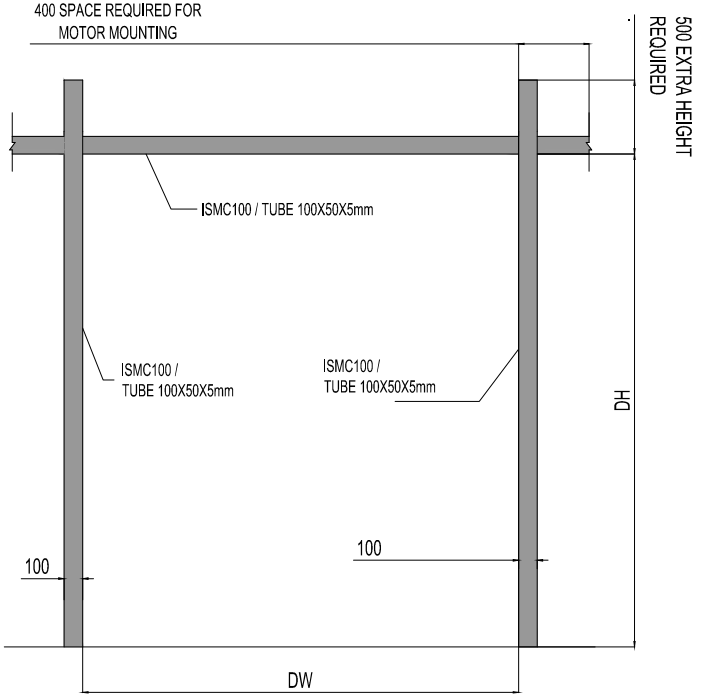

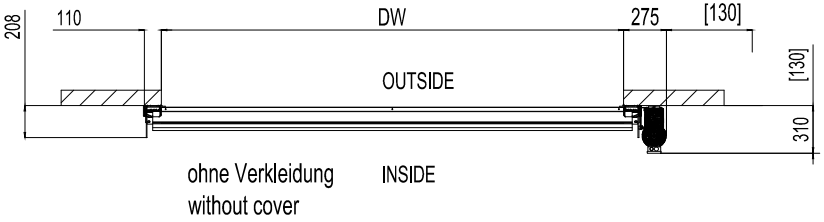

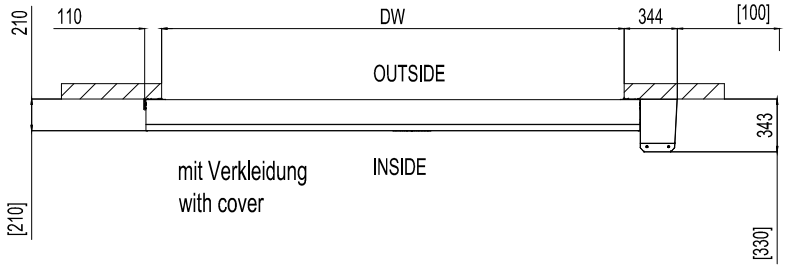



Tolerance ±3 mm (for all dimensions)

Dimensions in [ ] ==> clearance for installation

NOTE : REQ. ALL CIVIL WORK & M.S STRUCTURE WILL BE IN CLIENT SCOPE.

CURTAIN:-ROLLTEX

CLEAR WIDTH(DW)	CLEAR HEIGHT(DH)	CERTIFICATION	QTY	MOTOR LOCATION
3000mm	2500mm	UL	02 NOS	
1500mm	2500mm	CE	01 NOS	

This drawing & design is the property of NIHVA TECHNOLOGIES. Not to be sold or copied to any other concern.

TITLE	HIGH SPEED DOOR RP300 & STRUCTURE		
	NAME	SIGN	DATE
DRAWN	P.V.A		15.03.2019
CHECK	V.M.T		15.03.2019
APPV'ED			
If any queries contact : design@nihva.com			
ALL DIMENSION ARE IN mm			

NIHVA TECHNOLOGIES PVT. LTD. PUNE
Tel : 020 66304033
Email:- info@nihva.com
Website:- www.nihva.com

CLIENT :- **MOTHERSON AUTOMOTIVE TECHNOLOGIES & ENGINEERING**

PROJECT :-

LOCATION :- **URAPAKKAM, TAMILNADU**

DWG. NO. :- NIHVA/18-19/0289 REV.:- 0

SCALE: NTS WT: SHEET: 01 OF 01