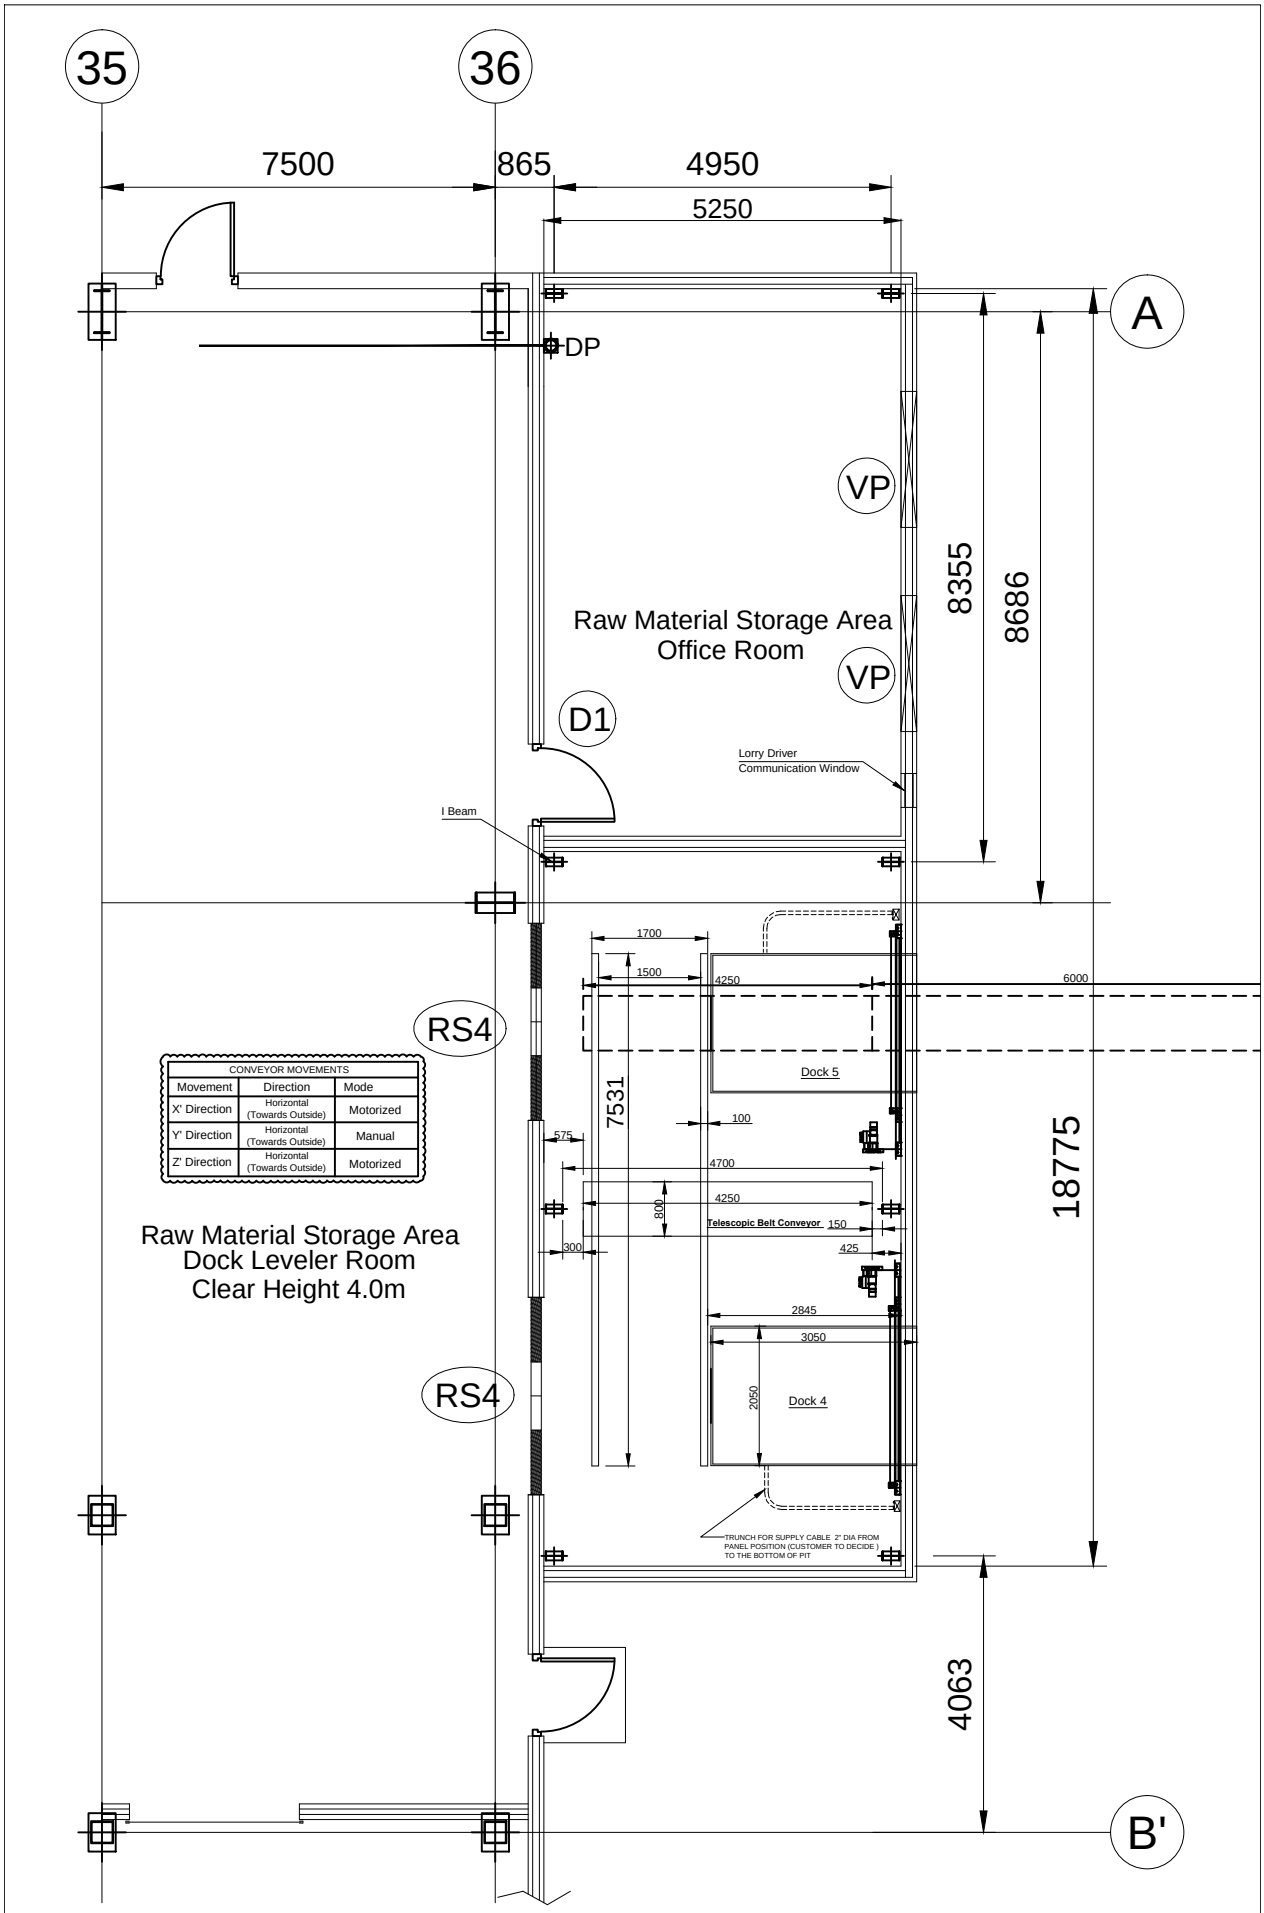

35
36
7500
865
4950
5250
A
DP
VP
8355
8686
Raw Material Storage Area
Office Room
VP
D1
Lorry Driver
Communication Window
I Beam
1700
1500
4250
6000
RS4
Dock 5
7531
100
575
4700
4250
800
Telescopic Belt Conveyor
150
425
300
18775
2845
3050
RS4
2050
Dock 4
TRUNCH FOR SUPPLY CABLE 2" DIA FROM PANEL POSITION (CUSTOMER TO DECIDE) TO THE BOTTOM OF PIT
4063
B'
CONVEYOR MOVEMENTS
Movement | Direction | Mode
X' Direction | Horizontal (Towards Outside) | Motorized
Y' Direction | Horizontal (Towards Outside) | Manual
Z' Direction | Horizontal (Towards Outside) | Motorized
Raw Material Storage Area
Dock Leveler Room
Clear Height 4.0m