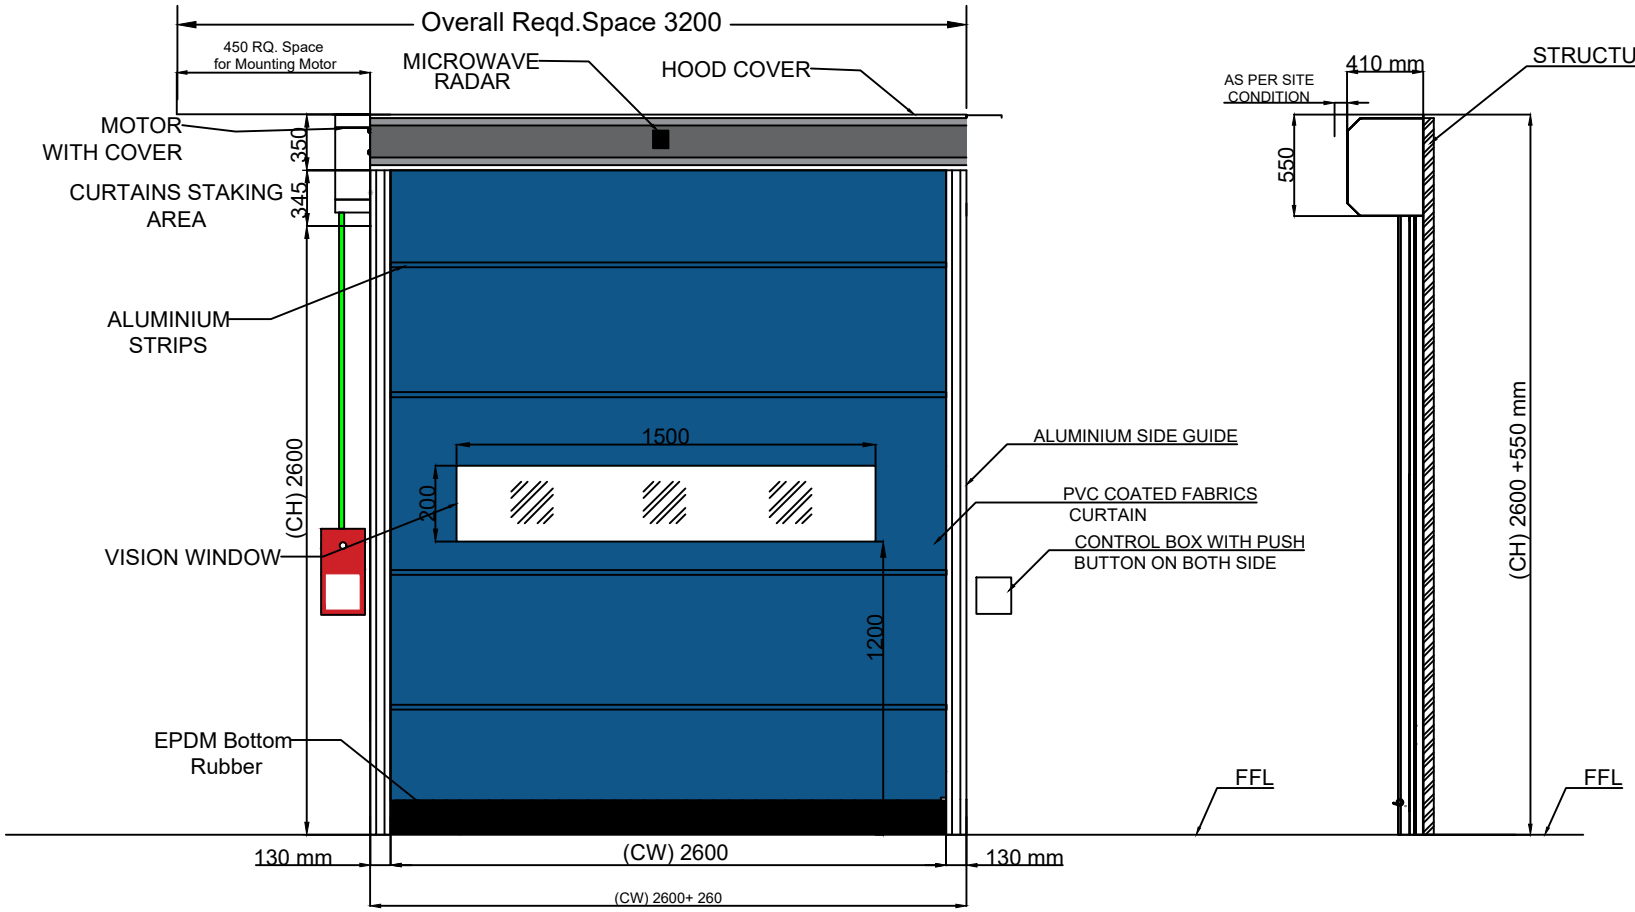


Location area :- SEZ 1 C -Groung floor- entry

TECHNICAL SPECIFICATION :

SR.	SPECIFICATIONS	DETAILS
	Use	Internal Door
	Mounting	On Structure: Inside / outside
	Control Panel	As per STD
2	Motor	Nihva make
3	Manual Release	Hand Crank
4	Door Travel Speed	Opening: 0.3m/Sec & Closing: 0.8m/Sec
5	Safety Device	Safety Photocell Pair & Safety Edges
6	Accessories	Microwave radar on both side ,interlocking system for two doors Flashing Light,Motor & Hood cover,push button

Note:-
1. All Dimensions are in mm
2.This drawing is solely meant to be understood.
3. RAL code confirm by client

Sr	Clear Width (CW)	Clear Height (CH)	QTY
1	**2600**	**2600**	01

This drawing & design is the property of NIHVA TECHNOLOGIES. Not to be sold or copied to any other concern.

TITLE	HIGH SPEED DOOR		
	NAME	SIGN	DATE
DRAWN	S.J		22.10.2024
CHECK	S.J		23.10.2024
APPRD.	V.T		23.10.2024

NIHVA TECHNOLOGIES PVT. LTD. PUNE
Tel : 020 66304033
Email:- info@nihva.com
Website:- www.nihva.com

CLIENT - bilcare
PROJECT - HIGH SPEED DOOR
FORMAT NO - NIHVA-DD-F-03
If any queries contact : projectsupport@nihva.com
DWG. NO. : NIHVA/24-25/SM/241001 REV- R00
ALL DIMENSION ARE IN mm
SCALE: NTS WT: SHEET: