


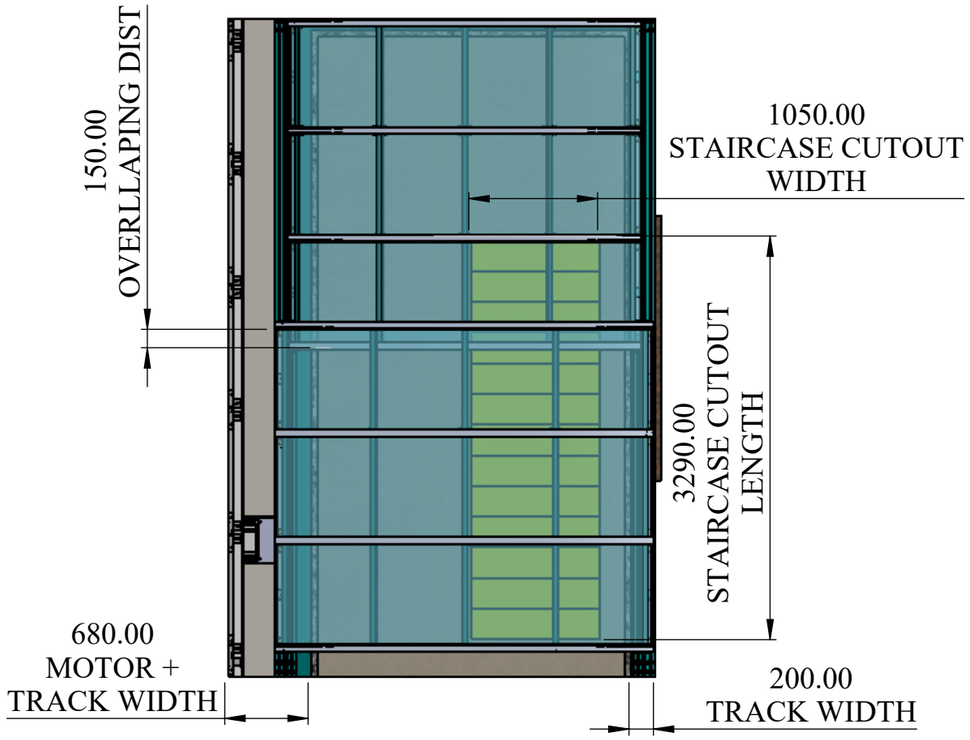


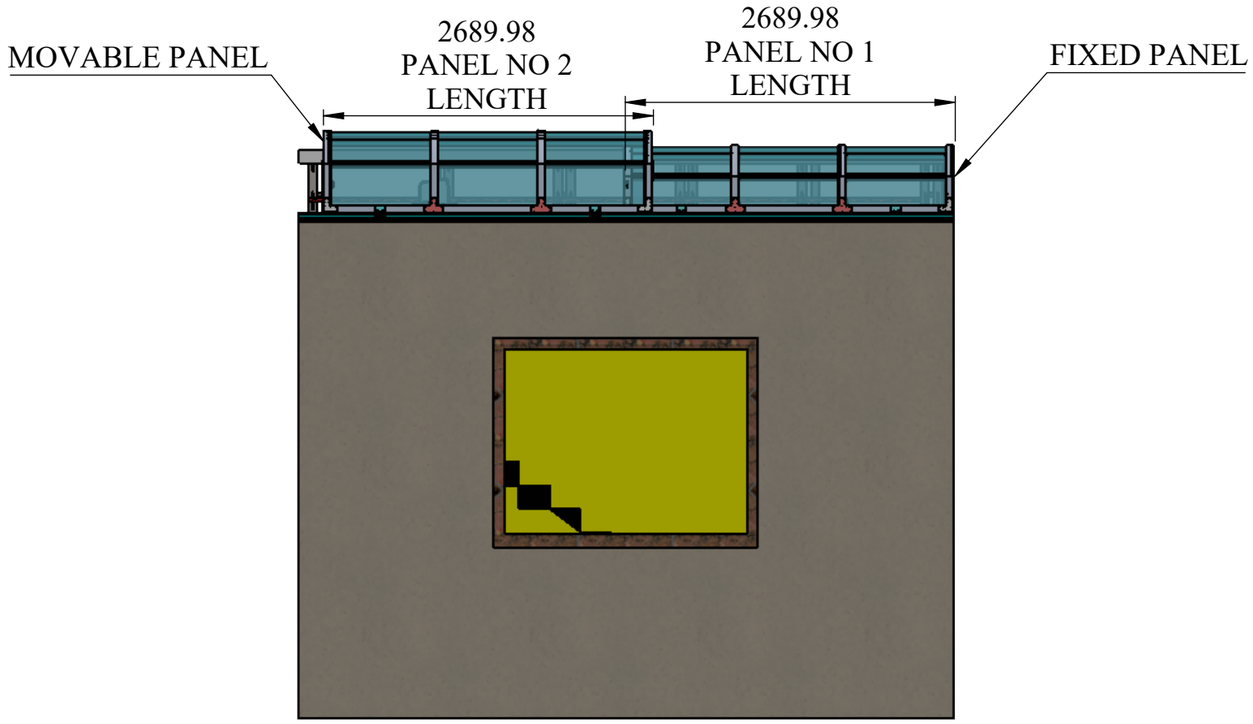

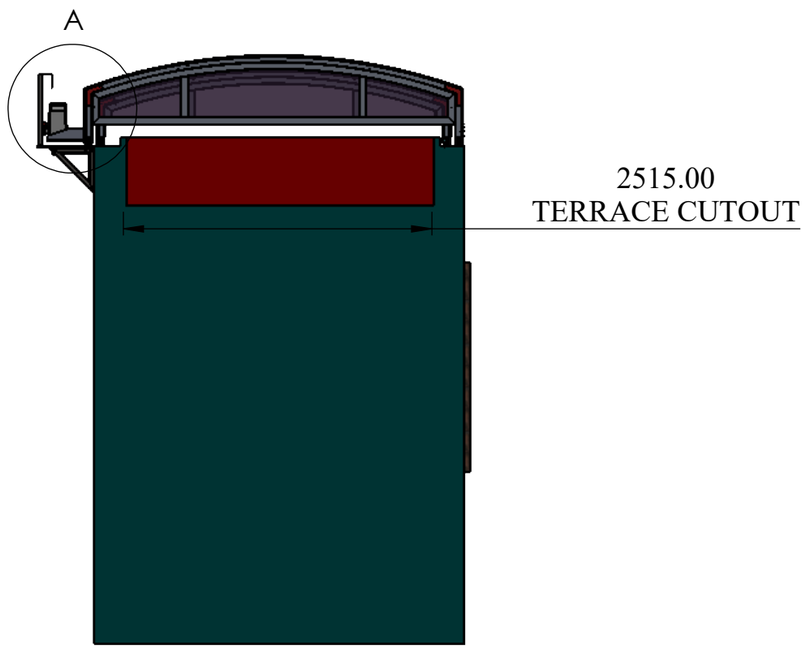


MAIN ASSEMBLY

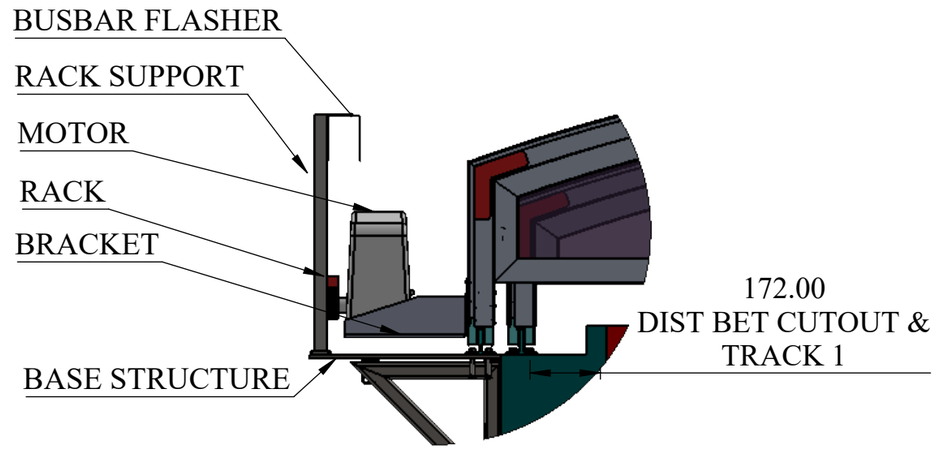

DETAIL A
SCALE 1 : 15

TITLE - ROOF AUTOMATION				NIHVA TECHNOLOGIES PVT.LTD.PUNE
DWG NO - NTPL-000-PM-001-00-00-00				Website - www.nihva.com
	NAME	SIGNATURE	DATE	PROJECT NO - NTPL-000-PM
DRAWN	V.W		26-05-2025	PRODUCT - RETRACTABLE ROOF
CHK'D	S.W.		26-05-2025	SITE LOCATION - LUCKNOW
APPV'D	V.T.		26-05-2025	
if any queries contact - supportautomation@nihva.com				REVISION - / QTY - 1
ALL DIMENSION ARE IN mm			A3	SCALE / SHEET 1 OF 28


ITEM NO.	PART NUMBER	DESCRIPTION	QTY.
1	RR_BASE STRUCTURE		1
2	RR_BASE STRCUTURE		1
3	GUIDE RAILS-T75-1B	STD (5 M LENGTH)	4
4	RR_PANEL NO 01 ASM		1
5	RR_PANEL NO 02 ASM		1
6	RR_RACK SUPPORT	STD (LOOSE PART)	6
7	RR_BUSBAR FLASHER	STD (LOOSE PART) 2100MM	1
8	RR_PRJ LUCKANOW RACK ASM		1
9	RR_MOTOR (600 kg)	STD	1
10	RR_ENCLOSURE NO 02		1
11	RR_ENCLOSURE NO 01		1
12	RR_L ANGLE PLATE CORNNER JOINING PLATE	AL JOINING PLATE	8
13	RR_ Anchor Bolt M10x75	STD	48
14	NYLON STOPPER		4
15	IS 2269 - M6 x 40-N		8

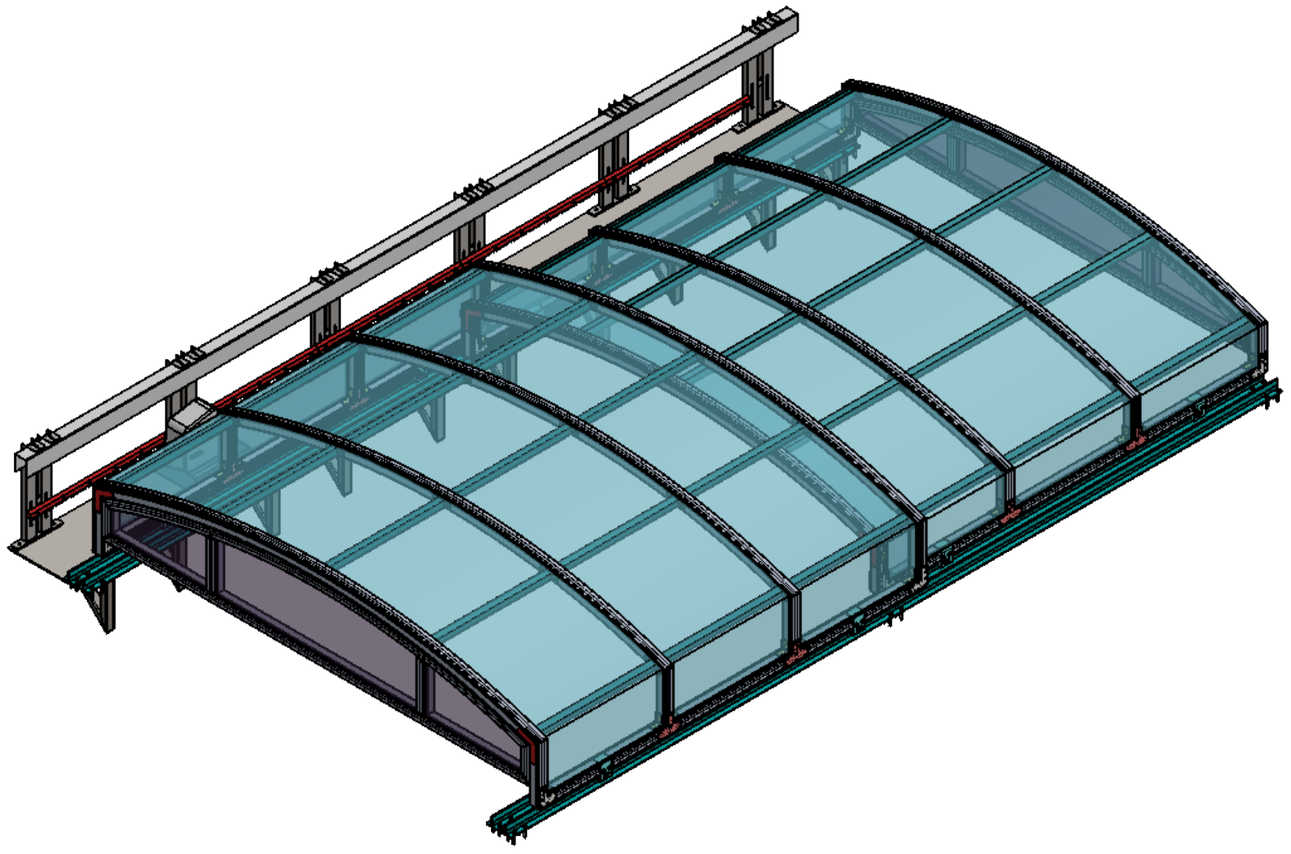



ISOMETRIC VIEW OF RECTRATABLE ROOF

TITLE - ROOF AUTOMATION				NIHVA Technologies Pvt. Ltd.	NIHVA TECHNOLOGIES PVT.LTD.PUNE Website - www.nihva.com
DWG NO - NTPL-000-PM-001-00-00-00					
	NAME	SIGNATURE	DATE	PROJECT NO - NTPL-000-PM	
DRAWN	V.W		26-05-2025	PRODUCT - RETRACTABLE ROOF	
CHK'D	S.W.		26-05-2025	SITE LOCATION - LUCKNOW	
APPV'D	V.T.		26-05-2025		
if any queries contact - supportautomation@nihva.com				REVISION -	QTY - 1
ALL DIMENSION ARE IN mm		A3		SCALE	SHEET 2 OF 28


ITEM NO.	PART NUMBER	DESCRIPTION	QTY.
1	RR_CIVIL BASE		1
2	RR_BASE STRUCTURE		1
3	RR_BASE STRCUTURE		1
4	GUIDE RAILS-T75-1B	STD (5 M LENGTH)	4
5	RR_RACK SUPPORT	STD (LOOSE PART)	6
6	RR_BUSBAR FLASHER	STD (LOOSE PART) 2100MM	1
7	RR_PRJ LUCKANOW RACK ASM		1
8	RR_ Anchor Bolt M10x75	STD	48

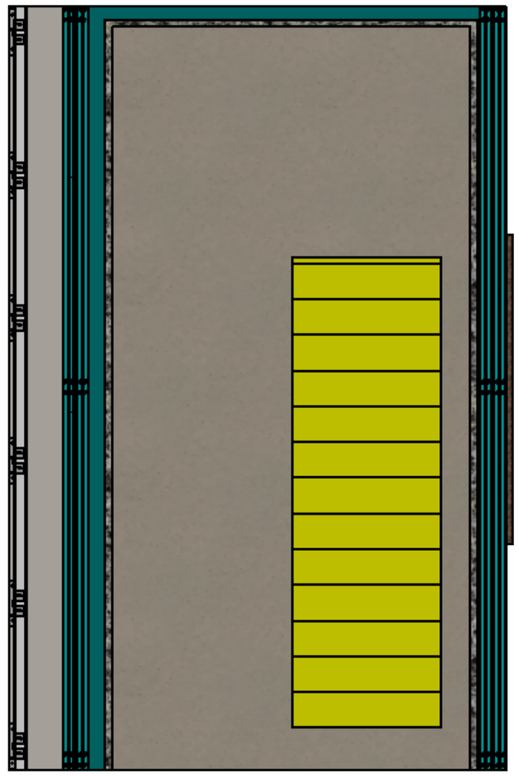

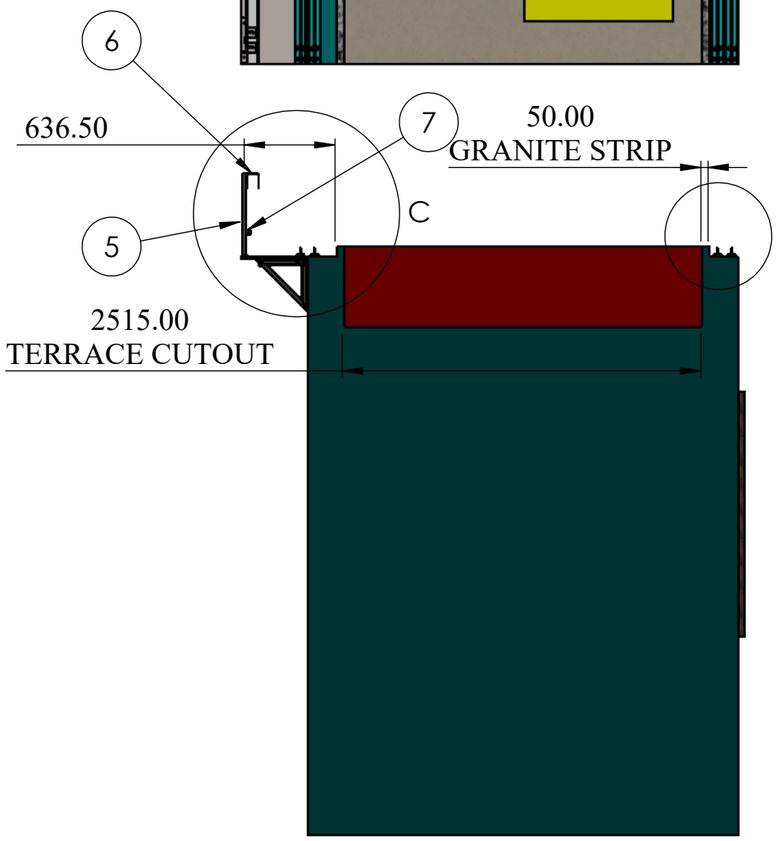

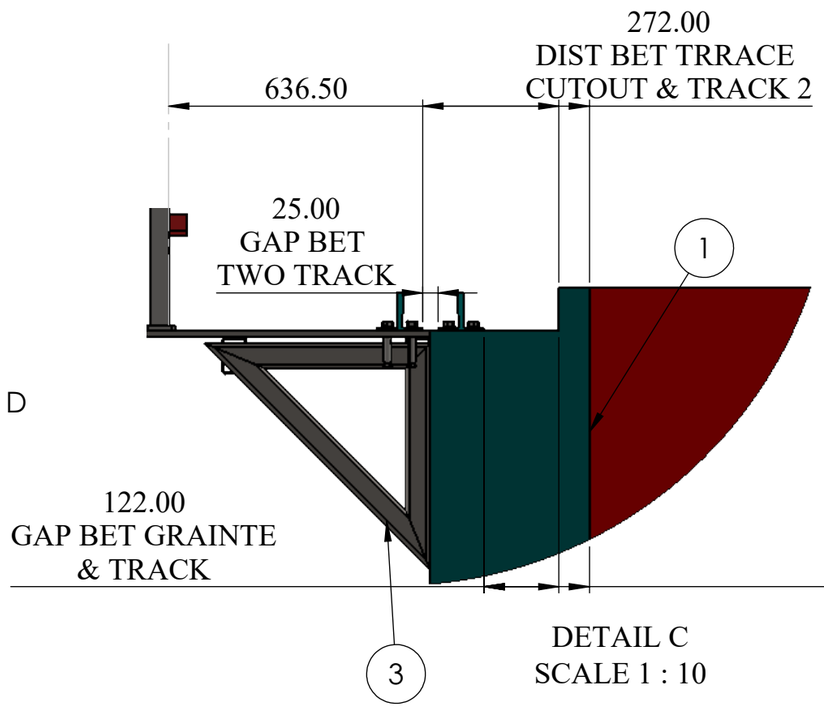


DETAIL C
SCALE 1 : 10

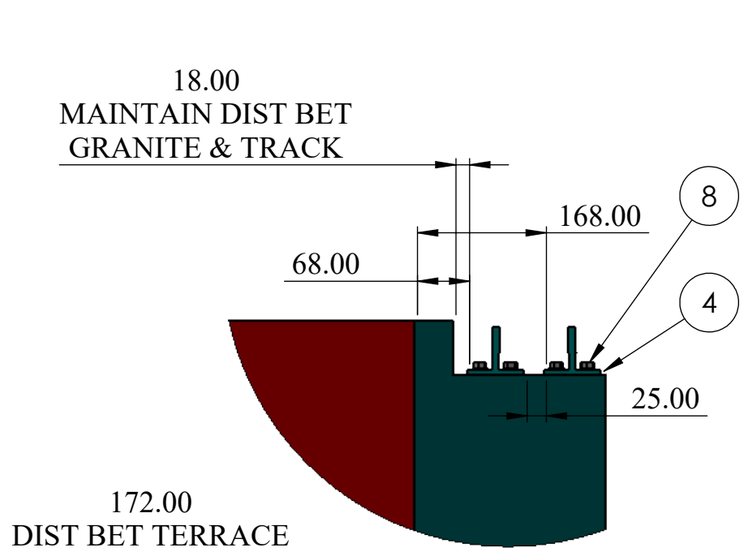


DETAIL D
SCALE 1 : 8


NOTE :
SUB ASSEMBLY NO 01
TRACK ASSEMBLY

TITLE - ROOF AUTOMATION				NIHVA TECHNOLOGIES PVT.LTD.PUNE
DWG NO - NTPL-000-PM-001-02-00-00				Website - www.nihva.com
	NAME	SIGNATURE	DATE	PROJECT NO - NTPL-000-PM
DRAWN	V.W		26-05-2025	PRODUCT - RETRACTABLE ROOF
CHK'D	S.W.		26-05-2025	SITE LOCATION - LUCKNOW
APPV'D	V.T.		26-05-2025	
if any queries contact - supportautomation@nihva.com				REVISION - / QTY - 1
ALL DIMENSION ARE IN mm		A3		SCALE / SHEET 3 OF 28

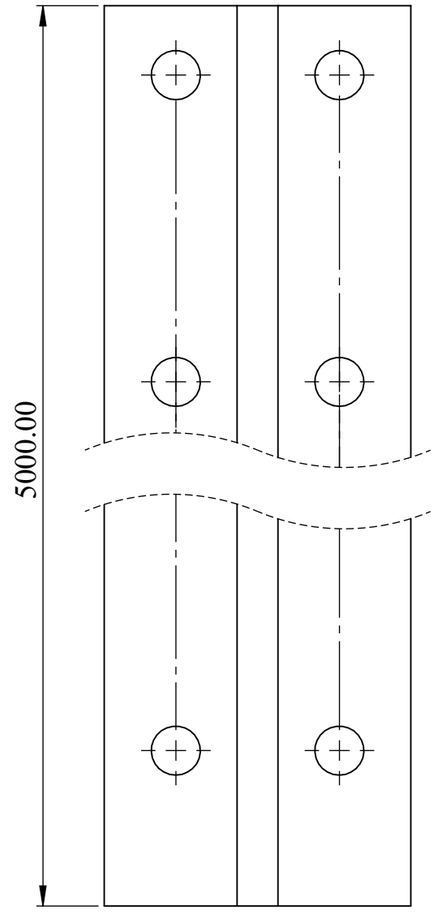

ITEM NO.	PART NUMBER	DESCRIPTION	QTY.
1	GUIDE RAILS-T75-1B	STD (5 M LENGTH)	4

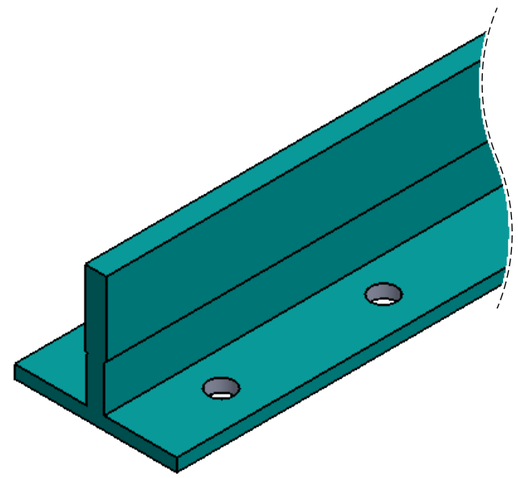


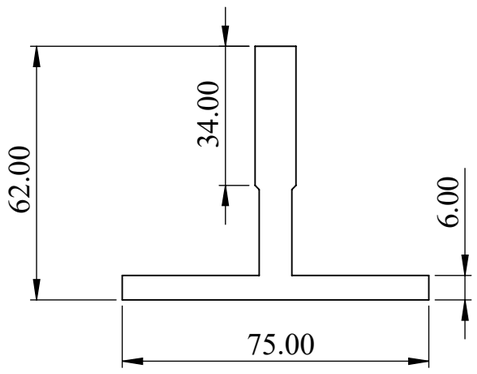


NOTE :
LIFT TRACK - T 75
5M UNIT LENGTH
QTY - 4 No's

TITLE - ROOF AUTOMATION				NIHVA TECHNOLOGIES PVT.LTD.PUNE Website - www.nihva.com
DWG NO - NTPL-000-PM-001-02-01-04				
	NAME	SIGNATURE	DATE	PROJECT NO - NTPL-000-PM
DRAWN	V.W		26-05-2025	PRODUCT - RETRACTABLE ROOF
CHK'D	S.W.		26-05-2025	SITE LOCATION - LUCKNOW
APPV'D	V.T.		26-05-2025	
if any queries contact - supportautomation@nihva.com				REVISION - QTY - 1
ALL DIMENSION ARE IN mm		A3		SCALE SHEET 4 OF 28

ITEM NO.	PART NUMBER	DESCRIPTION	QTY.
1	GUIDE RAILS-T75-1B	PART TO BE CUT-350MM	1

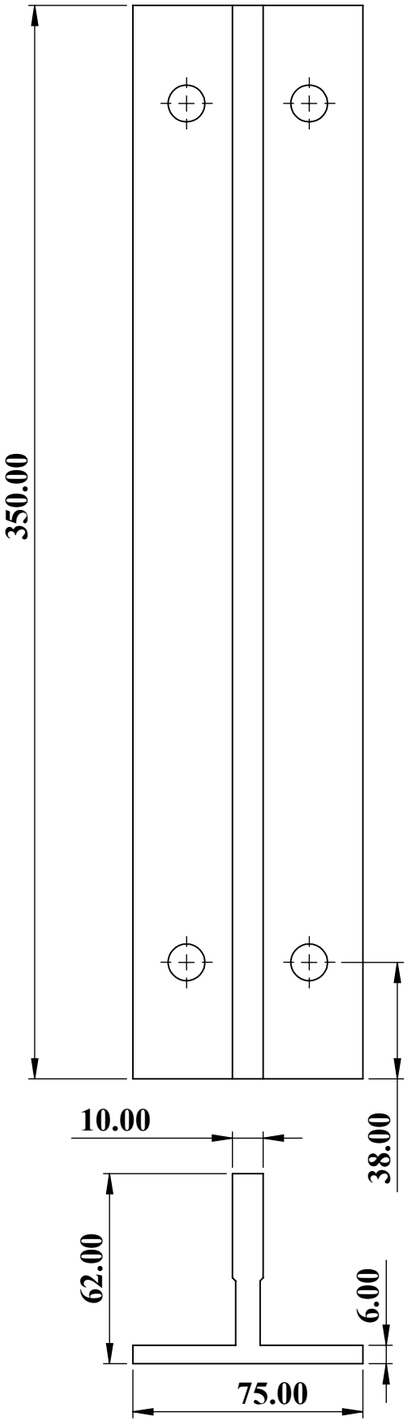

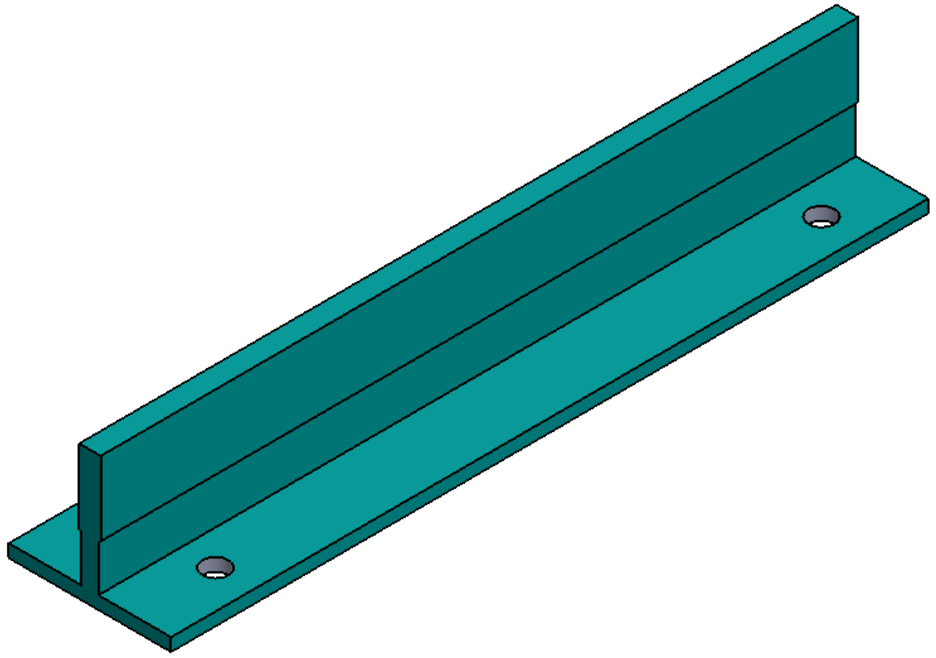



NOTE :
LIFT TRACK - T 75
PART REQUIRED TO CUT - 350MM
QTY - 4 No's

TITLE - ROOF AUTOMATION				NIHVA TECHNOLOGIES PVT.LTD.PUNE
DWG NO - NTPL-000-PM-001-02-01-04				Website - www.nihva.com
	NAME	SIGNATURE	DATE	PROJECT NO - NTPL-000-PM
DRAWN	V.W		26-05-2025	PRODUCT - RETRACTABLE ROOF
CHK'D	S.W.		26-05-2025	SITE LOCATION - LUCKNOW
APPV'D	V.T.		26-05-2025	
if any queries contact - supportautomation@nihva.com				REVISION - QTY - 1
ALL DIMENSION ARE IN mm			A3	SCALE SHEET 5 OF 28

ITEM NO.	PART NUMBER	DESCRIPTION	QTY.
1	RR_ Anchor Bolt M10x75	STD	48



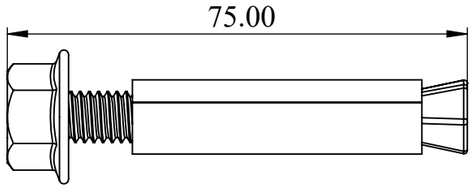


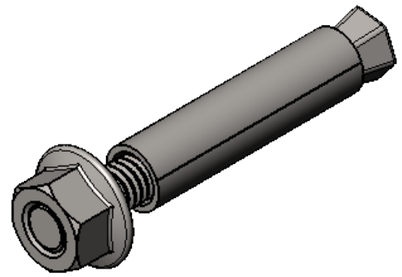


NOTE :
ANCHOR BOLT M10x75MM
QTY - 48

TITLE - ROOF AUTOMATION				NIHVA TECHNOLOGIES PVT.LTD.PUNE
DWG NO - NTPL-000-PM-001-02-08-08				Website - www.nihva.com
	NAME	SIGNATURE	DATE	PROJECT NO - NTPL-000-PM
DRAWN	V.W		26-05-2025	PRODUCT - RETRACTABLE ROOF
CHK'D	S.W.		26-05-2025	SITE LOCATION - LUCKNOW
APPV'D	V.T.		26-05-2025	
if any queries contact - supportautomation@nihva.com				REVISION - QTY - 1
ALL DIMENSION ARE IN mm		A3		SCALE SHEET 6 OF 28

ITEM NO.	PART NUMBER	DESCRIPTION	QTY.
1	C- CHANEL MTG BASE PLATE	320X50X10MM THK	6
2	C - CHANEL	70X30X575	12
3	C- CHANEL JOINING PLATE	35X40X10MM THK	12
4	RR_ BUSBAR MTG PLATE		12

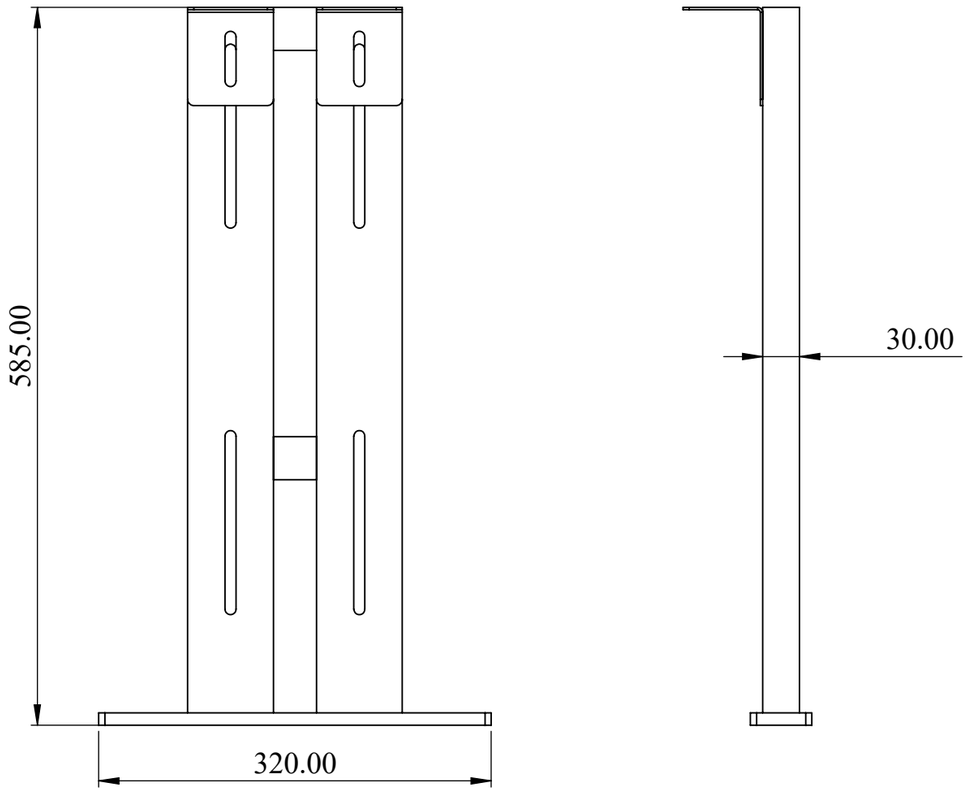


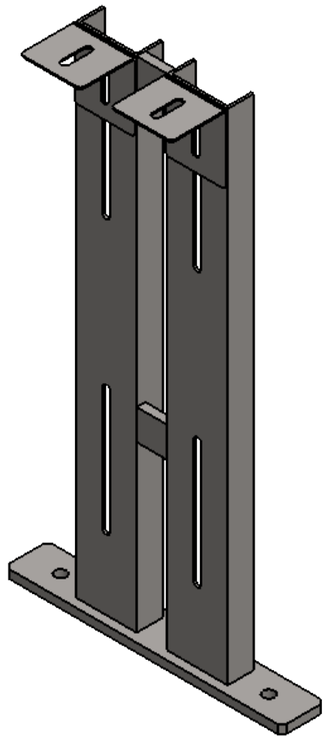

TITLE - ROOF AUTOMATION				NIHVA TECHNOLOGIES PVT.LTD.PUNE
DWG NO - NTPL-000-PM-001-02-05-05				Website - www.nihva.com
	NAME	SIGNATURE	DATE	PROJECT NO - NTPL-000-PM
DRAWN	V.W		26-05-2025	PRODUCT - RETRACTABLE ROOF
CHK'D	S.W.		26-05-2025	SITE LOCATION - LUCKNOW
APPV'D	V.T.		26-05-2025	
if any queries contact - supportautomation@nihva.com				REVISION - QTY - 1
ALL DIMENSION ARE IN mm		A3		SCALE SHEET 7 OF 28

ITEM NO.	PART NUMBER	DESCRIPTION	QTY.
1	RR_RACK	STD (M4 RACK, 30x8x1000 mm, ZINC COATED WITH SPACERS AND SCREWS.)	6




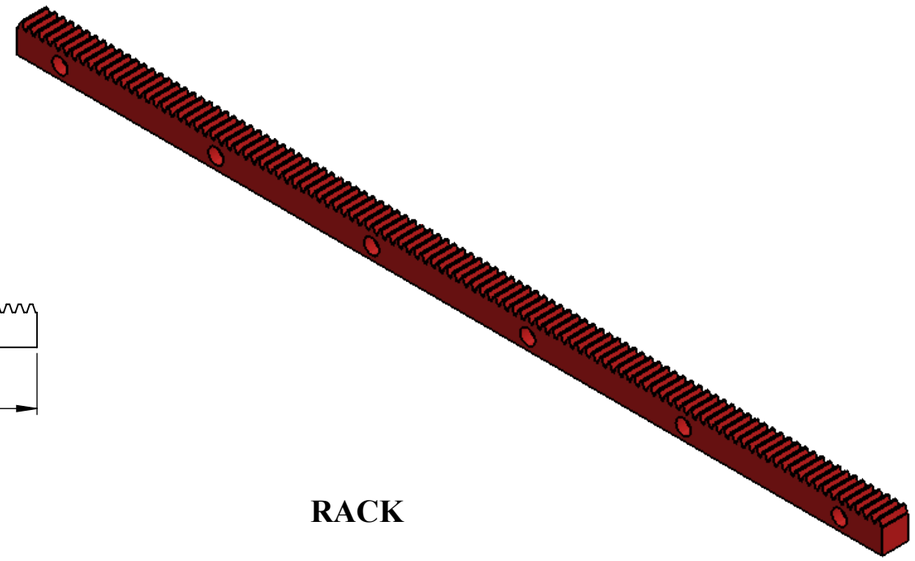



RACK

TITLE - ROOF AUTOMATION				NIHVA TECHNOLOGIES PVT.LTD.PUNE
DWG NO - NTPL-000-PM-001-02-07-07				Website - www.nihva.com
	NAME	SIGNATURE	DATE	PROJECT NO - NTPL-000-PM
DRAWN	V.W		26-05-2025	PRODUCT - RETRACTABLE ROOF
CHK'D	S.W.		26-05-2025	SITE LOCATION - LUCKNOW
APPV'D	V.T.		26-05-2025	
if any queries contact - supportautomation@nihva.com				REVISION - QTY - 1
ALL DIMENSION ARE IN mm		A3		SCALE SHEET 8 OF 28

ITEM NO.	PART NUMBER	DESCRIPTION	QTY.
1	RR_BUSBAR FLASHER	STD (LOOSE PART) 2100MM	3
		Sheet	1

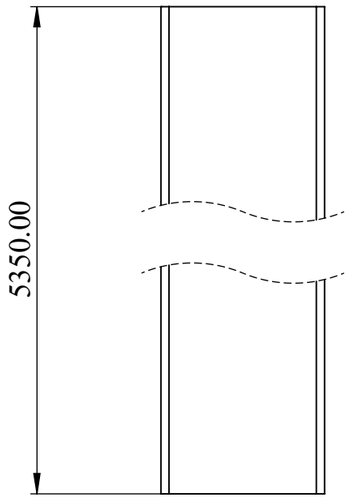


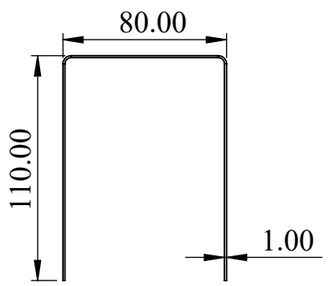

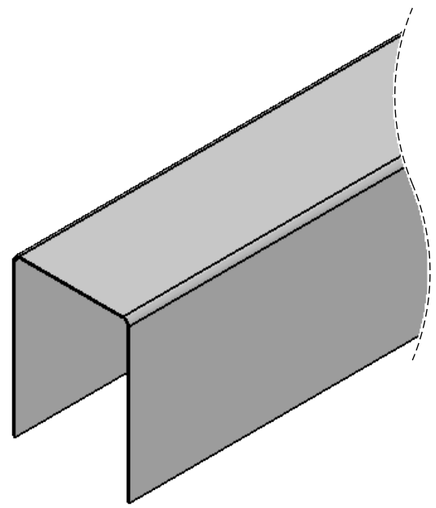



NOTE :
BUSBAR FLASHER

TITLE - ROOF AUTOMATION				NIHVA TECHNOLOGIES PVT.LTD.PUNE
DWG NO - NTPL-000-PM-001-02-06-06				Website - www.nihva.com
	NAME	SIGNATURE	DATE	PROJECT NO - NTPL-000-PM
DRAWN	V.W		26-05-2025	PRODUCT - RETRACTABLE ROOF
CHK'D	S.W.		26-05-2025	SITE LOCATION - LUCKNOW
APPV'D	V.T.		26-05-2025	
if any queries contact - supportautomation@nihva.com				REVISION - QTY - 1
ALL DIMENSION ARE IN mm		A3		SCALE SHEET 9 OF 28

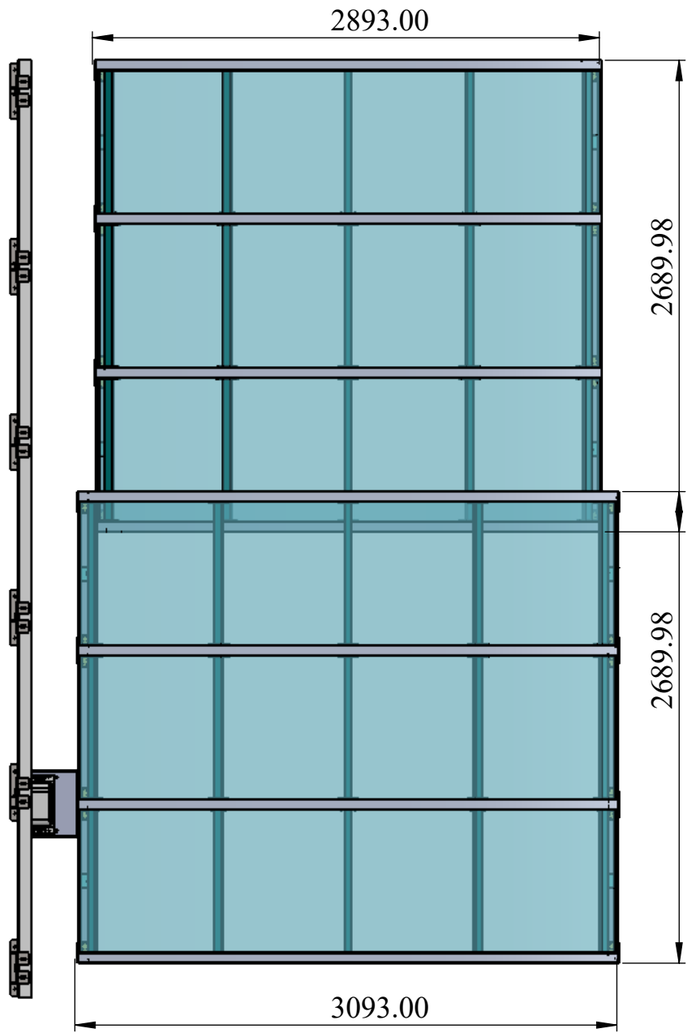


ITEM NO.	PART NUMBER	DESCRIPTION	QTY.
1	RR_PANEL NO 01 ASM		1
2	RR_PANEL NO 02 ASM		1
3	RR_RACK SUPPORT	STD (LOOSE PART)	6
4	RR_BUSBAR FLASHER	STD (LOOSE PART) 2100MM	1
5	RR_PRJ LUCKANOW RACK ASM		1
6	RR_MOTOR (600 kg)	STD	1
7	RR_ENCLOSURE NO 02		1
8	RR_ENCLOSURE NO 01		1
9	NYLON STOPPER		4
10	IS 2269 - M6 x 40-N		8

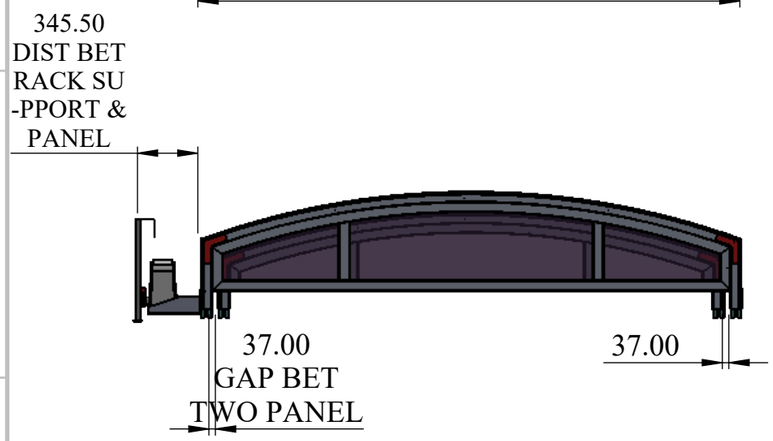

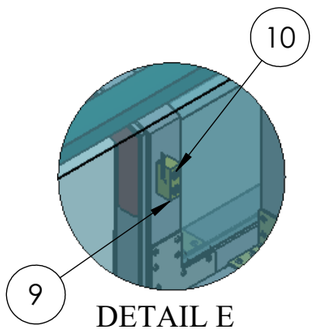

DETAIL E
SCALE 1 : 8


NYLON STOPPER

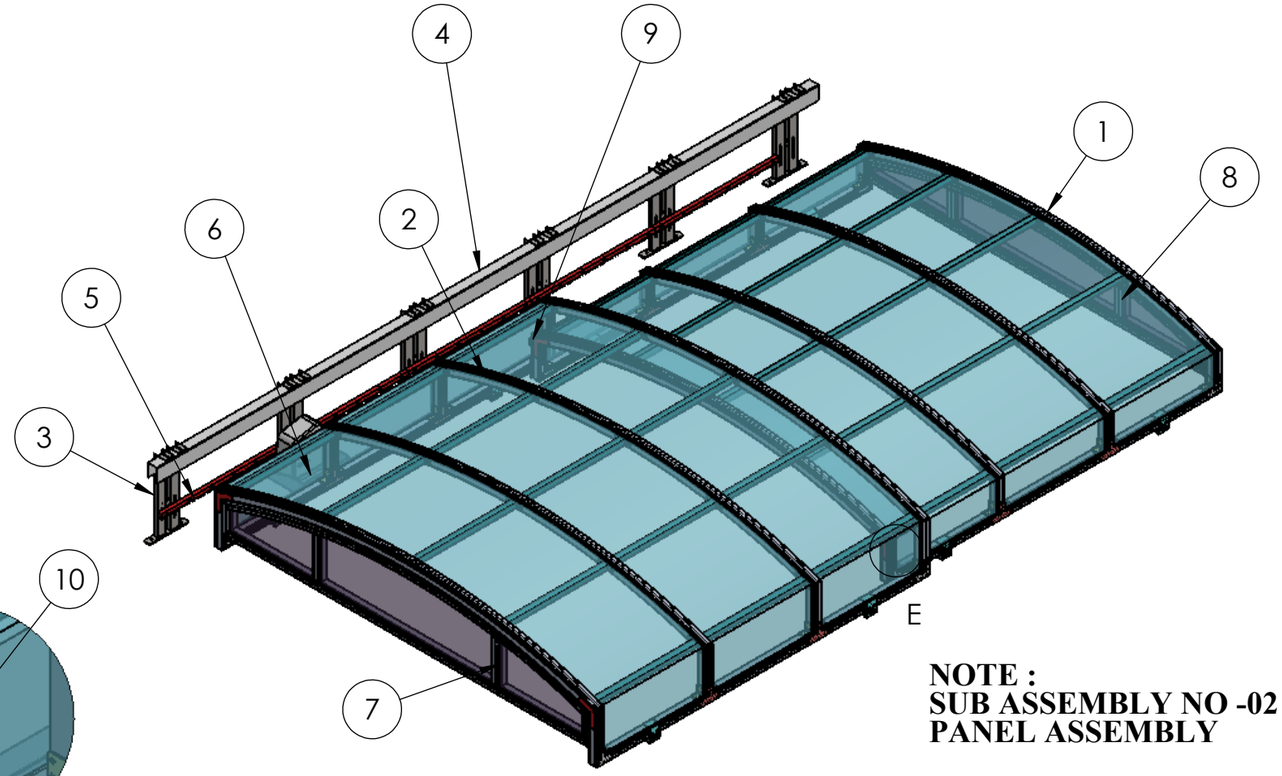


NOTE :
SUB ASSEMBLY NO -02
PANEL ASSEMBLY

TITLE - ROOF AUTOMATION				NIHVA TECHNOLOGIES PVT.LTD.PUNE
DWG NO - NTPL-000-PM-001-00-00-00				Website - www.nihva.com
	NAME	SIGNATURE	DATE	PROJECT NO - NTPL-000-PM
DRAWN	V.W		26-05-2025	PRODUCT - RETRACTABLE ROOF
CHK'D	S.W.		26-05-2025	SITE LOCATION - LUCKNOW
APPV'D	V.T.		26-05-2025	
if any queries contact - supportautomation@nihva.com				REVISION - / QTY - 1
ALL DIMENSION ARE IN mm			A3	SCALE / SHEET 10 OF 28

ITEM NO.	PART NUMBER	DESCRIPTION	QTY.
1	RR_ PANEL NO 01		1
2	AL Support tube SQ TUBE 40X40X1.5 MM L-816.66 MM	AL INTERMEDIAT SUPPORT TUBE	15
3	RR_BEARING BLOCK ASM WITH SHOULDER BOLT	SLIDING BLOCK	4
4	T PLATE	JOINING PLATE	8
5	L PALTE	JOINING PLATE	8
6	L ANGLE PLATE	JOINING PLATE	12
7	RR_L ANGLE PLATE CORNNER JOINING PLATE	AL JOINING PLATE	4
8	RR_ PANEL NO 01 polycarbonet sheet		3

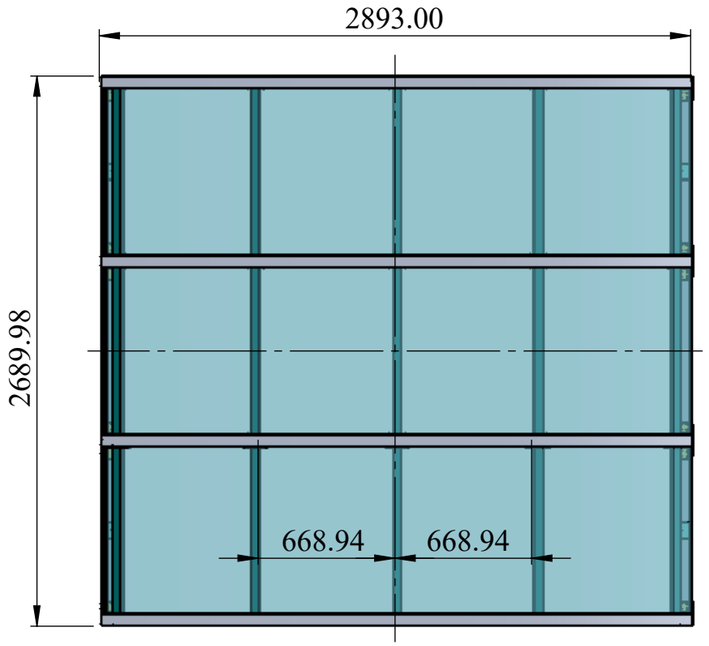




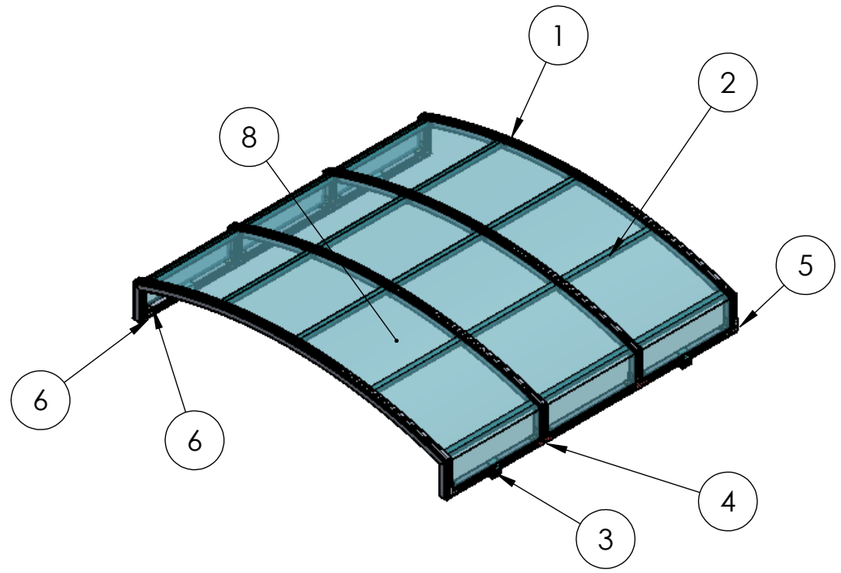


NOTE :
PANEL NO 01 ASM


TITLE - ROOF AUTOMATION				NIHVA TECHNOLOGIES PVT.LTD.PUNE
DWG NO - NTPL-000-PM-001-02-01-00				Website - www.nihva.com
	NAME	SIGNATURE	DATE	PROJECT NO - NTPL-000-PM
DRAWN	V.W		26-05-2025	PRODUCT - RETRACTABLE ROOF
CHK'D	S.W.		26-05-2025	SITE LOCATION - LUCKNOW
APPV'D	V.T.		26-05-2025	
if any queries contact - supportautomation@nihva.com				REVISION - QTY - 1
ALL DIMENSION ARE IN mm		A3		SCALE SHEET 11 OF 28


ITEM NO.	PART NUMBER	DESCRIPTION	QTY.
1	RR_ PANEL NO 01		1

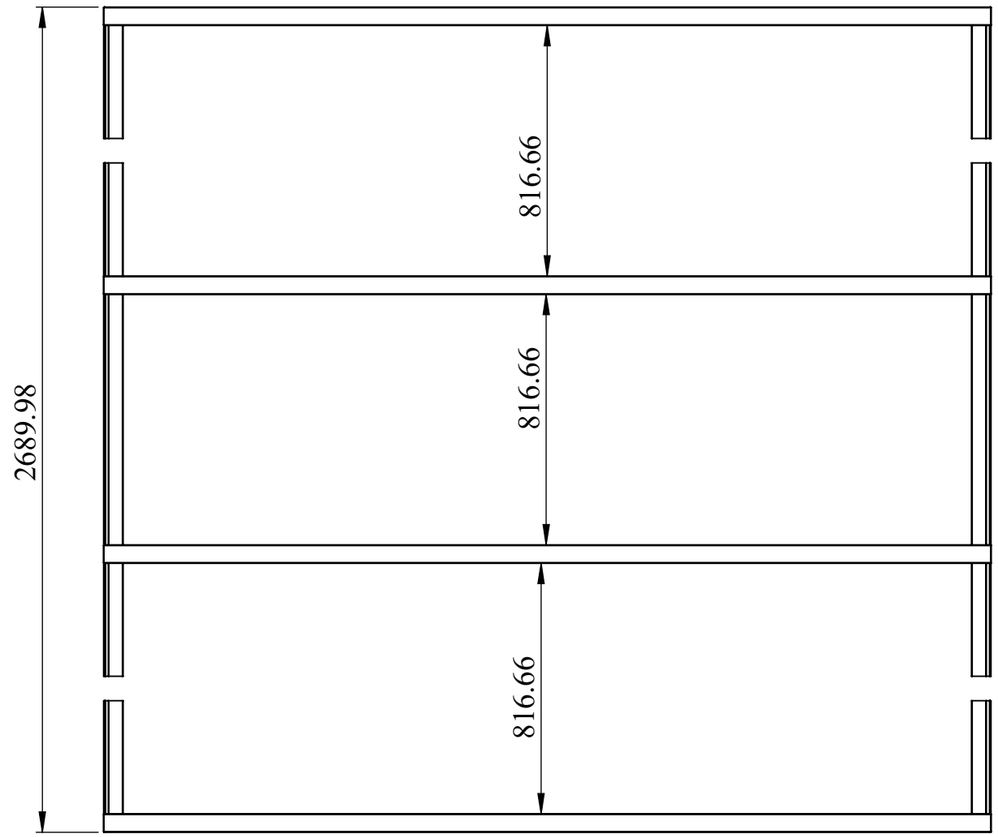

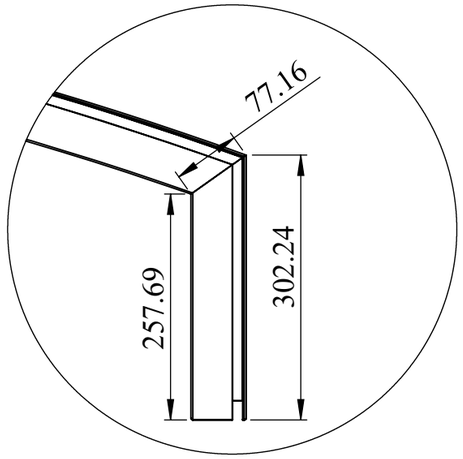

DETAIL F
SCALE 1 : 7

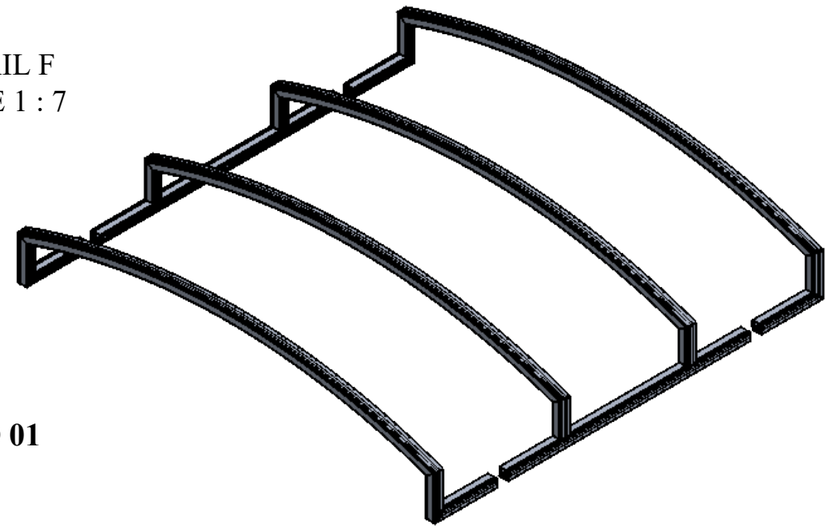


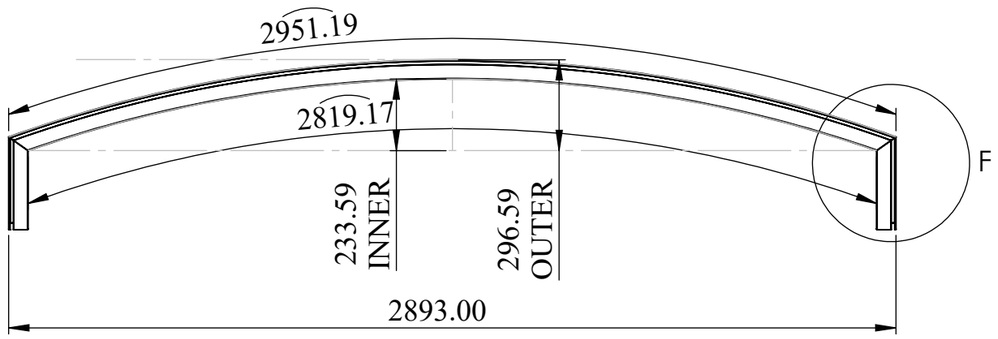

NOTE :
PANEL NO 01

TITLE - ROOF AUTOMATION				NIHVA TECHNOLOGIES PVT.LTD.PUNE
DWG NO - NTPL-000-PM-001-02-01-01				Website - www.nihva.com
	NAME	SIGNATURE	DATE	PROJECT NO - NTPL-000-PM
DRAWN	V.W		27-05-2025	PRODUCT - RETRACTABLE ROOF
CHK'D	S.W.		27-05-2025	SITE LOCATION - LUCKNOW
APPV'D	V.T.		27-05-2025	
if any queries contact - supportautomation@nihva.com				REVISION - QTY - 1
ALL DIMENSION ARE IN mm		A3		SCALE SHEET 12 OF 28


ITEM NO.	PART NUMBER	DESCRIPTION	QTY.
1	AL Support tube SQ TUBE 40X40X1.5 MM L-816.66MM	AL INTERMEDIAT SUPPORT TUBE	15

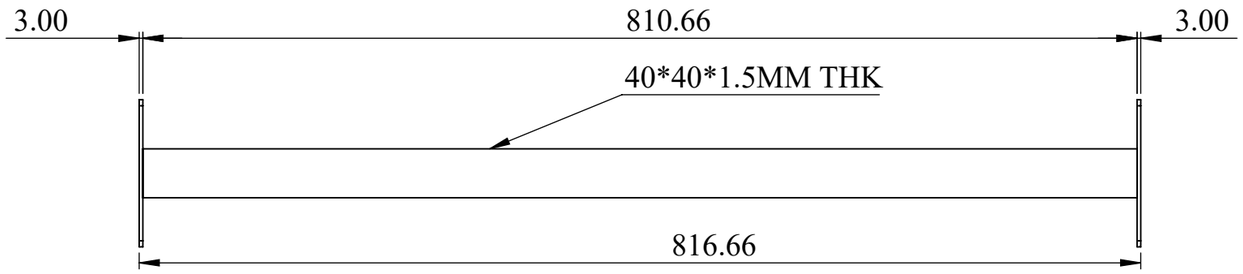





NOTE :
INTERMEDIATE SUPPORT TUBE
ONE PANEL QTY REQ -15 No's
TOTAL REQ - 30 No's

TITLE - ROOF AUTOMATION				NIHVA TECHNOLOGIES PVT.LTD.PUNE
DWG NO - NTPL-000-PM-001-02-02-02				Website - www.nihva.com
	NAME	SIGNATURE	DATE	PROJECT NO - NTPL-000-PM
DRAWN	V.W		27-05-2025	PRODUCT - RETRACTABLE ROOF
CHK'D	S.W.		27-05-2025	SITE LOCATION - LUCKNOW
APPV'D	V.T.		27-05-2025	
if any queries contact - supportautomation@nihva.com				REVISION - QTY - 1
ALL DIMENSION ARE IN mm		A3		SCALE SHEET 13 OF 28

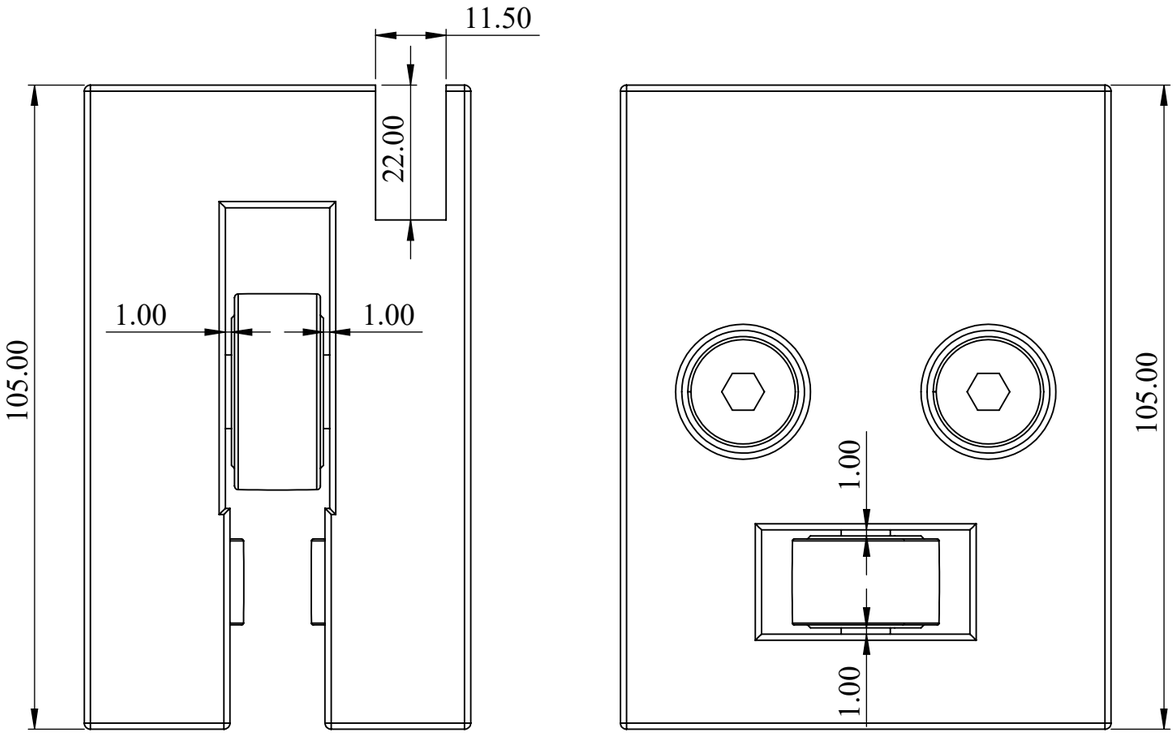

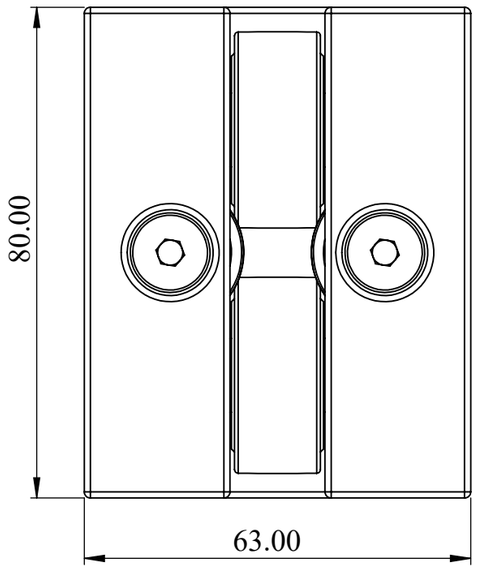


ITEM NO.	PART NUMBER	DESCRIPTION	QTY.
1	BEARING BLOCK (T75-1B)	80X105X63 MM (VMC PART)	4
2	SKF_bearing NATR 12	BRG(STD)	8
3	SKF_bearing NATR 8	BRG(STD)	8
4	RR_ SHOULDER BOLT NATR 12		8
5	ISO 7379 - 8 x 30 --- N		8

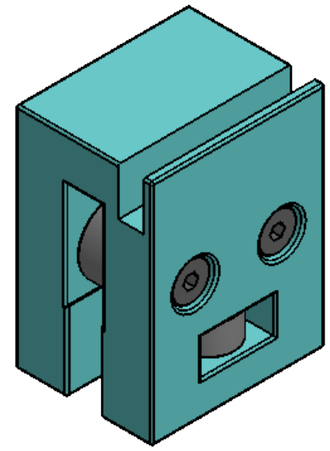



NOTE :
BEARING BLOCK ASM
ONE PANEL QTY REQ - 4 No's
TOTAL REQ - 8 No's.
THIS BEARING BLOCK ASM IS USED FOR ALL PANEL'S

TITLE - ROOF AUTOMATION				NIHVA Technologies Pvt. Ltd.	NIHVA TECHNOLOGIES PVT.LTD.PUNE Website - www.nihva.com
DWG NO - NTPL-000-PM-001-02-03-03				PROJECT NO - NTPL-000-PM	
	NAME	SIGNATURE	DATE	PRODUCT - RETRACTABLE ROOF	
DRAWN	V.W		27-05-2025	SITE LOCATION - LUCKNOW	
CHK'D	S.W.		27-05-2025		
APPV'D	V.T.		27-05-2025		
if any queries contact - supportautomation@nihva.com				REVISION -	QTY - 1
ALL DIMENSION ARE IN mm		A3		SCALE	SHEET 14 OF 28

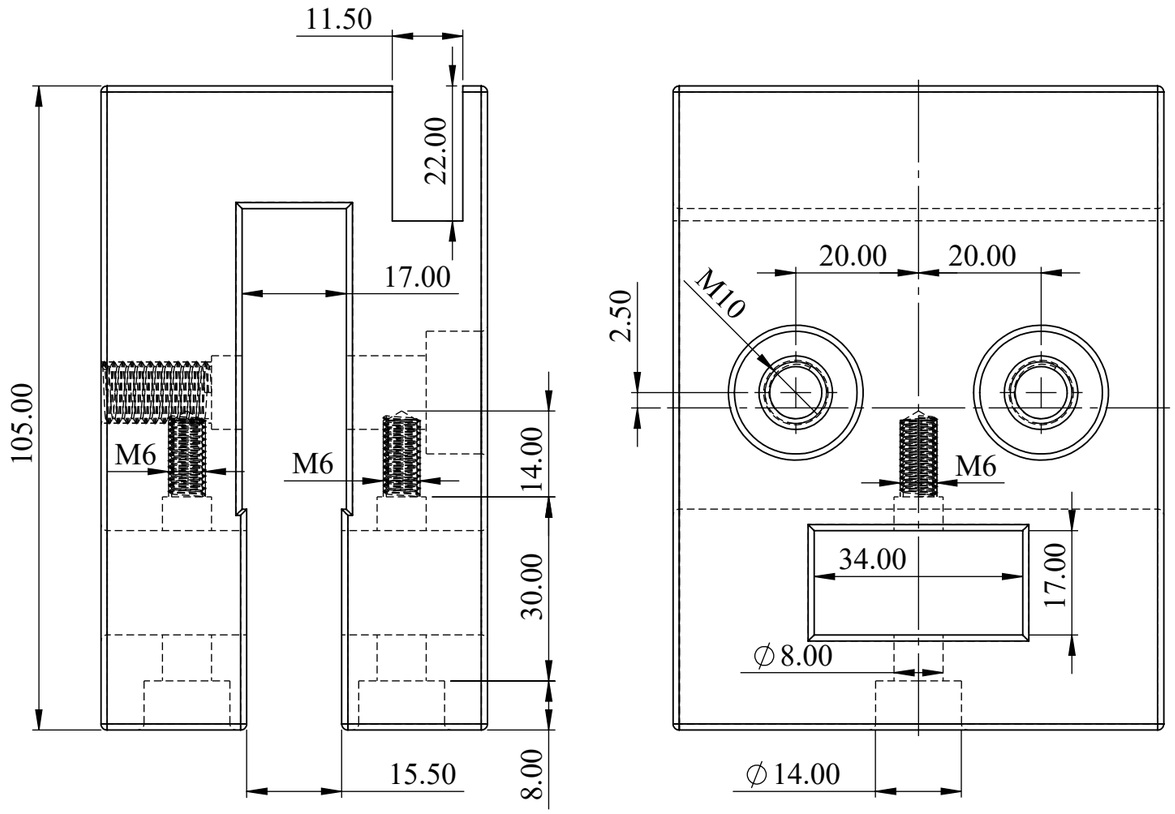

ITEM NO.	PART NUMBER	DESCRIPTION	QTY.
1	BEARING BLOCK (T75-1B)	80X105X63 MM (VMC PART)	8

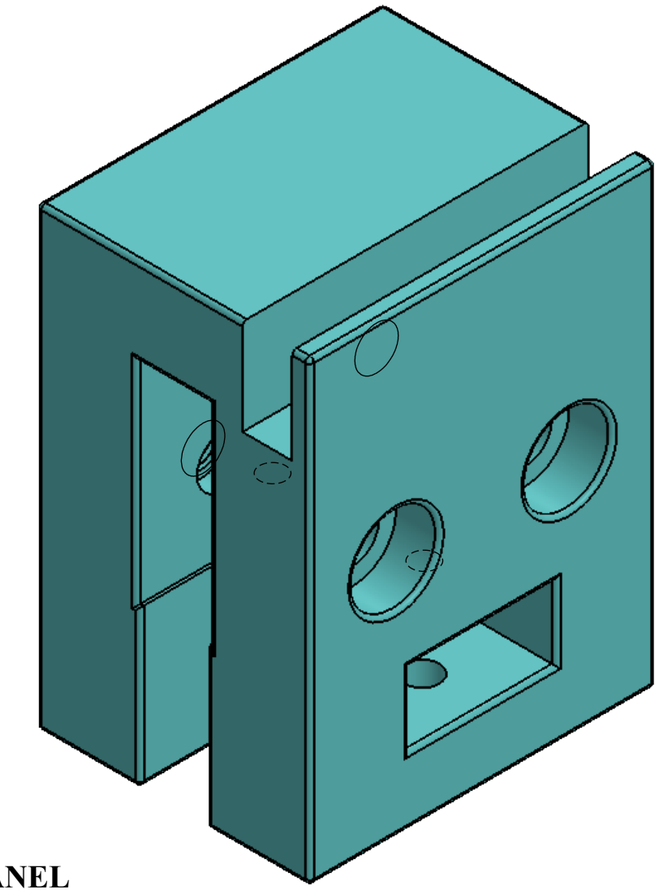


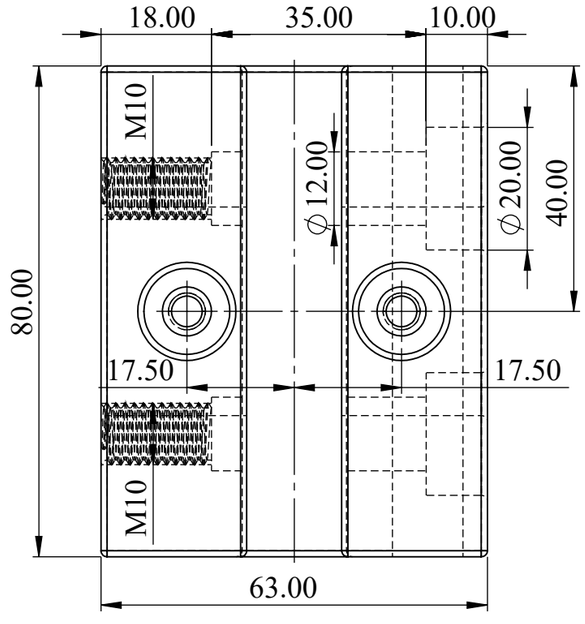


NOTE :
BEARING BLOCK
THIS BEARING BLOCK IS USED FOR ALL PANEL VMC MACHINIG.

TITLE - ROOF AUTOMATION				NIHVA TECHNOLOGIES PVT.LTD.PUNE
DWG NO - NTPL-000-PM-001-02-03-03				Website - www.nihva.com
	NAME	SIGNATURE	DATE	PROJECT NO - NTPL-000-PM
DRAWN	V.W		27-05-2025	PRODUCT - RETRACTABLE ROOF
CHK'D	S.W.		27-05-2025	SITE LOCATION - LUCKNOW
APPV'D	V.T.		27-05-2025	
if any queries contact - supportautomation@nihva.com				REVISION - QTY - 1
ALL DIMENSION ARE IN mm			A3	SCALE SHEET 15 OF 28

ITEM NO.	PART NUMBER	DESCRIPTION	QTY.
1	T PLATE	SS304 -117.5X156X3 MM THK	8
2	RR_rivet_iso_15977_4_x_16_0 ss	RIVET M4X16	80

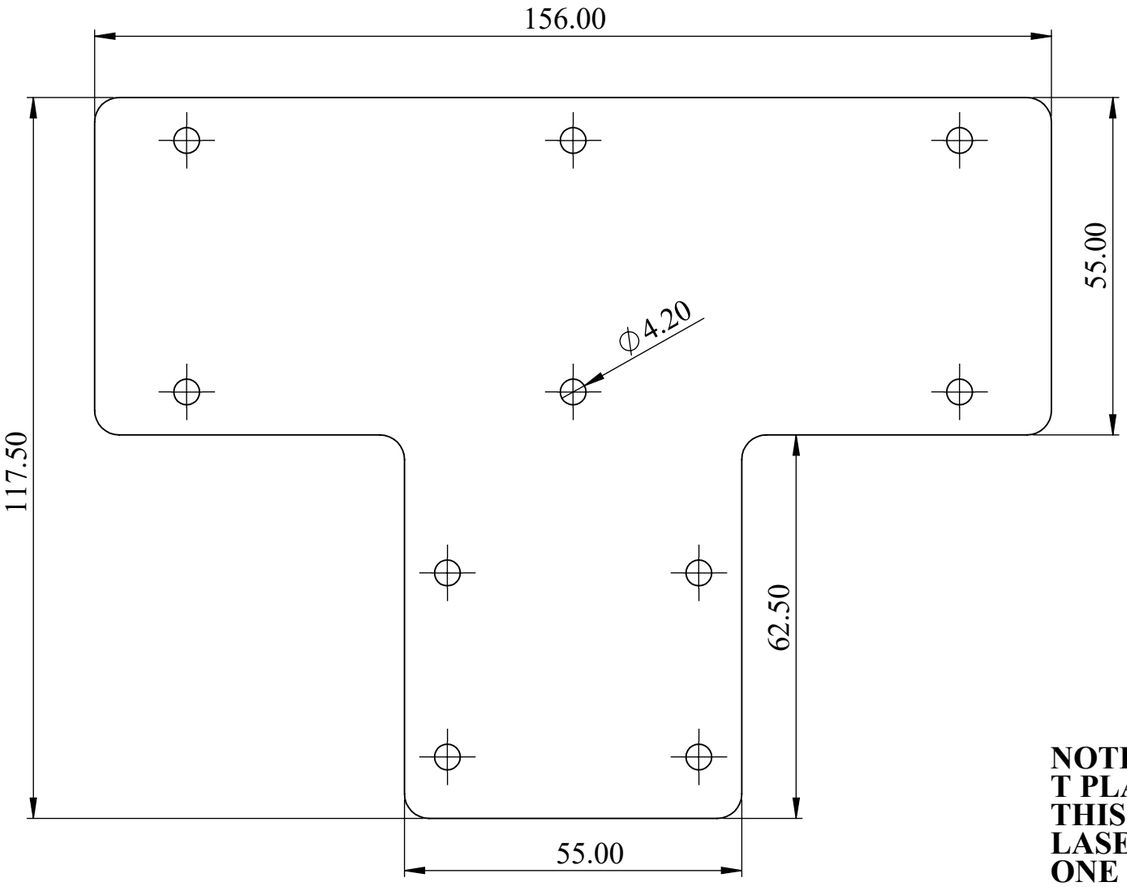


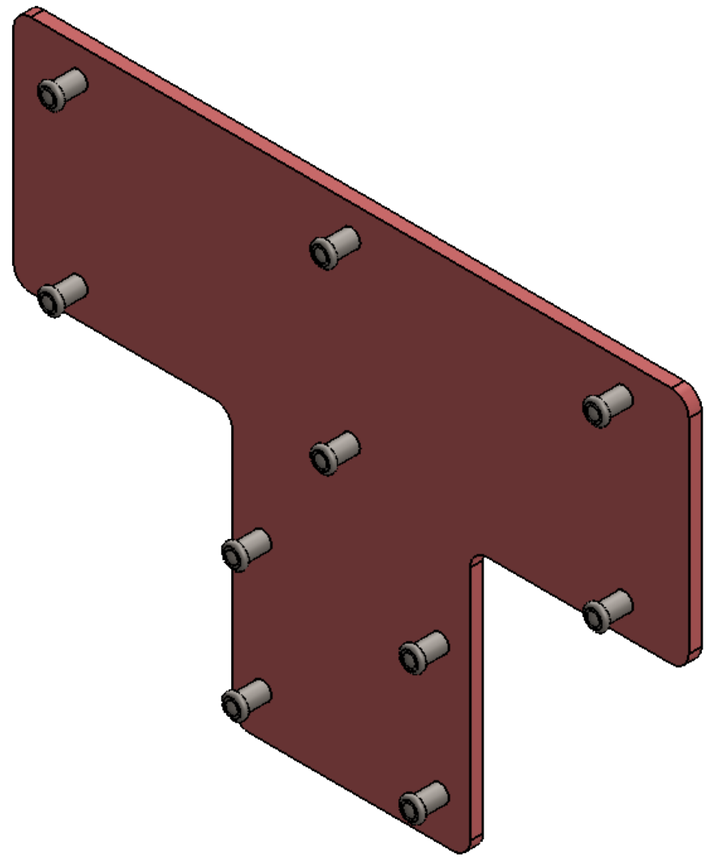


NOTE :
T PLATE
THIS T PLATE IS USED FOR ALL PANEL
LASER CUTTING
ONE PANEL QTY REQ - 8 No's
TOTAL REQ - 16 No'S
THK - 3MM

TITLE - ROOF AUTOMATION				NIHVA TECHNOLOGIES PVT.LTD.PUNE	
DWG NO - NTPL-000-PM-001-02-04-04				Website - www.nihva.com	
	NAME	SIGNATURE	DATE	PROJECT NO - NTPL-000-PM	
DRAWN	V.W		27-05-2025	PRODUCT - RETRACTABLE ROOF	
CHK'D	S.W.		27-05-2025	SITE LOCATION - LUCKNOW	
APPV'D	V.T.		27-05-2025		
if any queries contact - supportautomation@nihva.com				REVISION -	QTY - 1
ALL DIMENSION ARE IN mm		A3		SCALE	SHEET 16 OF 28

ITEM NO.	PART NUMBER	DESCRIPTION	QTY.
1	L PLATE	SS304- 91X106X3 MM THK	8
2	RR_rivet_iso_15977_4_x_16_0 ss	RIVET M4X16	80

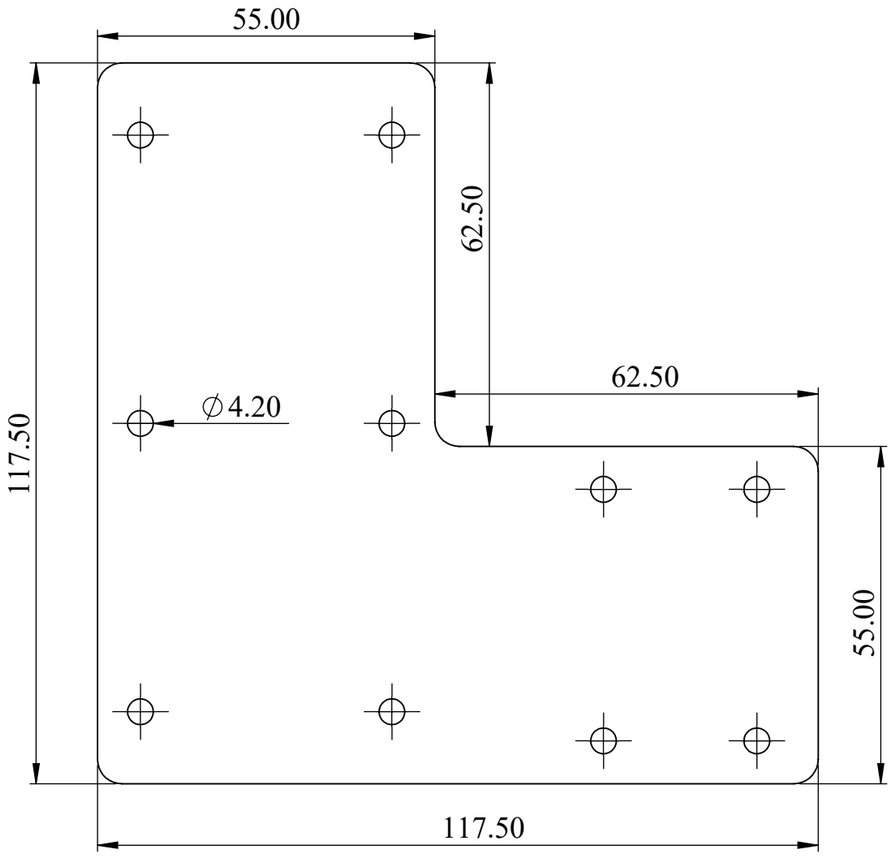


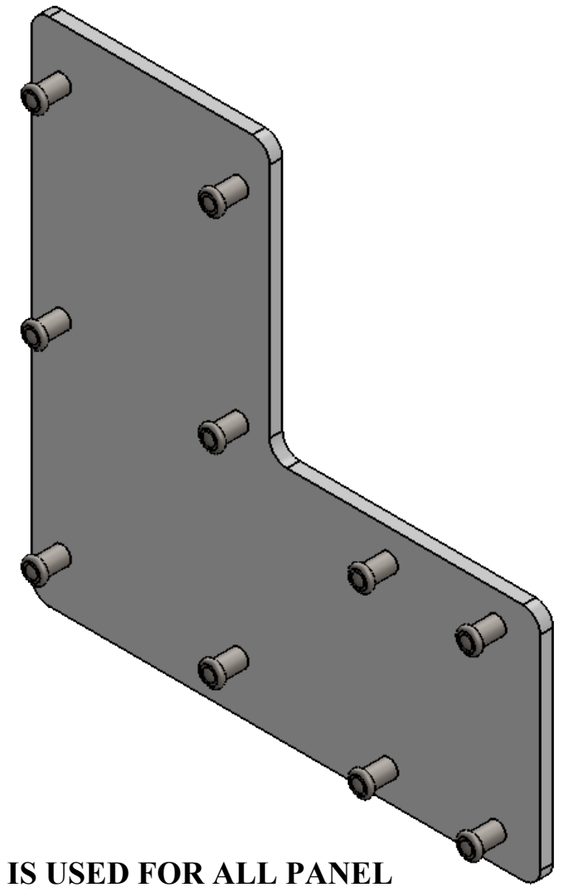


NOTE :
L PLATE
THIS L PLATE IS USED FOR ALL PANEL
LASER CUTTING
ONE PANEL QTY REQ - 8 No's
TOTAL REQ - 16 No'S
THK - 3MM

TITLE - ROOF AUTOMATION				NIHVA TECHNOLOGIES PVT.LTD.PUNE
DWG NO - NTPL-000-PM-001-02-05-05				Website - www.nihva.com
	NAME	SIGNATURE	DATE	PROJECT NO - NTPL-000-PM
DRAWN	V.W		27-05-2025	PRODUCT - RETRACTABLE ROOF
CHK'D	S.W.		27-05-2025	SITE LOCATION - LUCKNOW
APPV'D	V.T.		27-05-2025	
if any queries contact - supportautomation@nihva.com				REVISION - QTY - 1
ALL DIMENSION ARE IN mm		A3		SCALE SHEET 17 OF 28

ITEM NO.	PART NUMBER	DESCRIPTION	QTY.
1	L ANGLE PLATE	SS304 - 60X60X3 MM	12
2	RR_02-PRJ-LUCKANOW SALAVI MAM rivet_iso_15977_4_x_16_0	RIVET M4X16	96

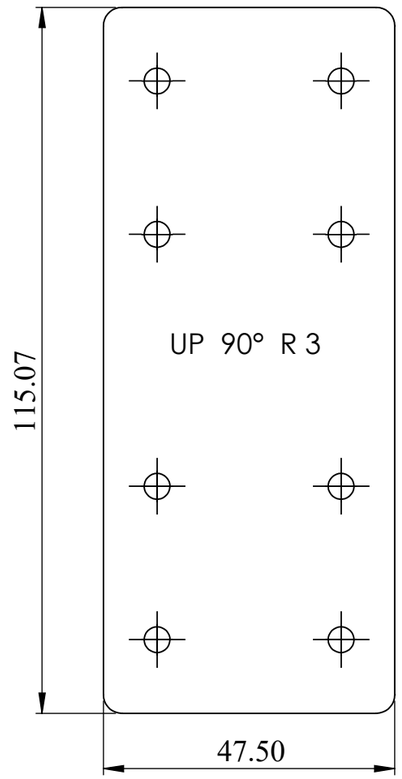


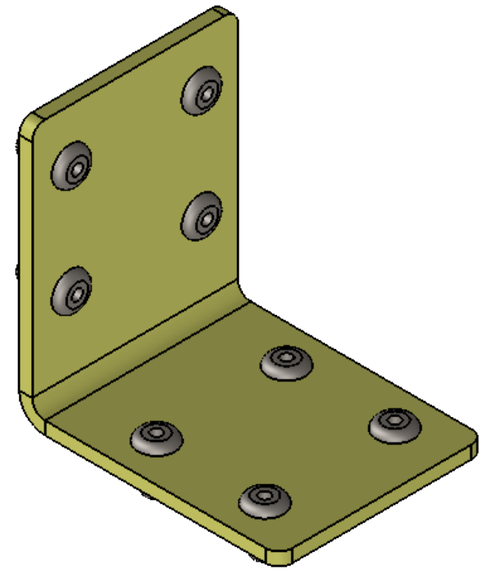


NOTE :
L ANGLE PLATE
THIS L ANGLE PLATE IS USED FOR ALL PANEL
LASER CUTTING
ONE PANEL QTY REQ - 12 No's
TOTAL REQ - 24 No'S
THK - 3MM

TITLE - ROOF AUTOMATION				NIHVA TECHNOLOGIES PVT.LTD.PUNE
DWG NO - NTPL-000-PM-001-02-06-06				Website - www.nihva.com
	NAME	SIGNATURE	DATE	PROJECT NO - NTPL-000-PM
DRAWN	V.W		27-05-2025	PRODUCT - RETRACTABLE ROOF
CHK'D	S.W.		27-05-2025	SITE LOCATION - LUCKNOW
APPV'D	V.T.		27-05-2025	
if any queries contact - supportautomation@nihva.com				REVISION - QTY - 1
ALL DIMENSION ARE IN mm		A3		SCALE SHEET 18 OF 28

ITEM NO.	PART NUMBER	DESCRIPTION	QTY.
1	RR_L ANGLE PLATE CORNNER JOINING PLATE	AL JOINING PLATE	1
		Sheet	1

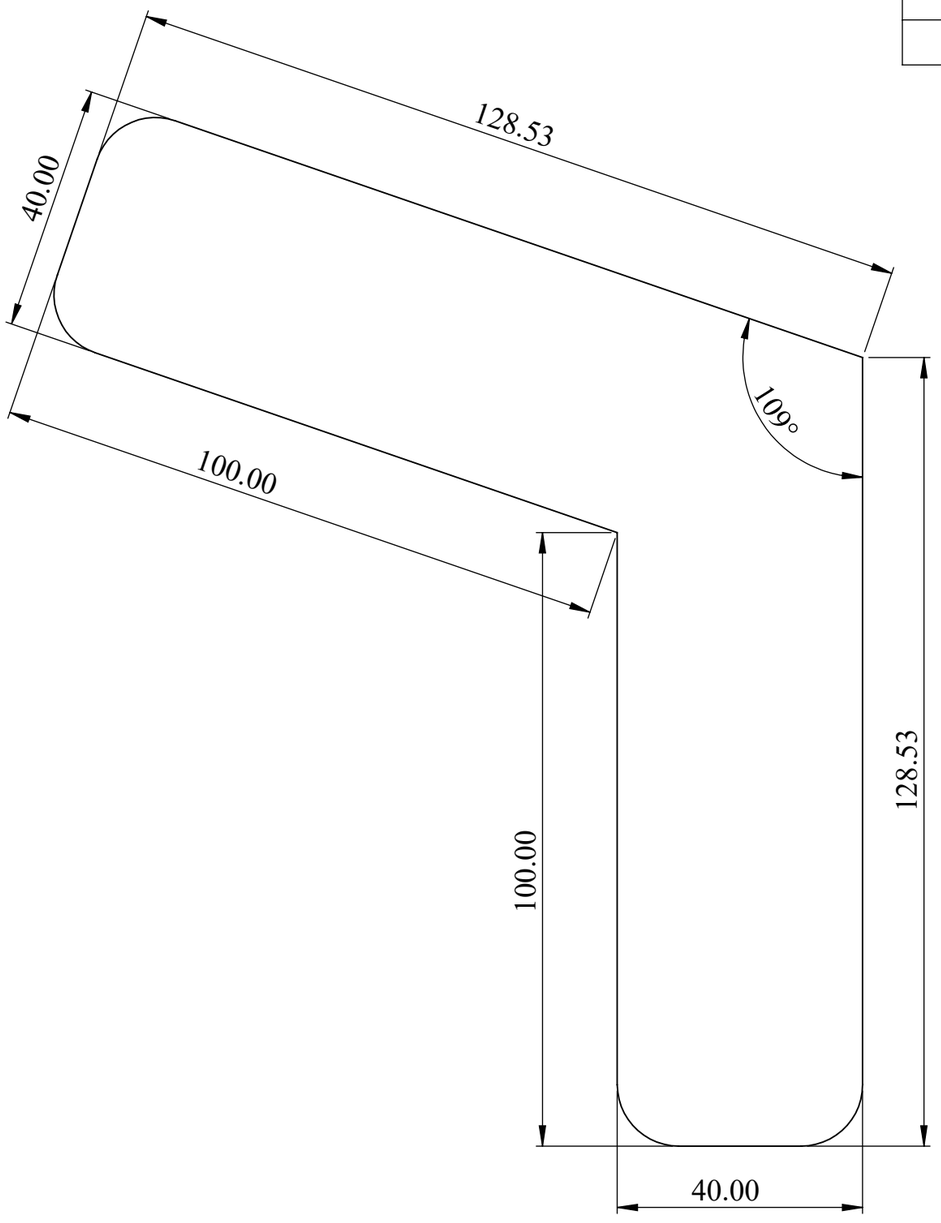


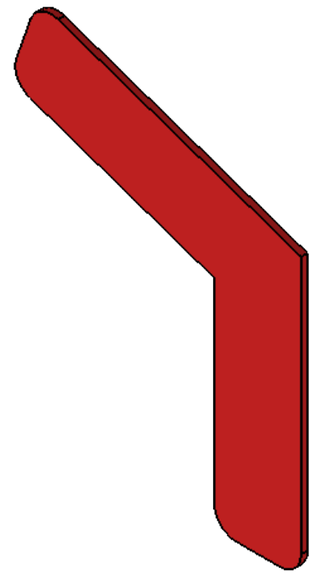


NOTE :
L ANGLE CORNER JOINING PLATE
THIS L ANGLE CORNER JOINING PLATE IS USED FOR ALL PANEL LASER CUTTING
ONE PANEL QTY REQ - 4 No's
TOTAL REQ - 8 No'S
THK - 3MM


TITLE - ROOF AUTOMATION				NIHVA TECHNOLOGIES PVT.LTD.PUNE
DWG NO - NTPL-000-PM-001-02-07-07				Website - www.nihva.com
	NAME	SIGNATURE	DATE	PROJECT NO - NTPL-000-PM
DRAWN	V.W		27-05-2025	PRODUCT - RETRACTABLE ROOF
CHK'D	S.W.		27-05-2025	SITE LOCATION - LUCKNOW
APPV'D	V.T.		27-05-2025	
if any queries contact - supportautomation@nihva.com				REVISION - QTY - 1
ALL DIMENSION ARE IN mm		A3		SCALE SHEET 19 OF 28

ITEM NO.	PART NUMBER	DESCRIPTION	QTY.
1	RR_ENCLOSURE NO 01		1

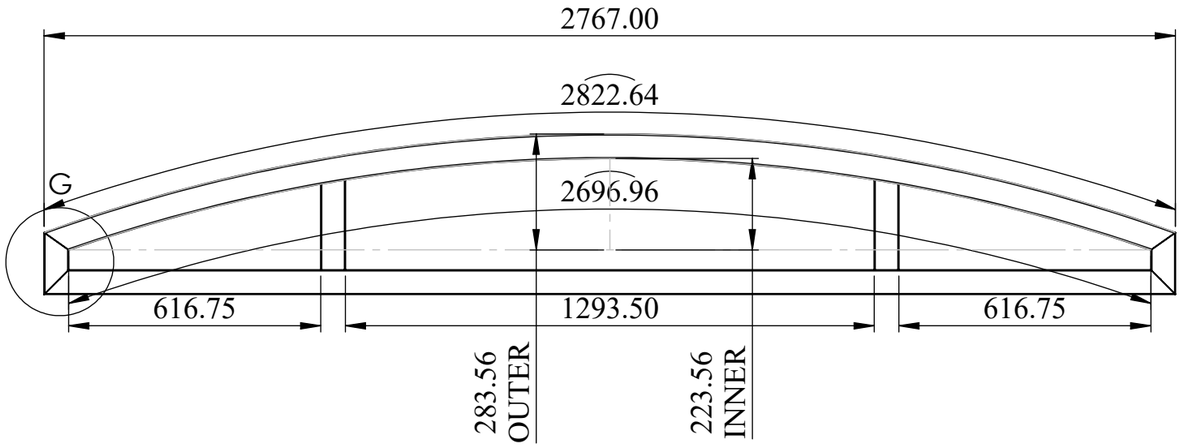

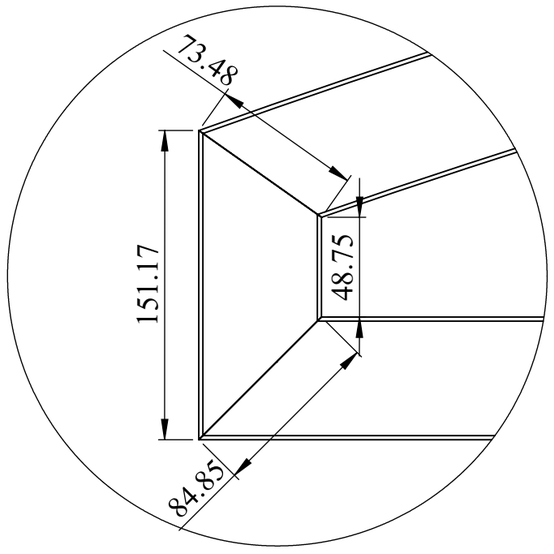


DETAIL G
SCALE 1 : 3

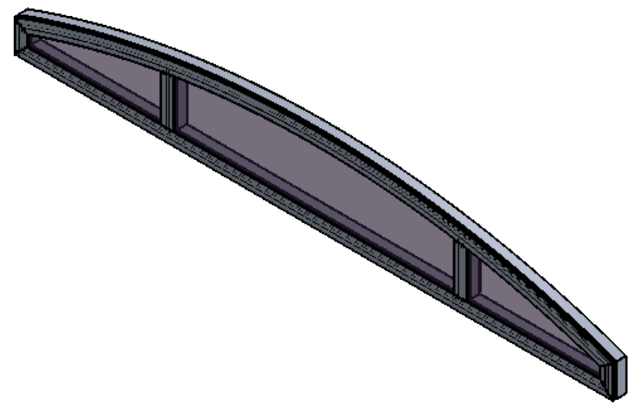


NOTE :
PANEL NO 01 ENCLOSER
ENCLOSER NO 01

TITLE - ROOF AUTOMATION				NIHVA TECHNOLOGIES PVT.LTD.PUNE
DWG NO - NTPL-000-PM-001-02-08-08				Website - www.nihva.com
	NAME	SIGNATURE	DATE	PROJECT NO - NTPL-000-PM
DRAWN	V.W		27-05-2025	PRODUCT - RETRACTABLE ROOF
CHK'D	S.W.		27-05-2025	SITE LOCATION - LUCKNOW
APPV'D	V.T.		27-05-2025	
if any queries contact - supportautomation@nihva.com				REVISION - QTY - 1
ALL DIMENSION ARE IN mm			A3	SCALE SHEET 20 OF 28

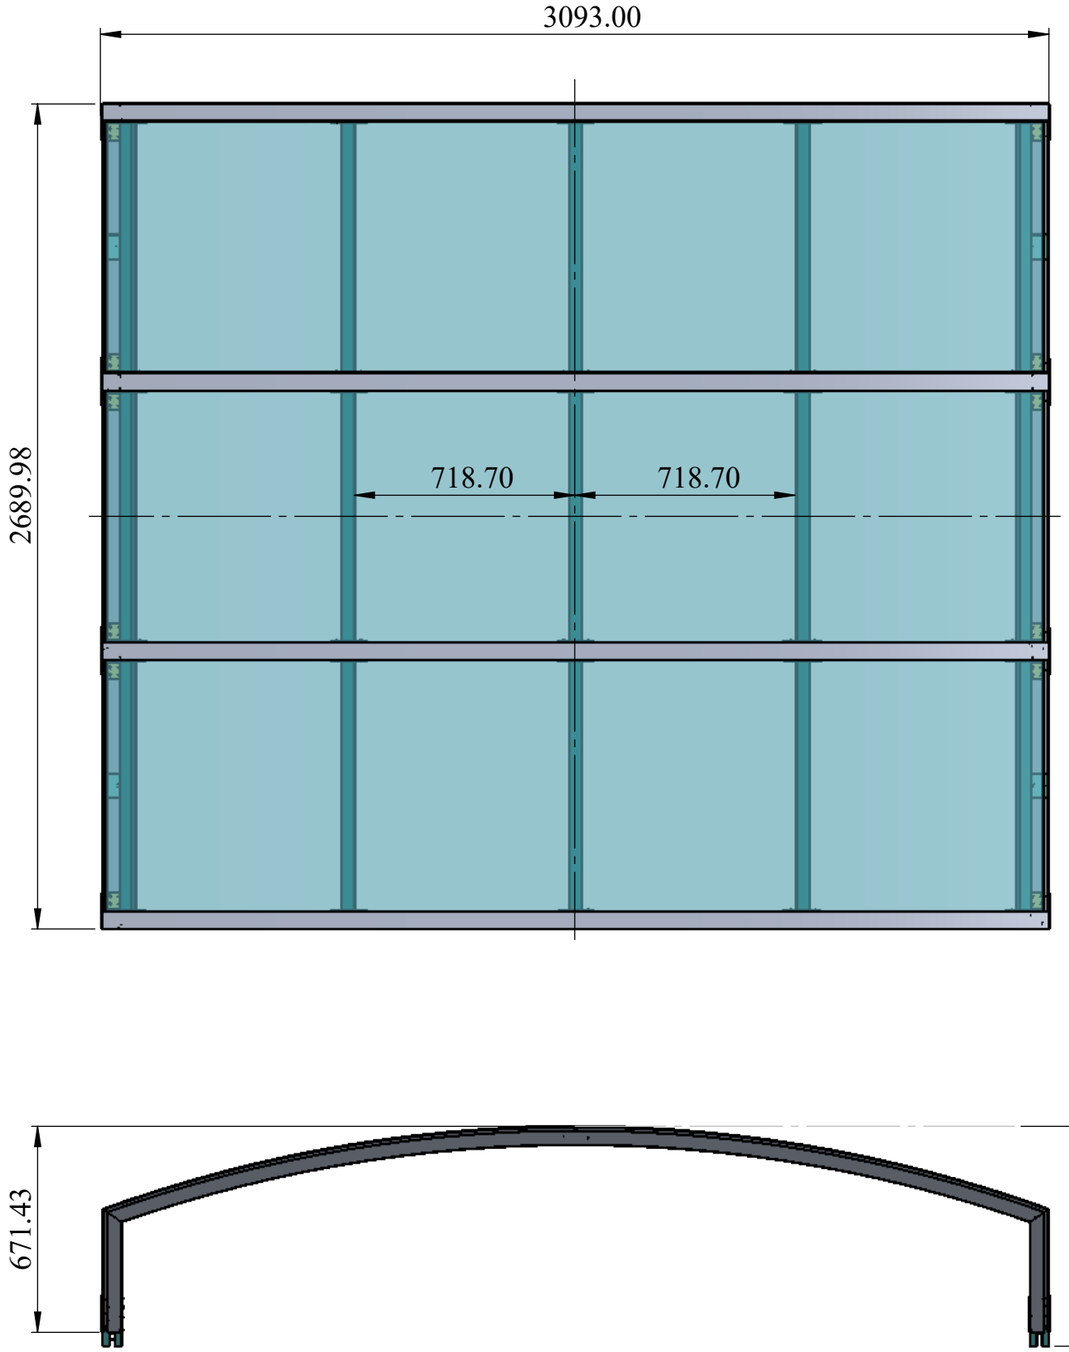



ITEM NO.	PART NUMBER	DESCRIPTION	QTY.
1	RR_ PANEL 2		1
2	AL Support tube SQ TUBE 40X40X1.5 MM L-816.66MM	AL INTERMEDIAT SUPPORT TUBE	15
3	RR_ BEARING BLOCK ASM WITH SHOULDER BOLT	SLIDING BLOCK	4
4	T PLATE	JOINING PLATE	8
5	L PLATE	JOINING PLATE	8
6	L ANGLE PLATE	JOINING PLATE	12
7	L ANGLE CORNER JOINING PLATE		4
8	RR_ PANEL 2 polycarbonet sheet		3

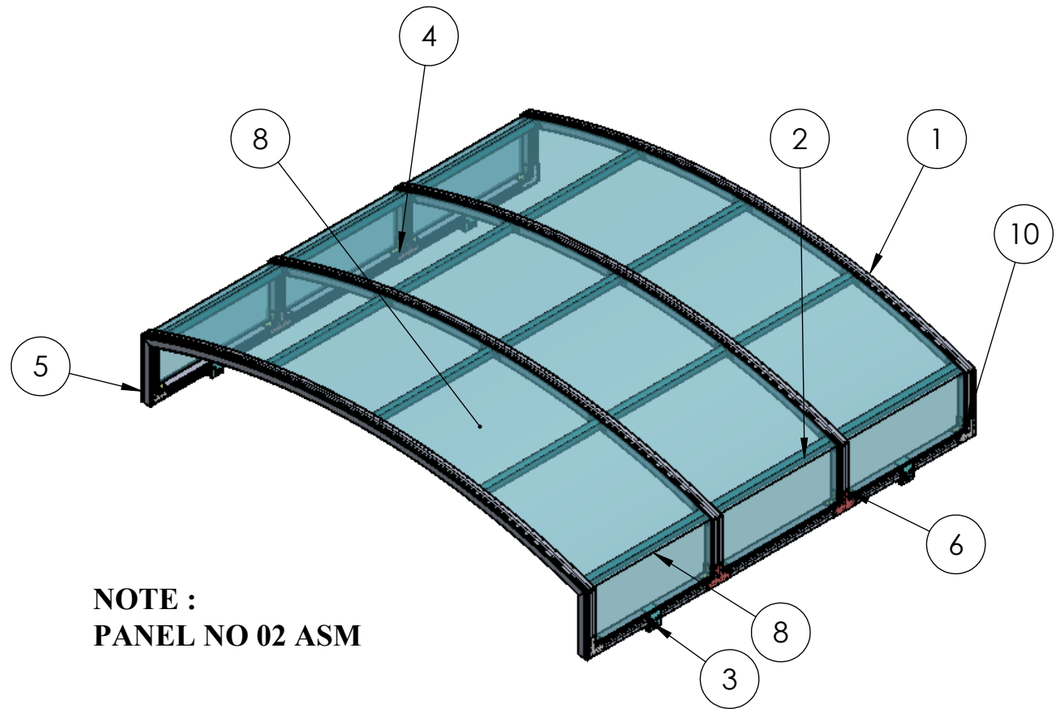


NOTE :
PANEL NO 02 ASM


TITLE - ROOF AUTOMATION				NIHVA TECHNOLOGIES PVT.LTD.PUNE
DWG NO - NTPL-000-PM-001-02-02-02				Website - www.nihva.com
	NAME	SIGNATURE	DATE	PROJECT NO - NTPL-000-PM
DRAWN	V.W		27-05-2025	PRODUCT - RETRACTABLE ROOF
CHK'D	S.W.		27-05-2025	SITE LOCATION - LUCKNOW
APPV'D	V.T.		27-05-2025	
if any queries contact - supportautomation@nihva.com				REVISION - QTY - 1
ALL DIMENSION ARE IN mm		A3		SCALE SHEET 21 OF 28

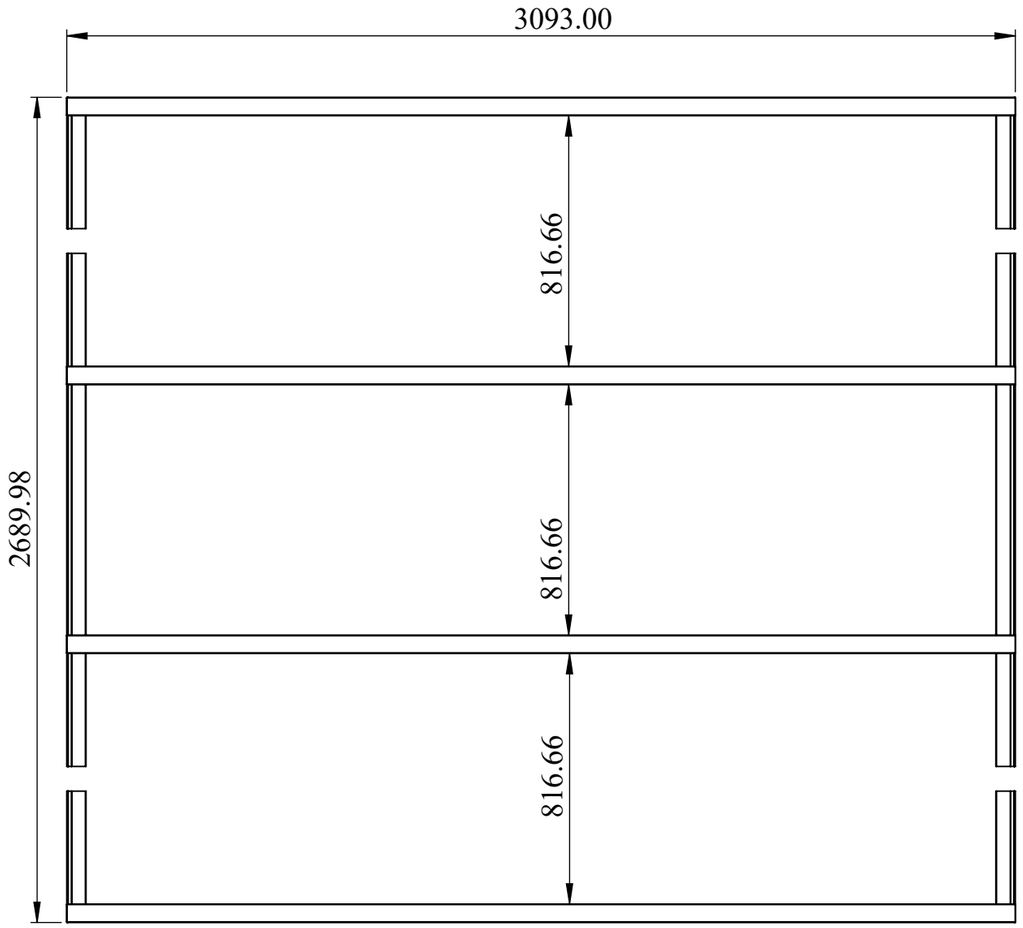

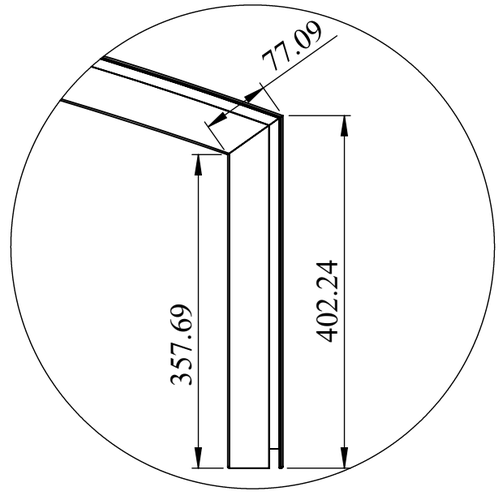

DETAIL H
SCALE 1 : 7

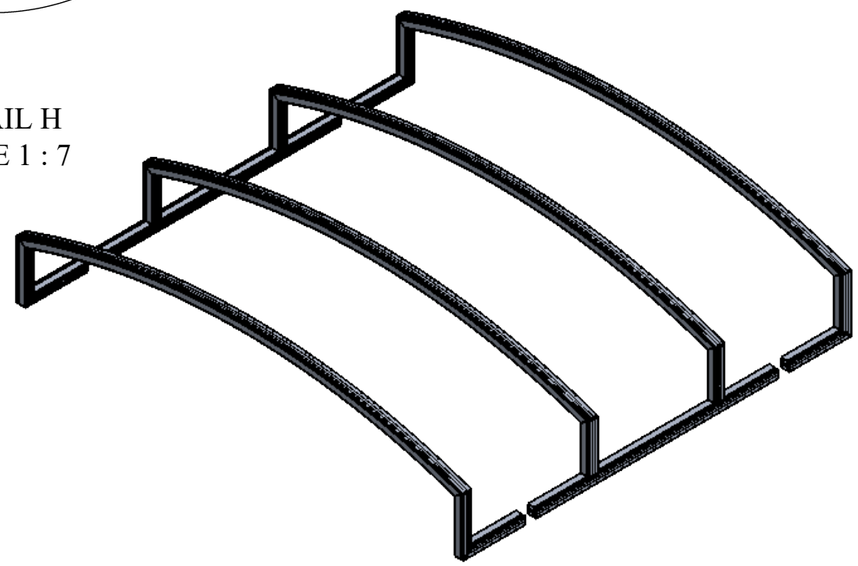


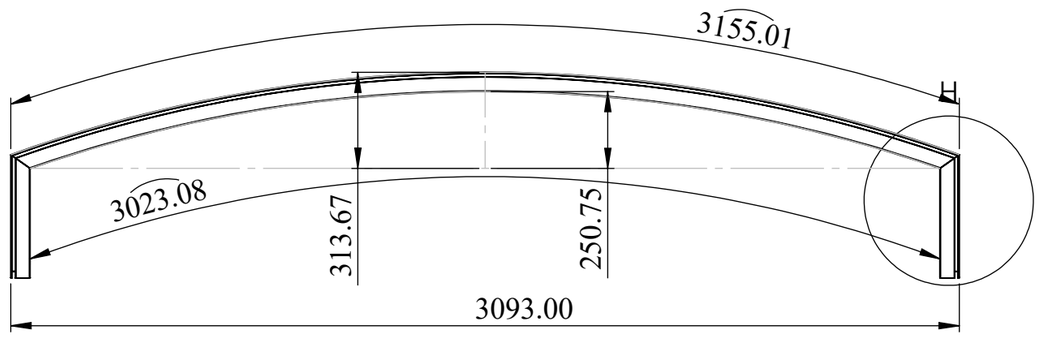


NOTE :
PANEL NO 1


TITLE - ROOF AUTOMATION				NIHVA TECHNOLOGIES PVT.LTD.PUNE
DWG NO - NTPL-000-PM-001-02-01-01				Website - www.nihva.com
	NAME	SIGNATURE	DATE	PROJECT NO - NTPL-000-PM
DRAWN	V.W		27-05-2025	PRODUCT - RETRACTABLE ROOF
CHK'D	S.W.		27-05-2025	SITE LOCATION - LUCKNOW
APPV'D	V.T.		27-05-2025	
if any queries contact - supportautomation@nihva.com				REVISION - QTY - 1
ALL DIMENSION ARE IN mm			A3	SCALE SHEET 22 OF 28

ITEM NO.	PART NUMBER	DESCRIPTION	QTY.
1	RR_ENCLOSURE NO 02		1

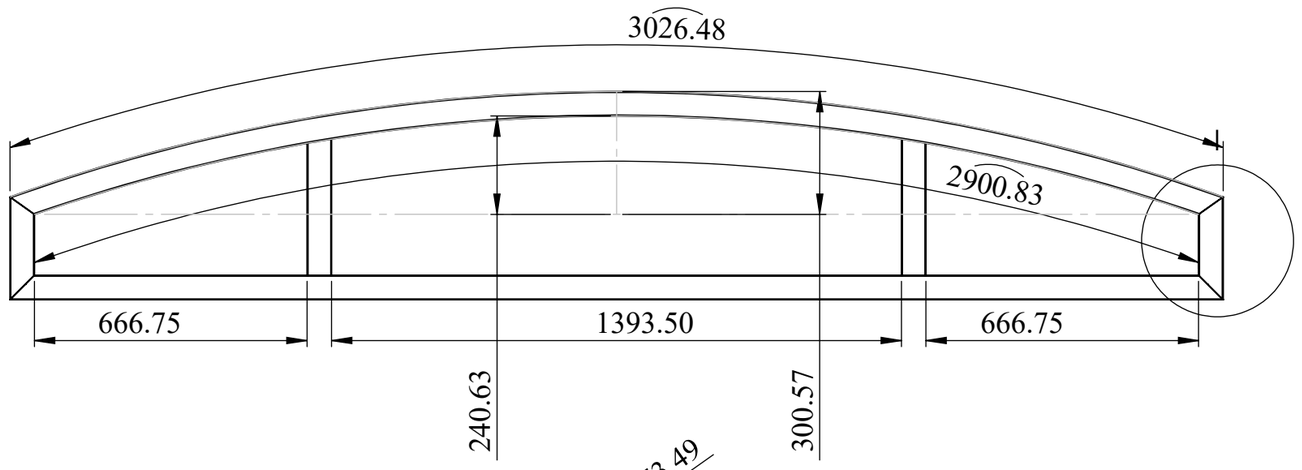

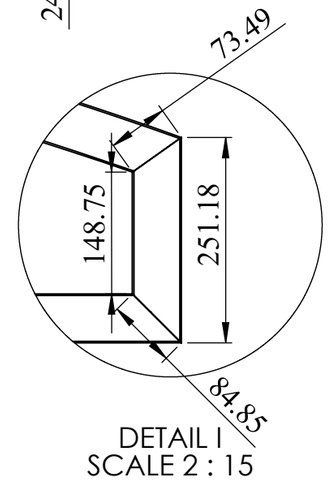



DETAIL I
SCALE 2 : 15

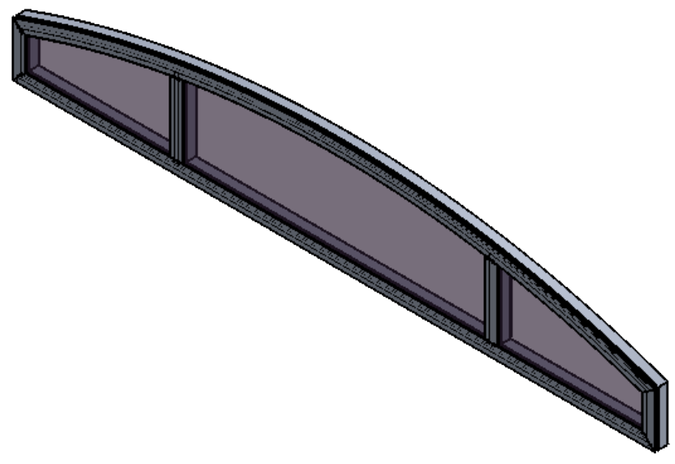

TITLE - ROOF AUTOMATION				NIHVA TECHNOLOGIES PVT.LTD.PUNE Website - www.nihva.com
DWG NO - NTPL-000-PM-001-02-07-07				
	NAME	SIGNATURE	DATE	PROJECT NO - NTPL-000-PM
DRAWN	V.W		27-05-2025	PRODUCT - RETRACTABLE ROOF
CHK'D	S.W.		27-05-2025	SITE LOCATION - LUCKNOW
APPV'D	V.T.		27-05-2025	
if any queries contact - supportautomation@nihva.com				REVISION - QTY - 1
ALL DIMENSION ARE IN mm			A3	SCALE SHEET 23 OF 28

ITEM NO.	PART NUMBER	DESCRIPTION	QTY.
1	RR_NICE RB 600		1

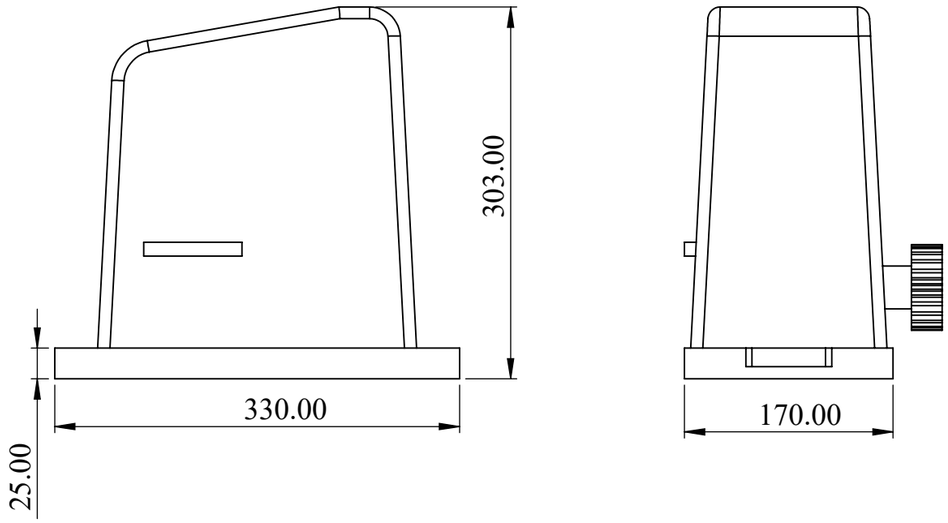


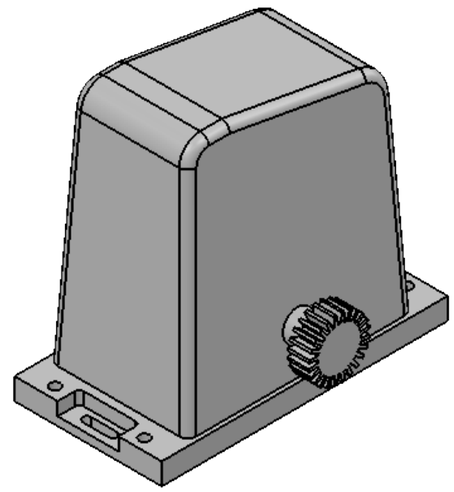



NOTE ;
MOTOR - NICE RB 600

TITLE - ROOF AUTOMATION				NIHVA TECHNOLOGIES PVT.LTD.PUNE
DWG NO - NTPL-000-PM-001-06-00-06				Website - www.nihva.com
	NAME	SIGNATURE	DATE	PROJECT NO - NTPL-000-PM
DRAWN	V.W		27-05-2025	PRODUCT - RETRACTABLE ROOF
CHK'D	S.W.		27-05-2025	SITE LOCATION - LUCKNOW
APPV'D	V.T.		27-05-2025	
if any queries contact - supportautomation@nihva.com				REVISION - QTY - 1
ALL DIMENSION ARE IN mm		A3		SCALE SHEET 24 OF 28

ITEM NO.	PART NUMBER	DESCRIPTION	QTY.
1	MOTOR MTG BRACKET NICE 1T	MS	1
		Sheet	1

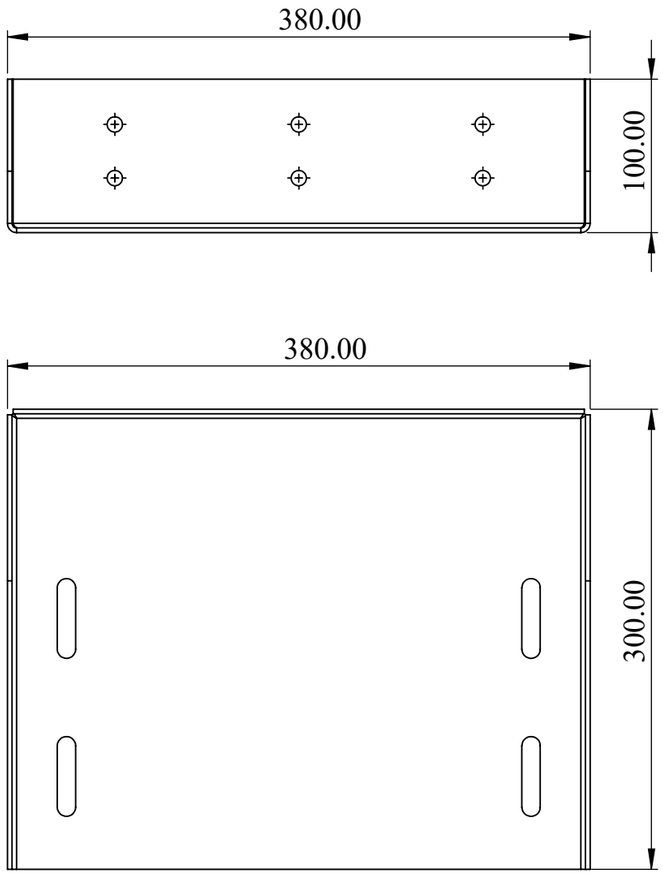


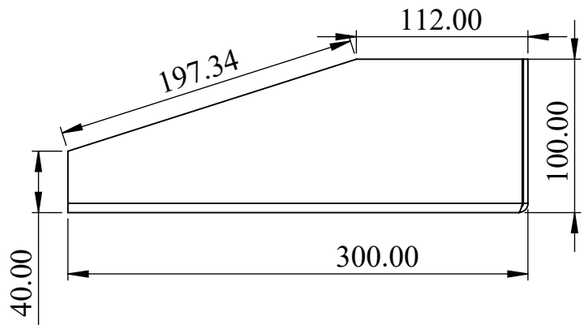


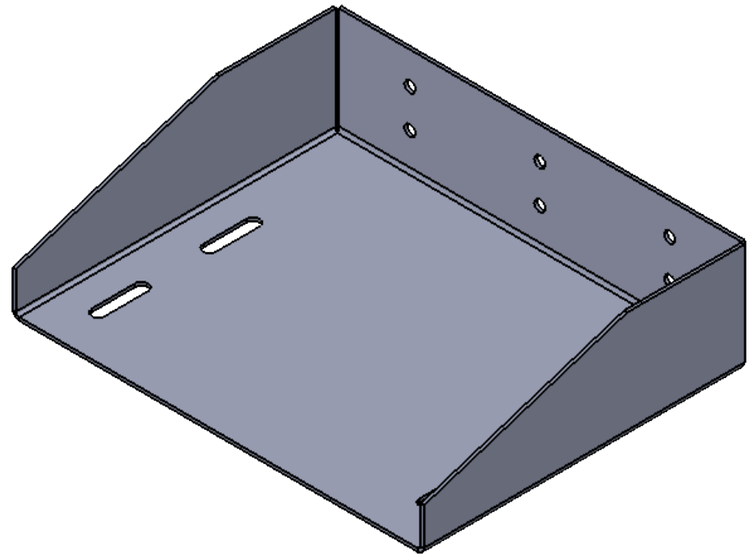


NOTE :
MOTOR BRACKET
MOTOR BRACKET DIMENSIONS FOR 600 KG NICE MOTOR IS SAME AS 1000 KG NICE MOTOR BRACKET

TITLE - ROOF AUTOMATION				NIHVA TECHNOLOGIES PVT.LTD.PUNE
DWG NO - NTPL-000-PM-001-02-06-06				Website - www.nihva.com
	NAME	SIGNATURE	DATE	PROJECT NO - NTPL-000-PM
DRAWN	V.W		27-05-2025	PRODUCT - RETRACTABLE ROOF
CHK'D	S.W.		27-05-2025	SITE LOCATION - LUCKNOW
APPV'D	V.T.		27-05-2025	
if any queries contact - supportautomation@nihva.com				REVISION - QTY - 1
ALL DIMENSION ARE IN mm		A3		SCALE SHEET 25 OF 28

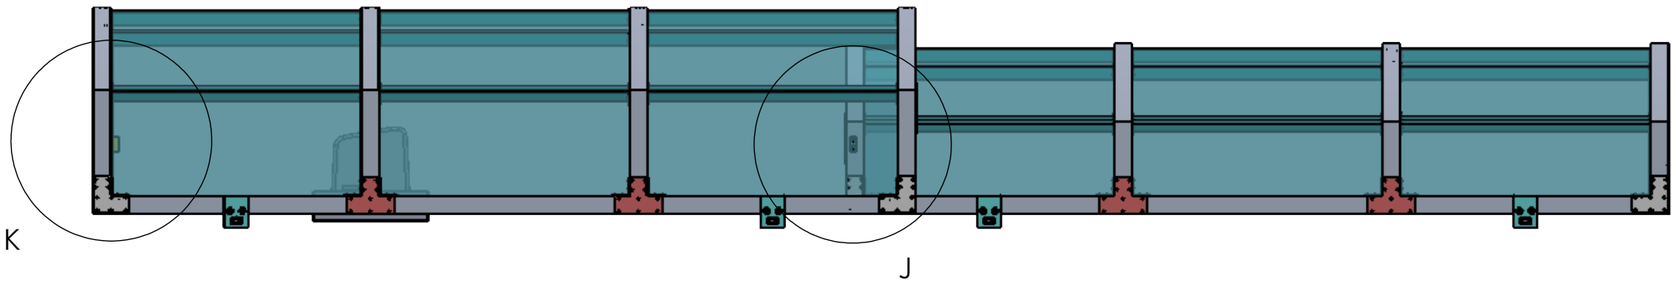

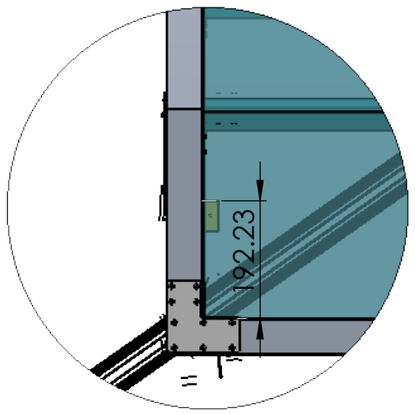

DETAIL K
SCALE 1 : 10

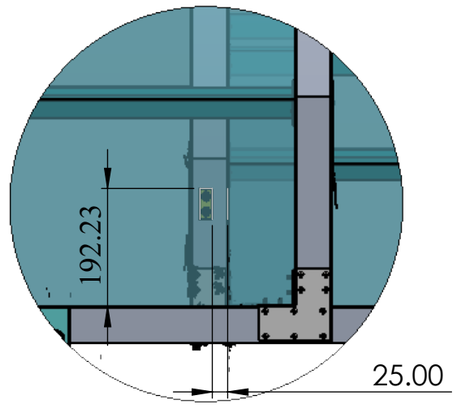



DETAIL J
SCALE 1 : 10

NOTE :
SUB ASSEMBLY NO 03
NYLON STOPPER ASM

TITLE - ROOF AUTOMATION				NIHVA TECHNOLOGIES PVT.LTD.PUNE
DWG NO - NTPL-000-PM-001-02-09-09				Website - www.nihva.com
	NAME	SIGNATURE	DATE	PROJECT NO - NTPL-000-PM
DRAWN	V.W		27-05-2025	PRODUCT - RETRACTABLE ROOF
CHK'D	S.W.		27-05-2025	SITE LOCATION - LUCKNOW
APPV'D	V.T.		27-05-2025	
if any queries contact - supportautomation@nihva.com				REVISION - QTY - 1
ALL DIMENSION ARE IN mm		A3		SCALE SHEET 26 OF 28

ITEM NO.	PART NUMBER	DESCRIPTION	QTY.
1	NYLON STOPPER		4

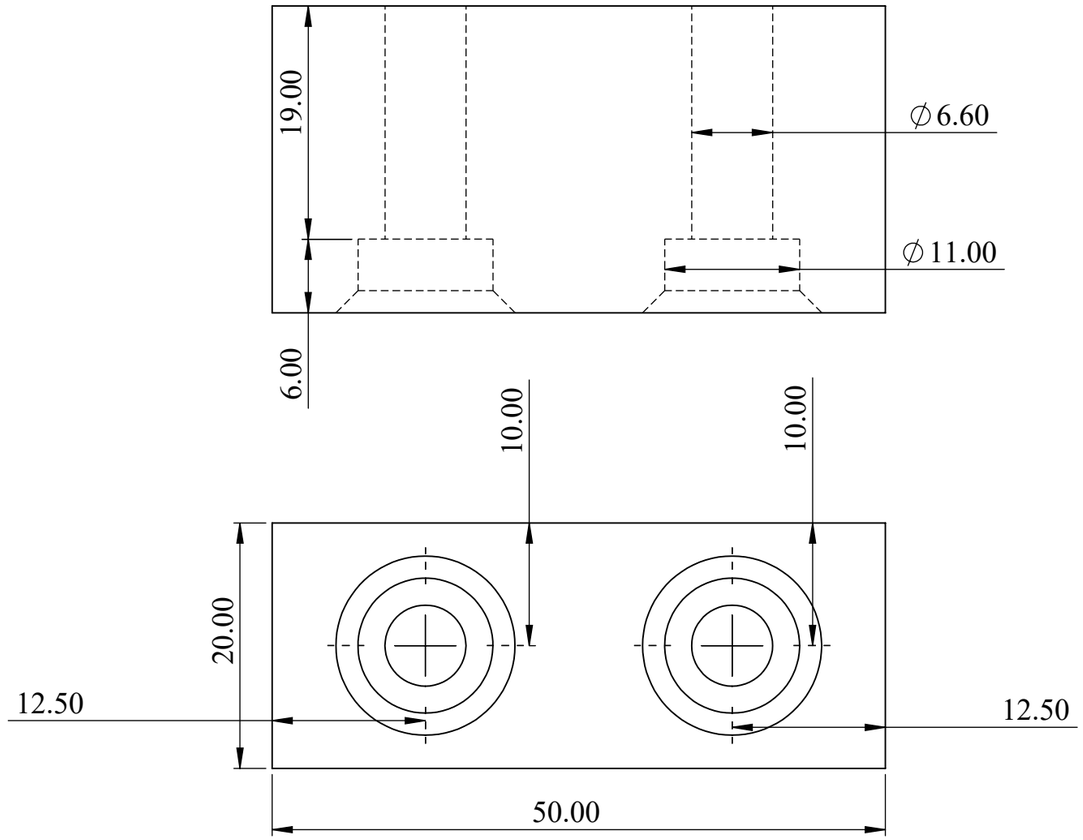


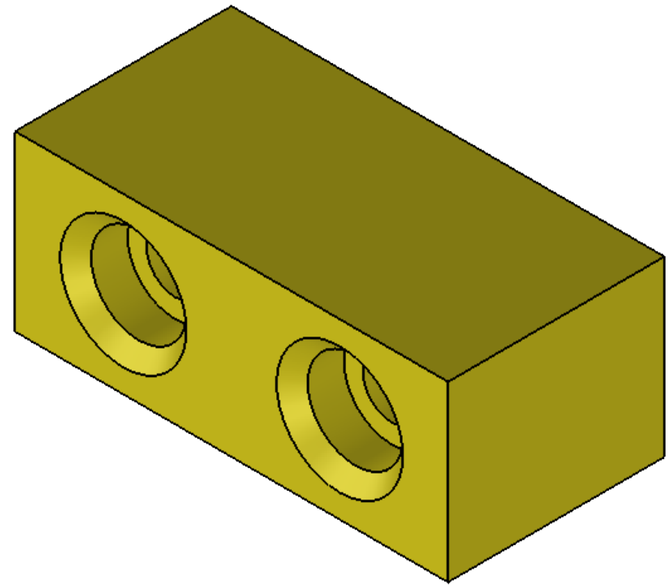


NOTE :
NYLON STOPPER

TITLE - ROOF AUTOMATION				NIHVA TECHNOLOGIES PVT.LTD.PUNE
DWG NO - NTPL-000-PM-001-03-01-10				Website - www.nihva.com
	NAME	SIGNATURE	DATE	PROJECT NO - NTPL-000-PM
DRAWN	V.W		27-05-2025	PRODUCT - RETRACTABLE ROOF
CHK'D	S.W.		27-05-2025	SITE LOCATION - LUCKNOW
APPV'D	V.T.		27-05-2025	
if any queries contact - supportautomation@nihva.com				REVISION - QTY - 1
ALL DIMENSION ARE IN mm		A3		SCALE SHEET 27 OF 28

ITEM NO.	PART NUMBER	DESCRIPTION	QTY.
1	IS 2269 - M6 x 40-N		8

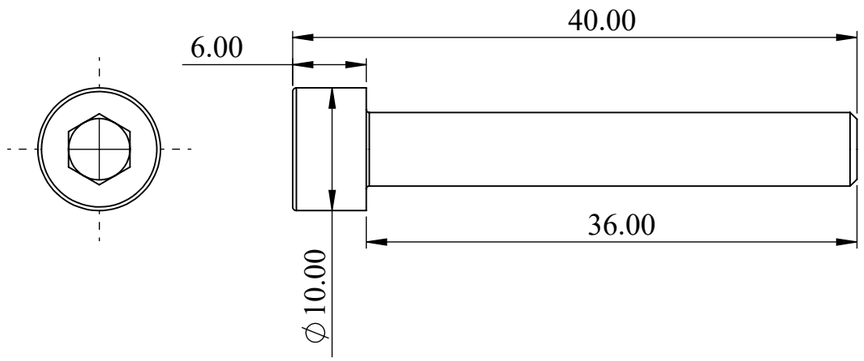

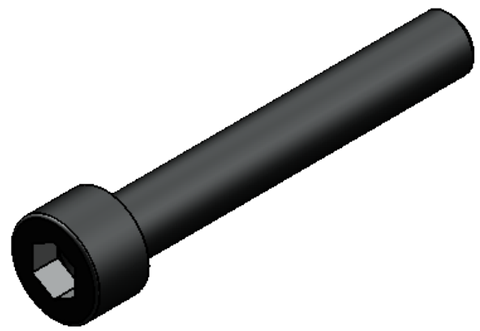

NOTE :
ALLEN BOLT M6x40MM

TITLE - ROOF AUTOMATION				NIHVA TECHNOLOGIES PVT.LTD.PUNE
DWG NO - NTPL-000-PM-001-03-02-10				Website - www.nihva.com
	NAME	SIGNATURE	DATE	PROJECT NO - NTPL-000-PM
DRAWN	V.W		27-05-2025	PRODUCT - RETRACTABLE ROOF
CHK'D	S.W.		27-05-2025	SITE LOCATION - LUCKNOW
APPV'D	V.T.		27-05-2025	
if any queries contact - supportautomation@nihva.com				REVISION - QTY - 1
ALL DIMENSION ARE IN mm		A3		SCALE SHEET 28 OF 28