

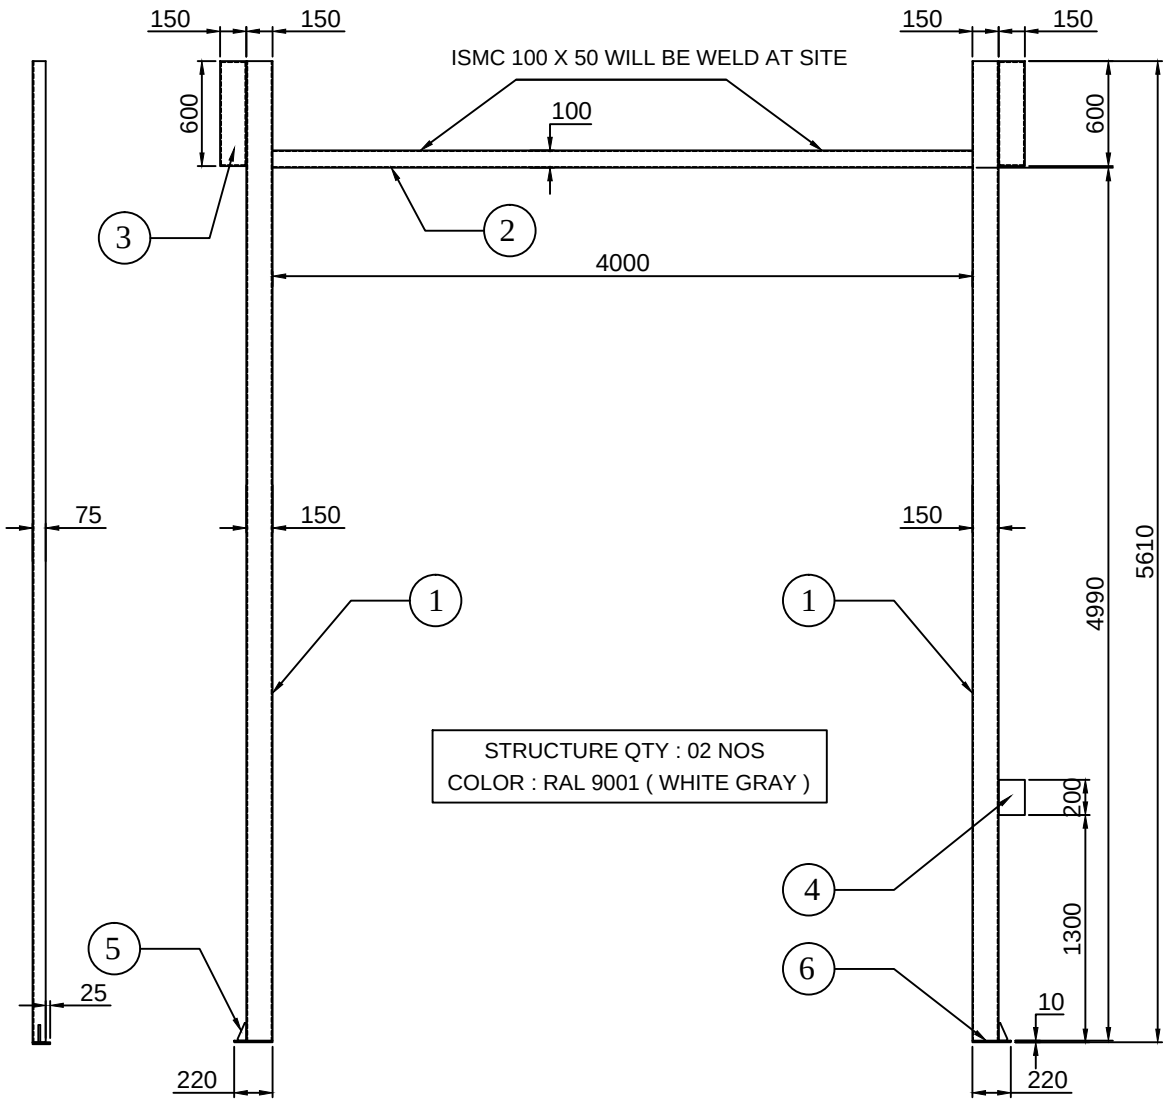


STRUCTURE QTY : 02 NOS
COLOR : RAL 9001 (WHITE GRAY)

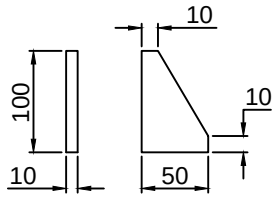

5

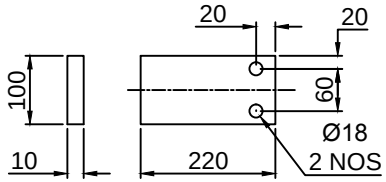

6

TOLERANCE - ±10mm

SR. NO	DESCRIPTION	SPECIFICATION	QTY
06	FLAT	100 X 10 THK X 220L	2 NOS
05	RIB	50 X 10THK X 100L	2 NOS
04	FLAT	150 X 6THK X 200L	1 NO
03	ISMC	150 X 75 X 600L	2 NOS
02	ISMC	100 X 50 X 4000L	1 NO
01	ISMC	150 X 75 X 5600L	2 NOS

This drawing & design is the property of NIHVA TECHNOLOGIES. Not to be sold or copied to any other concern.

TITLE
STRUCTURE FOR MOTORIZED ROLLING SHUTTER

NIHVA TECHNOLOGIES PVT. LTD.

NIHVA TECHNOLOGIES PVT. LTD. PUNE
Tel : 020 66304033
Email:- info@nihva.com
Website:- www.nihva.com

	NAME	SIGN	DATE
DRAWN	P.A		09.01.2020
CHECK	G.J		09.01.2020
APPRD.			

CLIENT -
PROJECT-
SITE LOCATION -
If any queries contact : design@nihva.com
DWG. NO. : NIHVA/19-20/VDR/279
REV- 00
ALL DIMENSION ARE IN mm
SCALE: NTS
WT:
SHEET: 01 OF 01