

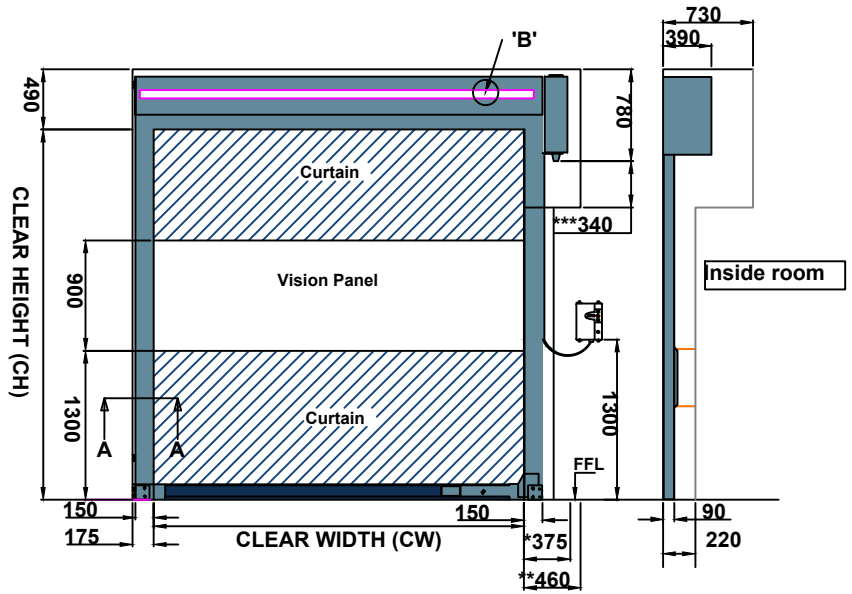


INSIDE ELEVATION

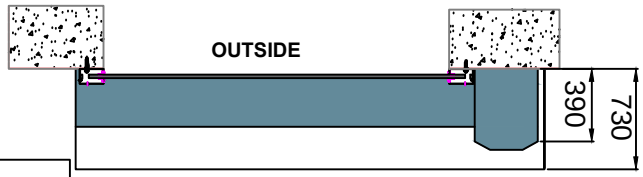


INSIDE HORIZONTAL SECTION


* Space for fiting the door
** Space require for fit and dismantle the operator
*** For Emergency Crank Handle

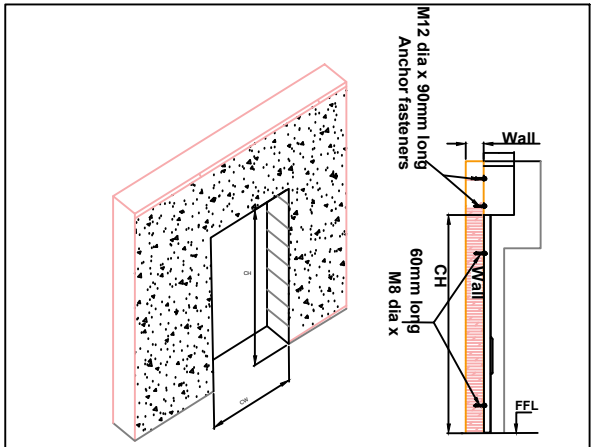

FIXING ON CONCRETE

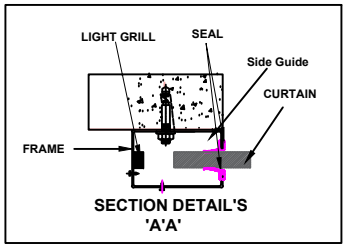

SECTION DETAIL'S 'A'A'

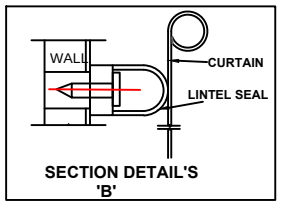

SECTION DETAIL'S 'B'

ELCTRICAL REQUIREMENT FROM CLIENT AT SITE-

1) 16A 3 Pin Industrial type female Metal clad socket 230V, 50Hz, with earthing around 1/2 Meter From Controller
2) Clean Uninterrupted Power Supply WithOut Voltage Fluctuations Needed.
3) Solid State Inline (UPS/Stabilizer) 2kva Capacity Required

Notes:

1) Operator is Always on Right side as Standard
2) Controller is Always On Operator Side
3) If Required Civil work is in client scope.

3650 MM	4400 MM	1 NO	RAL 5010	ON CONCRETE
CLEAR WIDTH (CW)	CLEAR HEIGHT (CH)	QTY	RAL COLOUR CURTAIN PANEL	MOUNTING

This drawing & design is the property of NIHVA TECHNOLOGIES. Not to be sold or copied to any other concern.

TITLE- HIGH SPEED DOOR

NIHVA TECHNOLOGIES PVT. LTD.
NIHVA TECHNOLOGIES PVT. LTD. PUNE
Tel : 020 66304033
Email:- info@nihva.com
Website:- www.nihva.com

	NAME	SIGN	DATE
DRAWN	SIDDHESHWAR		1.12.2020
CHECK	A.K.		1.12.2020
APPRD.			

CLIENT - CONGLOMERATE
PROJECT - CONGLOMERATE
SITE LOCATION - PUNE
If any queries contact : projectsupport@nihva.com
DWG. NO. : NIHVA/20-21/0097 REV- R00
ALL DIMENSION ARE IN mm
SCALE: NTS WT: SHEET: