


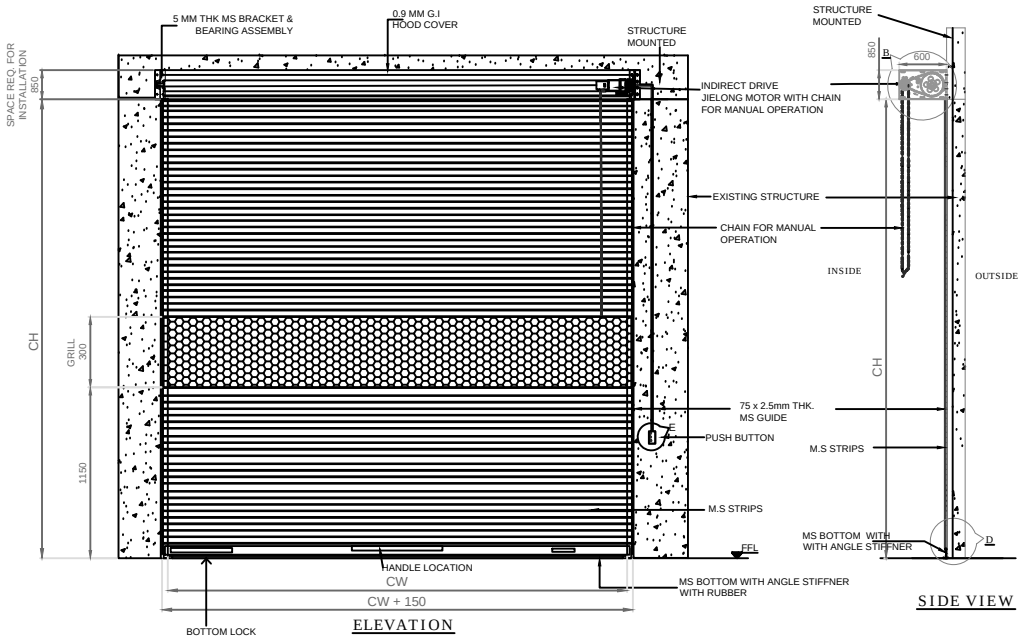


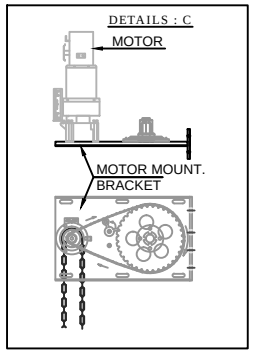


DETAILS : A & B

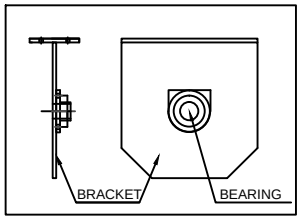


DETAILS : C
5 MM THK SHAFT BRACKET

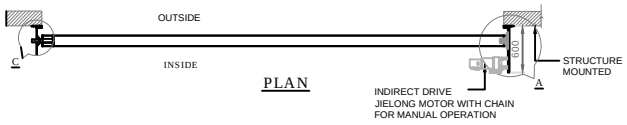


PLAN

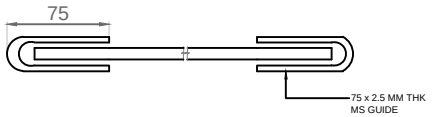


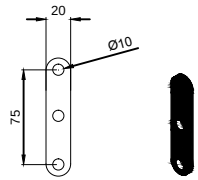

5 m m THK. LINK

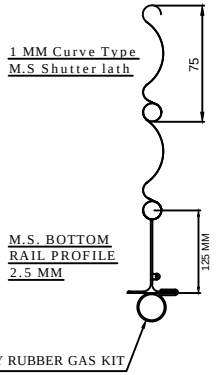

DETAILS : D

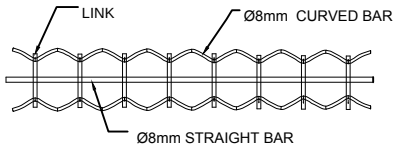

2500	2200	2
CLEAR WIDTH (CW)	CLEAR HEIGHT (CH)	QUANTITY

NOTE:
1. REQUIRED TECHNICAL M.S STRUCTURE FOR SHUTTER IN CLIENT SCOPE.
2. POWDER COATING.

RAL CODE-RAL 5002 ULTRA MARINE BLUE

REV NO	DATE	DRAWN	REMARK
R01	28.09.20	S.S.	CLEAR HEIGHT CHANGED

This drawing & design is the property of NIHVA TECHNOLOGIES. Not to be sold or copied to any other concern.

TITLE: MOTORIZED ROLLING SHUTTER

NIHVA TECHNOLOGIES PVT. LTD.

NIHVA TECHNOLOGIES PVT. LTD. PUNE
Tel : 020 66304033
Email:- info@nihva.com
Website:- www.nihva.com

	NAME	SIGN	DATE
DRAWN	S.S.		28.09.2020
CHECK	P.A		28.09.2020
APPRD.			

CLIENT -
PROJECT -
SITE LOCATION -

If any queries contact : design@nihva.com
DWG. NO. : NIHVA/20-21/VDR/0043/R01 REV- R01
ALL DIMENSION ARE IN mm
SCALE: NTS WT: SHEET: