


DRAWING

REV DESCRIPTION	DATE	REV NO
	17-05-2026	REV 00
1.		

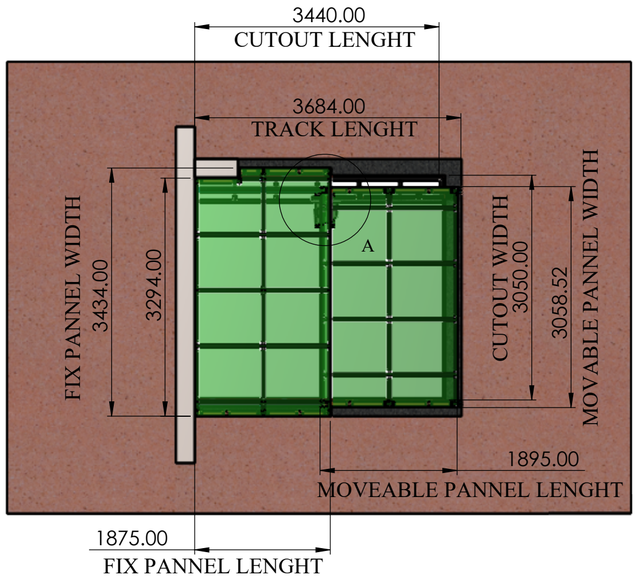


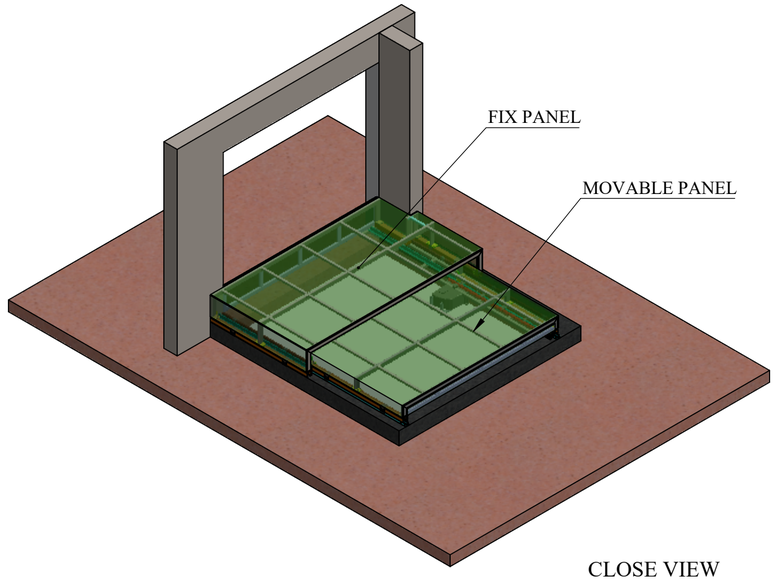


CLOSE VIEW

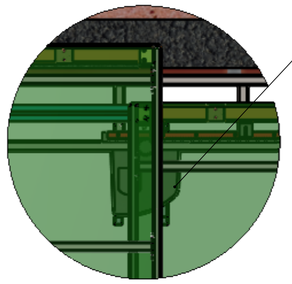

DETAIL A
SCALE 1 : 20

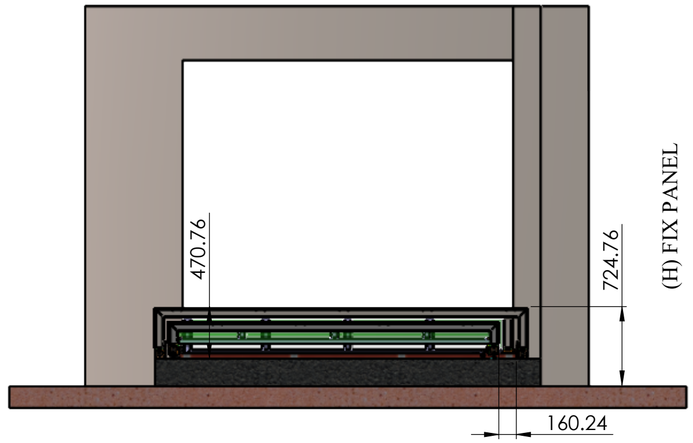

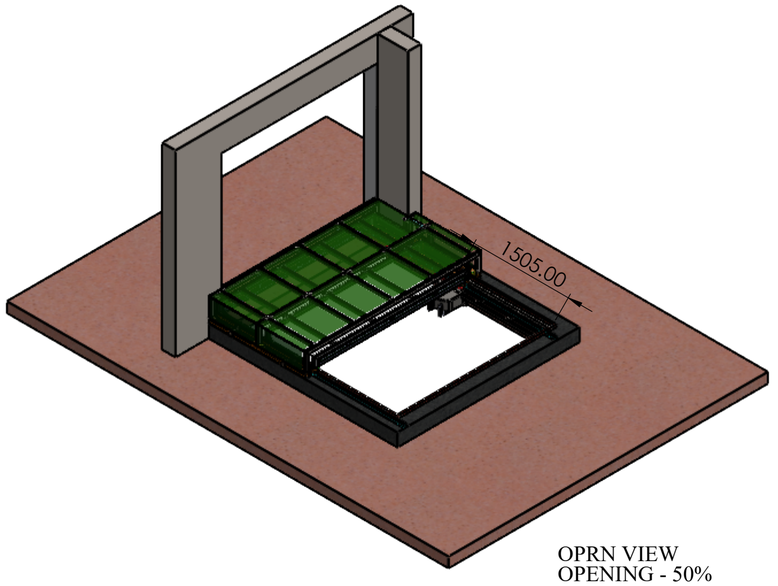

OPRN VIEW
OPENING - 50%

NOTE :
G.A. DRAWING
FOR MOTOR & TRACK MOUNTING FABRICATION REQ
ALL CIVIL WORK & FABRICATION IN CLIENT SCOPE

SPECIAL INSTRUCTION'S :

TITLE - ROOF AUTOMATION

DWG NO - NTPL-000-PM-001-00-00-00

NIHVA Technologies Pvt. Ltd.


NIHVA TECHNOLOGIES PVT.LTD.PUNE
Website - www.nihva.com


	NAME	SIGNATURE	DATE
DRAWN	V.W.		16-05-2026
CHK'D	B.S.		17-05-2026
APPV'D	V.T.		17-08-2026


PRODUCT - RETRACTABLE ROOF
PROJECT NO - NTPL-000-PM
REVISION - 00
SITE LOCATION -
WEIGHT -
MATRIAL -
QTY - 1
If any queries contact - Design@nihva.com
ALL DIMENSION ARE IN mm
A2
PROJECTION METHOD:
SCALE :
SHEET 1 OF 2


DRAWING

REV DESCRIPTION	DATE	REV NO
	16-05-2026	REV 00
1.		

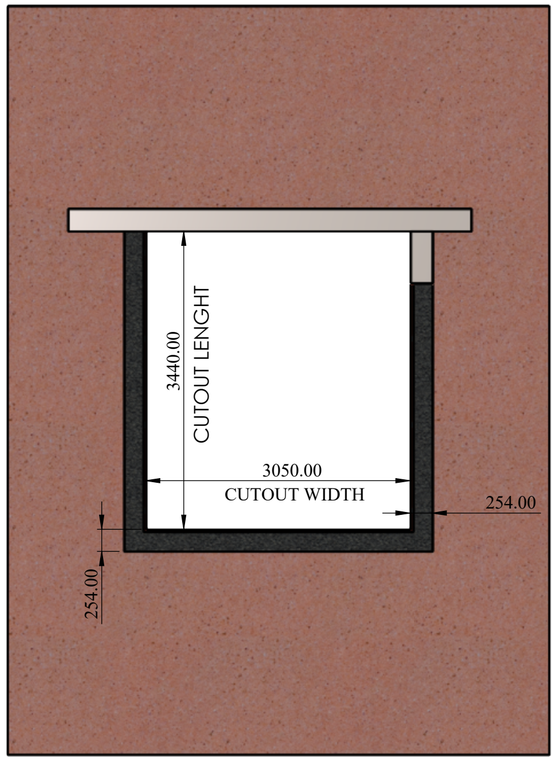

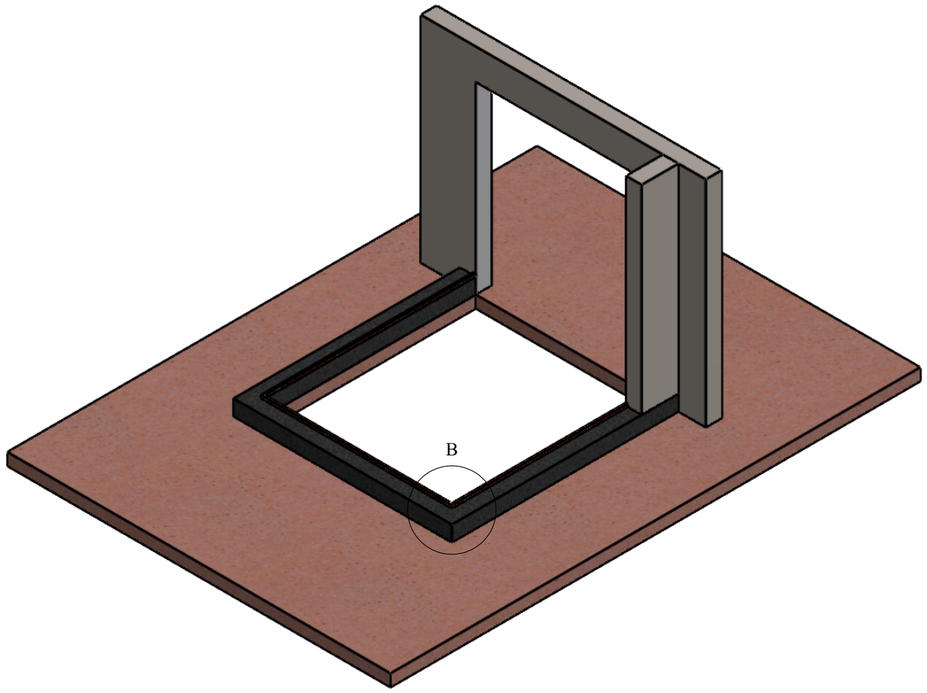

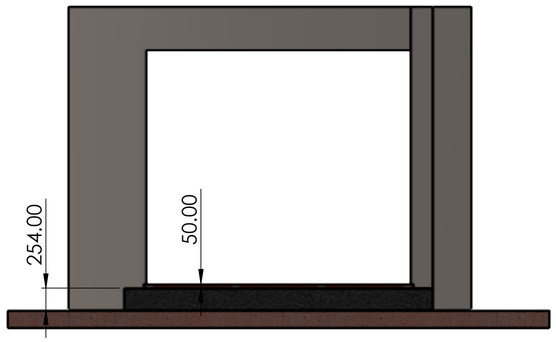

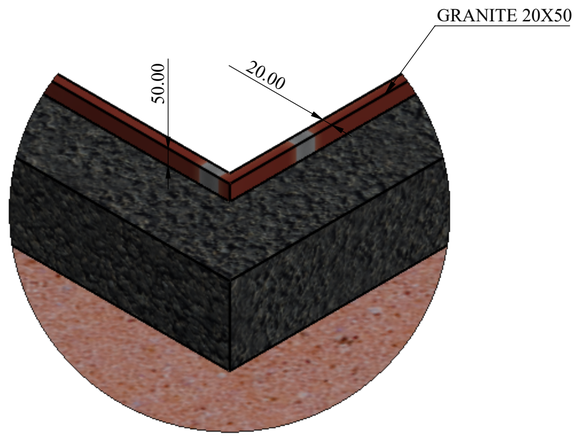

DETAIL B
SCALE 1 : 10

NOTE :

CIVIL DRAWING
FOR MOTOR & TRACK MOUNTING FABRICATION REQ
ALL CIVIL WORK & FABRICATION IN CLIENT SCOPE

SPECIAL INSTRUCTION'S :

TITLE - ROOF AUTOMATION

DWG NO - NTPL-000-PM-001-00-00-00

NIHVA Technologies Pvt. Ltd.

NIHVA TECHNOLOGIES PVT.LTD.PUNE
Website - www.nihva.com

	NAME	SIGNATURE	DATE
DRAWN	V.W.		16-05-2026
CHK'D	B.S.		17-05-2026
APPV'D	V.T.		17-05-2026

PRODUCT - RETRACTABLE ROOF	
PROJECT NO - NTPL-000-PM	REVISION - 00
SITE LOCATION -	WEIGHT -
MATRIAL -	QTY - 1
If any queries contact - Design@nihva.com	SCALE :
ALL DIMENSION ARE IN mm A2	PROJECTION METHOD: