

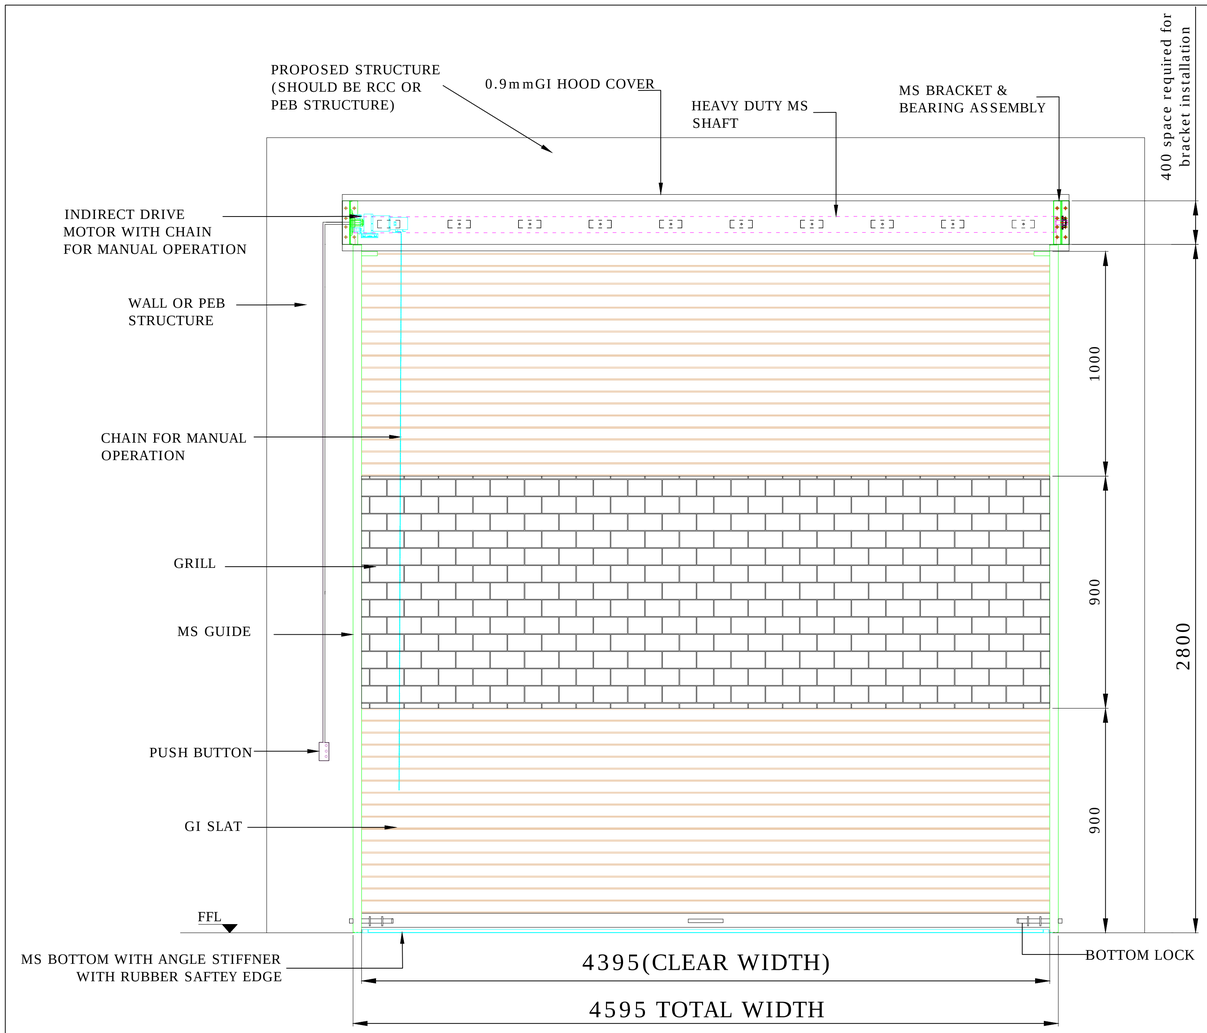



ELEVATION

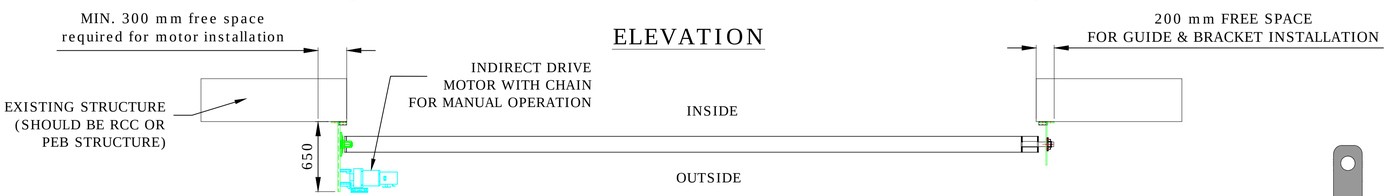


PLAN

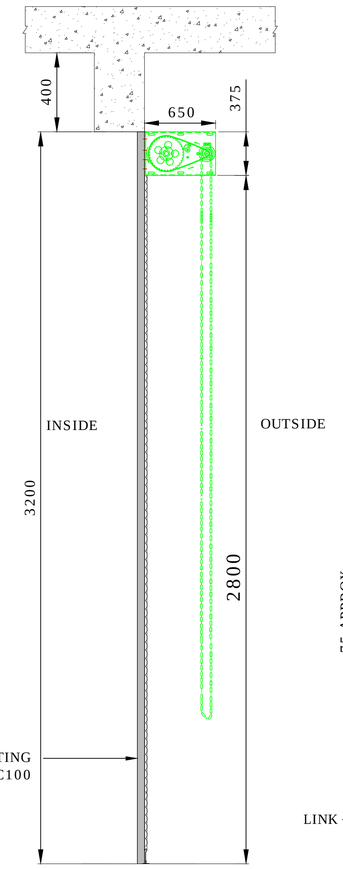



SIDE VIEW

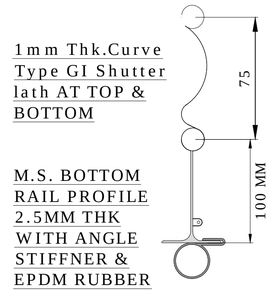

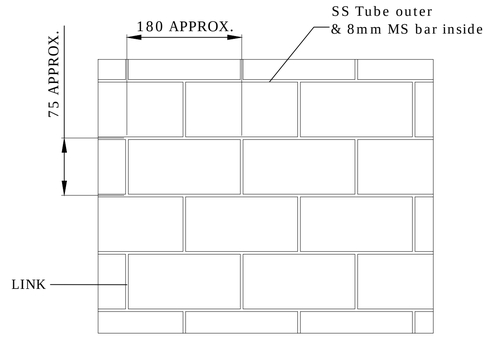

GRILL- BRICK PATTERN

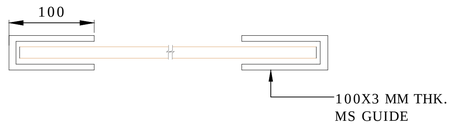

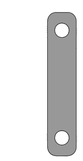

LINK/HINGE

SHOP NO-15

CLEAR WIDTH	CLEAR HEIGHT	QUANTITY
4395	2800	1

DIMENSION :

CLEAR WIDTH	CLEAR HEIGHT	QUANTITY
4395	2800	1

MATERIAL :

THICKNESS :

NOTE-
1.Shutter will be powder coated with approved color shade.

NIHVA TECHNOLOGIES PVT. LTD.
NIHVA TECHNOLOGIES PVT. LTD. PUNE
Email:- info@nihva.com
Website:- www.nihva.com

TITLE:

G.A. MOTORIZED GRILLED ROLLING SHUTTER

CLIENT'S APPROVAL :

CLIENT - ADANI

PROJECT - WESTERNS HEIGHTS

SITE LOCATION - MUMBAI

DWG. NO. :NIHVA/17-18/0094

SCALE: NTS	WT:	SHEET:1 OF 1

DRAWN BY: OMKAR	DATE: 01-06-2017
CHECK : SAGAR P.	DATE: 01-06-2017
APPROVED : S.S	DATE: 01-06-2017

If any queries contact : projects@nihva.com

NOTE: ALL DIMENSIONS ARE IN mm

THIS DRAWING & DESIGN IS THE PROPERTY OF NIHVA TECHNOLOGIES. NOT TO BE SOLD OR COPY TO ANY OTHER CONCERN.