




SIDE VIEW

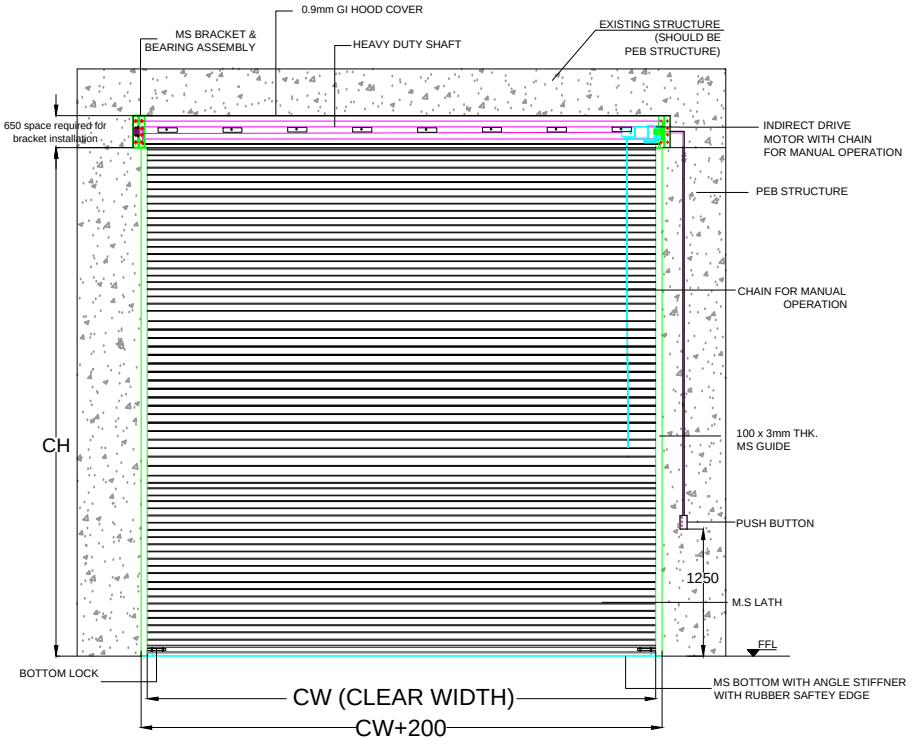


ELEVATION

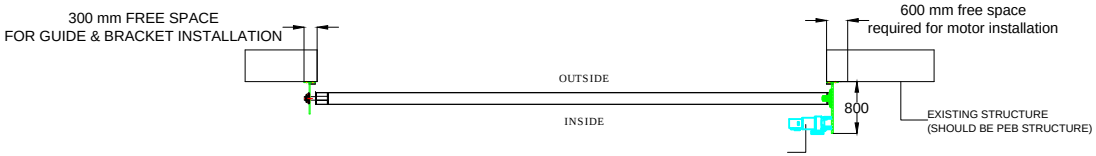

PLAN

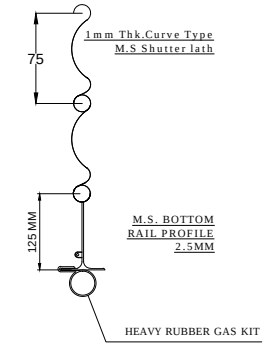

M.S. BOTTOM RAIL PROFILE 2.5MM

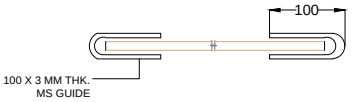

RAL COLOR & CODE

RAL 1003	
RAL 2004	
RAL 3000	
RAL 5002	
RAL 6005	
RAL 7035	
RAL 9005	
RAL 9010	

TOLERANCE - ±10mm

5000	3000	01NO	375
3000	3000	03 NOS	375
5000	7000	02 NOS	550
CLEAR WIDTH	CLEAR HEIGHT	QTY.	X

NOTE-
1. ALL CIVIL WORK WILL BE CLIENT'S SCOPE.
2.STRUCTURE REQUIRED FOR SHUTTER IS IN CLIENT'S SCOPE.
3. RAL CODE - PLEASE TICK IN GIVEN BOX.

This drawing & design is the property of NIHVA TECHNOLOGIES. Not to be sold or copied to any other concern.

TITLE
MOTORISED ROLLING SHUTTER

	NAME	SIGN	DATE
DRAWN	P.V.A		25.03.2019
CHECK	V.M.T		25.03.2019
APPRD.			

If any queries contact : design@nihva.com

ALL DIMENSION ARE IN mm

NIHVA
NIHVA TECHNOLOGIES PVT. LTD.
Website:- www.nihva.com
NIHVA TECHNOLOGIES PVT. LTD. PUNE
Tel : 020 66304033
Email:- info@nihva.com

CLIENT - UNITED ARCHITECT
PROJECT - A RAYMOND
SITE LOCATION - CHAKAN
DWG. NO. : NIHVA/18-19/0314 | REV- R00
SCALE: NTS | WT: | SHEET: 01 OF 01