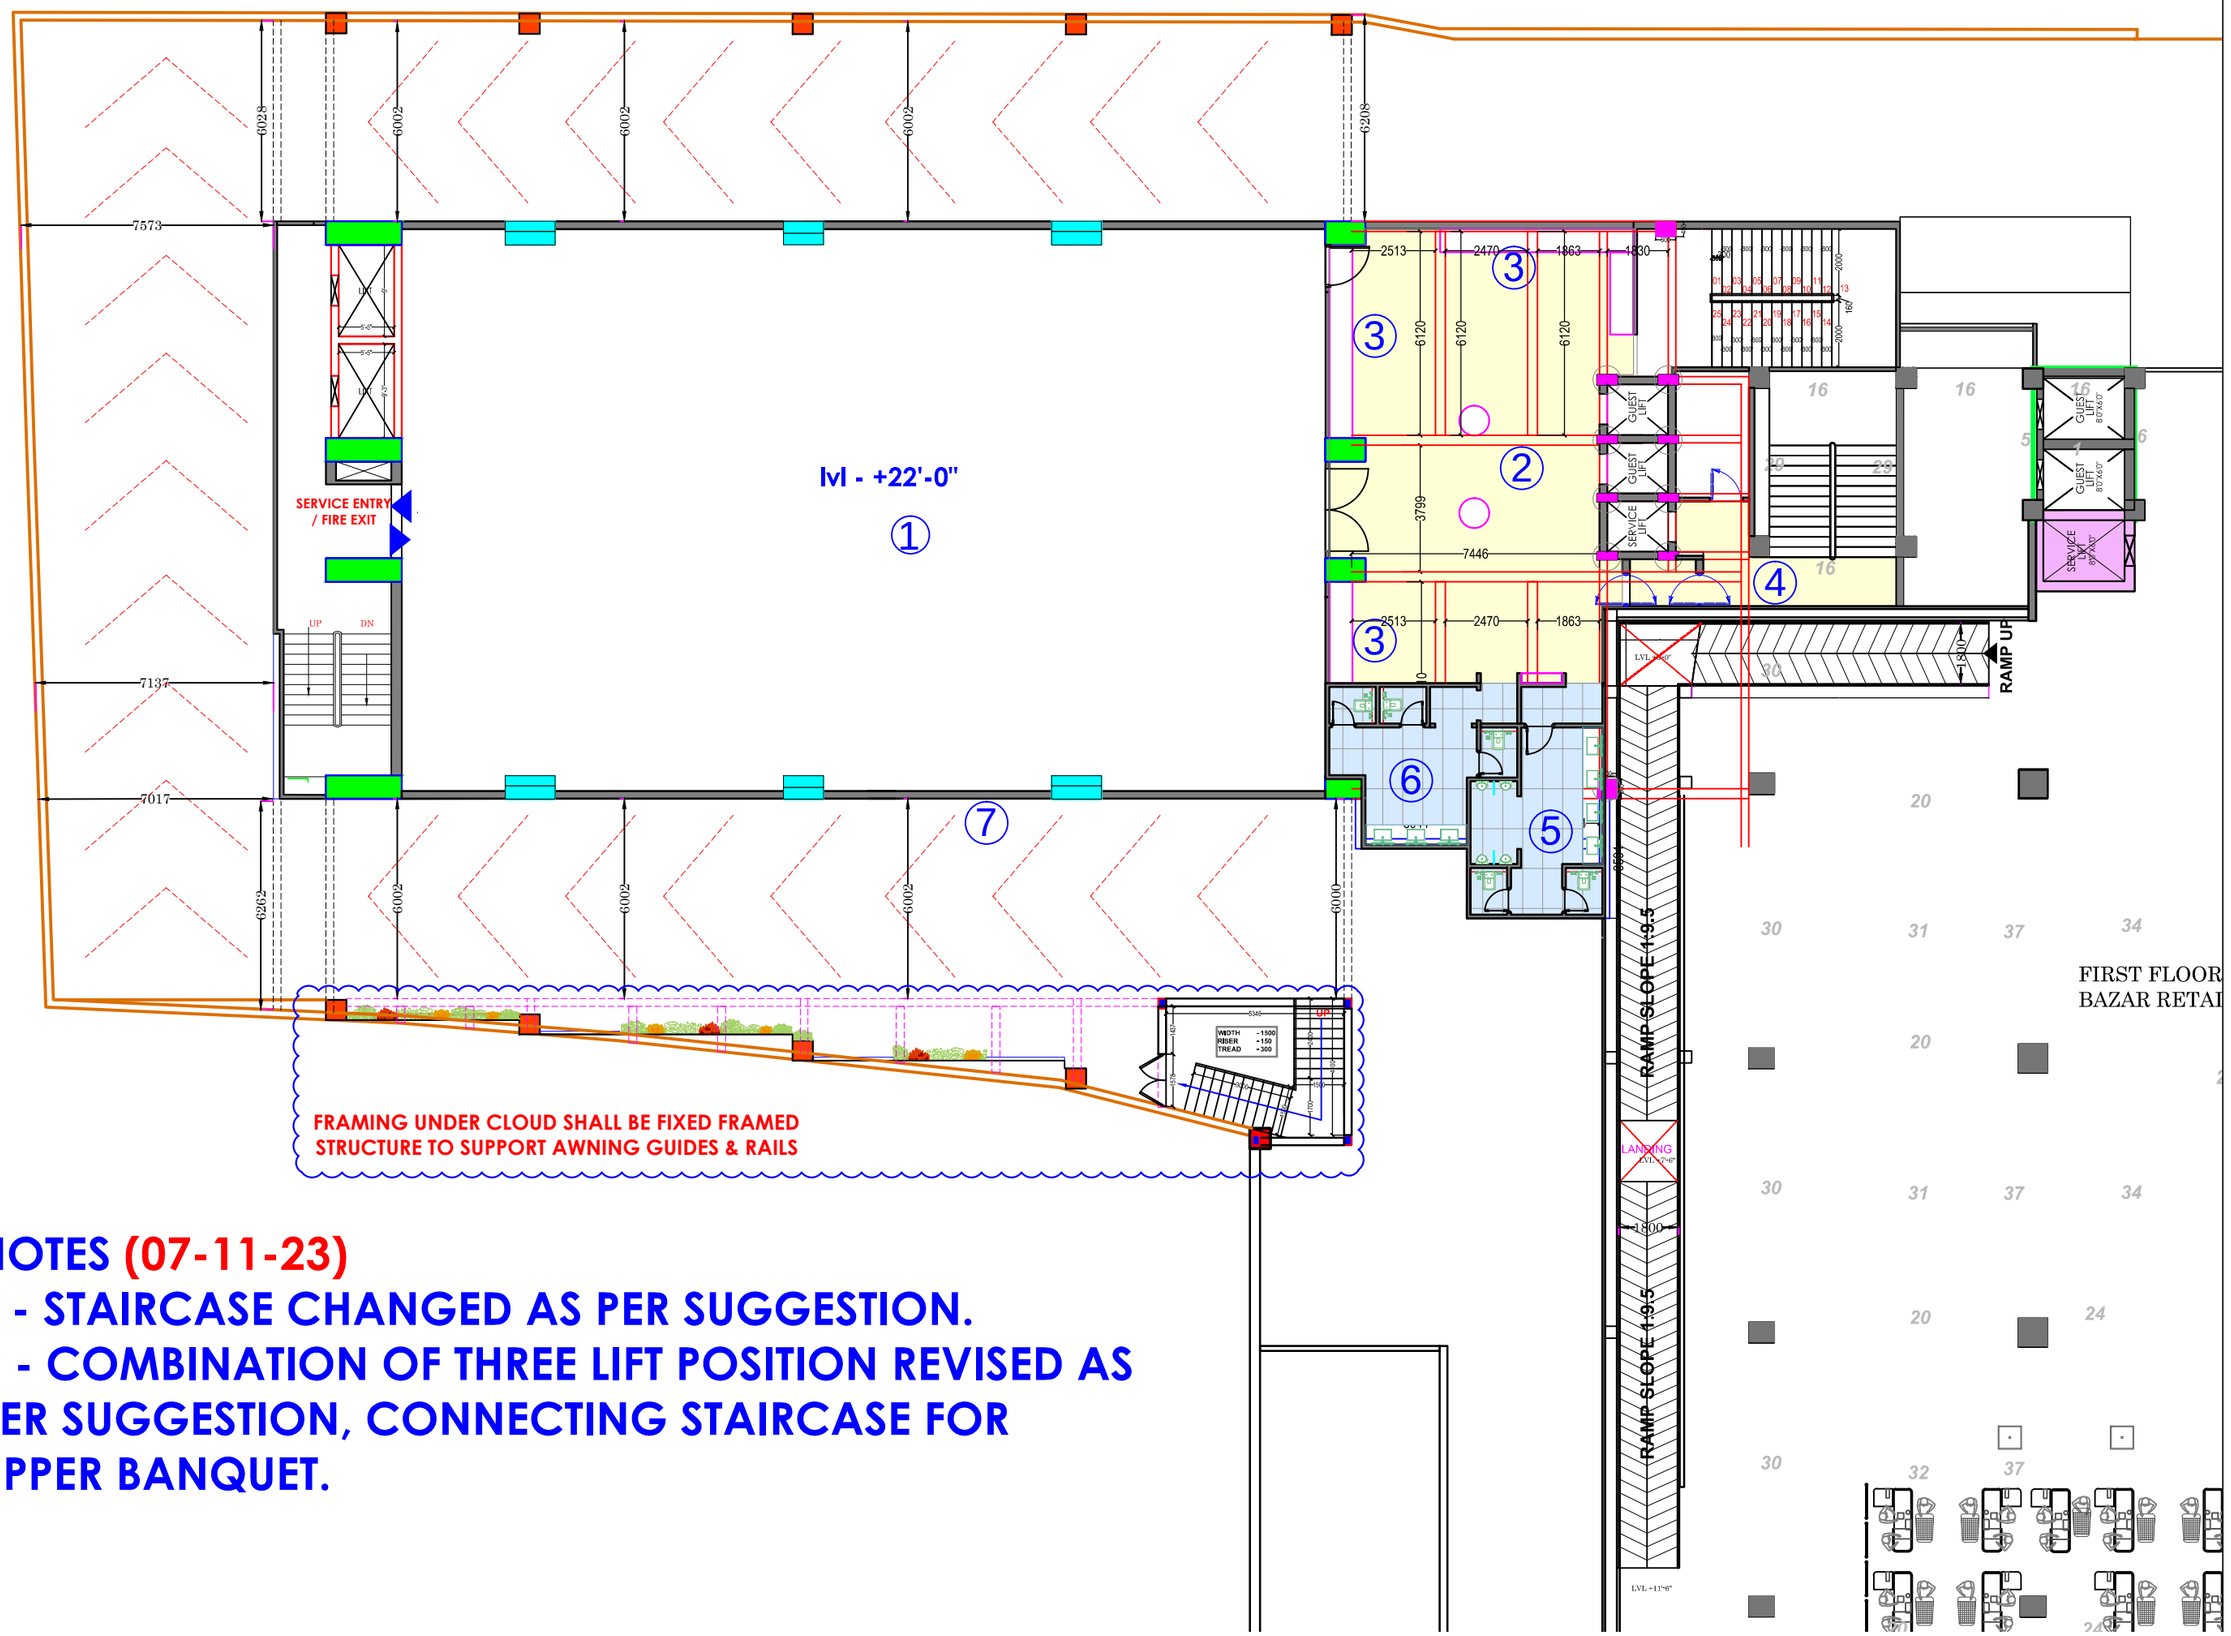
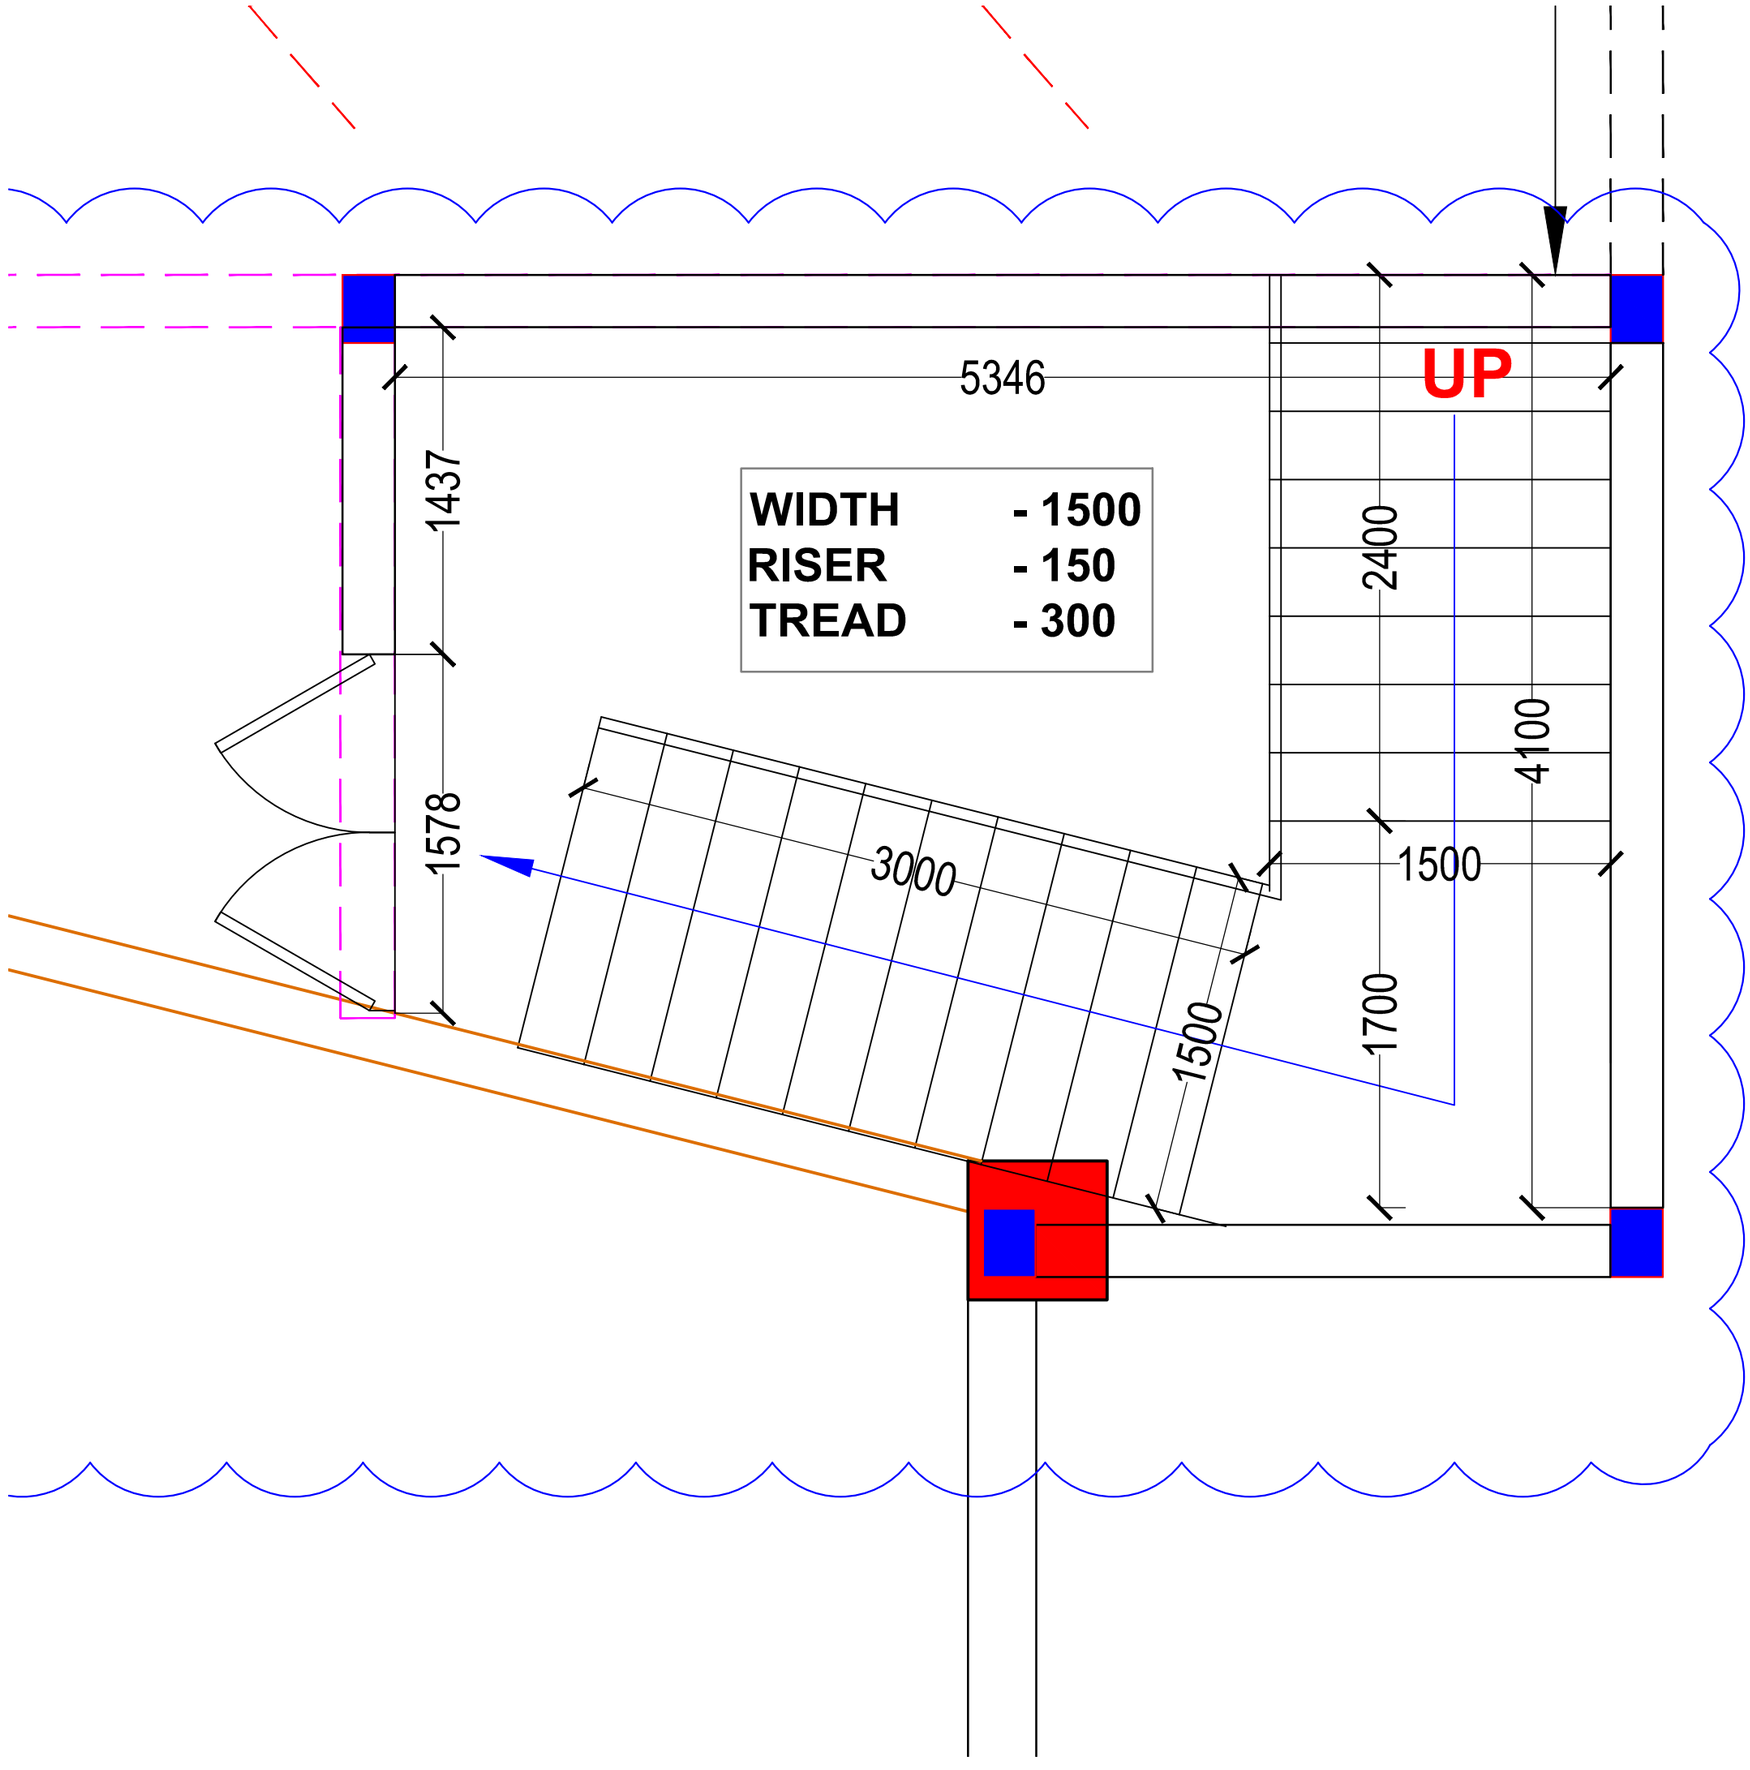


NOTES (07-11-23)

1 - STAIRCASE CHANGED AS PER SUGGESTION.

2 - COMBINATION OF THREE LIFT POSITION REVISED AS PER SUGGESTION, CONNECTING STAIRCASE FOR UPPER BANQUET.


5346
1437
1578
3000
1500
2400
4100
1500
1700
UP
WIDTH - 1500
RISER - 150
TREAD - 300