

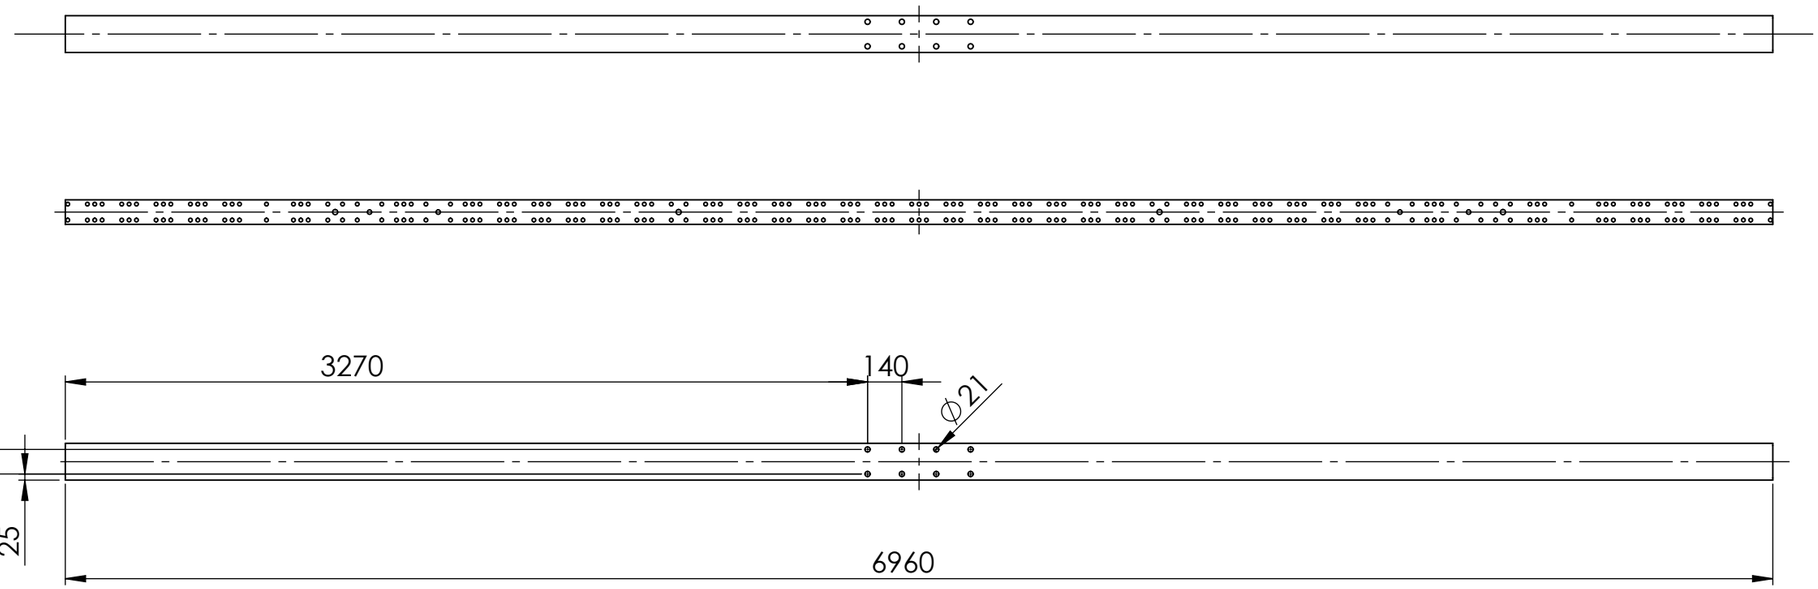


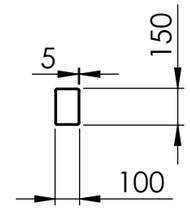

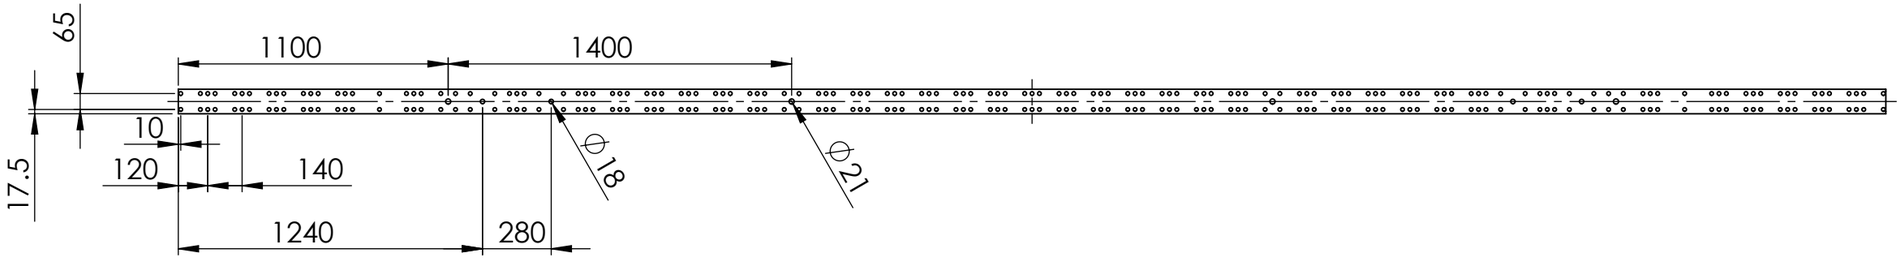

Wymiary nietolerowane wykonac w klasie dokladnosci
"m" wg. normy ISO 2768-1

PROJEKT:	
NAZWA ELEMENTU:	przeslo - profil A
FANCY FENCE®	NR KATALOGOWY:
KATEGORIA: przeslo	TYP ELEMENTU: profil
ETAP PRODUKCJI: laser 3D	NORMA:
MATERIAŁ: 1.0045 (S355JR)	MASA: 123.08 kg
ROZMIAR ARKUSZA: A3	PODZIALKA: 1:25
NUMER RYSUNKU: P.1.1	DATA/WERSJA: 24.04.2025

© 2018-2025 Copyright
JP NOVATION Sp. z o.o.
All rights reserved.