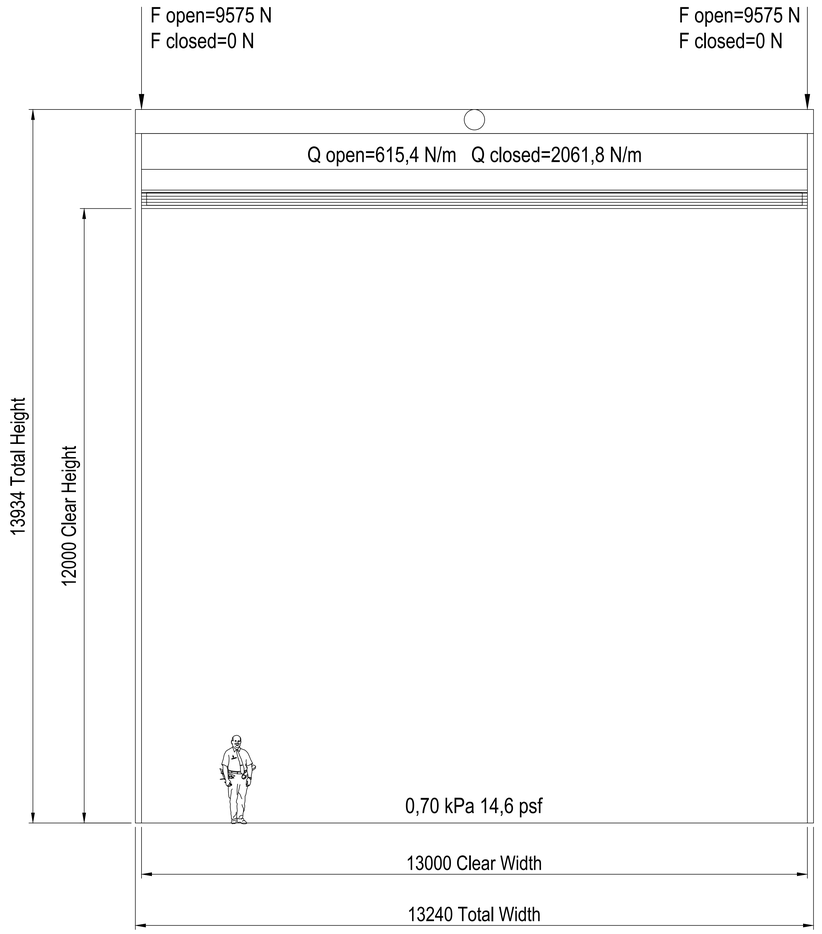


Contact Information

Henk v.d. Heijden
Project Manager
MEGADOOR/
ASSA ABLOY Entrance Systems
Servicegatan 6
P.O. Box 383
SE-931 24 Skellefteå
SWEDEN
Direct: +31 (0)65 323 61 77
Switchboard: +46 (0)10 47 47 190
E-mail: henk.van.der.heijden@assaabloy.com
www.megadoor.com

Quotation only. Do not use for design.
Nominal static vertical loads are indicated.
A dynamic surload factor of 1.25 should be added to door leaf loads in open position.
Includes items provided by ASSA ABLOY Entrance Systems only.
Total weight: 3057 kg
Total static weight: 2796 kg
Total motor power: 5,0 kW
Total rated current: 10,2 A
Total peak current: 45,0 A
Power supply: 400V/50Hz/3ph
(max. allowed voltage drop at start: 5%)
Control system: 24V
Mains power to control panel supplied by others than ASSA ABLOY Entrance Systems.

ASSA ABLOY

SALES REP. Ashish Nair	DATE ISSUED 1-10-2019
SALES No. 219-368	DATE DRAWN 1-10-2019
SCALE N.T.S.	
DRAWING No. 219-368	REVISION

Synco Industries
Mumbai
India

Load diagram