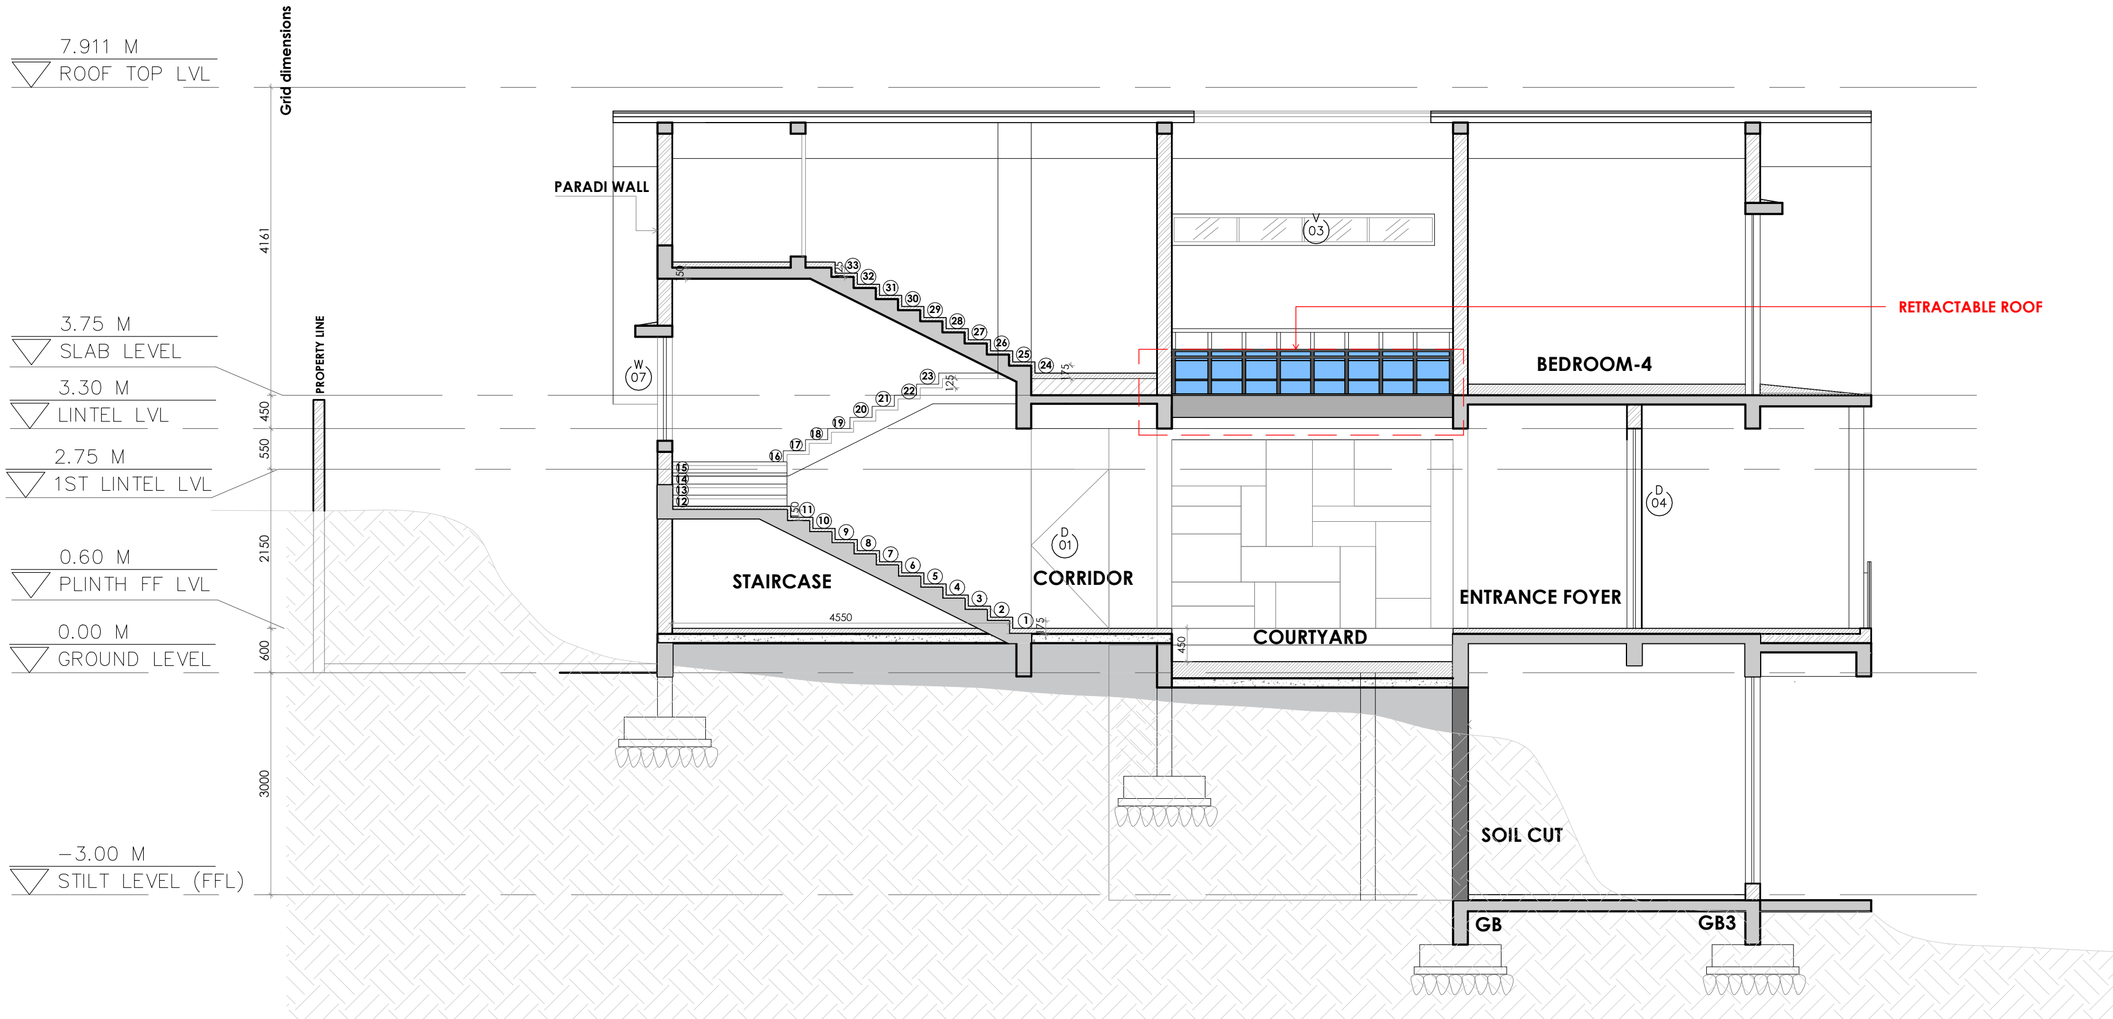


SECTION BB
SCALE 1:60

ARCHITECTURAL DRAWING

WORKING DRAWING

'SHELLSPACE' IS TOTAL OWNER OF THESE DRAWINGS AND THE DATA/DESIGN IT COVERS IS ITS PROPERTY. IN ANY SENSE, ONLY SHELLSPACE AND NO OTHER HAS ITS RIGHTS OF USE. THEY SHALL NEITHER BE ISSUED, EXHIBITED, USED, REPRODUCED OR COPIED EXCEPT IN THE LIMITED WAY AND PRIVATE USE PERMITTED BY ANY WRITTEN CONSENT GIVEN BY THE SHELLSPACE/LENDER TO THE BORROWER.

NOTES

1. ALL DIMENSIONS ARE IN MILLIMETERS UNLESS NOTES OTHERWISE.
2. ALL LEVELS ARE IN METERS UNLESS NOTED OTHERWISE.
3. ANY DISCREPANCY TO BE BROUGHT TO THE NOTICE OF CONSULTANT PRIOR TO COMMENCEMENT OF WORK
4. THESE DRAWINGS SHALL BE READ IN CO−ORDINATION WITH PROJECT SPECIFICATIONS AND OTHER CONSULTANT'S (LIKE STRUCTURE, MEP, LANDSCAPE & ID ETC) DETAILS/DRAWINGS AND BASED ON RELATED INFORMATION SHARED BY 'SHELLSPACE' FOR THESE DRAWINGS.

LEGENDS

FOR INFO-AUGUST-2021

PROJECT
FARMHOUSE

CLIENT

DESIGN CONSULTANT

SHELLSPACE
ARCHITECTS I INTERIOR D I PROJECT MANAGERS I ENGINEERS
SHELLSPACE DESIGN STUDIO
PUNE OFFICE
A-wing, 2nd floor, CASP, Baner Pashan Link Road, Pashan, Pune, India
Pin Code: 411 021 Tel: +91 99 2261 1717
Email: info@shellspace.co.in

STRUCTURAL CONSULTANT

MEP CONSULTANT
SDS

ID/LANDSCAPE CONSULTANT
SDS

DRAWING
SECTION BB
FOR RETRACTABLE ROOF

PROJECT SDS		JOB NO.	SUBM STAGE	LOCATION CO-ORDINATES
SCALE 1 : 60				.....
DATE 22.06.17		SDS-851	A2	
DRN. BY	CHKD BY	DRG NO	REVISION	NORTH
APOORVA SDS	PK SDS		R-00	