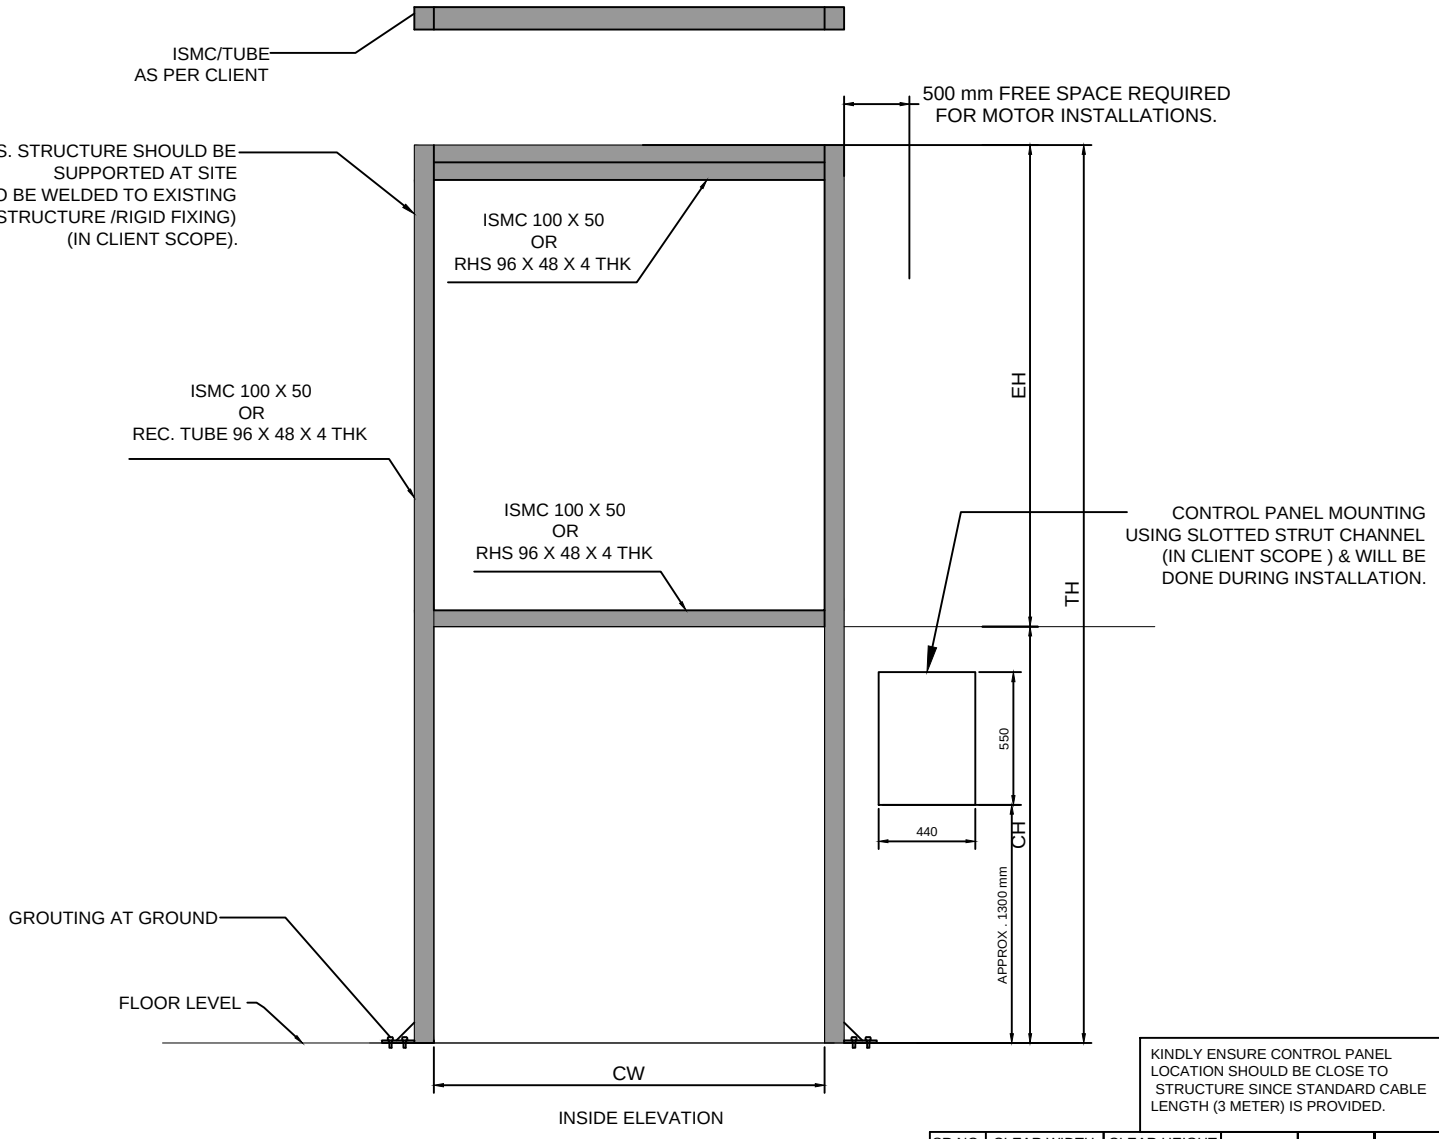

INSIDE ELEVATION

KINDLY ENSURE CONTROL PANEL LOCATION SHOULD BE CLOSE TO STRUCTURE SINCE STANDARD CABLE LENGTH (3 METER) IS PROVIDED.

SR NO	CLEAR WIDTH CW	CLEAR HEIGHT CH	QTY	TH	EH
1	5000mm	4000mm	1	8300	4300

REV NO	DATE	DRAWN	REMARK
R02	3.12.2020	S.M.S.	CONTROL PANEL MOUNTING ON STRUT
R01	30.11.20	S.M.S.	CONTROL PANEL MOUNTING ADDED.

NOTES-
(1) REQUIRED M.S. STRUCTURE , FITTING & ALL CIVIL WORK IN CLIENT SCOPE .
(2) PRODUCT WILL BE INSTALLED AFTER READINESS OF STRUCTURE AS PER DRAWING.

This drawing & design is the property of NIHVA TECHNOLOGIES. Not to be sold or copied to any other concern.

TITLE: STRUCTURE FOR SECTIONAL DOOR

NIHVA TECHNOLOGIES PVT. LTD. PUNE
Tel : 020 66304033
Email:- info@nihva.com
Website:- www.nihva.com

	NAME	SIGN	DATE
DRAWN	S.M.S.		20.11.2020
CHECK	K.P.		20.11.2020
REV.			
APPROVAL			

If any queries contact : projectsupport@nihva.com

ALL DIMENSION ARE IN mm

CLIENT - SCON PROJECTS PVT LTD
PROJECT - INNOVATEC INDIA PVT. LTD.
SITE LOCATION - SANAND
DWG. NO. : NIHVA/19-20/0092/R02
SCALE: NTS | WT: | SHEET: 01 OF 01