


ITEM NO.	PART NUMBER	DESCRIPTION	QTY.
1	NTPL174-MS STRUCTURE FOR CENTER ROOF	MS STRUCTURE FOR CENTER ROOF	1
2	NTPL174-PROF07	CENTER ROOF PROFILE	4
3	NTPL174-PROF10	ROOF SIDE PROFILE	2
4	NTPL174-PROF11	INTERMEDIATE SUPOORT	12
5	NTPL174-PROF08	GNT006	1
6	NTPL174-PROF09	GNT008	1
7	NTPL174-PROF14	FRONT ENCLOSER	1

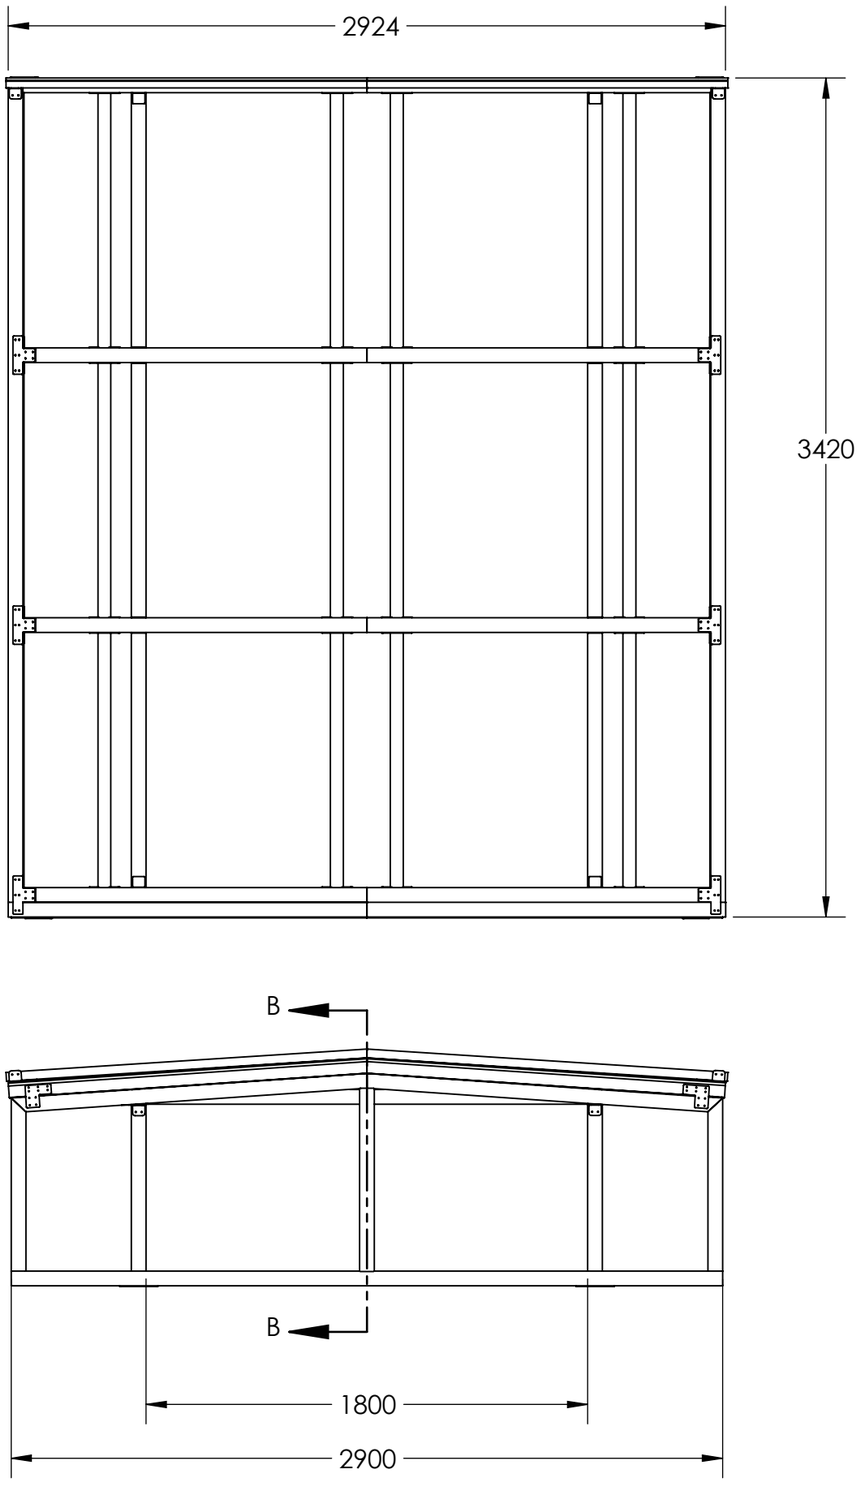


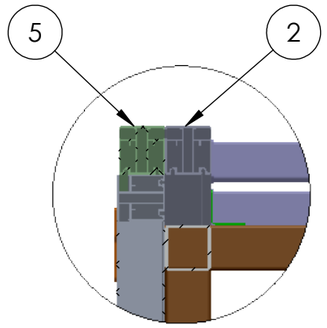


DETAIL A

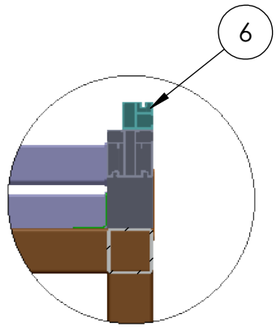

DETAIL E

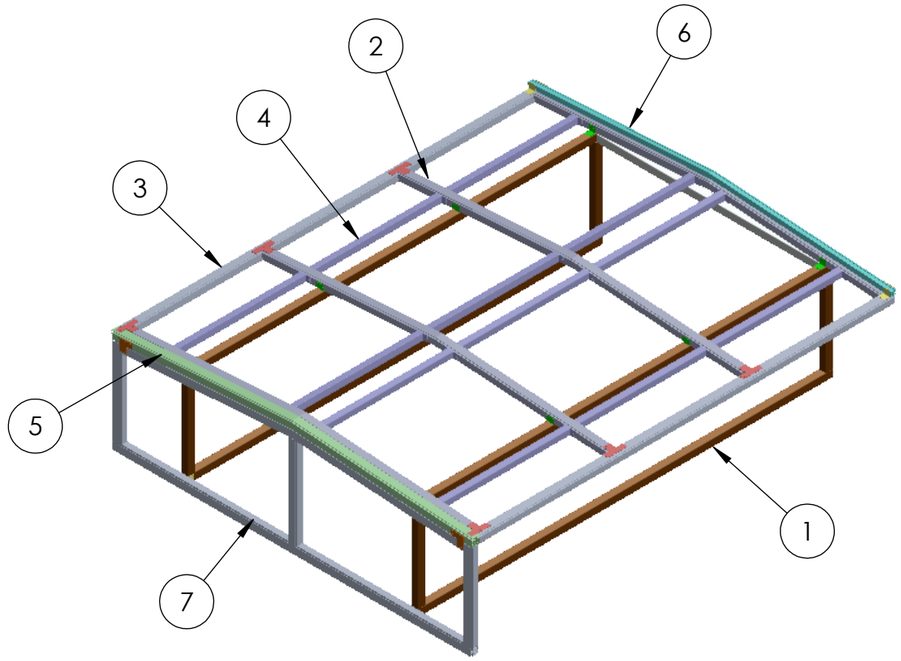


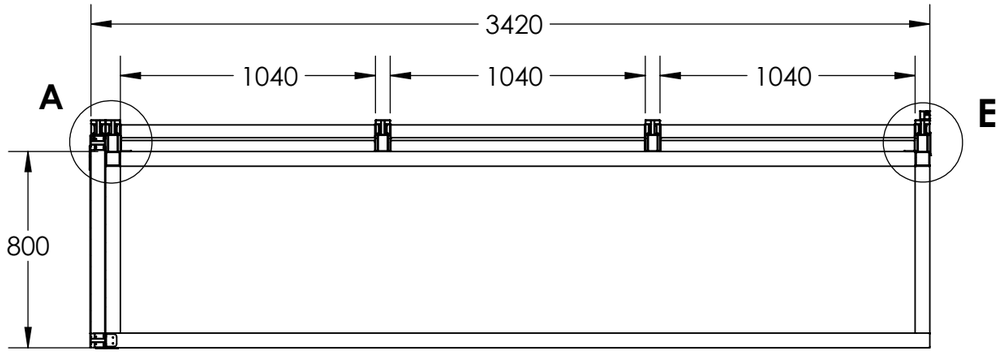

SECTION B-B

TITLE - CENTER ROOF ASSEMBLY				NIHVA TECHNOLOGIES PVT.LTD.PUNE
DWG NO - NTPL174-CENTER ROOF			QTY - 1	Website - www.nihva.com
	NAME	SIGNATURE	DATE	PROJECT NO - NTPL-PV
DRAWN	D.V.		20.06.2023	PRODUCT - RETRACTABLE ROOF
CHK'D	P.M.		20.06.2023	SITE LOCATION -
APPV'D	V.T.		20.06.2023	
if any queries contact - supportautomation@nihva.com				REVISION -
ALL DIMENSION ARE IN mm			A3	SCALE - SHEET 1 OF 2

ITEM NO.	PART NUMBER	DESCRIPTION	QTY.
1	NTPL174-MS STRUCTURE FOR CENTER ROOF	MS STRUCTURE FOR CENTER ROOF	1
2	NTPL174-PROF07	CENTER ROOF PROFILE	4
3	NTPL174-PROF10	ROOF SIDE PROFILE	2
4	NTPL174-PROF11	INTERMEDIATE SUPOORT	12
5	NTPL174-PROF08	GNT006	1
6	NTPL174-PROF09	GNT008	1
7	NTPL174-PROF14	FRONT ENCLOSER	1

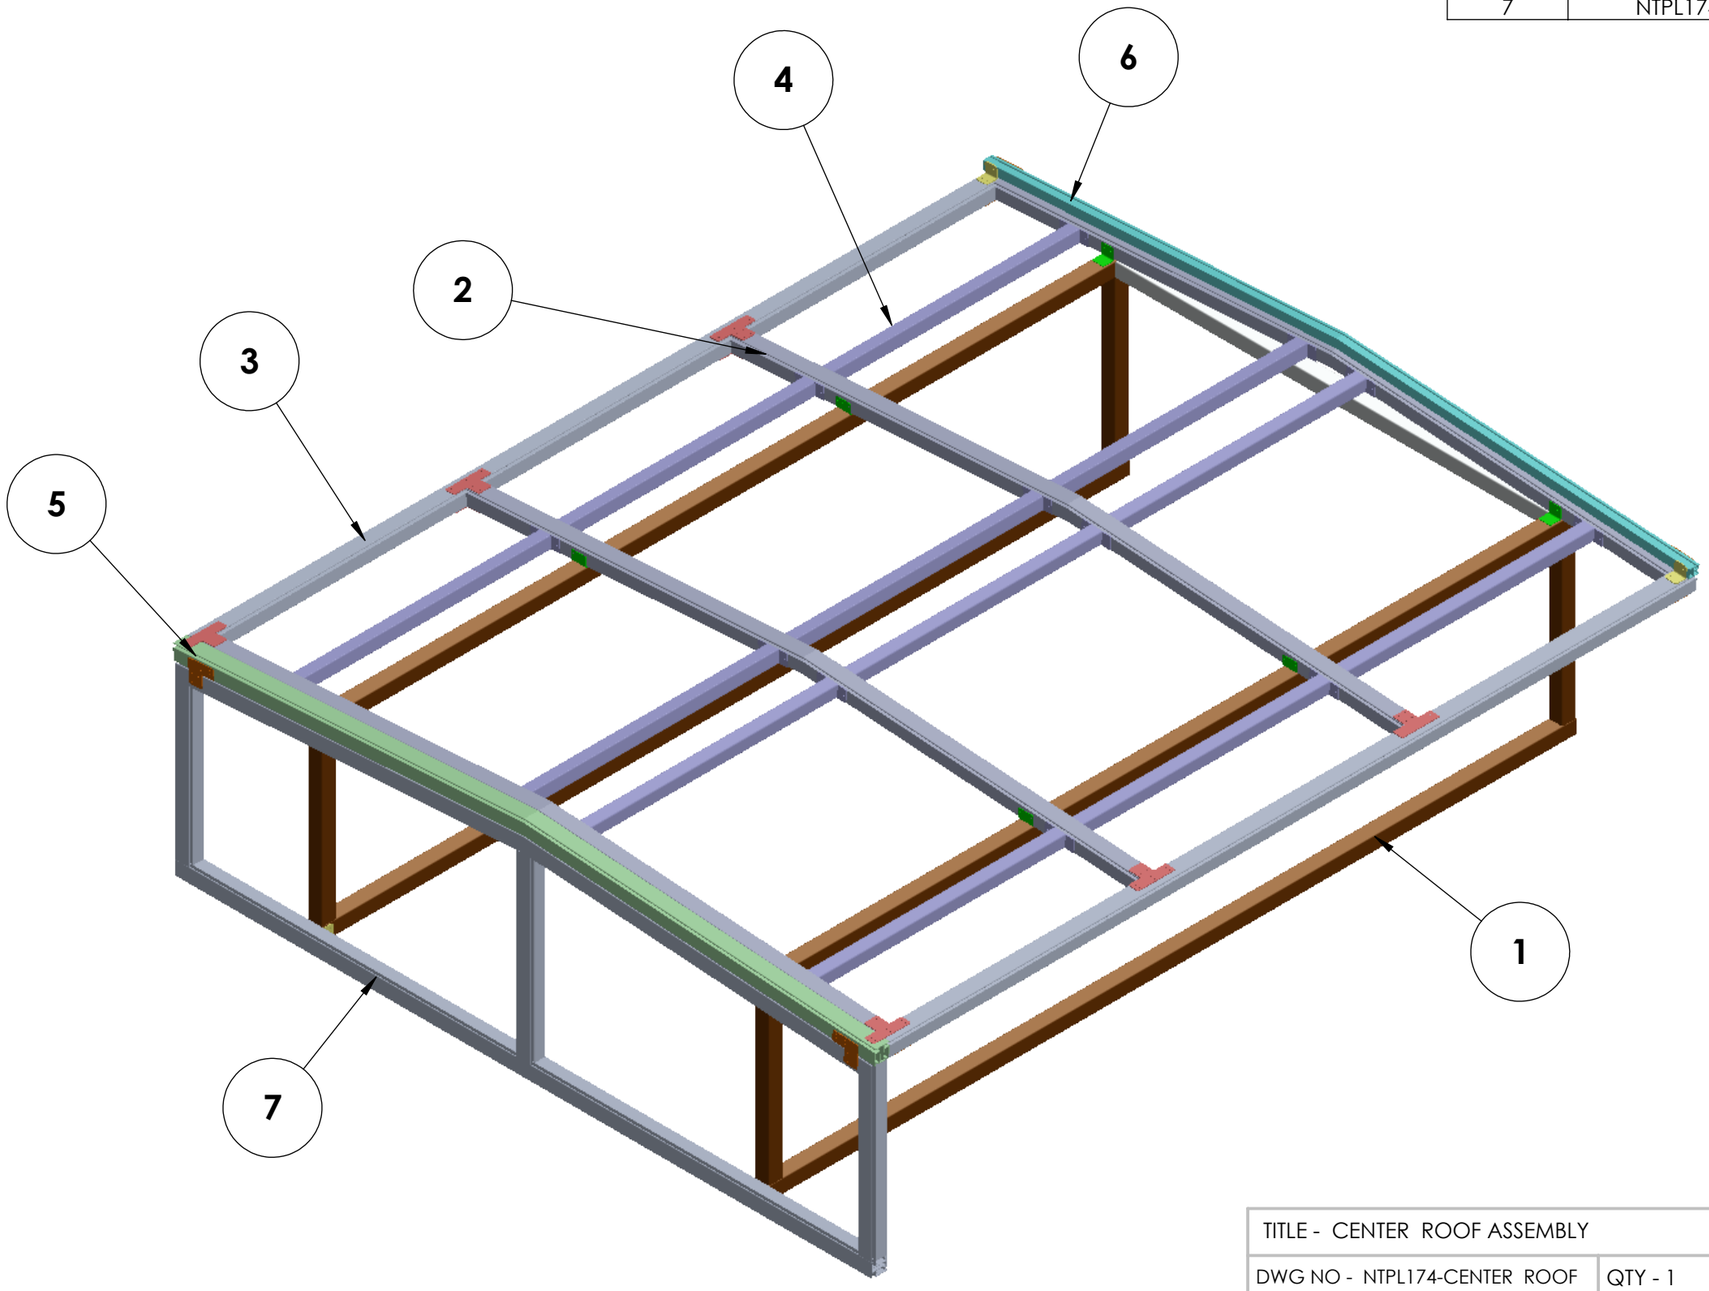

TITLE - CENTER ROOF ASSEMBLY				NIHVA TECHNOLOGIES PVT.LTD.PUNE Website - www.nihva.com
DWG NO - NTPL174-CENTER ROOF			QTY - 1	
	NAME	SIGNATURE	DATE	PROJECT NO - NTPL174
DRAWN	D.V.		20.06.2023	PRODUCT - RETRACTABLE ROOF
CHK'D	P.M.		20.06.2023	SITE LOCATION -
APPV'D	V.T.		20.06.2023	
if any queries contact - supportautomation@nihva.com				REVISION -
ALL DIMENSION ARE IN mm		A3		SCALE - SHEET 2 OF 2